


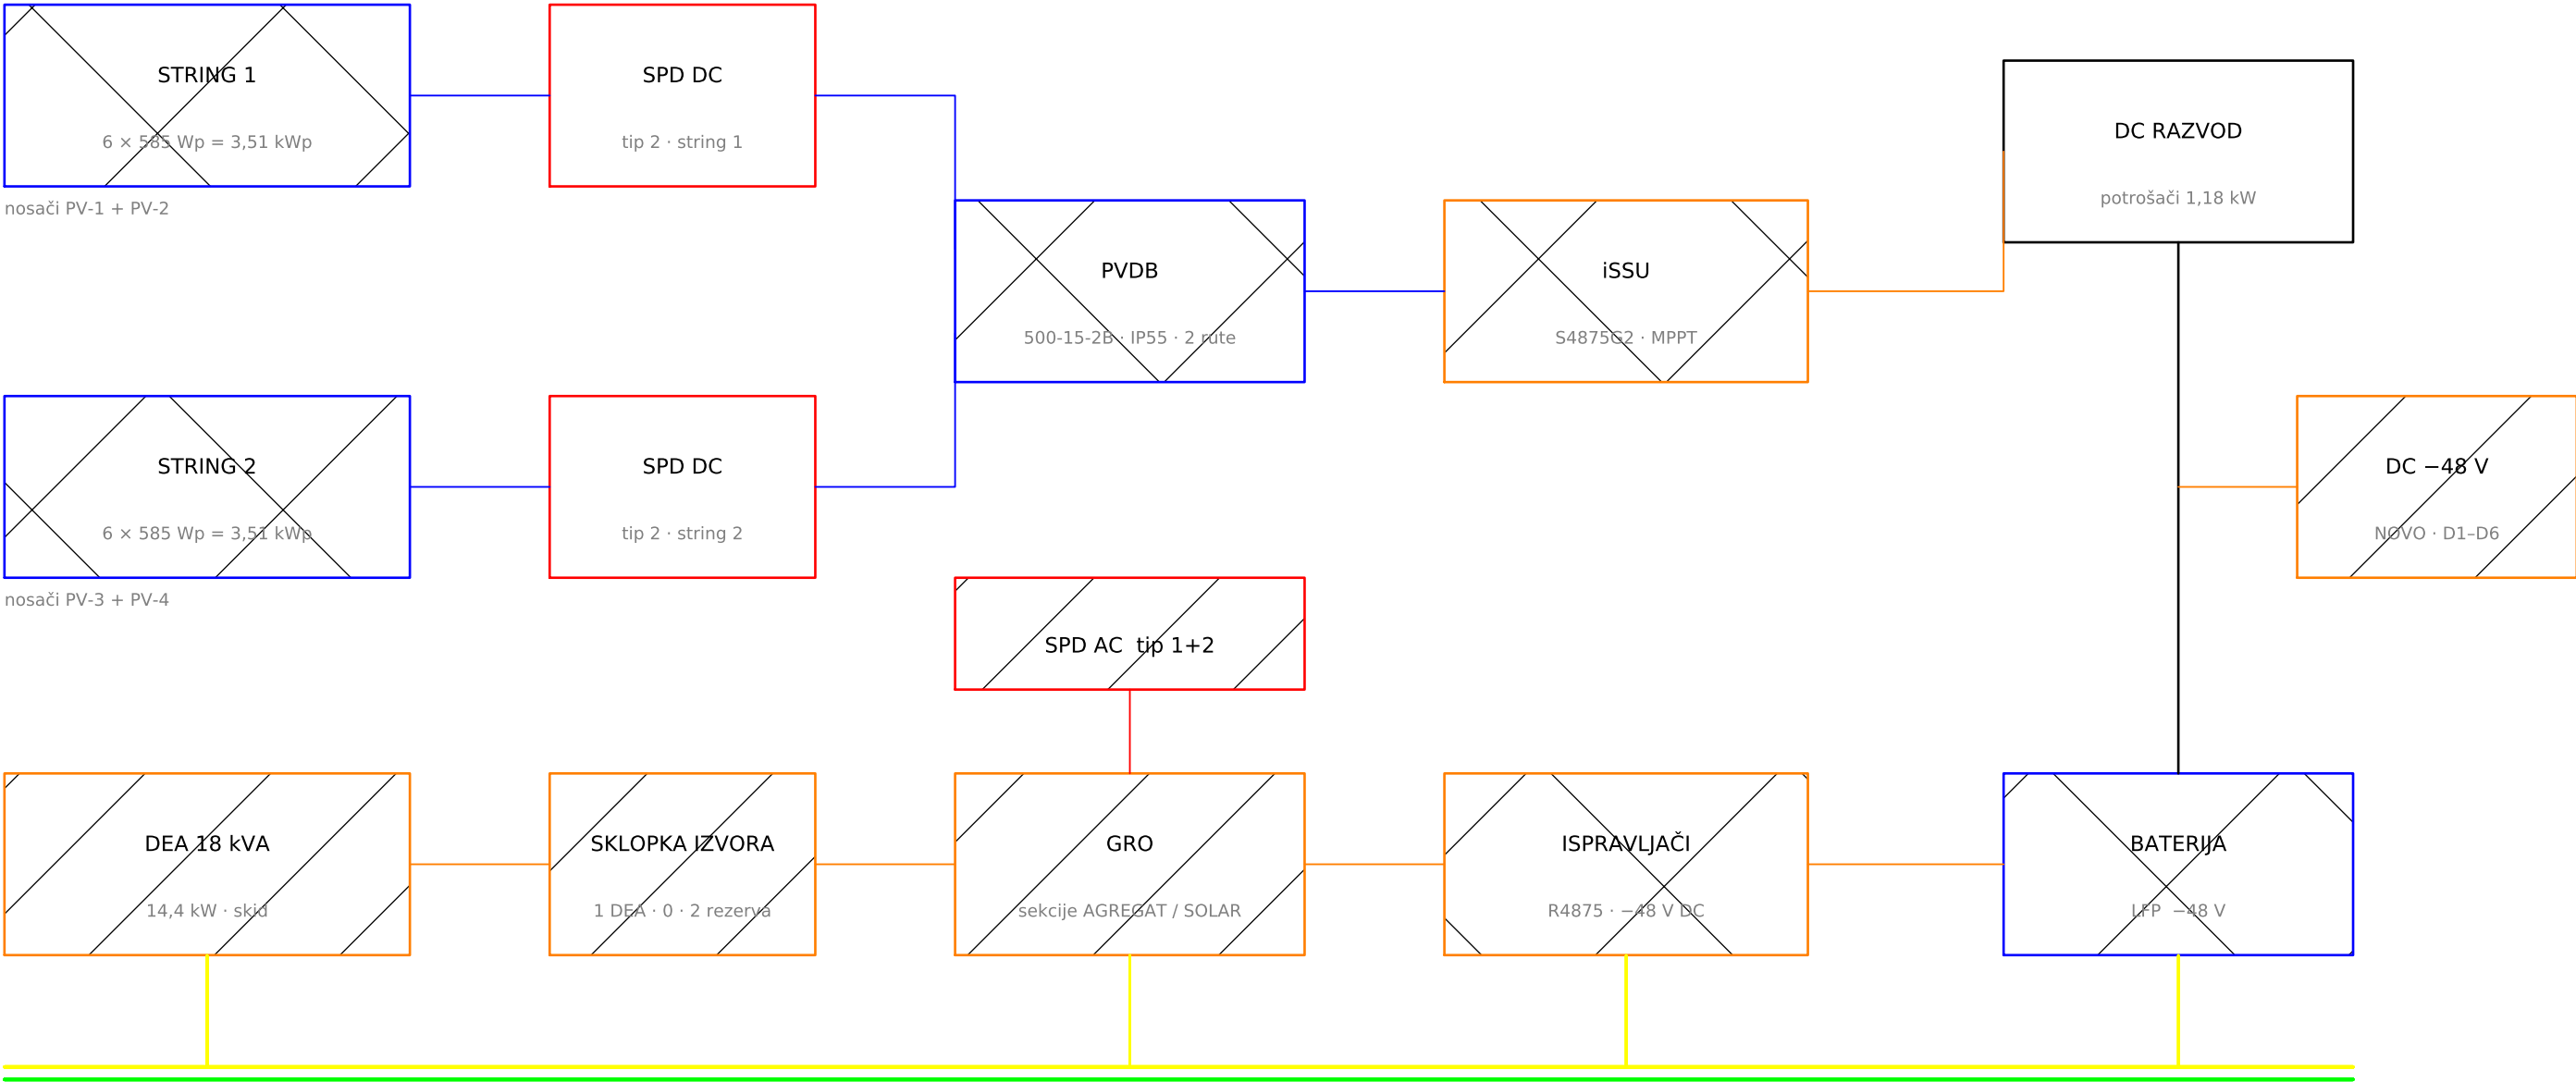

postojeći prstenasti uzemljivač Fe/Zn 25×4 · R ≤ 10 Ω · nosači FN na Cu uže 50 mm²

NAPOMENE:

- 1 Lokacija nije na mreži; DEA je jedini AC izvor. Sklopka: 1 DEA · 0 · 2 rezerva.
- 2 TN-S, spoj N-PE samo u novom GRO. Odvodnici: AC tip 1+2, DC tip 2 po stringu.
- 3 FN: 12 modula = 2 stringa × 6 (PV-1 + PV-2, PV-3 + PV-4); PVDB ima 2 rute.
- 4 DC razvod –48 V (novo), D1–D6: trajni potrošači prema Prilogu I, Tačka 4.5.

 isporuka i montaža Izvođača (LOT 2)

 oprema Kupca — ugradnja u LOT 2



BH TELECOM d.d. SARAJEVO

Izvršna direkcija za tehnologiju i razvoj servisa

Investitor:

BH Telecom d.d. Sarajevo, Franca Lehara 7, Sarajevo

Objekat:

BS SJEDNICA (Bileća) — autonomni hibridni sistem napajanja

Faza:

Tenderska dokumentacija — Prilog III

Naziv crteža:

Jednopolna shema — hibridni sistem napajanja

Projektant:

Rusmir Skopljak, dipl. ing. el.

ovjerio:

Rusmir Skopljak, dipl. ing. el.

šifra projekta:

BHT-SJEDNICA-2026

razmjera:

—

godina / broj crteža:

2026. E-01