
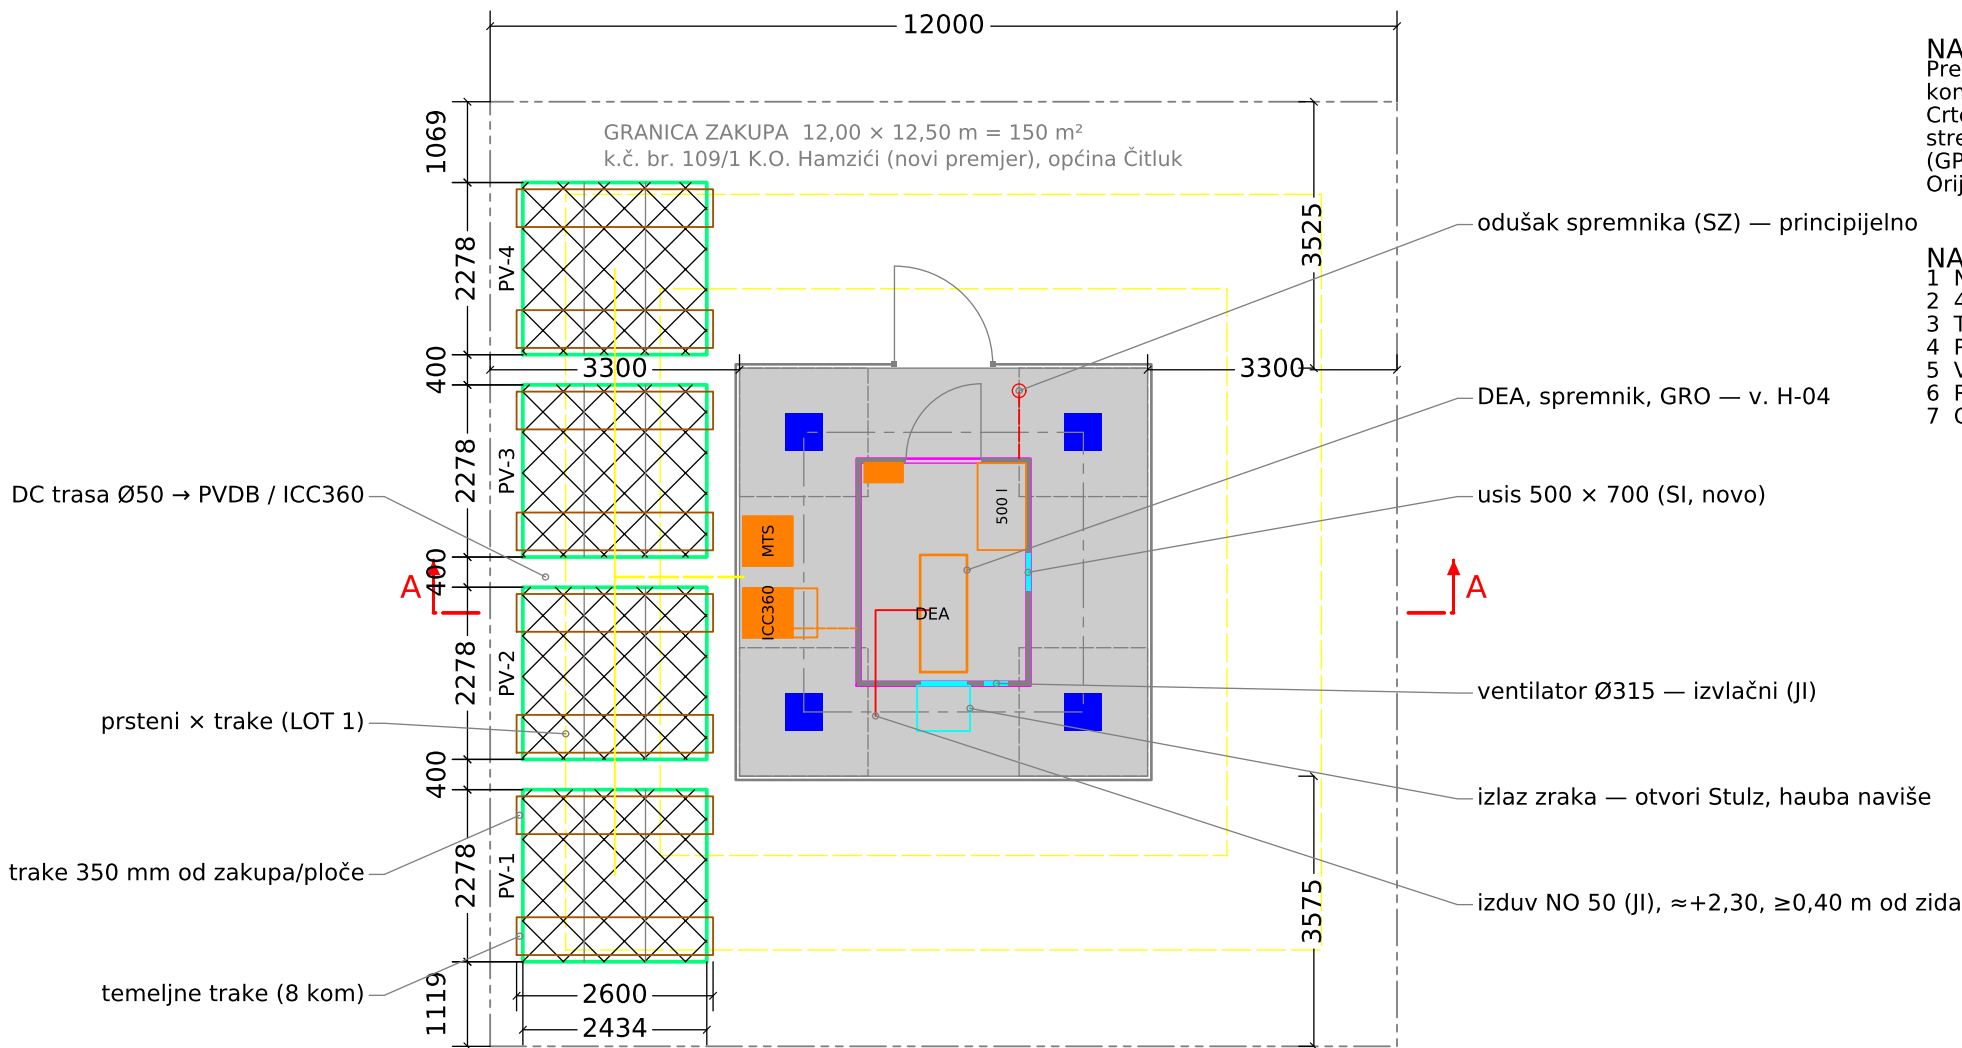


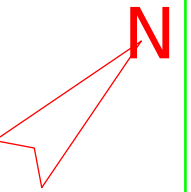

NAPOMENA — ORIJENTACIJA:
Prema Google Maps (Naručilac 11.09.2026) kompleks je zakrenut 45°: vrata kontejnera i kapija gledaju na SJEVEROZAPAD (SZ), klima-uređaj Stulz na JI. Crtež je pravougaon na kompleks (gore SZ, desno SI, dolje JI, lijevo JZ); strelica pokazuje pravi sjever. Ovjereni crtež lokacije iz 2017 (GP-BS-10472-291, 01. Situacija 1_200) zakrenut je ≈180° u odnosu na teren. Orijehtaciju potvrđuje Ponuđač obilaskom lokacije.

NAPOMENE:
1 Nosači na JUZOZAPAD (azimut 225°), nagib 45°; ivica panela +0,50 / +2,93 m.
2 4 odvojena nosača u nizu: 4 × 2278 + 3 × 400 = 10312 mm, u pojasu JZ.
3 Temeljne trake 500 × 2600 mm, d = 900 mm, na podložnom betonu 50 mm.
4 Postojeći prsteni uzemljivača (0,8 m) ukrštaju temeljne trake — LOT 1.
5 Vjetar qp ≥ 1,20 kN/m²; nosač CUSTOM izrade, proračun dostavlja Ponuđač.
6 Raspored u kontejneru prema H-04.
7 Ormari ICC360-HA1-C1 i MTS iza FN polja, u sjeni — principijelno.

LEGENDA

- FN nosači PV-1..PV-4 — po 3 × 585 Wp (1 × 3, položeno), 45°, azimut 225° (JZ) — 2 stringa × 6
- AB temeljne trake 500 × 2600 mm, d = 900 mm, razmak 1600 mm — 8 kom
- DC trasa u PEHD Ø50 (isprekidano) — od polja do PVDB uz ICC360
- DEA 18 kVA (skid), spremnik 500 l u koritu, novi GRO
- usis 500 × 700 (SI), izlaz zraka kroz otvore Stulz (JI) i haubu naviše, ventilator Ø315 (JI)
- izduv NO 50 (JI, ≈+2,30 m); odušak spremnika (SZ, isprekidano); presjek A-A
- Huawei ICC360-HA1-C1 i MTS vani na ploči (JZ), iza FN polja — principijelno



BH TELECOM d.d. SARAJEVO

Izvršna direkcija za tehnologiju i razvoj servisa

Investitor:

BH Telecom d.d. Sarajevo, Franca Lehara 7, Sarajevo

Objekat:

BS HAMZIĆI (ČITLUK) — autonomni hibridni sistem napajanja

Faza:

Tenderska dokumentacija — Prilog III

Naziv crteža:

Situacija — BUDUĆE STANJE

Projektant:

Rusmir Skopljak, dipl. ing. el.

Ovjerio:

Rusmir Skopljak, dipl. ing. el.

šifra projekta:

BHT-HAMZICI-2026

razmjera:

1:100

godina / broj crteža:

2026. H-02