


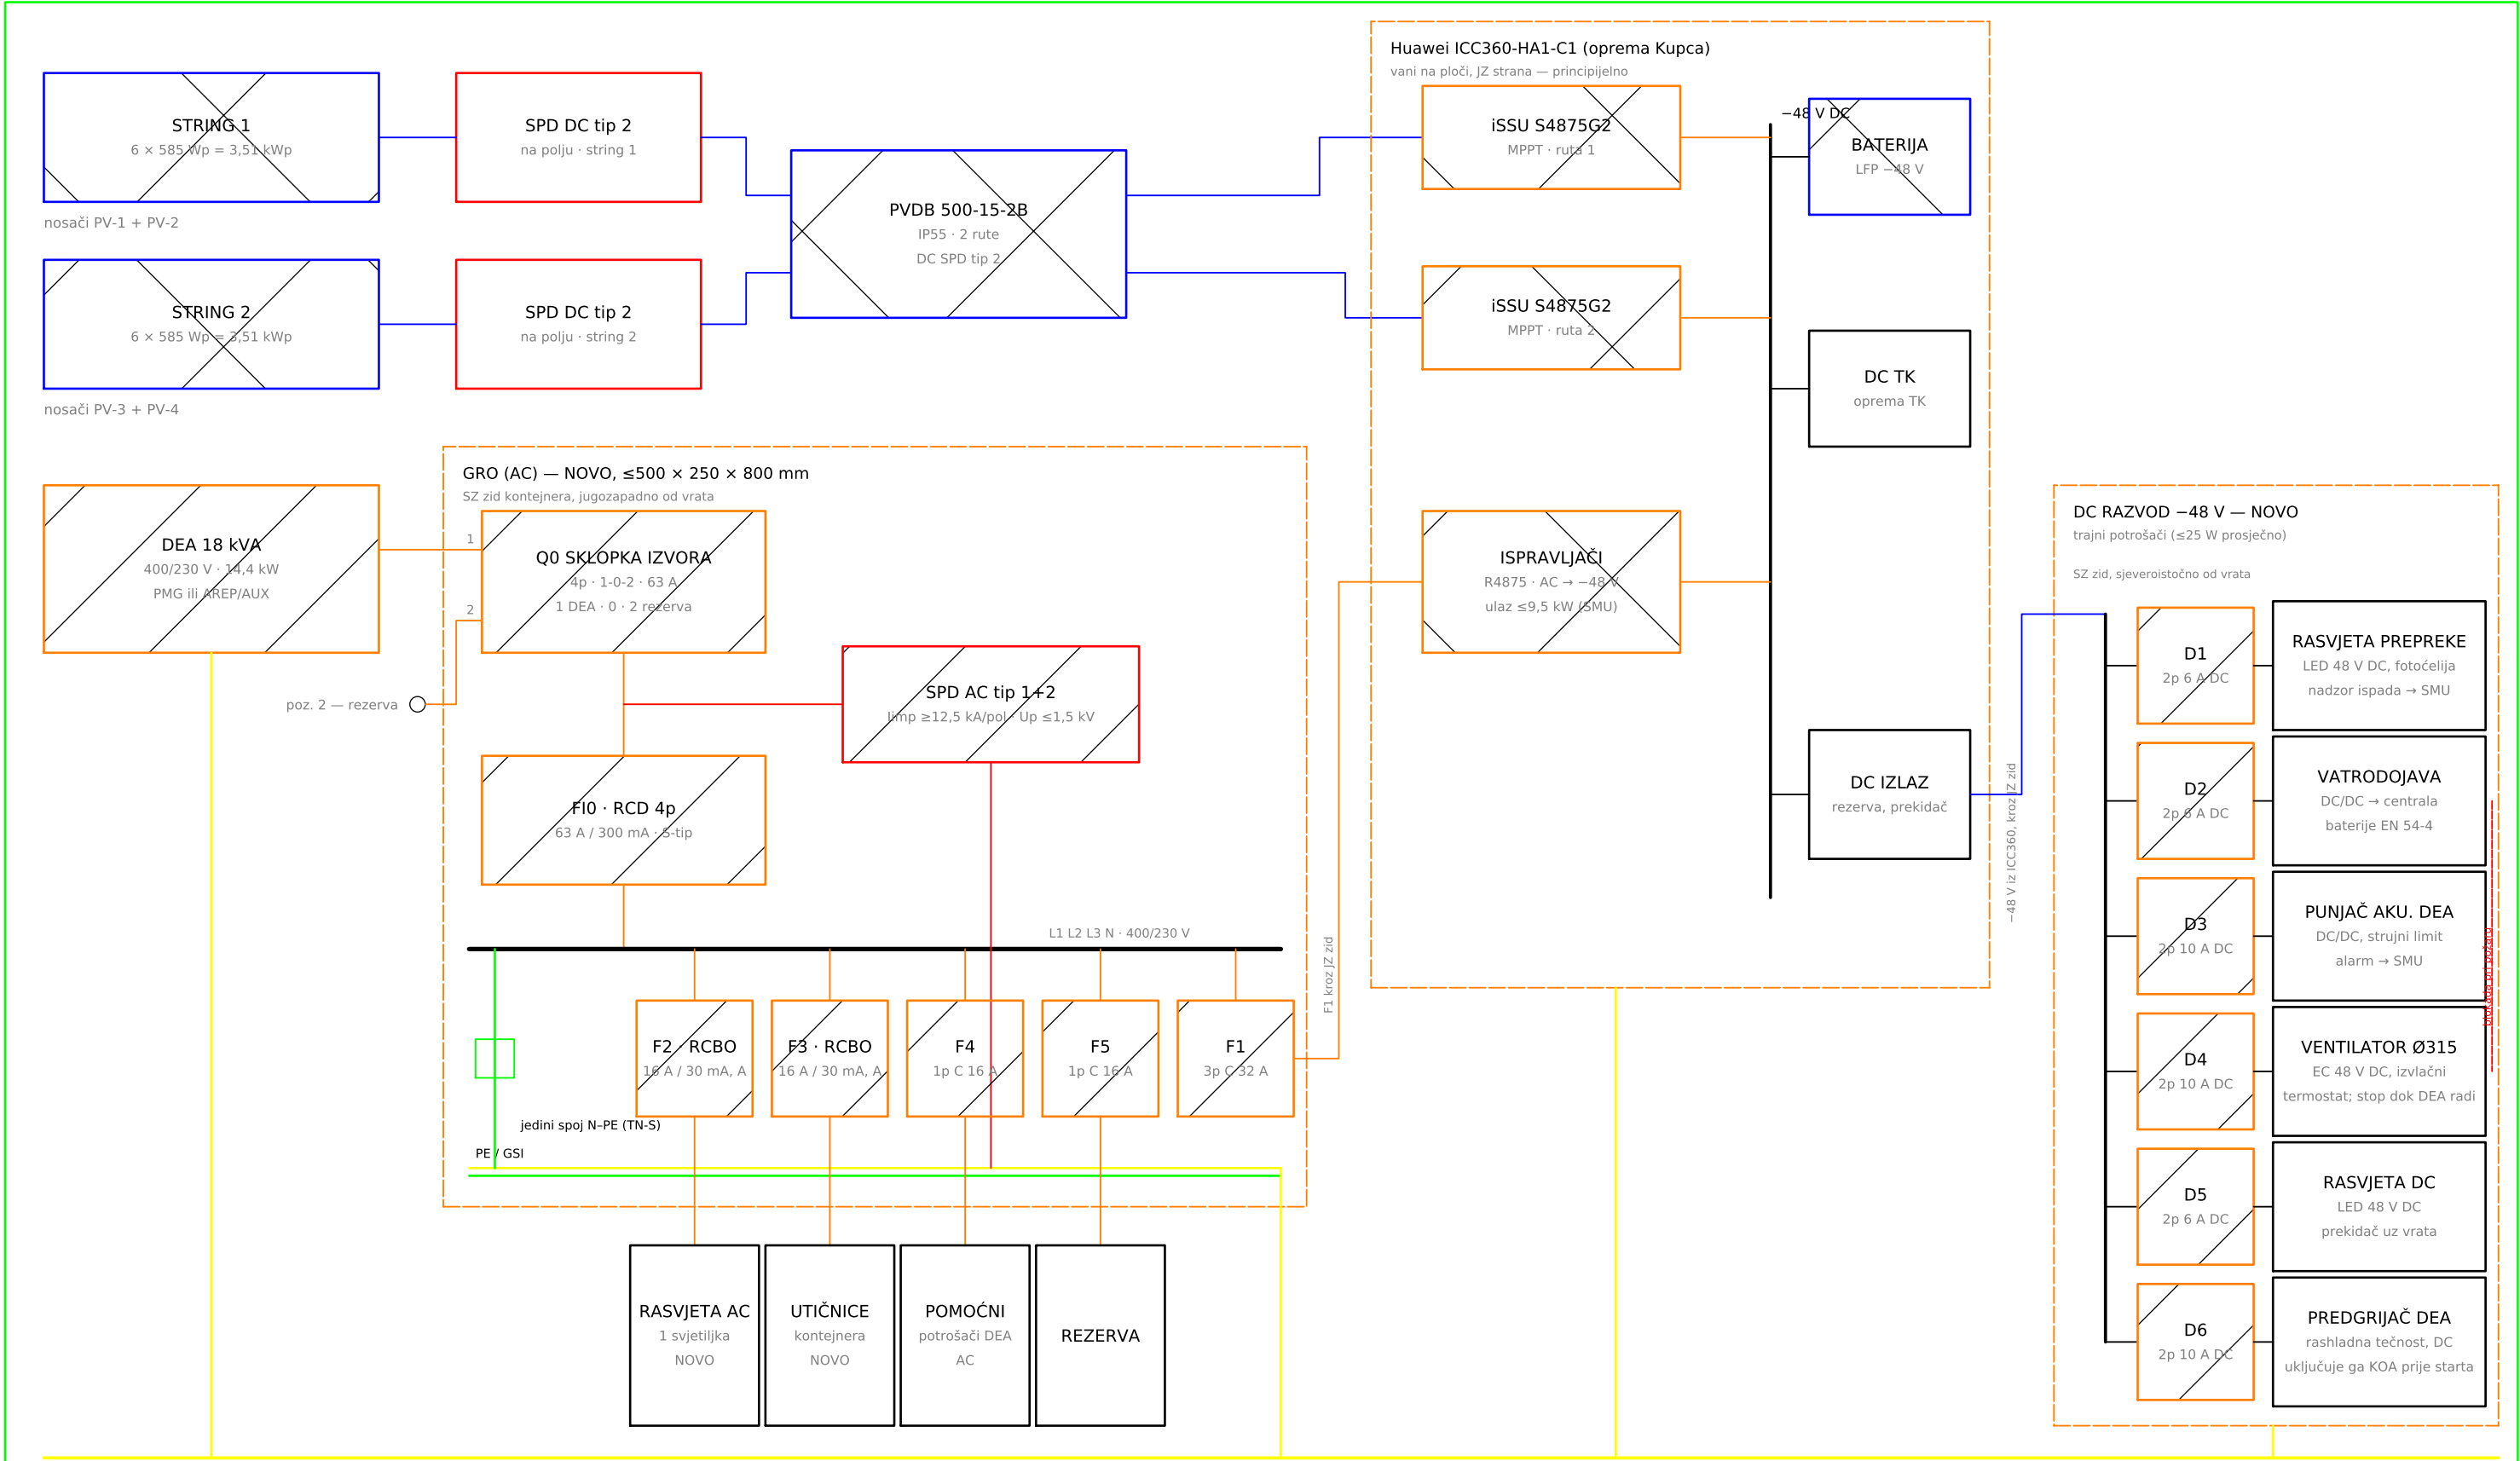

postojeći uzemljivač FeZn 25×4 (2 prstena na 0,8 m + temelji stuba) · R ≤ 10 Ω · nosači FN vezani Cu užetom 50 mm² preko bimetalnih spojeva

- NAPOMENE:**
- Lokacija NIJE na mreži — DEA je jedini AC izvor; izvodi GRO su pod naponom samo dok DEA radi. Trajni potrošači su na DC razvodu -48 V.
 - TN-S: jedini spoj N-PE je u novom GRO; R ≤ 10 Ω. Odvodnici: AC tip 1+2, DC tip 2 po stringu, signalni vodovi EN 61643-21.
 - DEA sa nezavisnom pobudom PMG ili AREP/AUX (≥3 × In ≈ 78 A, ≥10 s); RCD 63 A / 300 mA S-tip je obavezan.
 - Ulaz ispravljača ograničen na 9,5 kW dok radi DEA (SMU). Klima-uređaj Stulz se demontira — nema izvoda za klimatizaciju.
 - FN: 12 modula = 2 stringa × 6; PVDB ima 2 rute → 2 × iSSU S4875G2. Požar: STOP DEA i isključenje ventilatora.
 - Nazivne struje F4-F5 i D1-D6 su orijentacione; presjeke i selektivnost potvrđuje Izvođač. ICC360 — principijelno.

isporuka i montaža Izvođača (DEA, GRO, DC razvod -48 V)

oprema Kupca (FN, PVDB, iSSU, baterije, ICC360)



BH TELECOM d.d. SARAJEVO

Izvršna direkcija za tehnologiju i razvoj servisa

Investitor:

BH Telecom d.d. Sarajevo, Franca Lehara 7, Sarajevo

Objekat:

BS HAMZIĆI (ČITLUK) — autonomni hibridni sistem napajanja

Faza:

Tenderska dokumentacija — Prilog III

Naziv crteža:

Jednopolna šema — novi GRO i DC razvod -48 V

Projektant:

Rusmir Skopljak, dipl. ing. el.

ovjerio:

Rusmir Skopljak, dipl. ing. el.

šifra projekta:

BHT-HAMZICI-2026

razmjera:

—

godina / broj crteža:

2026. H-05