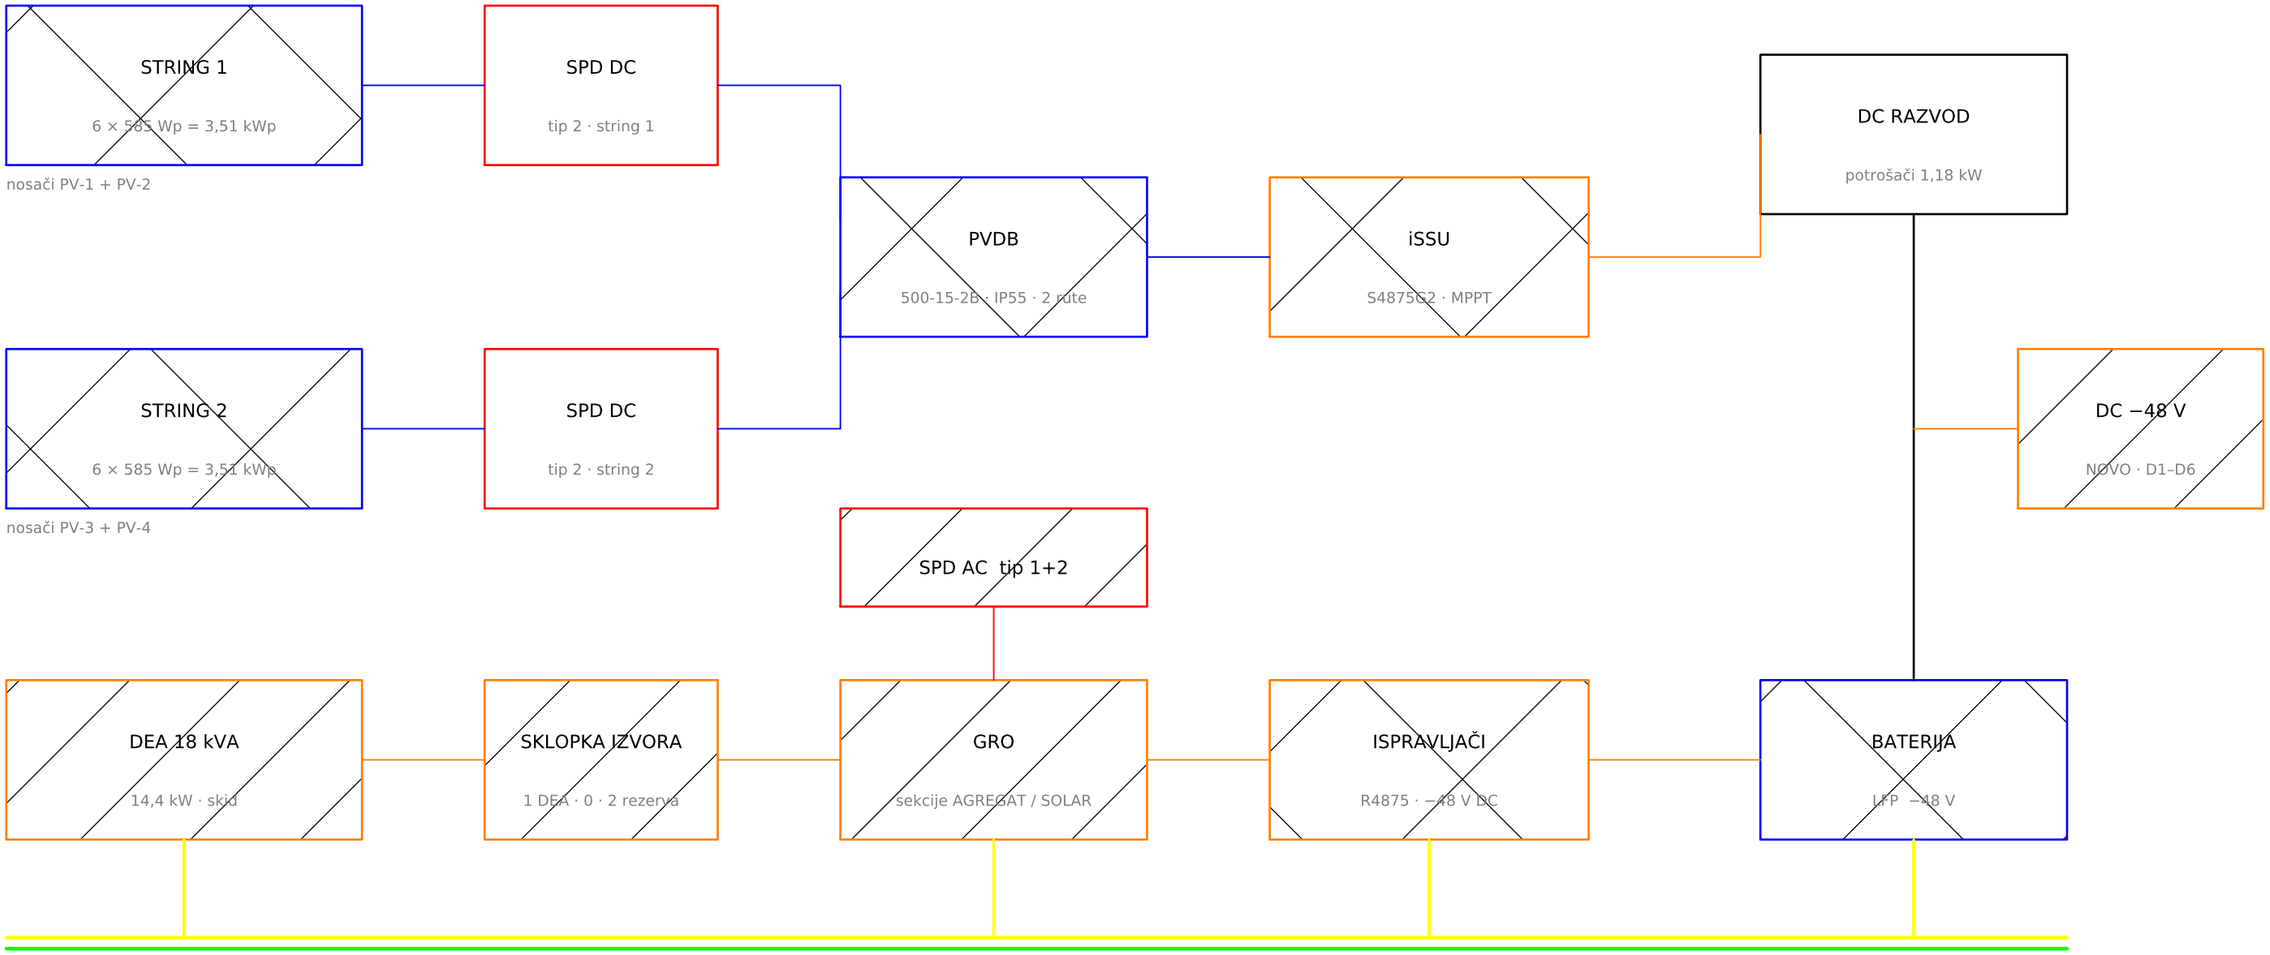



postojeći prstenasti uzemljivač Fe/Zn 25×4 · R ≤ 10 Ω · nosači FN na Cu uže 50 mm²

NAPOMENE:
1 Lokacija nije na mreži; DEA je jedini AC izvor. Sklopka: 1 DEA · 0 · 2 rezerva.
2 TN-S, spoj N–PE samo u novom GRO. Odvodnici: AC tip 1+2, DC tip 2 po stringu.
3 FN: 12 modula = 2 stringa × 6 (PV-1 + PV-2, PV-3 + PV-4); PVDB ima 2 rute.
4 DC razvod −48 V (novo), D1–D6: trajni potrošači prema Prilogu I, Tačka 4.5.

isporuka i montaža Izvođača (LOT 2)

oprema Kupca — ugradnja u LOT 2

BH TELECOM d.d. SARAJEVO
Izvršna direkcija za tehnologiju i razvoj servisa

Investitor:
BH Telecom d.d. Sarajevo, Franca Lehara 7, Sarajevo

Objekat:
BS SJEDNICA (Bileća) — autonomni hibridni sistem napajanja

Faza:
Tenderska dokumentacija — Prilog III

šifra projekta:
BHT-SJEDNICA-2026

Naziv crteža:
Jednopolna shema — hibridni sistem napajanja

razmjera:
—

Projektant:
Rusmir Skopljak, dipl. ing. el.

ovjerio:
Rusmir Skopljak, dipl. ing. el.

godina / broj crteža:
2026. E-01