



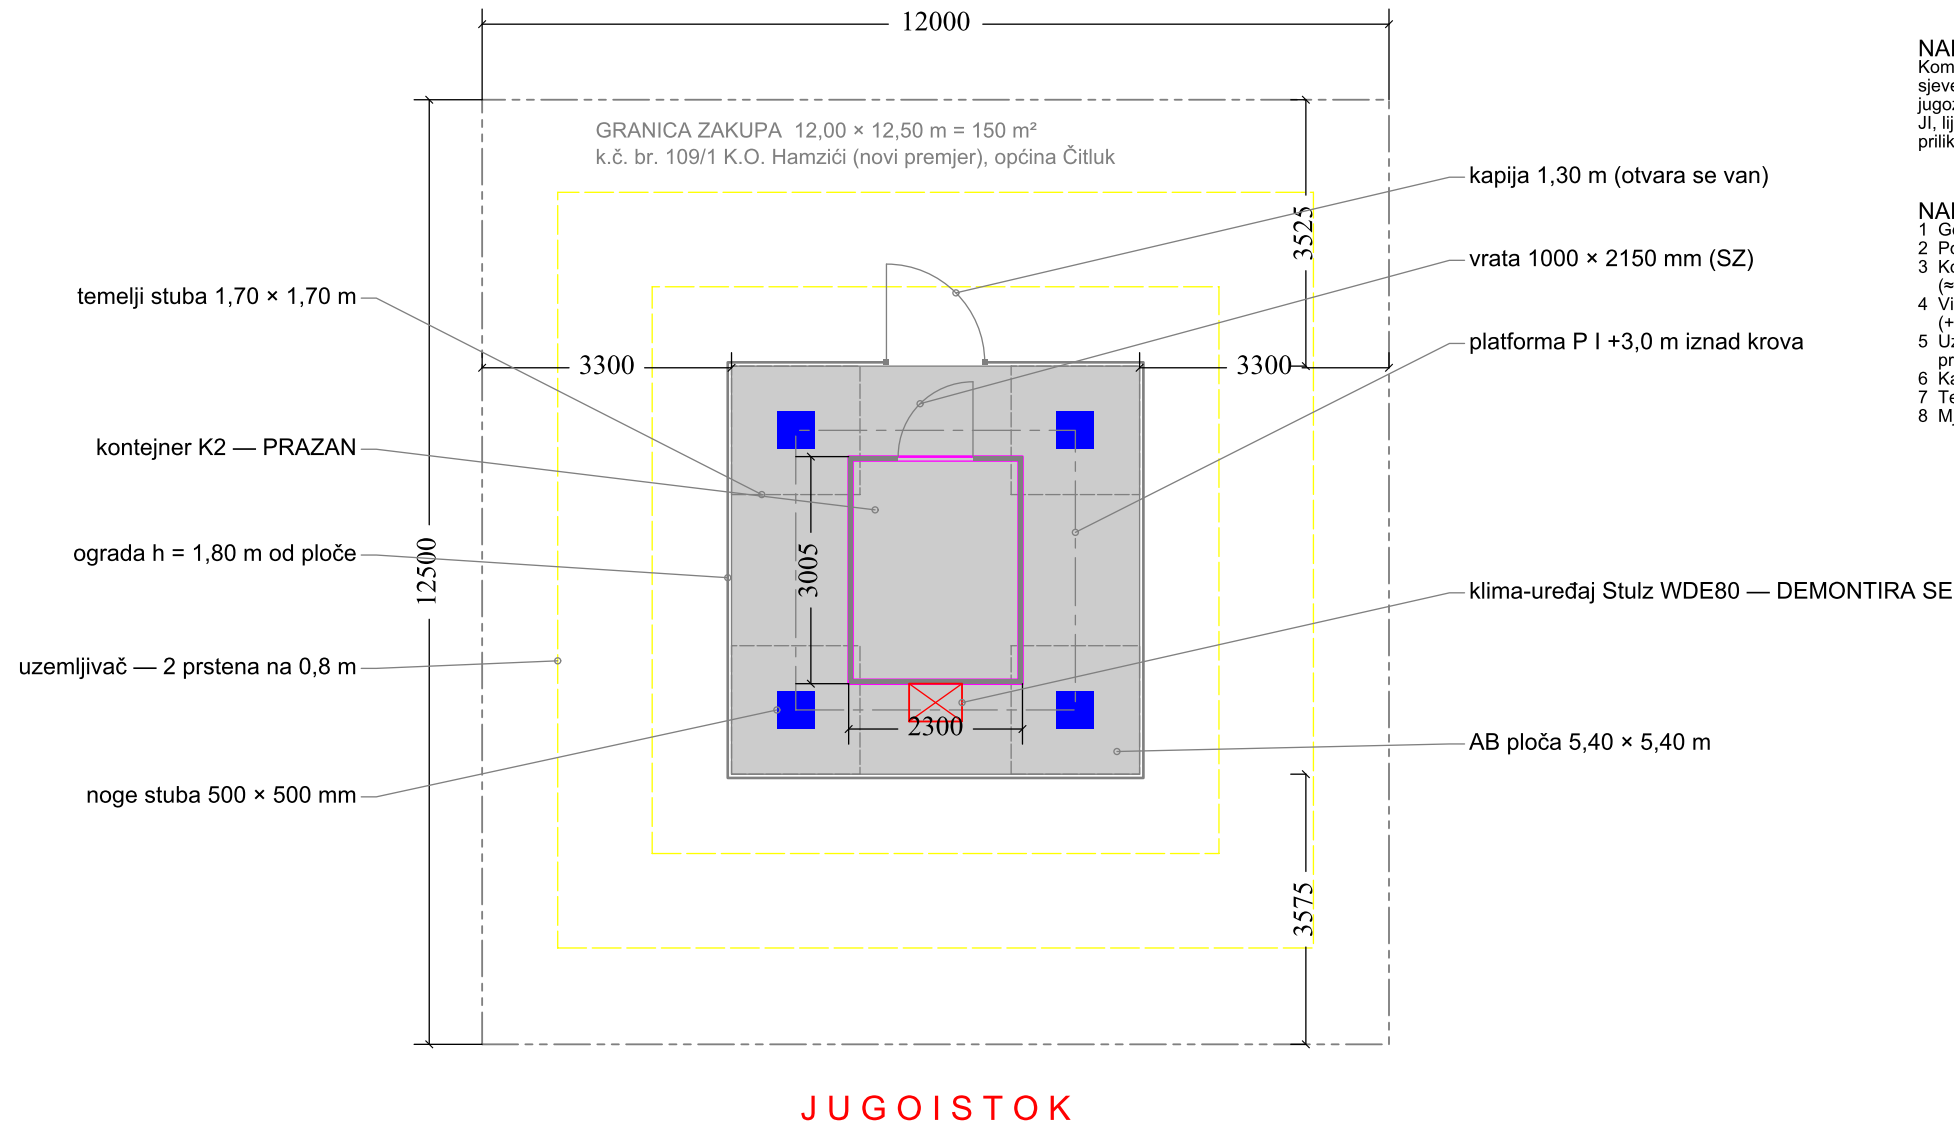

NAPOMENA — ORIJENTACIJA:
Kompleks je zakrenut za 45°: vrata kontejnera i kapija orijentisani su prema sjeverozapadu (SZ), klima-uređaj Stulz prema jugoistoku (JI), a FN polje prema jugozapadu (JZ). Crtež je orijentisan prema kompleksu (gore SZ, desno SI, dolje JI, lijevo JZ); strelica označava pravi sjever. Orijentaciju potvrđuje Ponuđač prilikom obilaska lokacije.

NAPOMENE:
1 Geometrija je preuzeta iz ovjerenog projekta lokacije GP-BS-10472-291 (2017).
2 Površina zakupa iznosi 12,00 × 12,50 m = 150 m², k.č. br. 109/1, općina Čitluk.
3 Kontejner je prazan; na sredini JI zida ugrađen je klima-uređaj Stulz WDE80 (≈700 × 500 × 2200 mm).
4 Visina stuba iznosi 32 m; platforma P I (+3,0 m) nalazi se iznad krova kontejnera (+2,63 / +2,89 m).
5 Uzemljivač FeZn 25×4 mm izveden je kao prsten u temeljima stopa stuba i dva prstena na dubini 0,8 m.
6 Kapija se otvara prema van; širina krila iznosi 1,30 m.
7 Teren uz ploču je na -0,20 m; ograda je visine 1,80 m iznad ploče, odnosno 2,00 m iznad terena.
8 Mjere uređaja i otvora utvrđuju se prilikom obaveznog obilaska lokacije.

- LEGENDA**
- postojeća ograda 5,50 × 5,50 m, h = 1,80 m od ploče (2,00 m od terena) — kapija 1,30 m na SZ strani
 - postojeća AB ploča 5,40 × 5,40 m
 - postojeći kontejner K2 2300 × 3005 mm — vrata na SZ strani
 - noge rešetkastog stuba h = 32 m, baza 3,70 × 3,70 m
 - klima-uređaj Stulz WDE80 (JI zid, u sredini) — demontira se
 - postojeći uzemljivač FeZn 25×4 mm (isprekidano — u tlu)

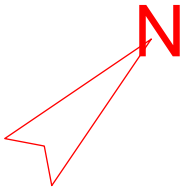

BH TELECOM d.d. SARAJEVO Izvršna direkcija za tehnologiju i razvoj servisa		
Investitor: BH Telecom d.d. Sarajevo, Franca Lebara 7, Sarajevo		
Objekat: BS HAMZIĆI (ČITLUK) — autonomni hibridni sistem napajanja		
Faza: Tenderska dokumentacija — Prilog III		šifra projekta: BHT-HAMZICI-2026
Naziv crteža: Situacija — POSTOJEĆE STANJE		razmjera: 1:100
Projektant: Rusmir Skopljak, dipl. ing. el.	ovjerio: Rusmir Skopljak, dipl. ing. el.	godina / broj crteža: 2026. H-01