


PRESJEK A–A (osa SZ trake nosača PV-2 — pogled prema SJEVEROZAPADU)

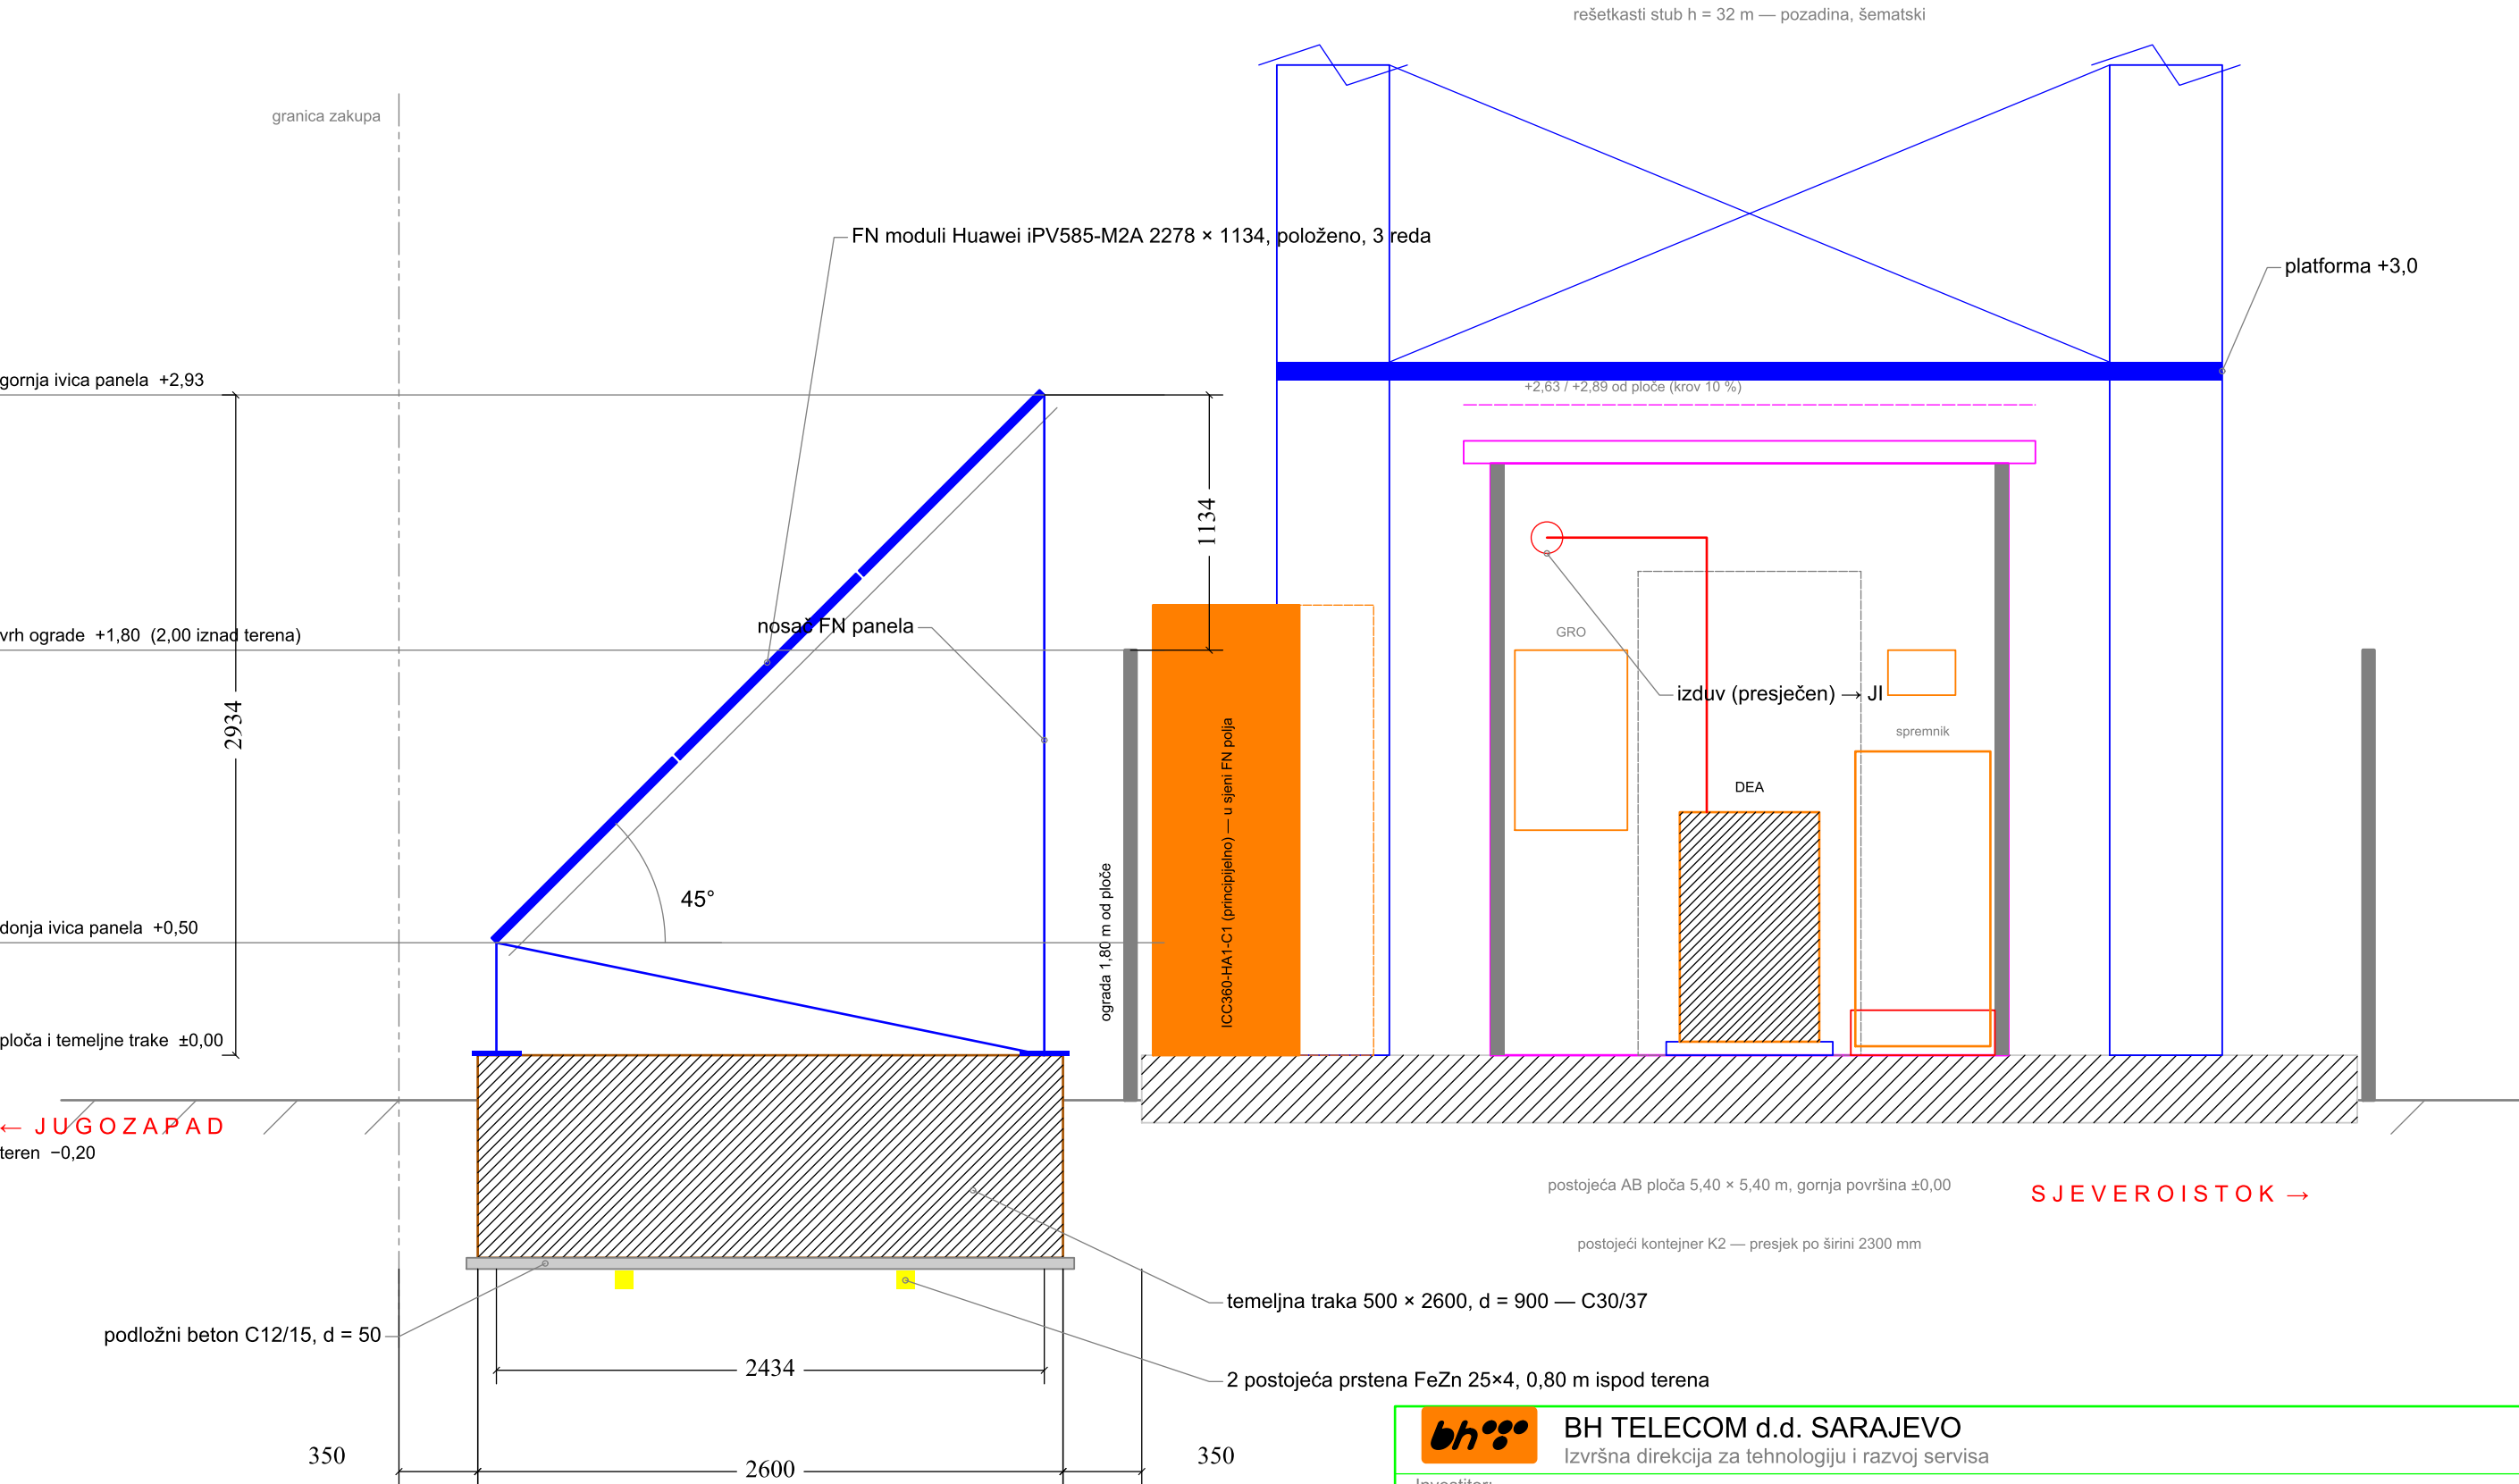

NAPOMENE:
1 FN polje: 3 reda x 1 modul 585 Wp, položeno; nagib 45°, horizontalna projekcija 2434 mm;
4 odvojena nosača u nizu (H-02).
2 Po nosaču dvije temeljne trake 500 x 2600 mm, dubine 900 mm, na razmaku 1600 mm (druga traka je iza ravni presjeka); beton C30/37 (XC4+XF3), armatura B500B, podložni beton C12/15 d = 50 mm.
3 Kote su date od gornje ivice ploče (±0,00), u čijem je nivou i vrh temeljnih traka; teren je na -0,20 m (04_Ograda). Donja ivica panela je na +0,50, gornja na +2,93; vrh ograde je na +1,80, pa je gornja ivica panela 1,13 m iznad ograde.
4 Postojeći prsteni uzemljivača (0,80 m ispod terena) prolaze ispod dna rova; lociraju se, otkopavaju i štite (LOT 1).
5 Trake su udaljene 350 mm od granice zakupa (JZ) i od ploče (SI); položaj presjeka prikazan je na H-02.
6 Stub, platforma P I (+3,0 m), kontejner i ormari prikazani su šematski; ICC360 i MTS nalaze se iza FN polja.

BH TELECOM d.d. SARAJEVO Izvršna direkcija za tehnologiju i razvoj servisa		
Investitor: BH Telecom d.d. Sarajevo, Franca Lehara 7, Sarajevo		
Objekat: BS HAMZIĆI (ČITLUK) — autonomni hibridni sistem napajanja		
Faza: Tenderska dokumentacija — Prilog III		šifra projekta: BHT-HAMZICI-2026
Naziv crteža: Presjek A–A kroz FN polje		razmjera: 1:30
Projektant: Rusmir Skopljak, dipl. ing. el.	ovjerio: Rusmir Skopljak, dipl. ing. el.	godina / broj crteža: 2026. H-03