


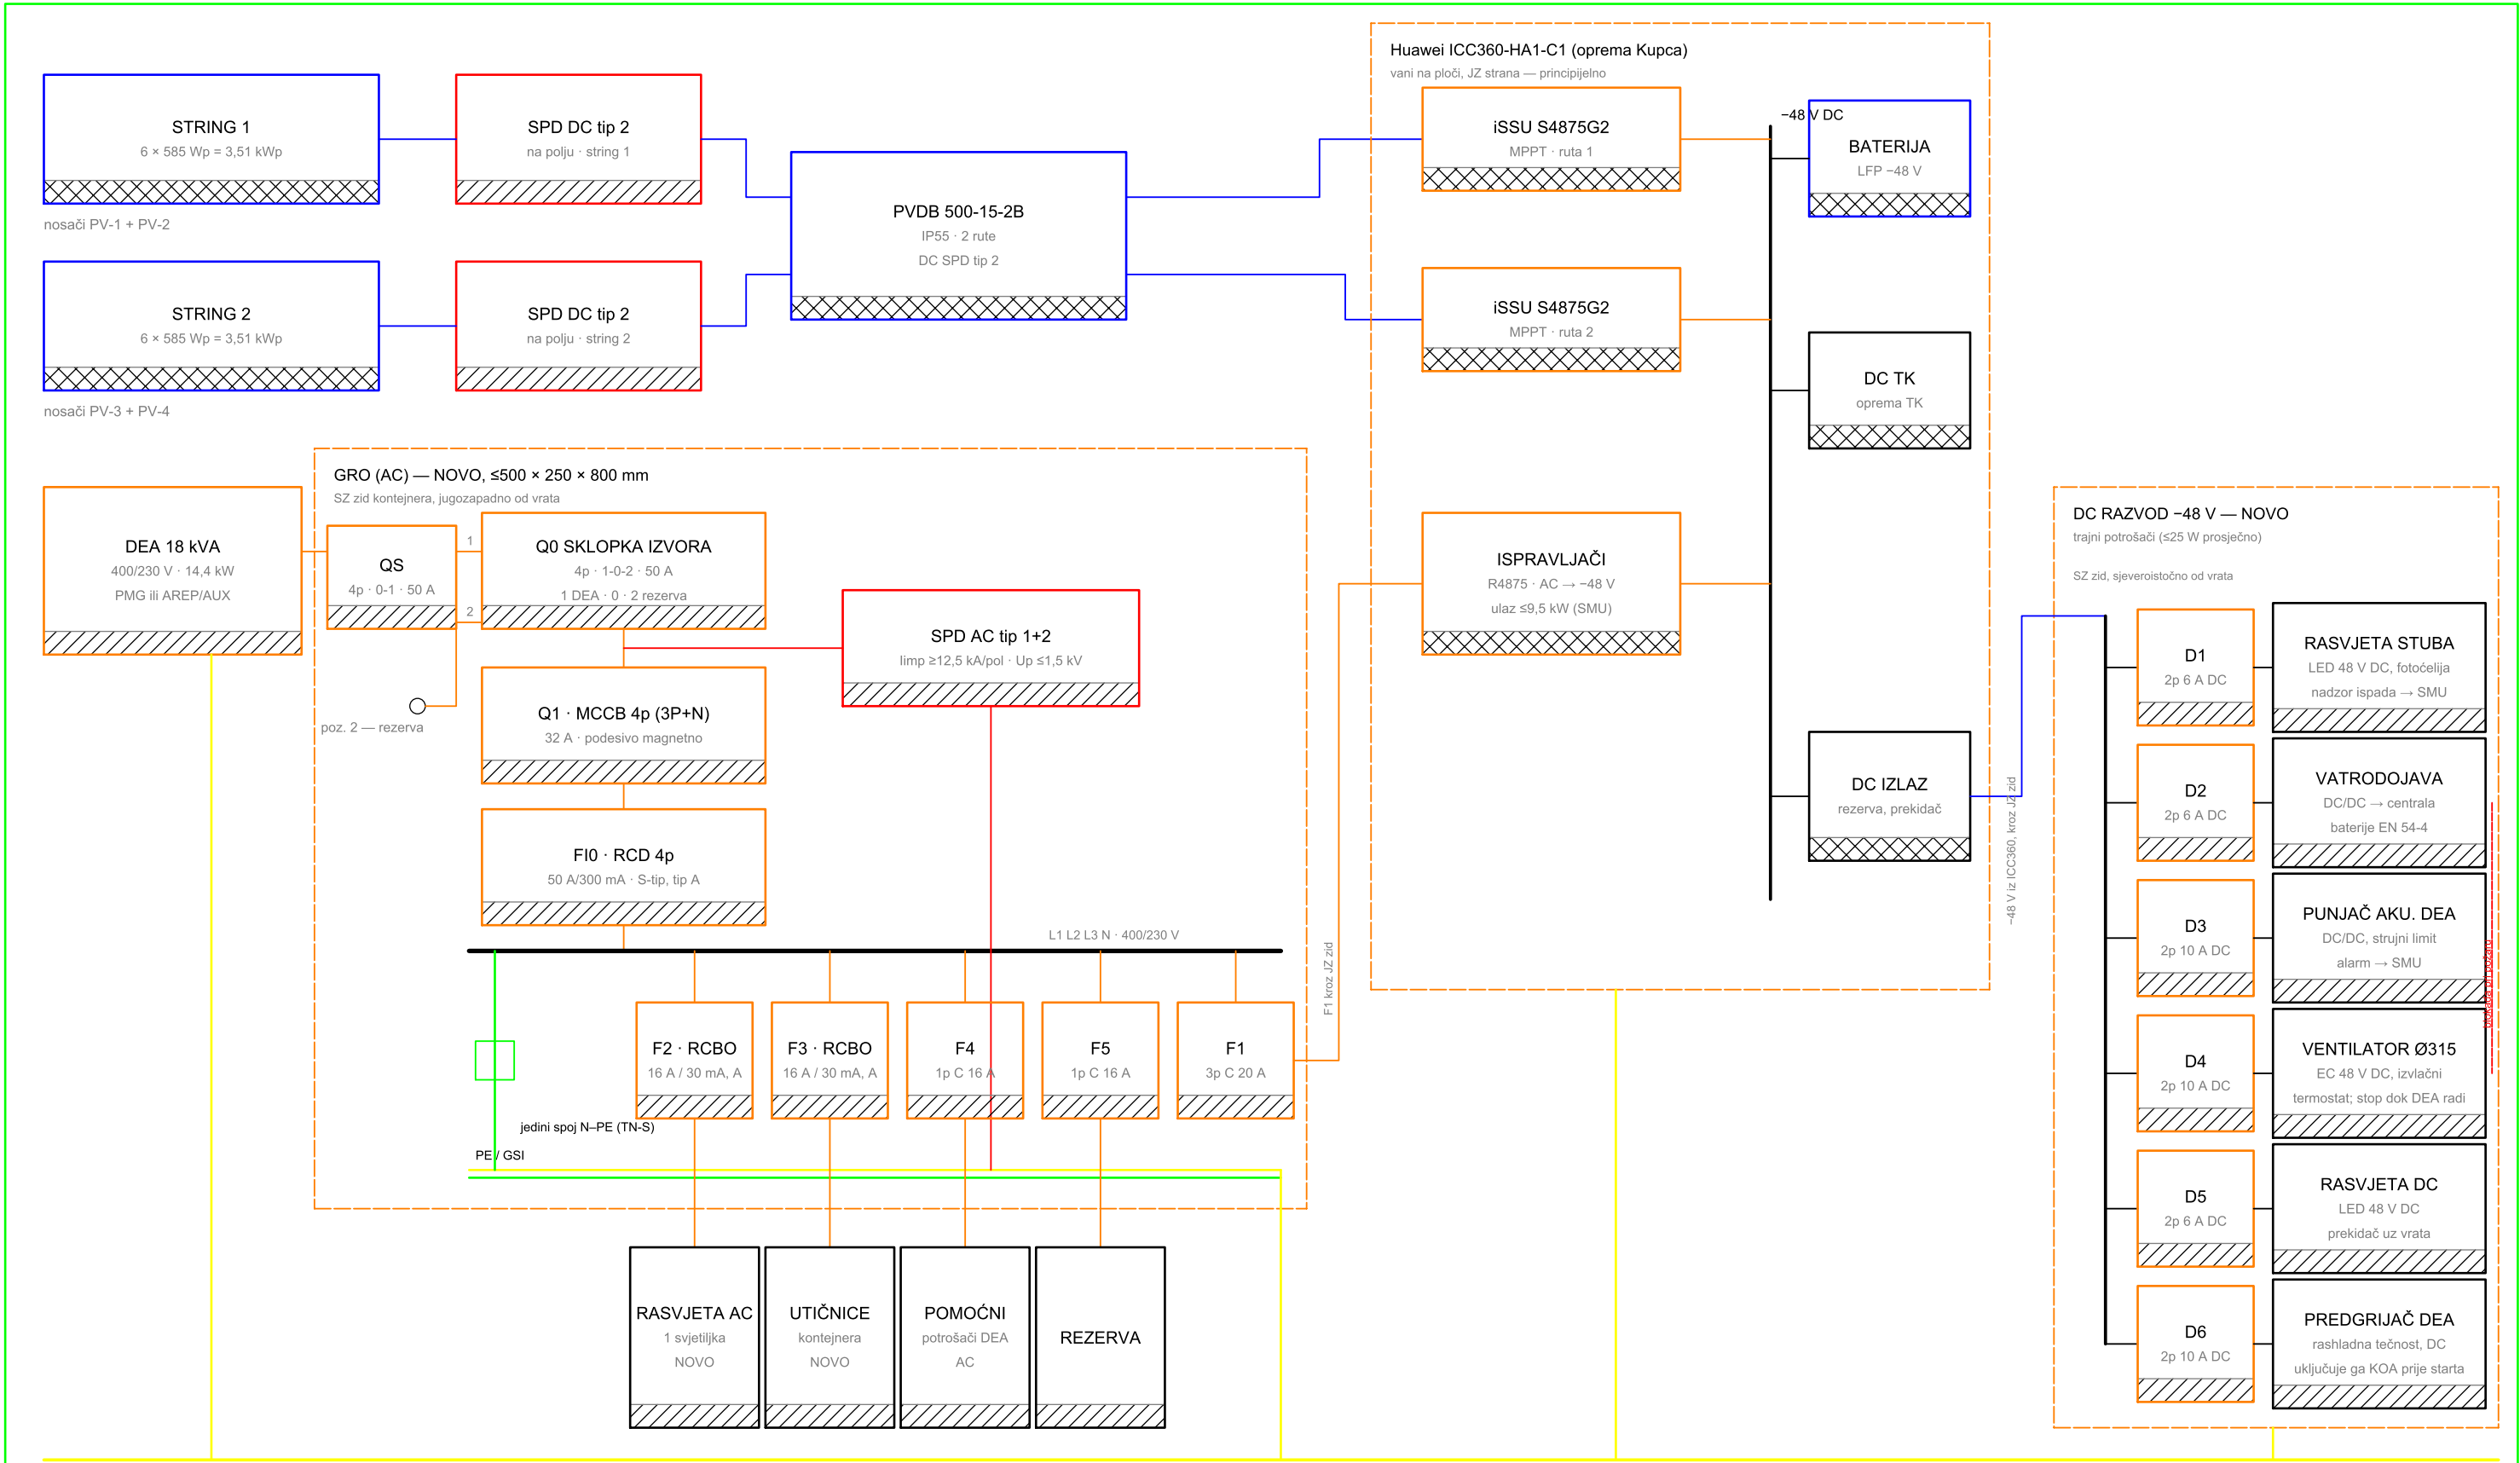

postojeći uzemljivač FeZn 25×4 (2 prstena na 0,8 m + temelji stuba) · R ≤ 10 Ω · nosači FN vezani Cu užetom 50 mm² preko bimetalnih spojeva

NAPOMENE:

- DEA je jedini izvor izmjeničnog napona; izvodi GRO su pod naponom samo za vrijeme rada DEA. Trajni potrošači priključeni su na DC razvod -48 V.
- Sistem TN-S: jedini spoj N-PE izveden je u novom GRO; R ≤ 10 Ω. Odvodnici prenapona: AC tip 1+2, DC tip 2 po stringu, signalni vodovi prema EN 61643-21.
- DEA mora imati nezavisnu pobudu PMG ili AREP/AUX (≥3 × I<sub>n</sub> = 78 A, ≥10 s); zaštitni uređaj diferencijalne struje 50 A / 300 mA, najmanje tip A, S-tip, je obavezan.
- Ulazna snaga ispravljača ograničena je na 9,5 kW za vrijeme rada DEA (SMU). Klima-uređaj Stulz se demontira; izvod za klimatizaciju nije predviđen.
- FN: 12 modula = 2 stringa × 6; PVDB ima 2 rute → 2 × iSSU S4875G2. U slučaju požara DEA se zaustavlja, a ventilator isključuje.
- Nazivne struje F4-F5 i D1-D6 su orijentacione; presjeka i selektivnost potvrđuje Izvođač. ICC360 je prikazan principijelno.



isporuka i montaža Izvođača (DEA, GRO, DC razvod -48 V)



oprema Kupca (FN, PVDB, iSSU, baterije, ICC360)



BH TELECOM d.d. SARAJEVO

Izvršna direkcija za tehnologiju i razvoj servisa

Investitor:

BH Telecom d.d. Sarajevo, Franca Lehara 7, Sarajevo

Objekat:

BS HAMZIĆI (ČITLUK) — autonomni hibridni sistem napajanja

Faza:

Tenderska dokumentacija — Prilog III

Naziv crteža:

Jednopolna šema — novi GRO i DC razvod -48 V

Projektant:

Rusmir Skopljak, dipl. ing. el.

ovjerio:

Rusmir Skopljak, dipl. ing. el.

šifra projekta:

BHT-HAMZICI-2026

razmjera:

—

godina / broj crteža:

2026. H-05