



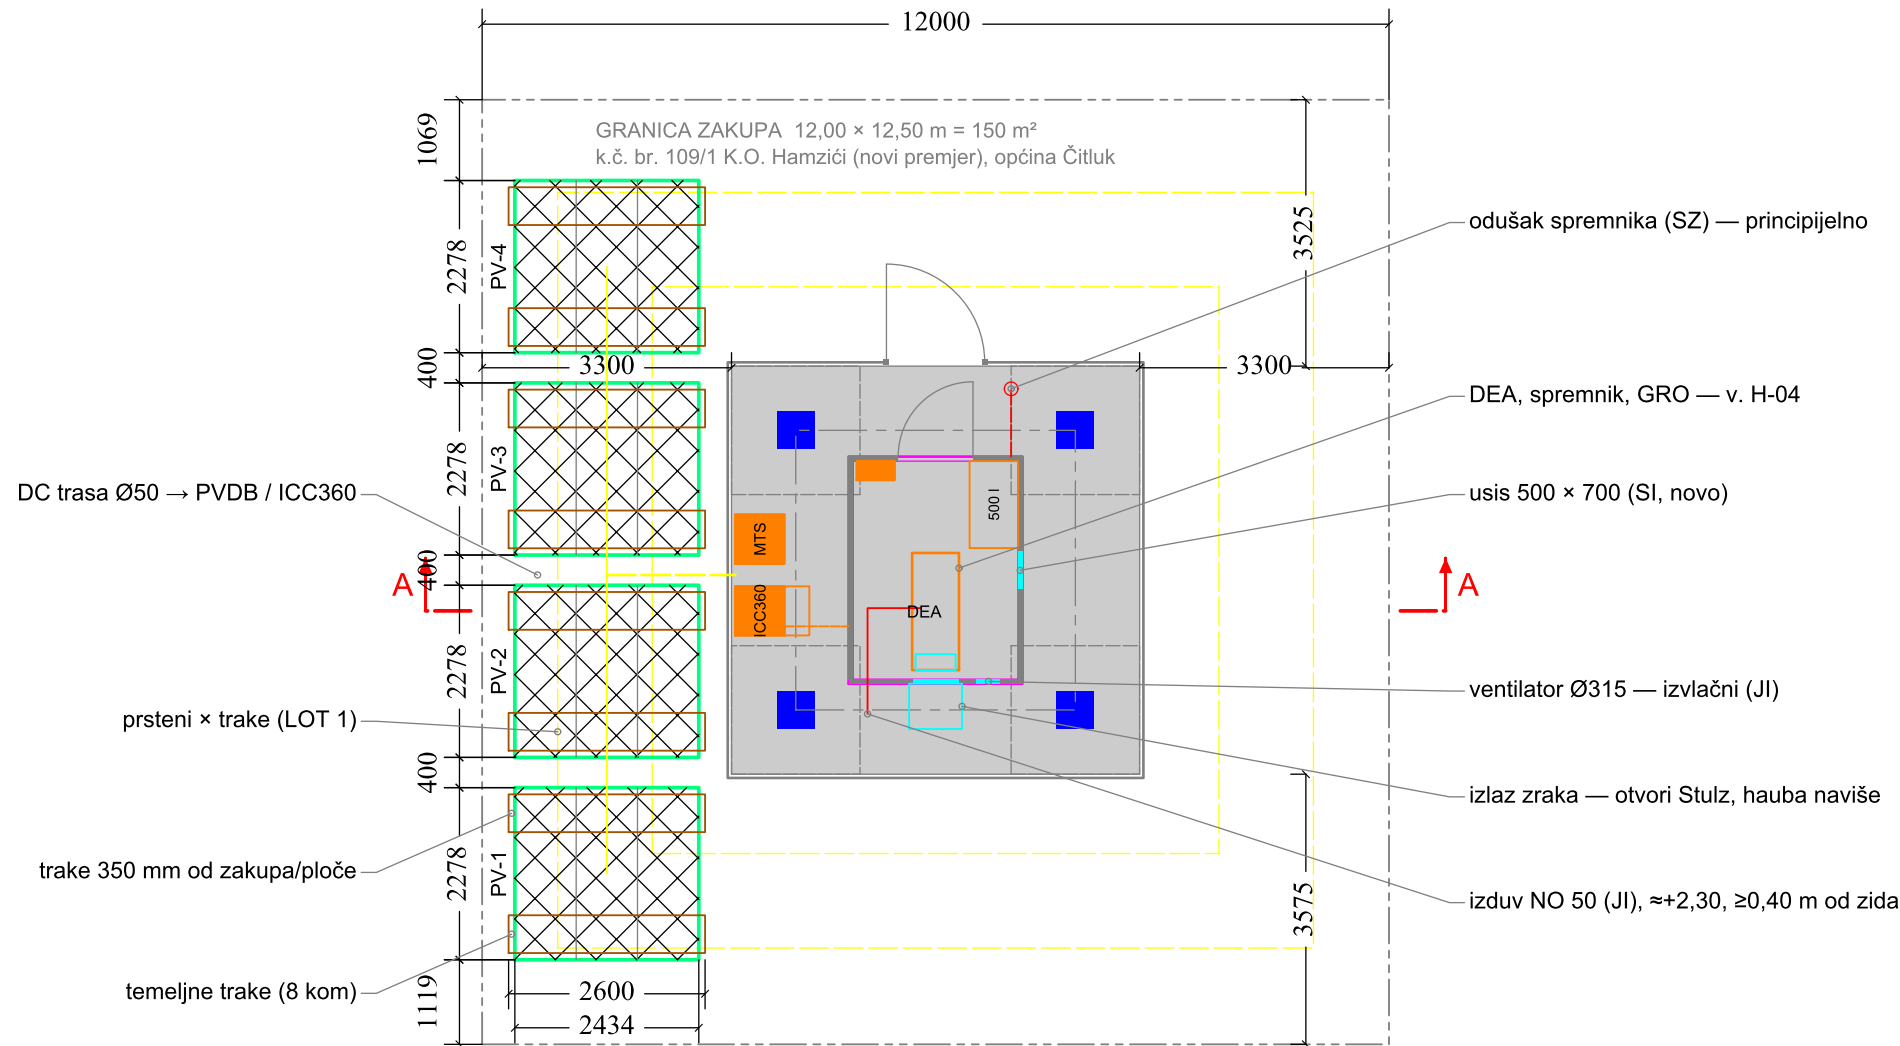

NAPOMENA — ORIJENTACIJA:
Kompleks je zakrenut za 45°: vrata kontejnera i kapija orijentisani su prema sjeverozapadu (SZ), klima-uređaj Stulz prema jugoistoku (JI), a FN polje prema jugozapadu (JZ). Crtež je orijentisan prema kompleksu (gore SZ, desno SI, dolje JI, lijevo JZ); strelica označava pravi sjever. Orijentaciju potvrđuje Ponuđač prilikom obilaska lokacije.

NAPOMENE:
1 Nosači su orijentisani prema jugozapadu (azimut 225°), nagib 45°; kote ivica panela su +0,50 / +2,93 m od gornje ivice ploče.
2 Niz čine 4 odvojena nosača: 4 × 2278 + 3 × 400 = 10312 mm, u JZ pojasu.
3 Temeljne trake 500 × 2600 mm, dubine 900 mm, na podložnom betonu d = 50 mm; vrh trake je u nivou ploče, 0,20 m iznad terena.
4 Postojeći prsteni uzemljivača (0,8 m ispod terena) prolaze ispod temeljnih traka; lociraju se i štite u okviru LOT 1.
5 Nosači i temelji izvode se prema tehničkom rješenju i statičkom proračunu Ponuđača.
6 Raspored opreme u kontejneru prikazan je na crtežu H-04.
7 Ormari ICC360-HA1-C1 i MTS prikazani su iza FN polja principijelno.

LEGENDA
■ FN nosači PV-1..PV-4 — po 3 × 585 Wp (1 × 3, položeno), 45°, azimut 225° (JZ) — 2 stringa × 6
■ AB temeljne trake 500 × 2600 mm, d = 900 mm, razmak 1600 mm — 8 kom
■ DC trasa u PEHD Ø50 (isprekidano) — od polja do PVDB uz ICC360
■ DEA 18 kVA (skid), spremnik 500 I u koritu, novi GRO
■ usis 500 × 700 (SI), izlaz zraka kroz otvore Stulz (JI) i haubu naviše, ventilator Ø315 (JI)
■ izdub NO 50 (JI, ≈+2,30 m); odušak spremnika (SZ, isprekidano); presjek A–A
■ Huawei ICC360-HA1-C1 i MTS vani na ploči (JZ), iza FN polja — principijelno

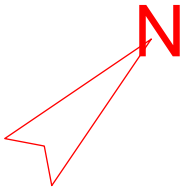

BH TELECOM d.d. SARAJEVO
Izvršna direkcija za tehnologiju i razvoj servisa

Investitor:
BH Telecom d.d. Sarajevo, Franca Lehara 7, Sarajevo

Objekat:
BS HAMZIĆI (ČITLUK) — autonomni hibridni sistem napajanja

Faza:
Tenderska dokumentacija — Prilog III

šifra projekta:
BHT-HAMZICI-2026

Naziv crteža:
Situacija — BUDUĆE STANJE

razmjera:
1:100

Projektant:
Rusmir Skopljak, dipl. ing. el.

ovjerio:
Rusmir Skopljak, dipl. ing. el.

godina / broj crteža:
2026. H-02