



OSNOVA — kontejner je PRAZAN; klima-uređaj Stulz se demontira

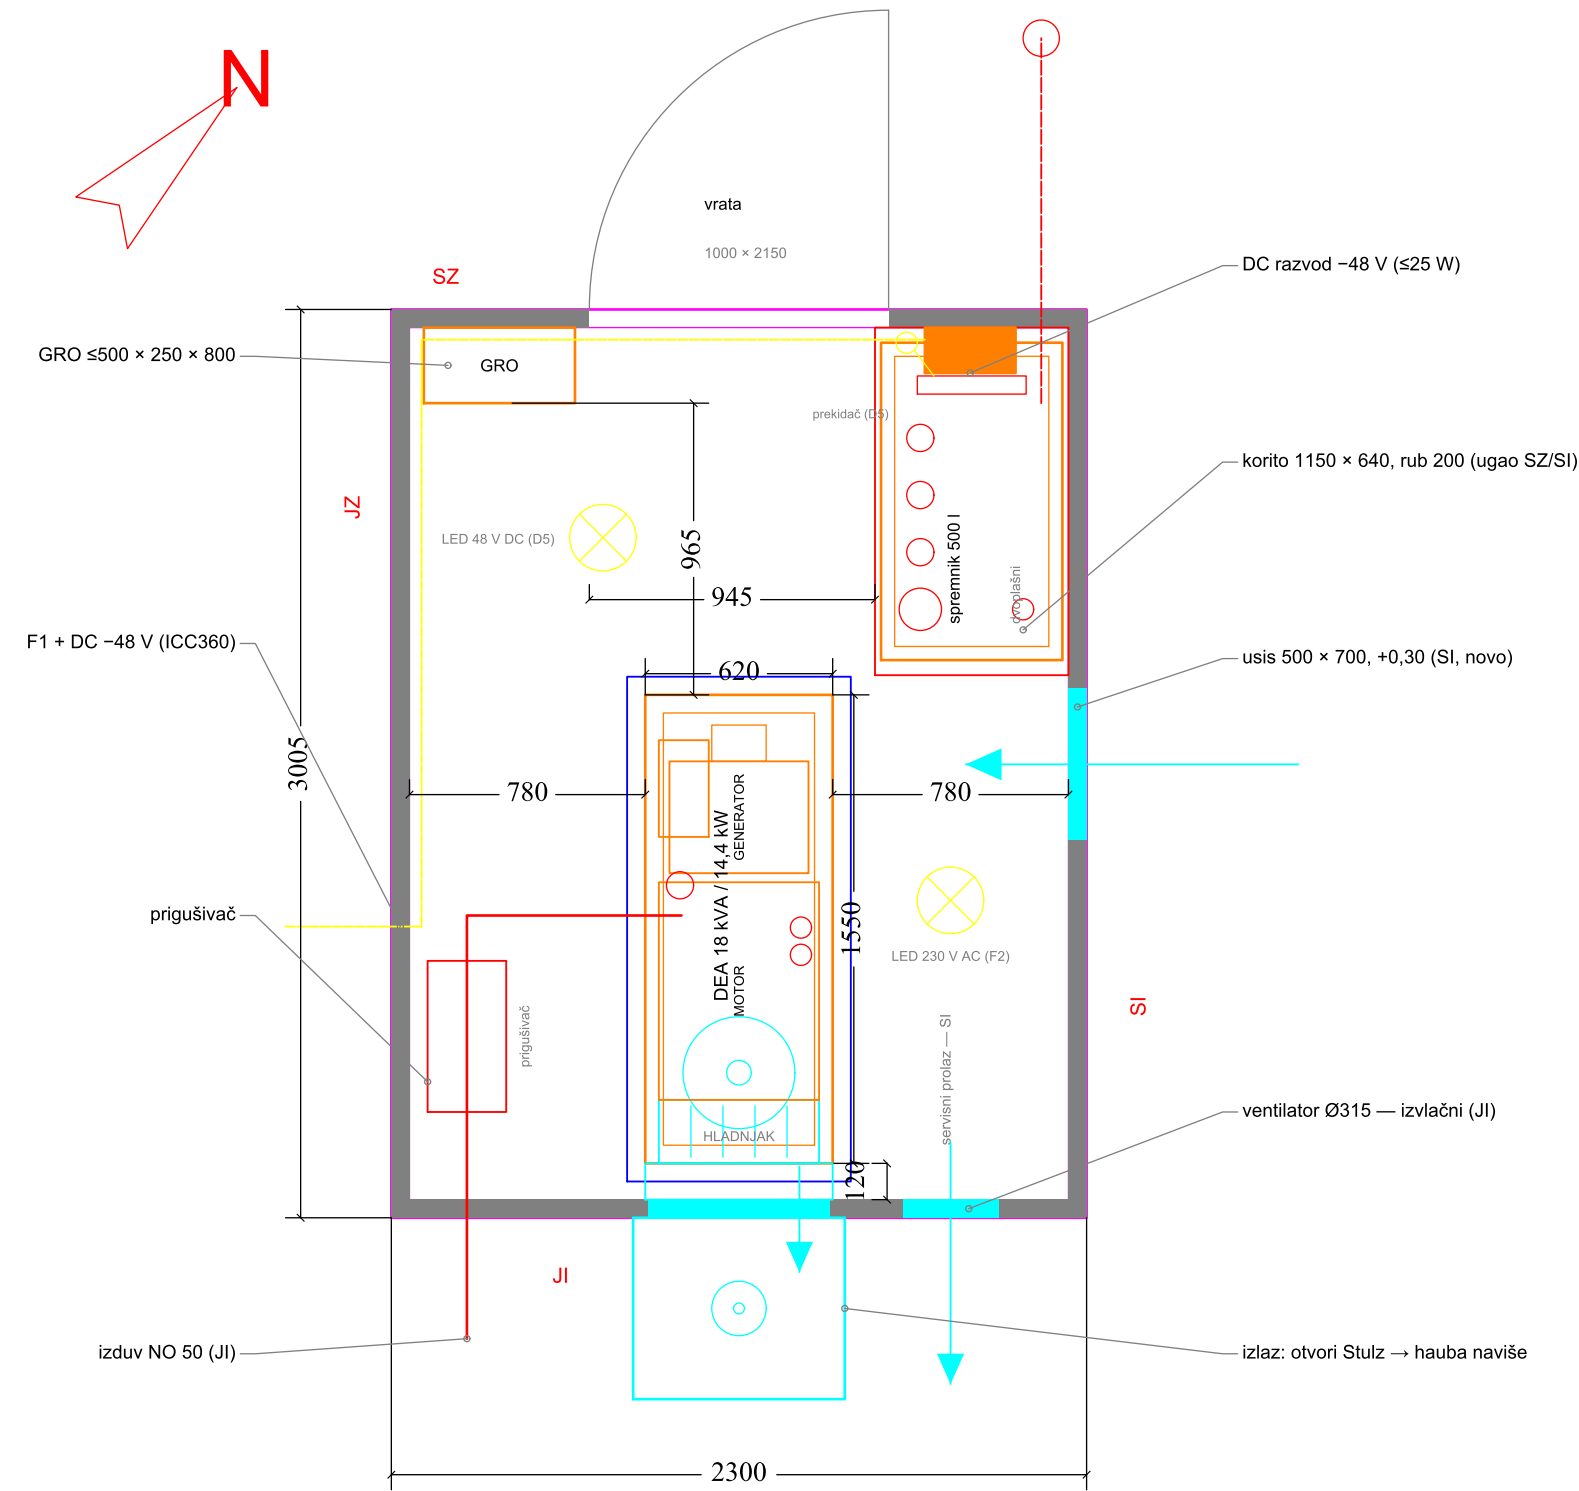

- NAPOMENE:**
- Dizel-električni agregat FG Wilson P18-6 (skid) ili ekvivalent, 18 kVA / 14,4 kW; osa SZ–JI, hladnjak prema JI.
 - Izlaz zraka kroz postojeće otvore klima-uređaja Stulz (sredina JI zida), najmanje 0,36 m² bruto; limeni plenum i hauba 700 × 600 mm usmjeravaju topli zrak naviše.
 - Usis zraka 500 × 700 mm na SI zidu (+0,30 m). Izduv NO 50 kroz JI zid na ≈+2,30 m, ispod platforme stuba.
 - GRO dimenzija do 500 × 250 × 800 mm na SZ zidu; dvoplašni spremnik 500 l u koritu 1150 × 640 mm; roštilj ispod skida i korita je obavezan.
 - Servisni prolazi iznose 780 / 780 mm i 965 mm do GRO; skid širine 620 mm unosi se kroz vrata širine 990 mm.
 - Ventilator Ø315 (JI zid, izvlačni, D4) i DC razvod –48 V istočno od vrata prikazani su na H-05.
 - Raspored je principijelan; mjere otvora i servisne tačke potvrđuje Ponuđač na licu mjesta. Zahtjevi: Prilog I, Tačka 4.

PRESJEK 1–1 (os agregata — pogled prema SI, SZ lijevo)

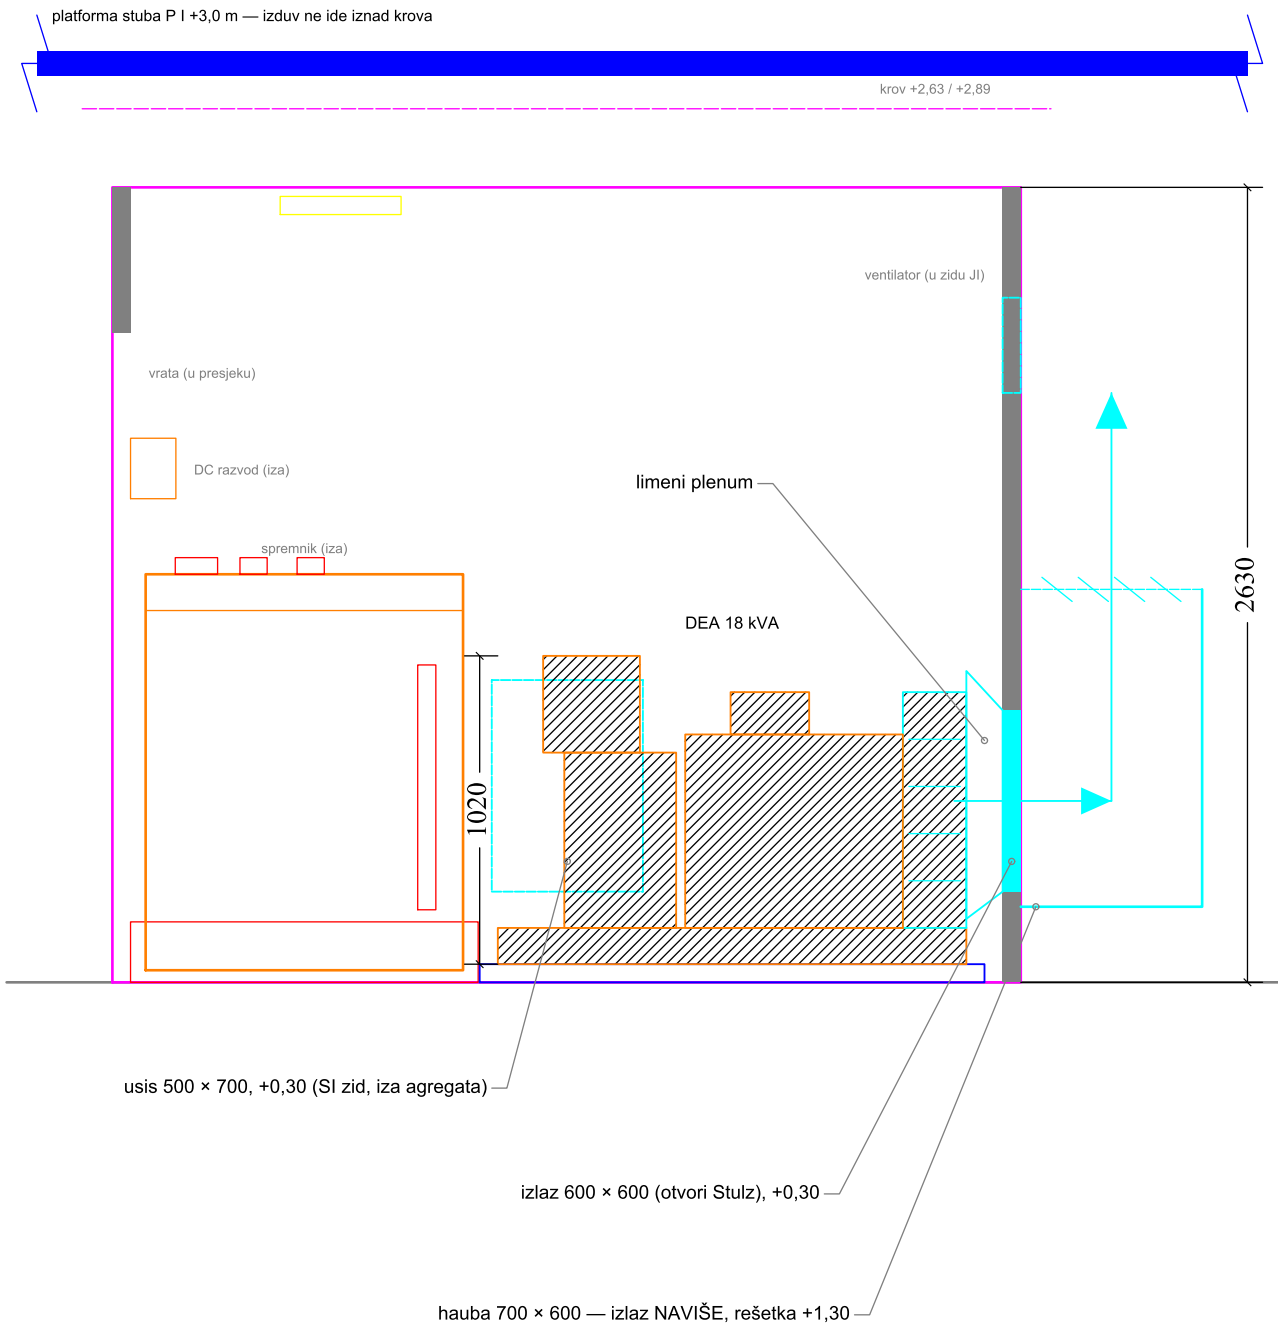

BH TELECOM d.d. SARAJEVO

Izvršna direkcija za tehnologiju i razvoj servisa

Investitor:

BH Telecom d.d. Sarajevo, Franca Lebara 7, Sarajevo

Objekat:

BS HAMZIĆI (ČITLUK) — autonomni hibridni sistem napajanja

Faza:

Tenderska dokumentacija — Prilog III

Naziv crteža:

Agregat u kontejneru — osnova i presjek 1–1

Projektant:

Rusmir Skopljak, dipl. ing. el.

ovjerio:

Rusmir Skopljak, dipl. ing. el.

šifra projekta:

BHT-HAMZICI-2026

razmjera:

1:25

godina / broj crteža:

2026. H-04