


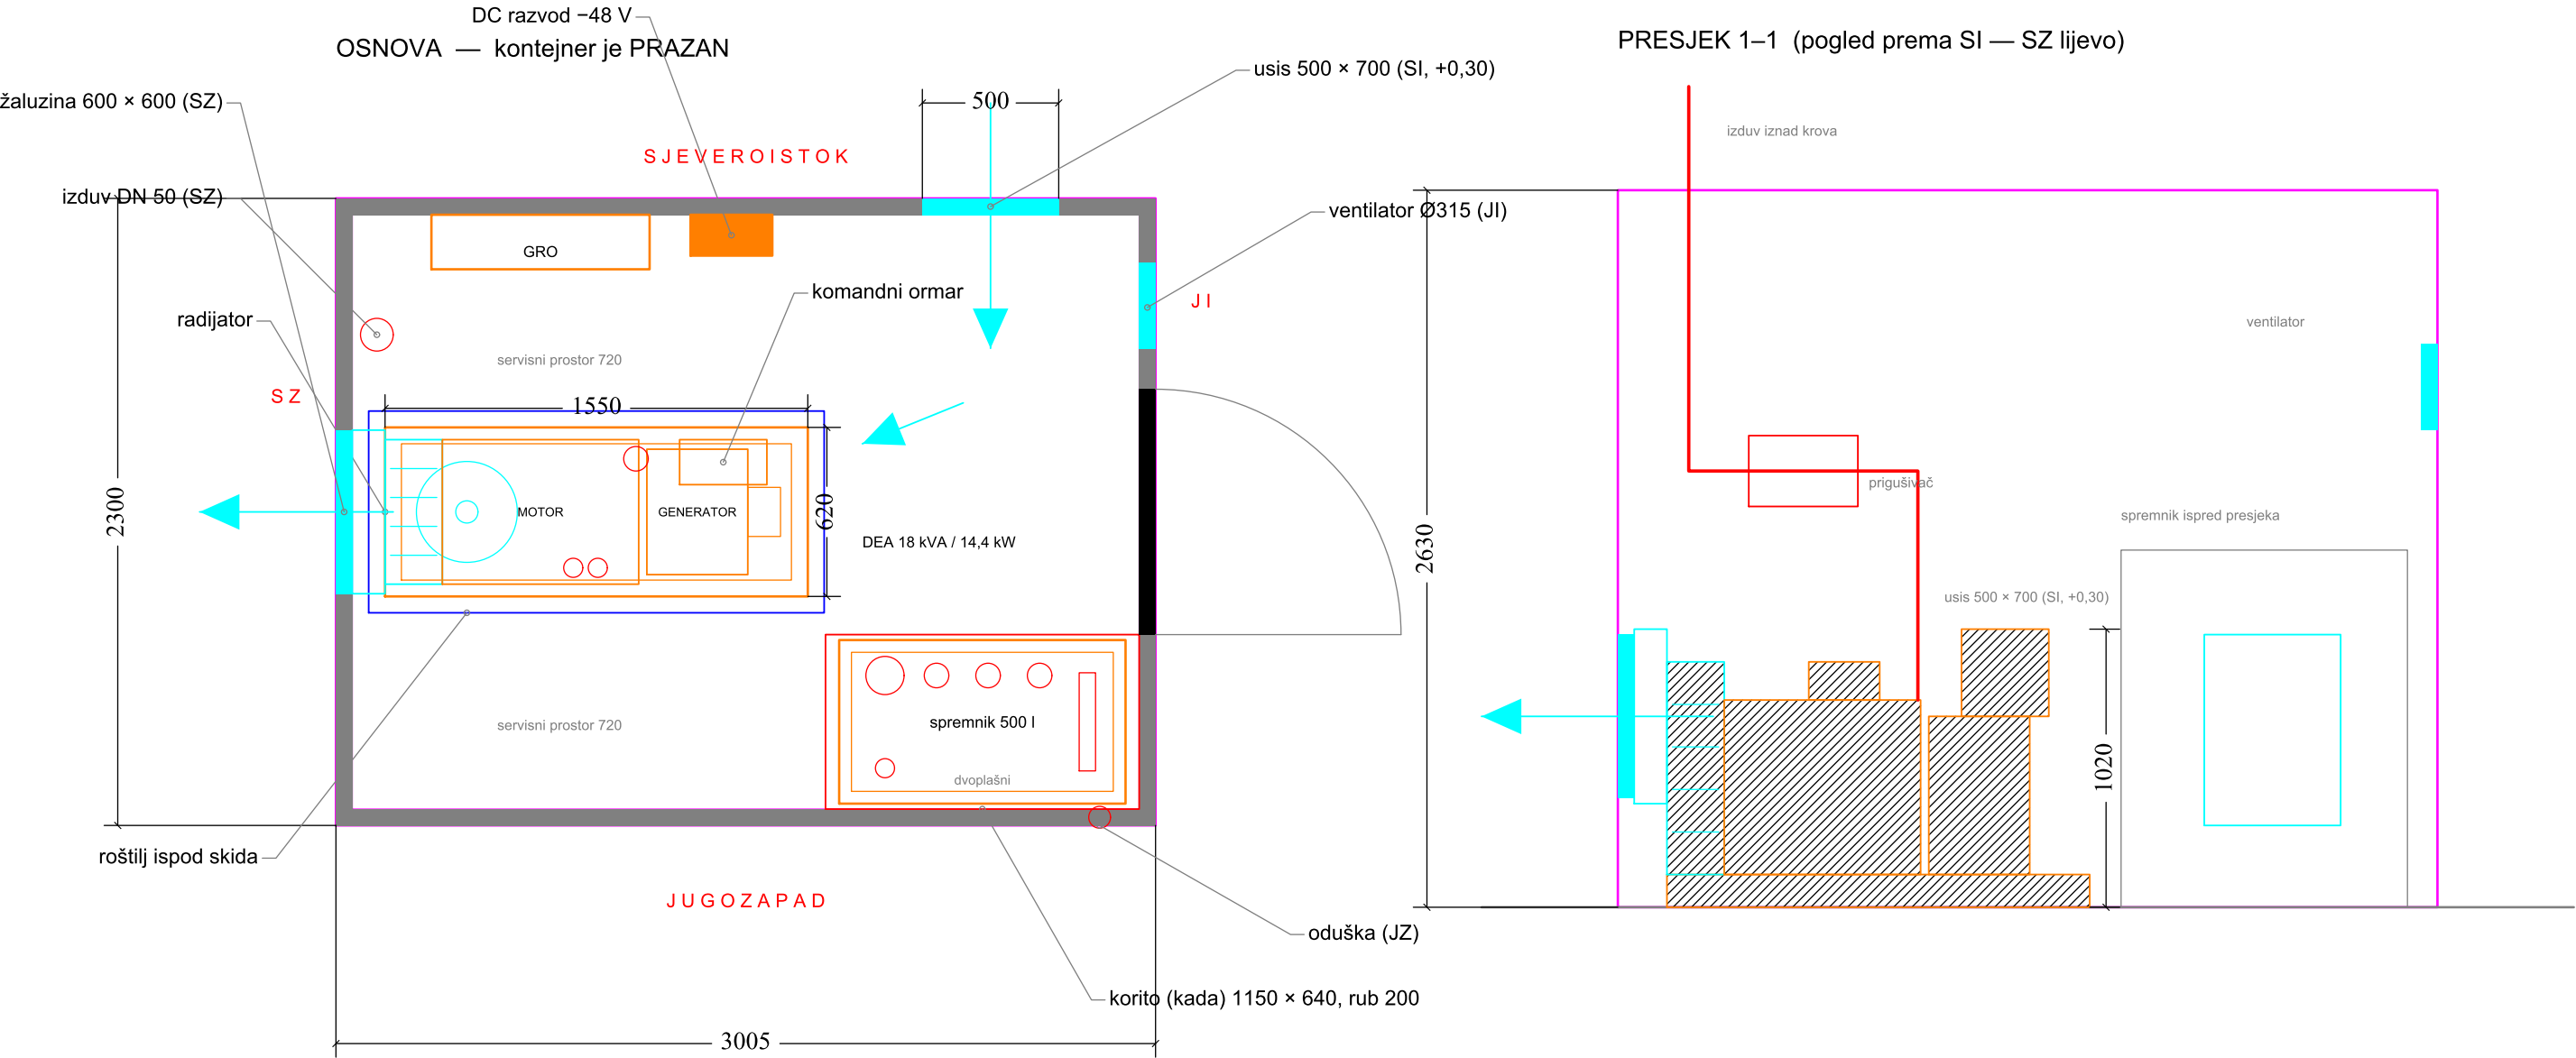

- NAPOMENE:
- 1 Dizel-električni agregat FG Wilson P18-6 (skid) ili ekvivalent, 18 kVA / 14,4 kW.
 - 2 Usis zraka 500 × 700 mm na SI zidu (+0,30 m); kanal i žaluzina 600 × 600 mm i izduv DN 50 na SZ zidu; oduška na JZ zidu; ventilator Ø315 na JI zidu.
 - 3 Roštilj ispod skida i ispod korita je obavezan.
 - 4 Spremnik je dvoplašni; ispod njega je korito 1150 × 640 mm, visine ruba 200 mm.
 - 5 Servisni prolazi 720 mm (JZ), 720 mm (SI) i 1155 mm (JI) moraju ostati slobodni.
 - 6 Skid širine 620 mm unosi se kroz vrata širine 900 mm. Kontejner je prazan.
 - 7 DC razvod -48 V nalazi se na SI zidu uz GRO; trajni potrošači D1–D6 prikazani su na E-01.
 - 8 Raspored je principijelan i potvrđuje se na licu mjesta. Zahtjevi: Prilog I, Tačka 4.

bh BH TELECOM d.d. SARAJEVO Izvršna direkcija za tehnologiju i razvoj servisa		
Investitor: BH Telecom d.d. Sarajevo, Franca Lehara 7, Sarajevo		
Objekat: BS SJEDNICA (Bileća) — autonomni hibridni sistem napajanja		
Faza: Tenderska dokumentacija — Prilog III		šifra projekta: BHT-SJEDNICA-2026
Naziv crteža: DEA u postojećem kontejneru — osnova i presjek		razmjera: 1:25
Projektant: Rusmir Skopljak, dipl. ing. el.	ovjerio: Rusmir Skopljak, dipl. ing. el.	godina / broj crteža: 2026. M-01