


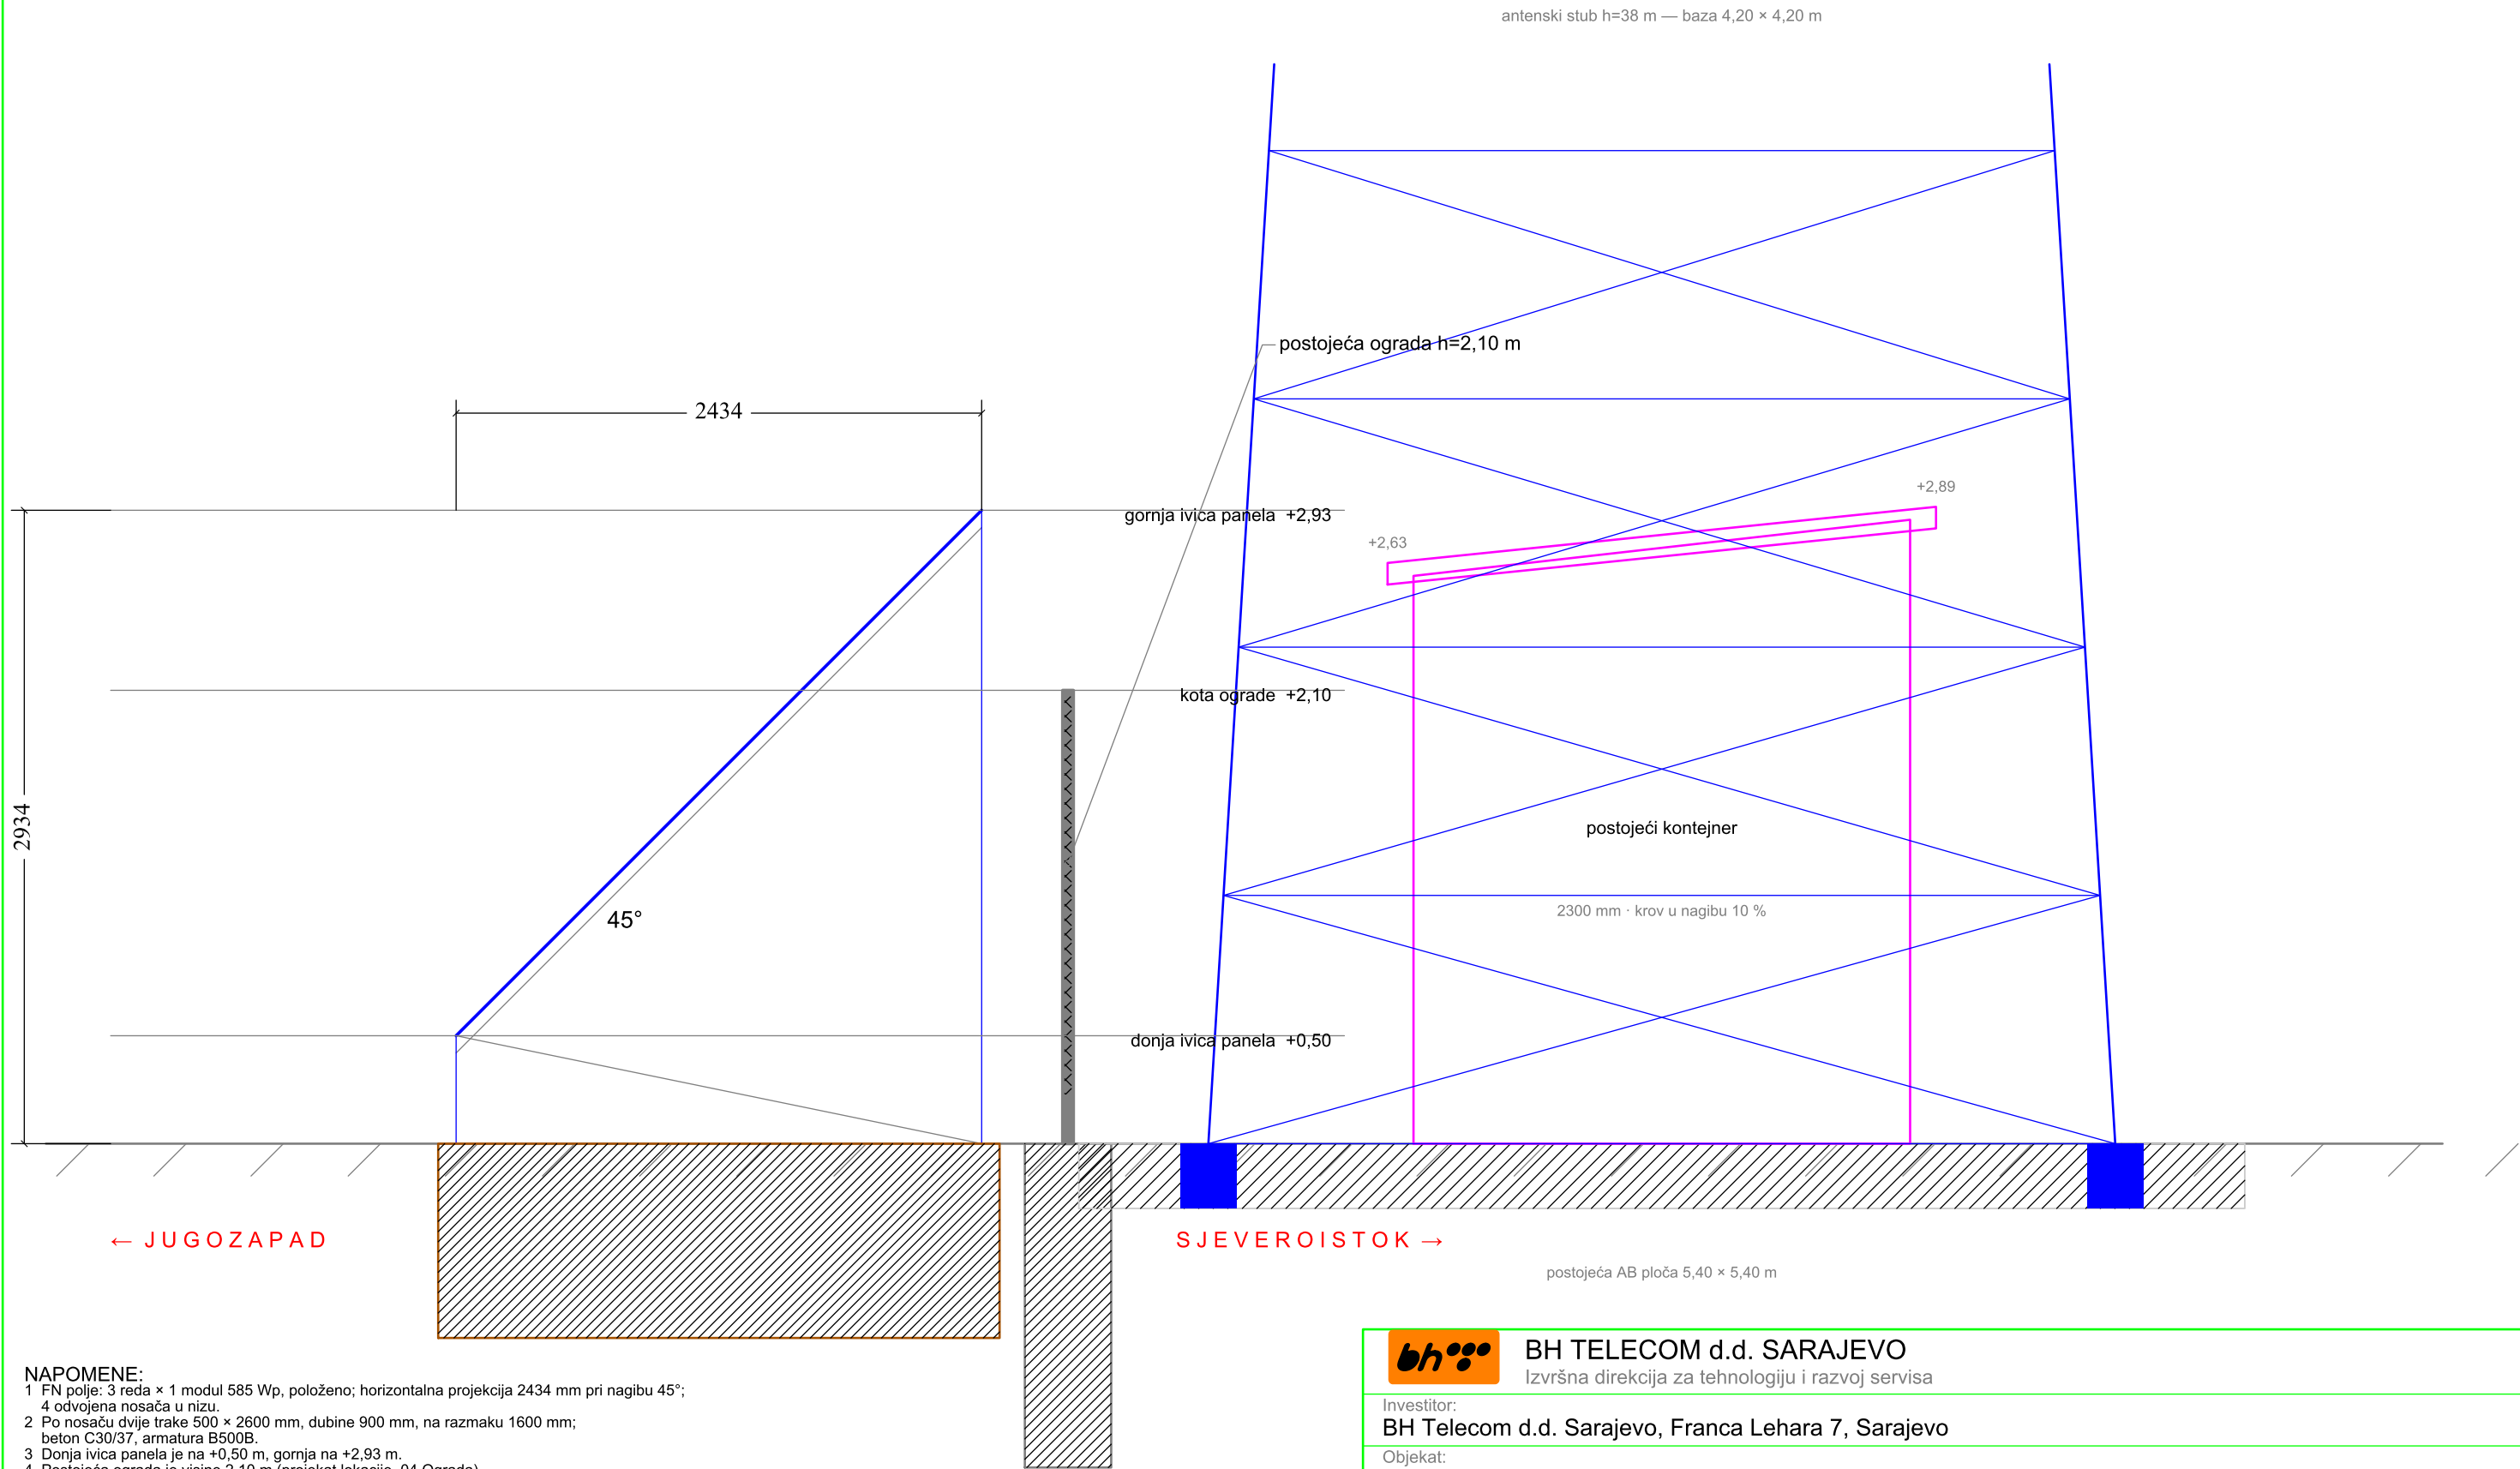

NAPOMENE:
1 FN polje: 3 reda x 1 modul 585 Wp, položeno; horizontalna projekcija 2434 mm pri nagibu 45°;
4 odvojena nosača u nizu.
2 Po nosaču dvije trake 500 x 2600 mm, dubine 900 mm, na razmaku 1600 mm;
beton C30/37, armatura B500B.
3 Donja ivica panela je na +0,50 m, gornja na +2,93 m.
4 Postojeća ograda je visine 2,10 m (projekat lokacije, 04 Ograda).

BH TELECOM d.d. SARAJEVO Izvršna direkcija za tehnologiju i razvoj servisa		
Investitor: BH Telecom d.d. Sarajevo, Franca Lehara 7, Sarajevo		
Objekat: BS SJEDNICA (Bileća) — autonomni hibridni sistem napajanja		
Faza: Tenderska dokumentacija — Prilog III		šifra projekta: BHT-SJEDNICA-2026
Naziv crteža: Presjek A–A kroz nosač FN panela		razmjera: 1:30
Projektant: Rusmir Skopljak, dipl. ing. el.	ovjerio: Rusmir Skopljak, dipl. ing. el.	godina / broj crteža: 2026. S-03