


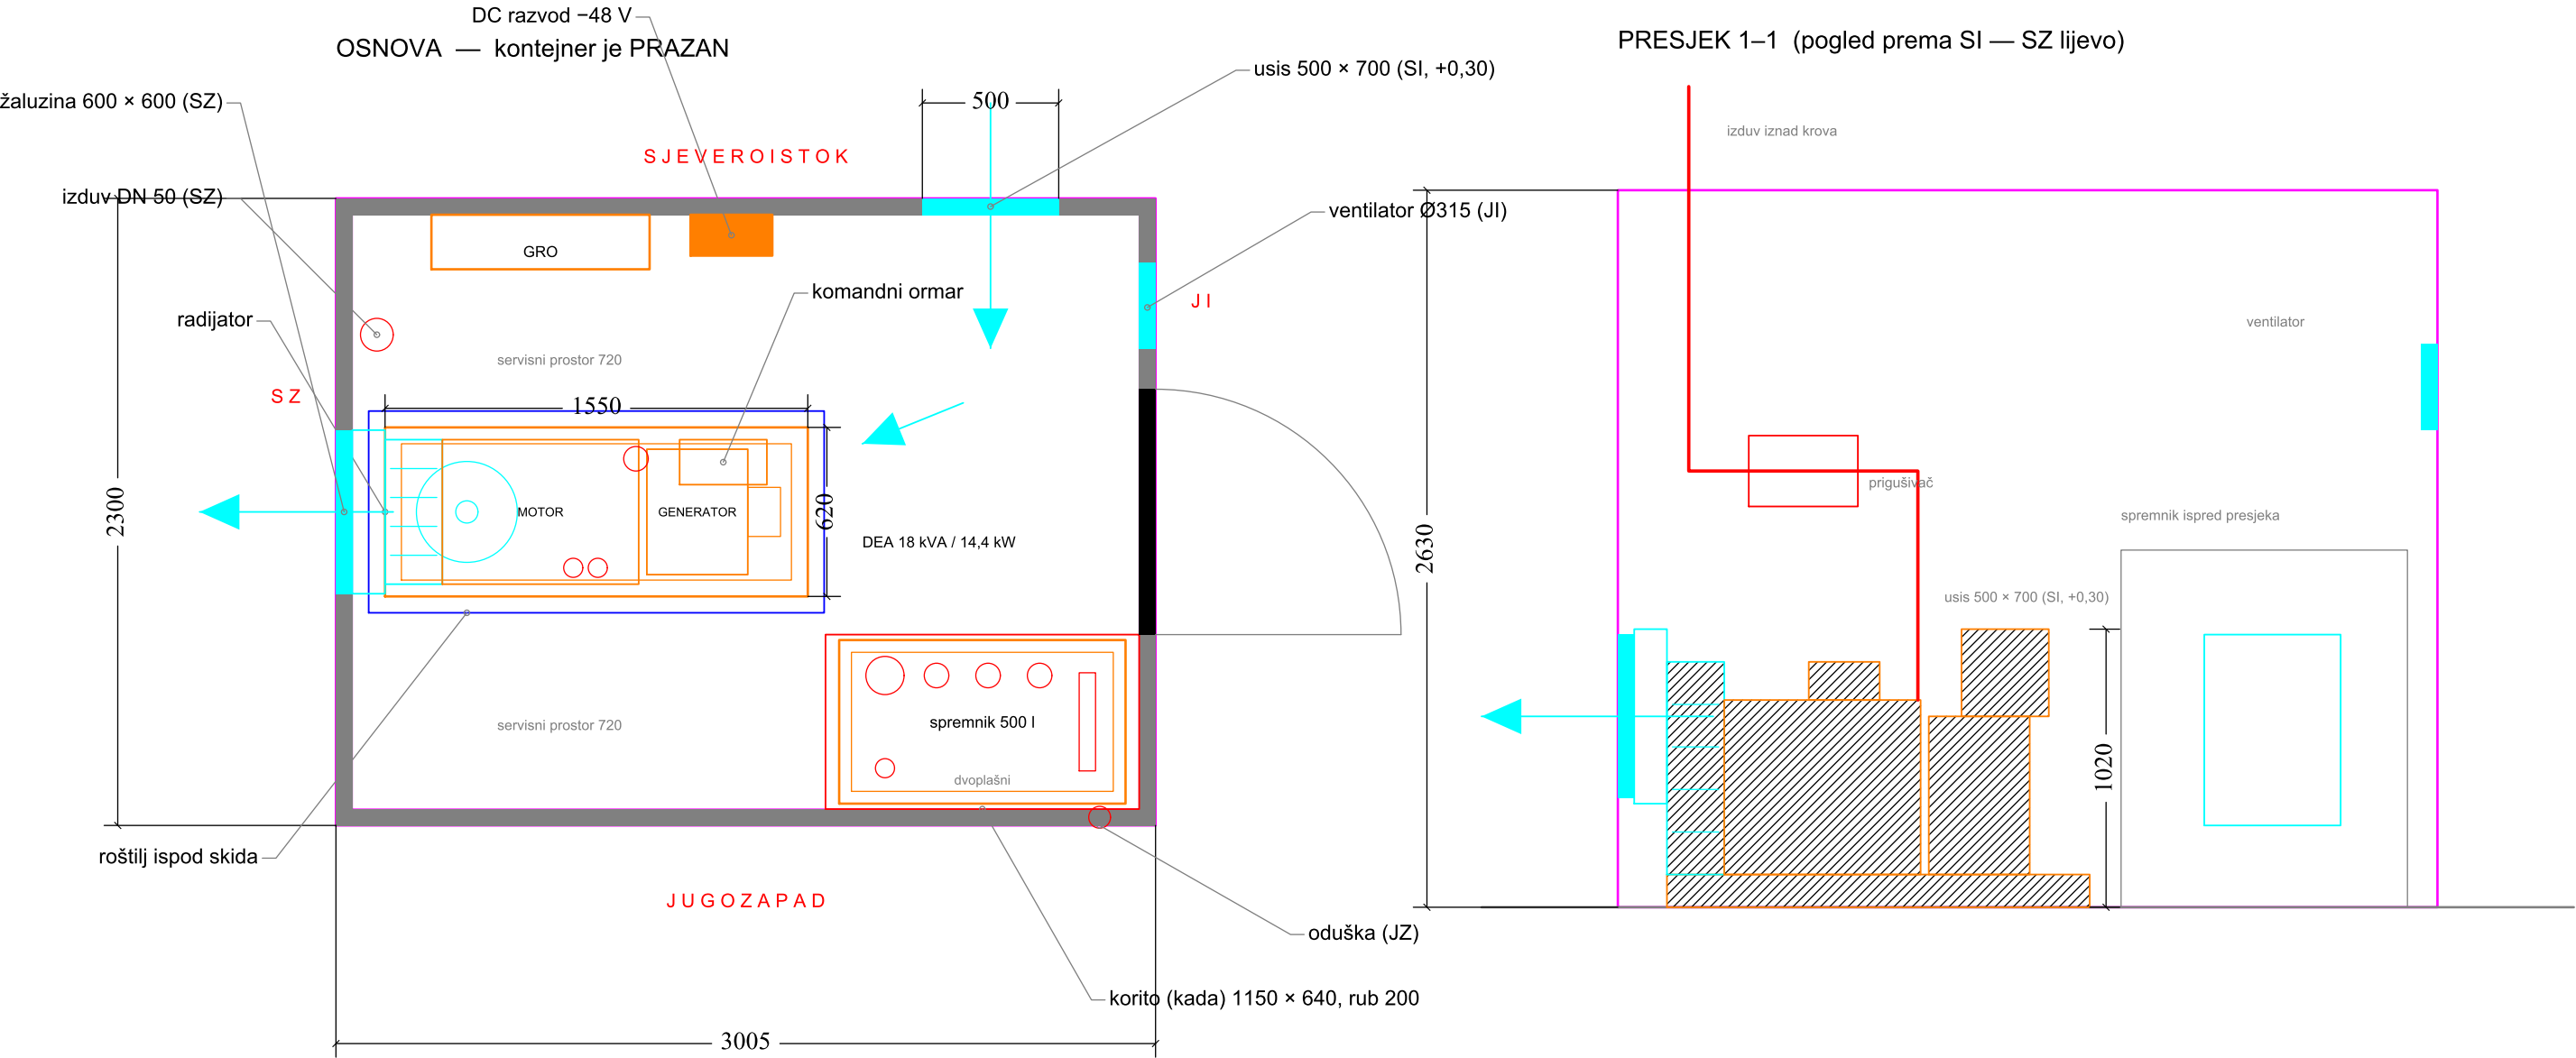

- NAPOMENE:**
- 1 DEA FG Wilson P18-6 (skid) ili ekv., 18 kVA / 14,4 kW.
 - 2 Usis 500 × 700 SI (+0,30); kanal i žaluzina 600 × 600 te izduv DN 50 SZ; oduška JZ; ventilator Ø315 JI.
 - 3 Roštilj OBAVEZAN ispod skida i ispod korita.
 - 4 Spremnik DVOPLAŠNI; ispod njega korito 1150 × 640, rub 200 mm.
 - 5 Servisni prolazi 720 mm JZ / 720 mm SI / 1155 mm JI — ne zauzimati.
 - 6 Unos skida 620 mm kroz vrata 900 mm. Kontejner je PRAZAN.
 - 7 DC razvod -48 V na SI zidu uz GRO; trajni potrošači D1-D6 — E-01.
 - 8 Raspored je principijelan; potvrđuje se na licu mjesta. Zahtjevi: Prilog I, Tačka 4.

bh BH TELECOM d.d. SARAJEVO Izvršna direkcija za tehnologiju i razvoj servisa		
Investitor: BH Telecom d.d. Sarajevo, Franca Lehara 7, Sarajevo		
Objekat: BS SJEDNICA (Bileća) — autonomni hibridni sistem napajanja		
Faza: Tenderska dokumentacija — Prilog III		šifra projekta: BHT-SJEDNICA-2026
Naziv crteža: DEA u postojećem kontejneru — osnova i presjek		razmjera: 1:25
Projektant: Rusmir Skopljak, dipl. ing. el.	ovjerio: Rusmir Skopljak, dipl. ing. el.	godina / broj crteža: 2026. M-01