


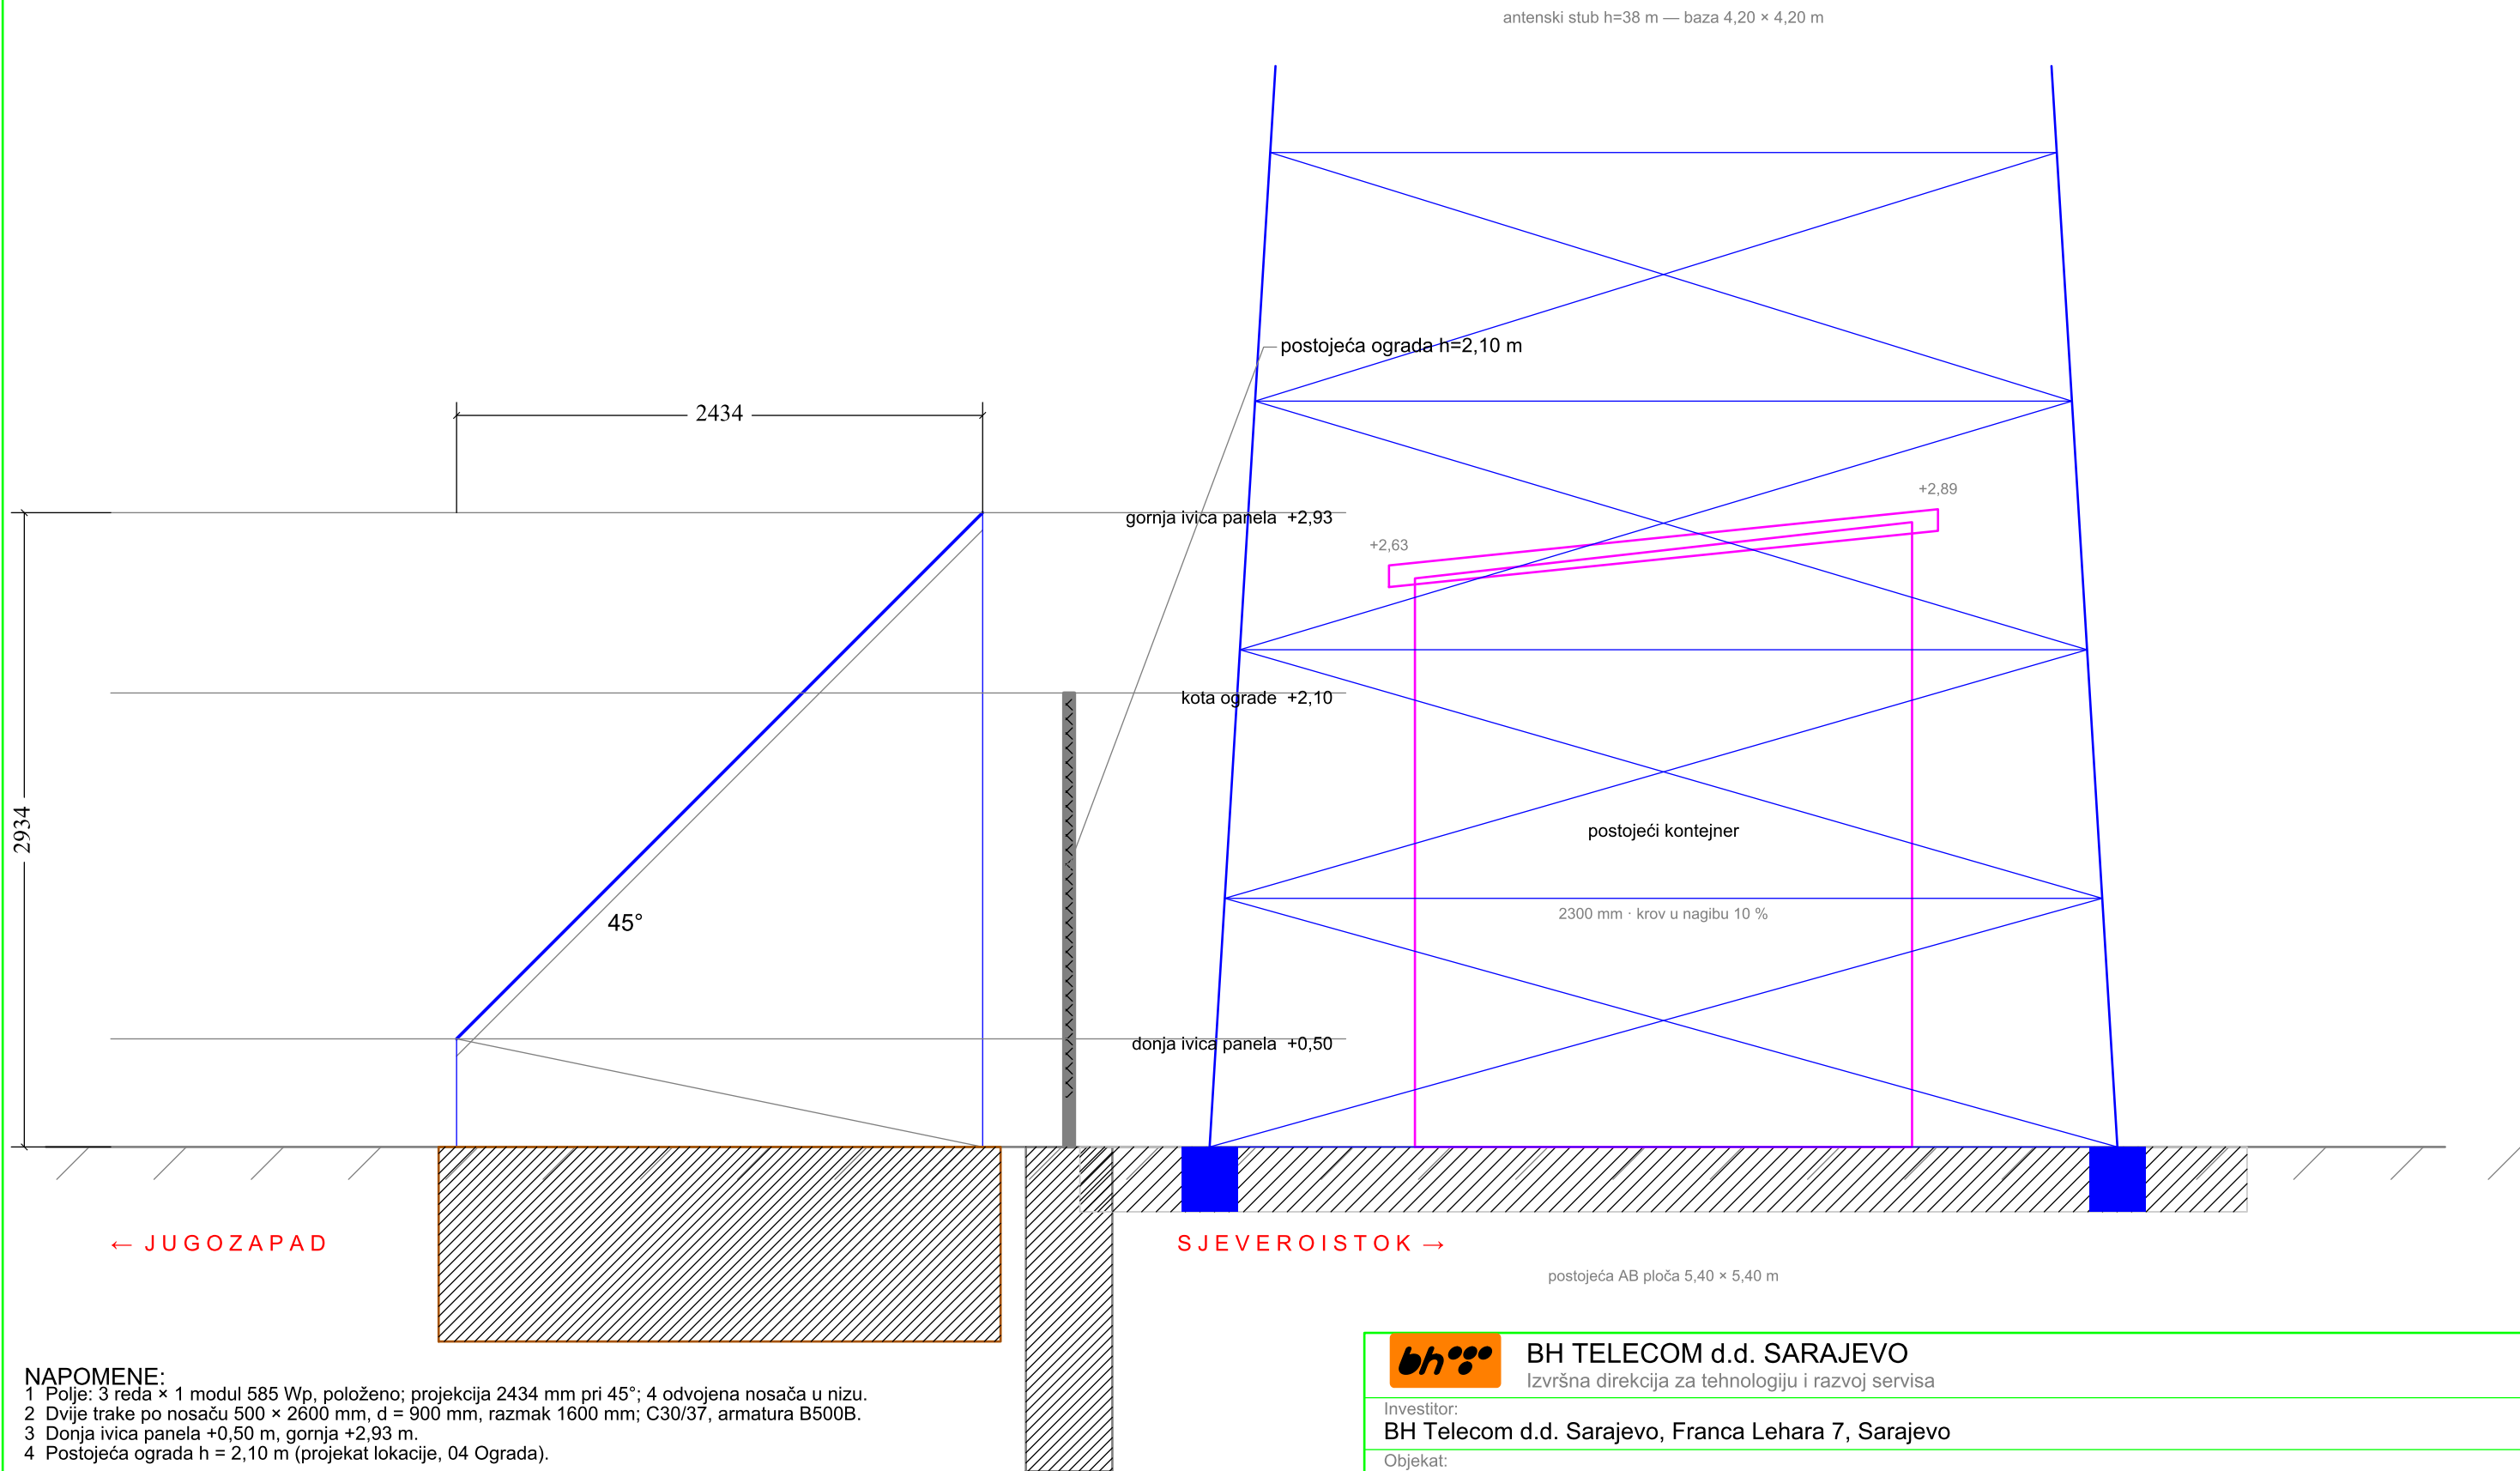

NAPOMENE:
1 Polje: 3 reda × 1 modul 585 Wp, položeno; projekcija 2434 mm pri 45°; 4 odvojena nosača u nizu.
2 Dvije trake po nosaču 500 × 2600 mm, d = 900 mm, razmak 1600 mm; C30/37, armatura B500B.
3 Donja ivica panela +0,50 m, gornja +2,93 m.
4 Postojeća ograda h = 2,10 m (projekat lokacije, 04 Ograda).



BH TELECOM d.d. SARAJEVO
Izvršna direkcija za tehnologiju i razvoj servisa

Investitor:
BH Telecom d.d. Sarajevo, Franca Lehara 7, Sarajevo

Objekat:
BS SJEDNICA (Bileća) — autonomni hibridni sistem napajanja

Faza:
Tenderska dokumentacija — Prilog III

Naziv crteža:
Presjek A–A kroz nosač FN panela

Projektant:
Rusmir Skopljak, dipl. ing. el.

ovjerio:
Rusmir Skopljak, dipl. ing. el.

šifra projekta:
BHT-SJEDNICA-2026

razmjera:
1:30

godina / broj crteža:
2026. S-03