


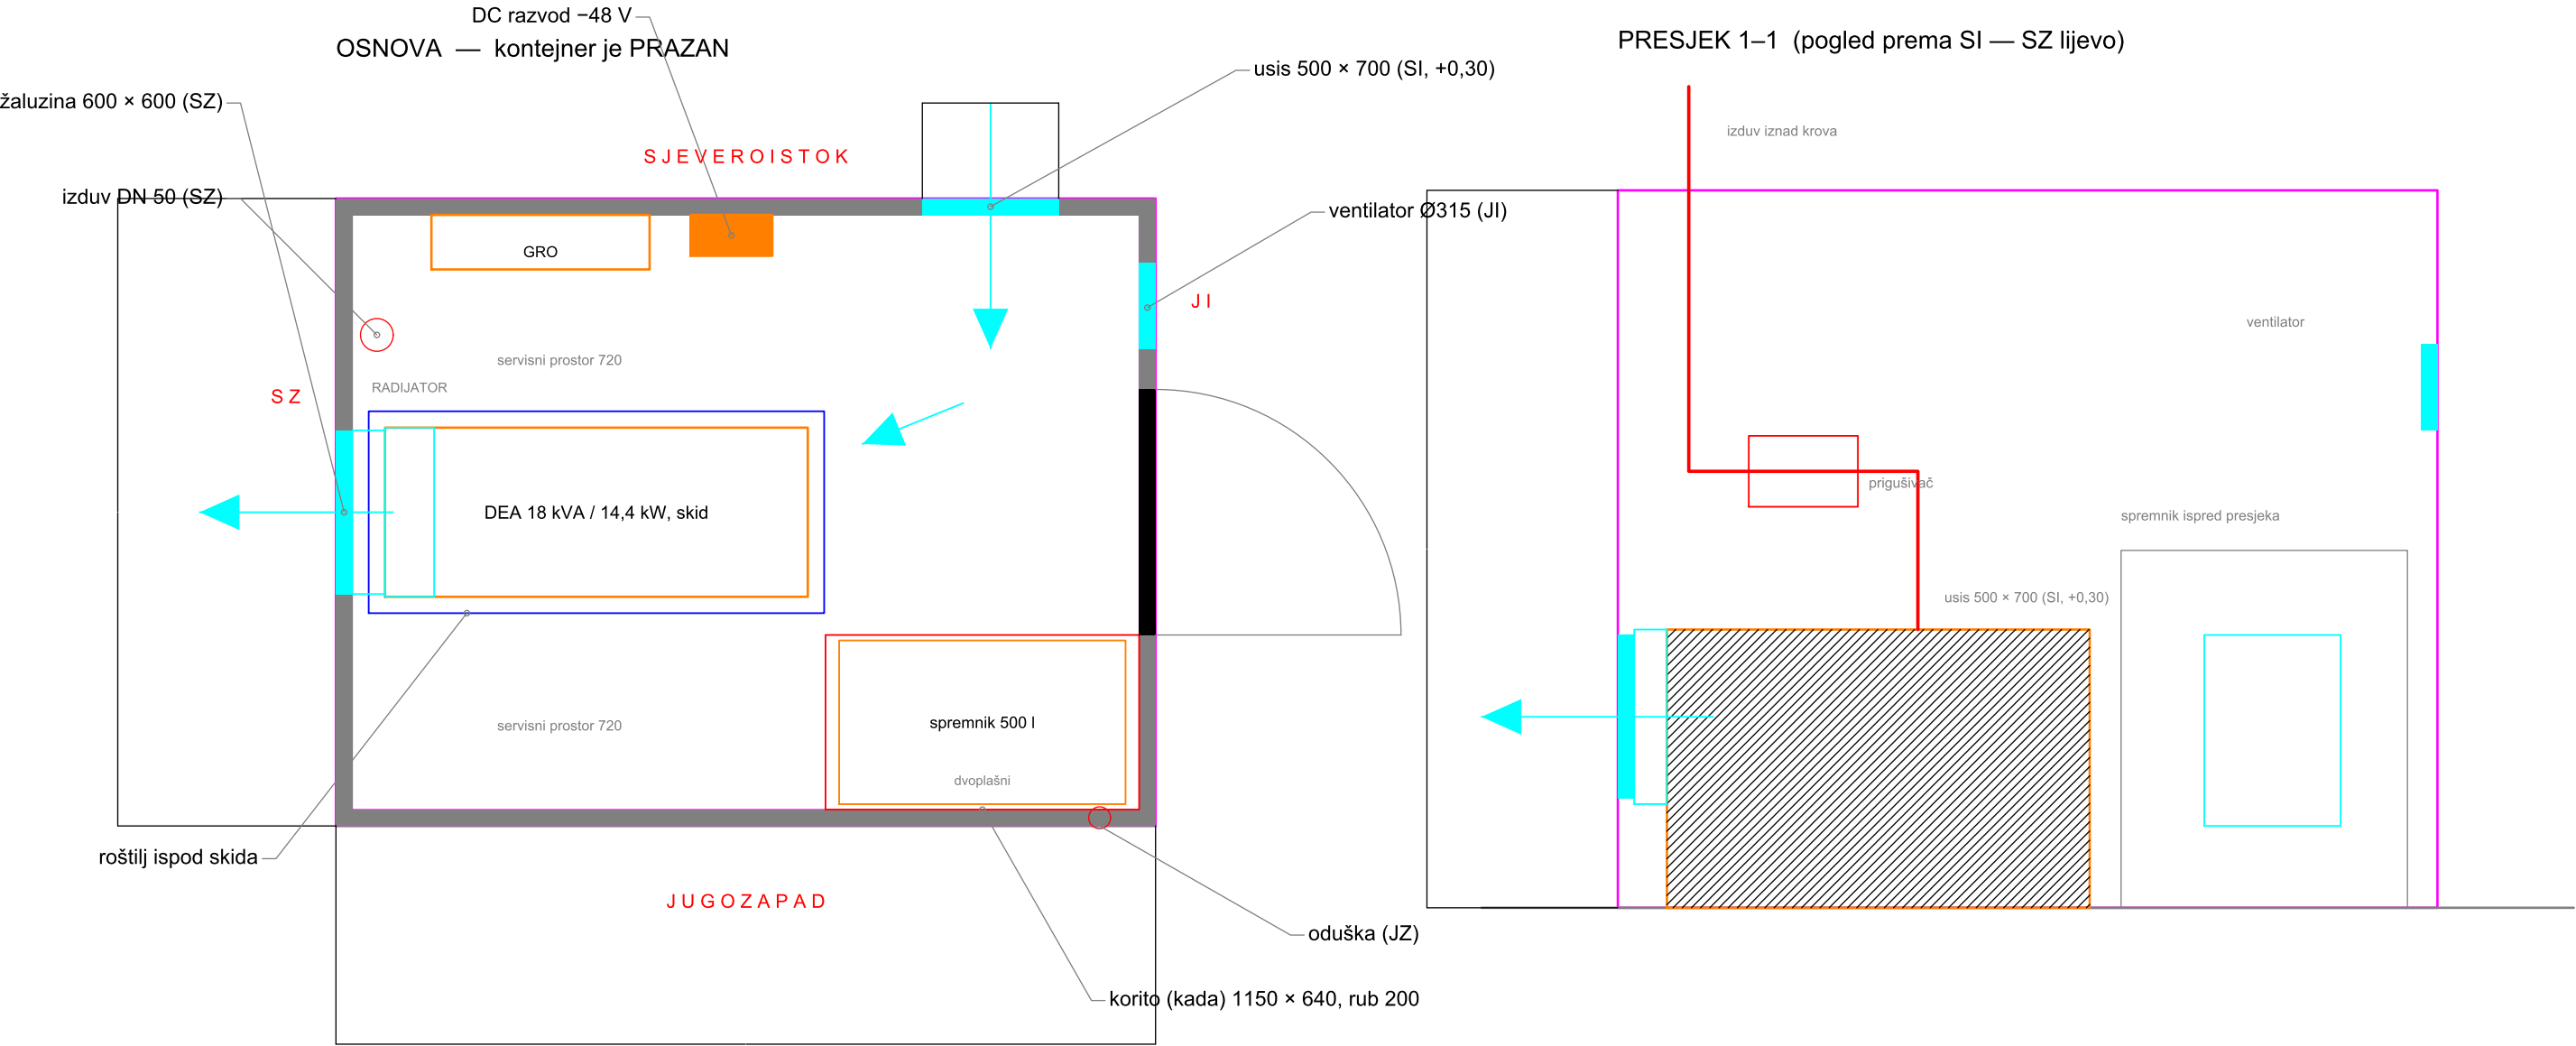

- NAPOMENE:
- DEA FG Wilson P18-6 (skid) ili ekv., 18 kVA / 14,4 kW.
  - Usis 500 × 700 SI (+0,30); kanal i žaluzina 600 × 600 te izduv DN 50 SZ; oduška JZ; ventilator Ø315 JI.
  - Roštilj OBAVEZAN ispod skida i ispod korita.
  - Spremnik DVOPLAŠNI; ispod njega korito 1150 × 640, rub 200 mm.
  - Servisni prolazi 720 mm JZ / 720 mm SI / 1155 mm JI — ne zauzimati.
  - Unos skida 620 mm kroz vrata 900 mm. Kontejner je PRAZAN.
  - DC razvod -48 V na SI zidu uz GRO; trajni potrošači D1-D6 — E-01.
  - Raspored je principijelan; potvrđuje se na licu mjesta. Zahtjevi: Prilog I, Tačka 4.

|   |                                             |                                      |
|---|---------------------------------------------|--------------------------------------|
| <div><div>bh</div><div>BH TELECOM d.d. SARAJEVO</div><div>Izvršna direkcija za tehnologiju i razvoj servisa</div></div> |                                             |                                      |
| Investitor:<br>BH Telecom d.d. Sarajevo, Franca Lehara 7, Sarajevo                                                      |                                             |                                      |
| Objekat:<br>BS SJEDNICA (Bileća) — autonomni hibridni sistem napajanja                                                  |                                             |                                      |
| Faza:<br>Tenderska dokumentacija — Prilog III                                                                           |                                             | šifra projekta:<br>BHT-SJEDNICA-2026 |
| Naziv crteža:<br>DEA u postojećem kontejneru — osnova i presjek                                                         |                                             | razmjera:<br>1:25                    |
| Projektant:<br>Rusmir Skopljak, dipl. ing. el.                                                                          | ovjerio:<br>Rusmir Skopljak, dipl. ing. el. | godina / broj crteža:<br>2026. M-01  |