



OSNOVA — kontejner je PRAZAN; klima-uređaj Stulz se demontira

PRESJEK 1–1 (os agregata — pogled prema SI, SZ lijevo)

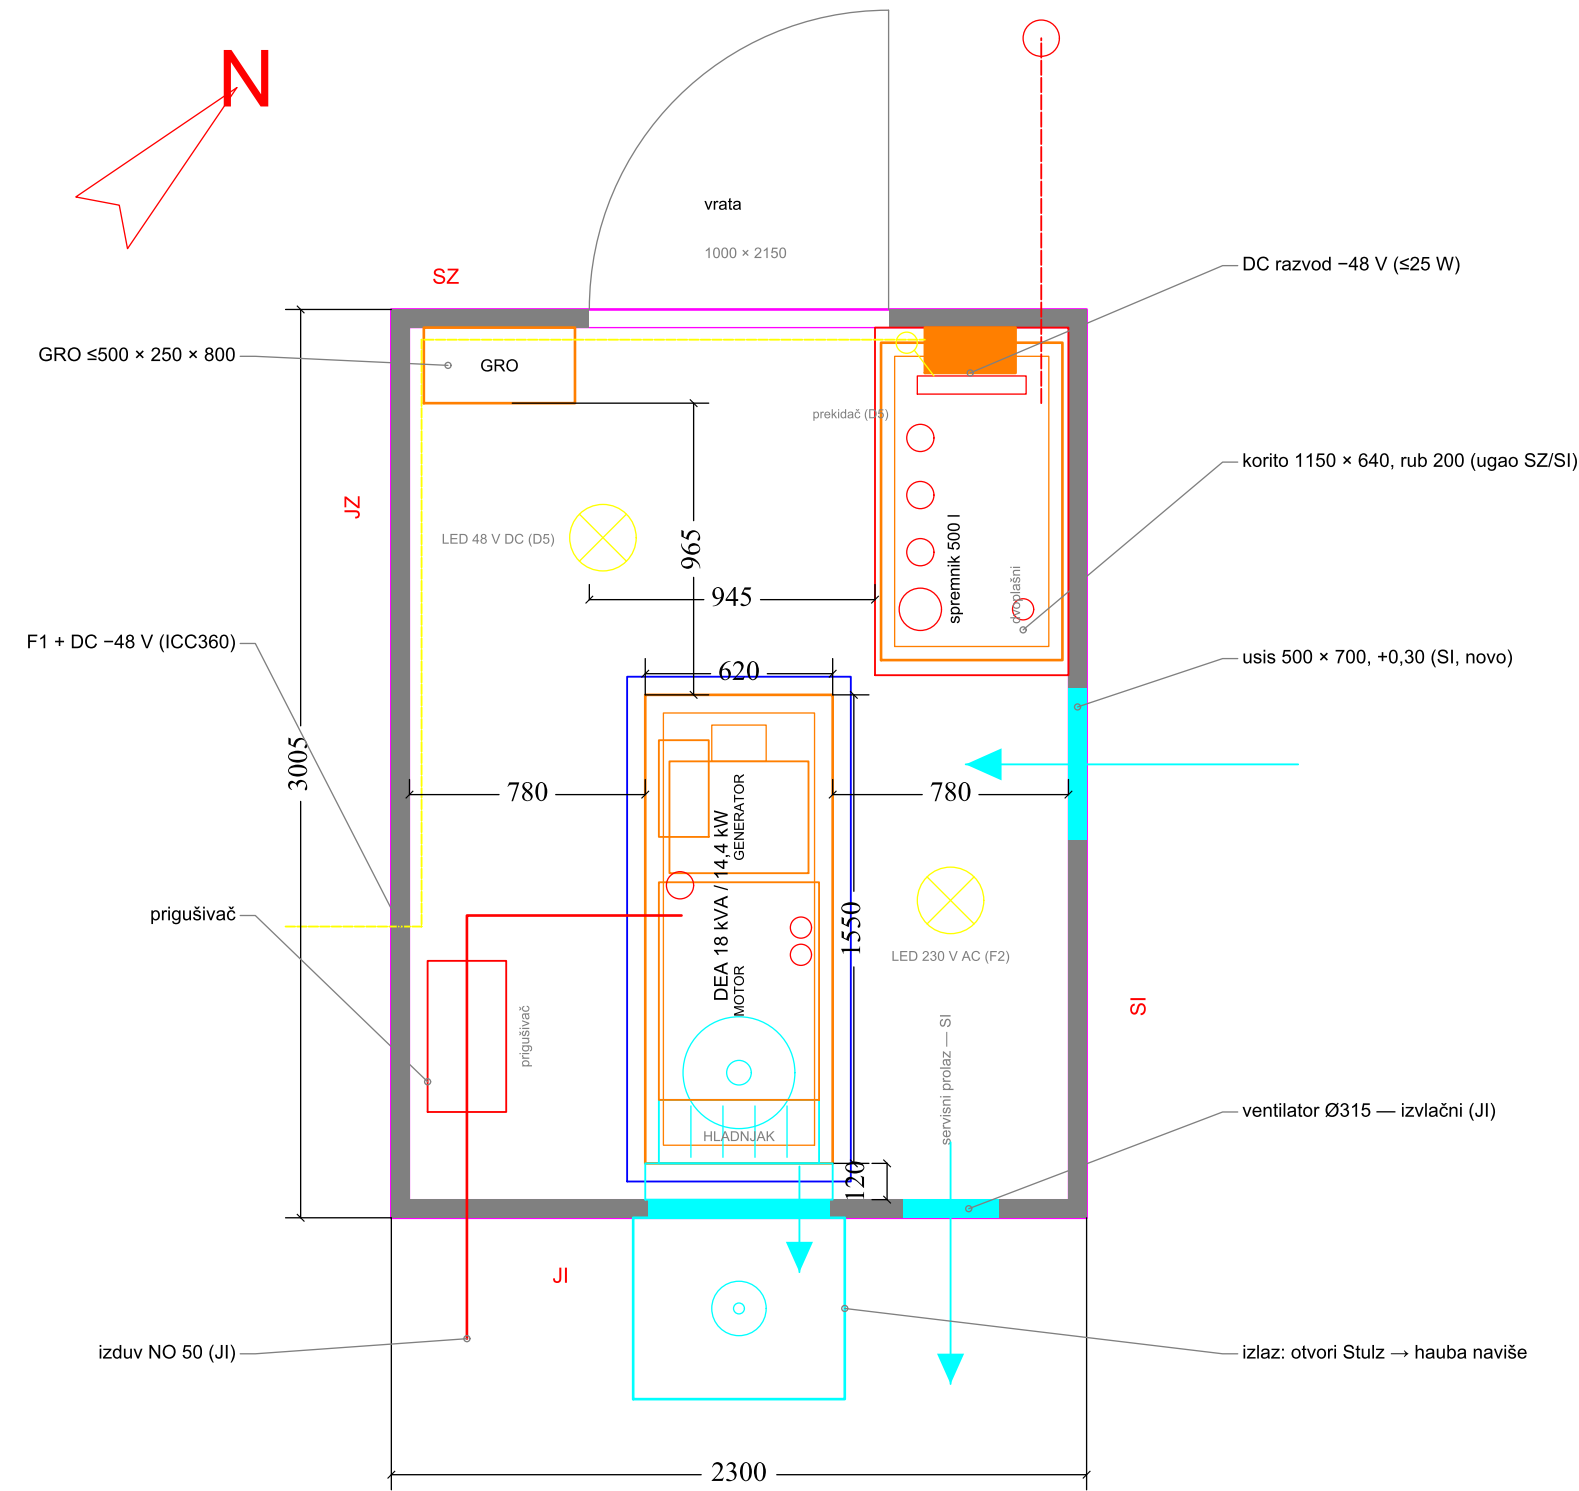

- NAPOMENE:**
- 1 DEA FG Wilson P18-6 (skid) ili ekv., 18 kVA / 14,4 kW; os SZ–JI, hladnjak JI.
 - 2 Izlaz zraka kroz postojeće otvore Stulz (sredina JI zida), ≥0,36 m² bruto, limeni plenum i hauba 700 × 600 — topli zrak NAVIŠE.
 - 3 Usis 500 × 700 na SI zidu (+0,30). Izdub NO 50 kroz JI zid na ≈+2,30 m, ispod platforme stuba.
 - 4 GRO ≤500 × 250 × 800 na SZ zidu; spremnik 500 l dvoplašni u koritu 1150 × 640; roštilj OBAVEZAN pod skidom i koritom.
 - 5 Servisni prolazi 780 / 780 mm i 965 mm do GRO; unos skida 620 mm kroz vrata 990 mm.
 - 6 Ventilator Ø315 (JI, izvlačni, D4) i DC razvod -48 V istočno od vrata — H-05.
 - 7 Raspored je principijelan; mjere otvora i servisne tačke potvrđuje Ponuđač na licu mjesta. Zahtjevi: Prilog I, Tačka 4.

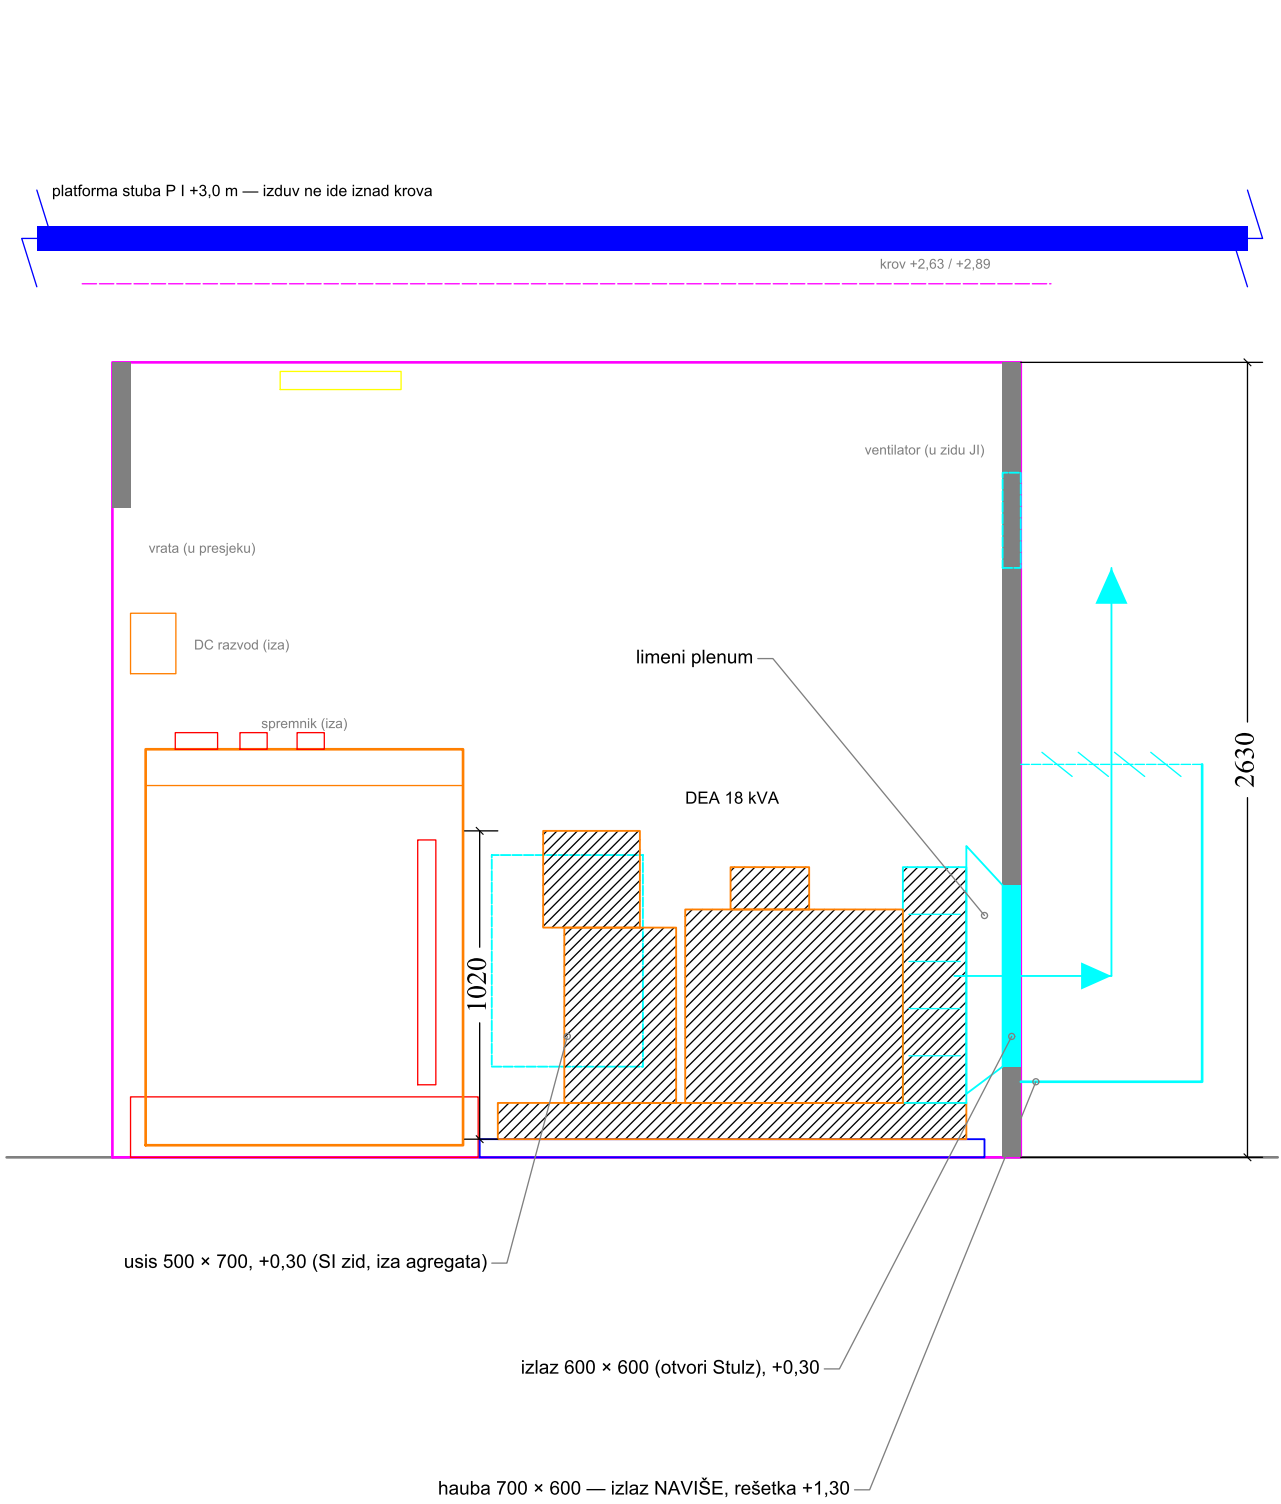

BH TELECOM d.d. SARAJEVO

Izvršna direkcija za tehnologiju i razvoj servisa

Investitor:

BH Telecom d.d. Sarajevo, Franca Lebara 7, Sarajevo

Objekat:

BS HAMZIĆI (ČITLUK) — autonomni hibridni sistem napajanja

Faza:

Tenderska dokumentacija — Prilog III

Naziv crteža:

Agregat u kontejneru — osnova i presjek 1–1

Projektant:

Rusmir Skopljak, dipl. ing. el.

ovjerio:

Rusmir Skopljak, dipl. ing. el.

šifra projekta:

BHT-HAMZICI-2026

razmjera:

1:25

godina / broj crteža:

2026. H-04