


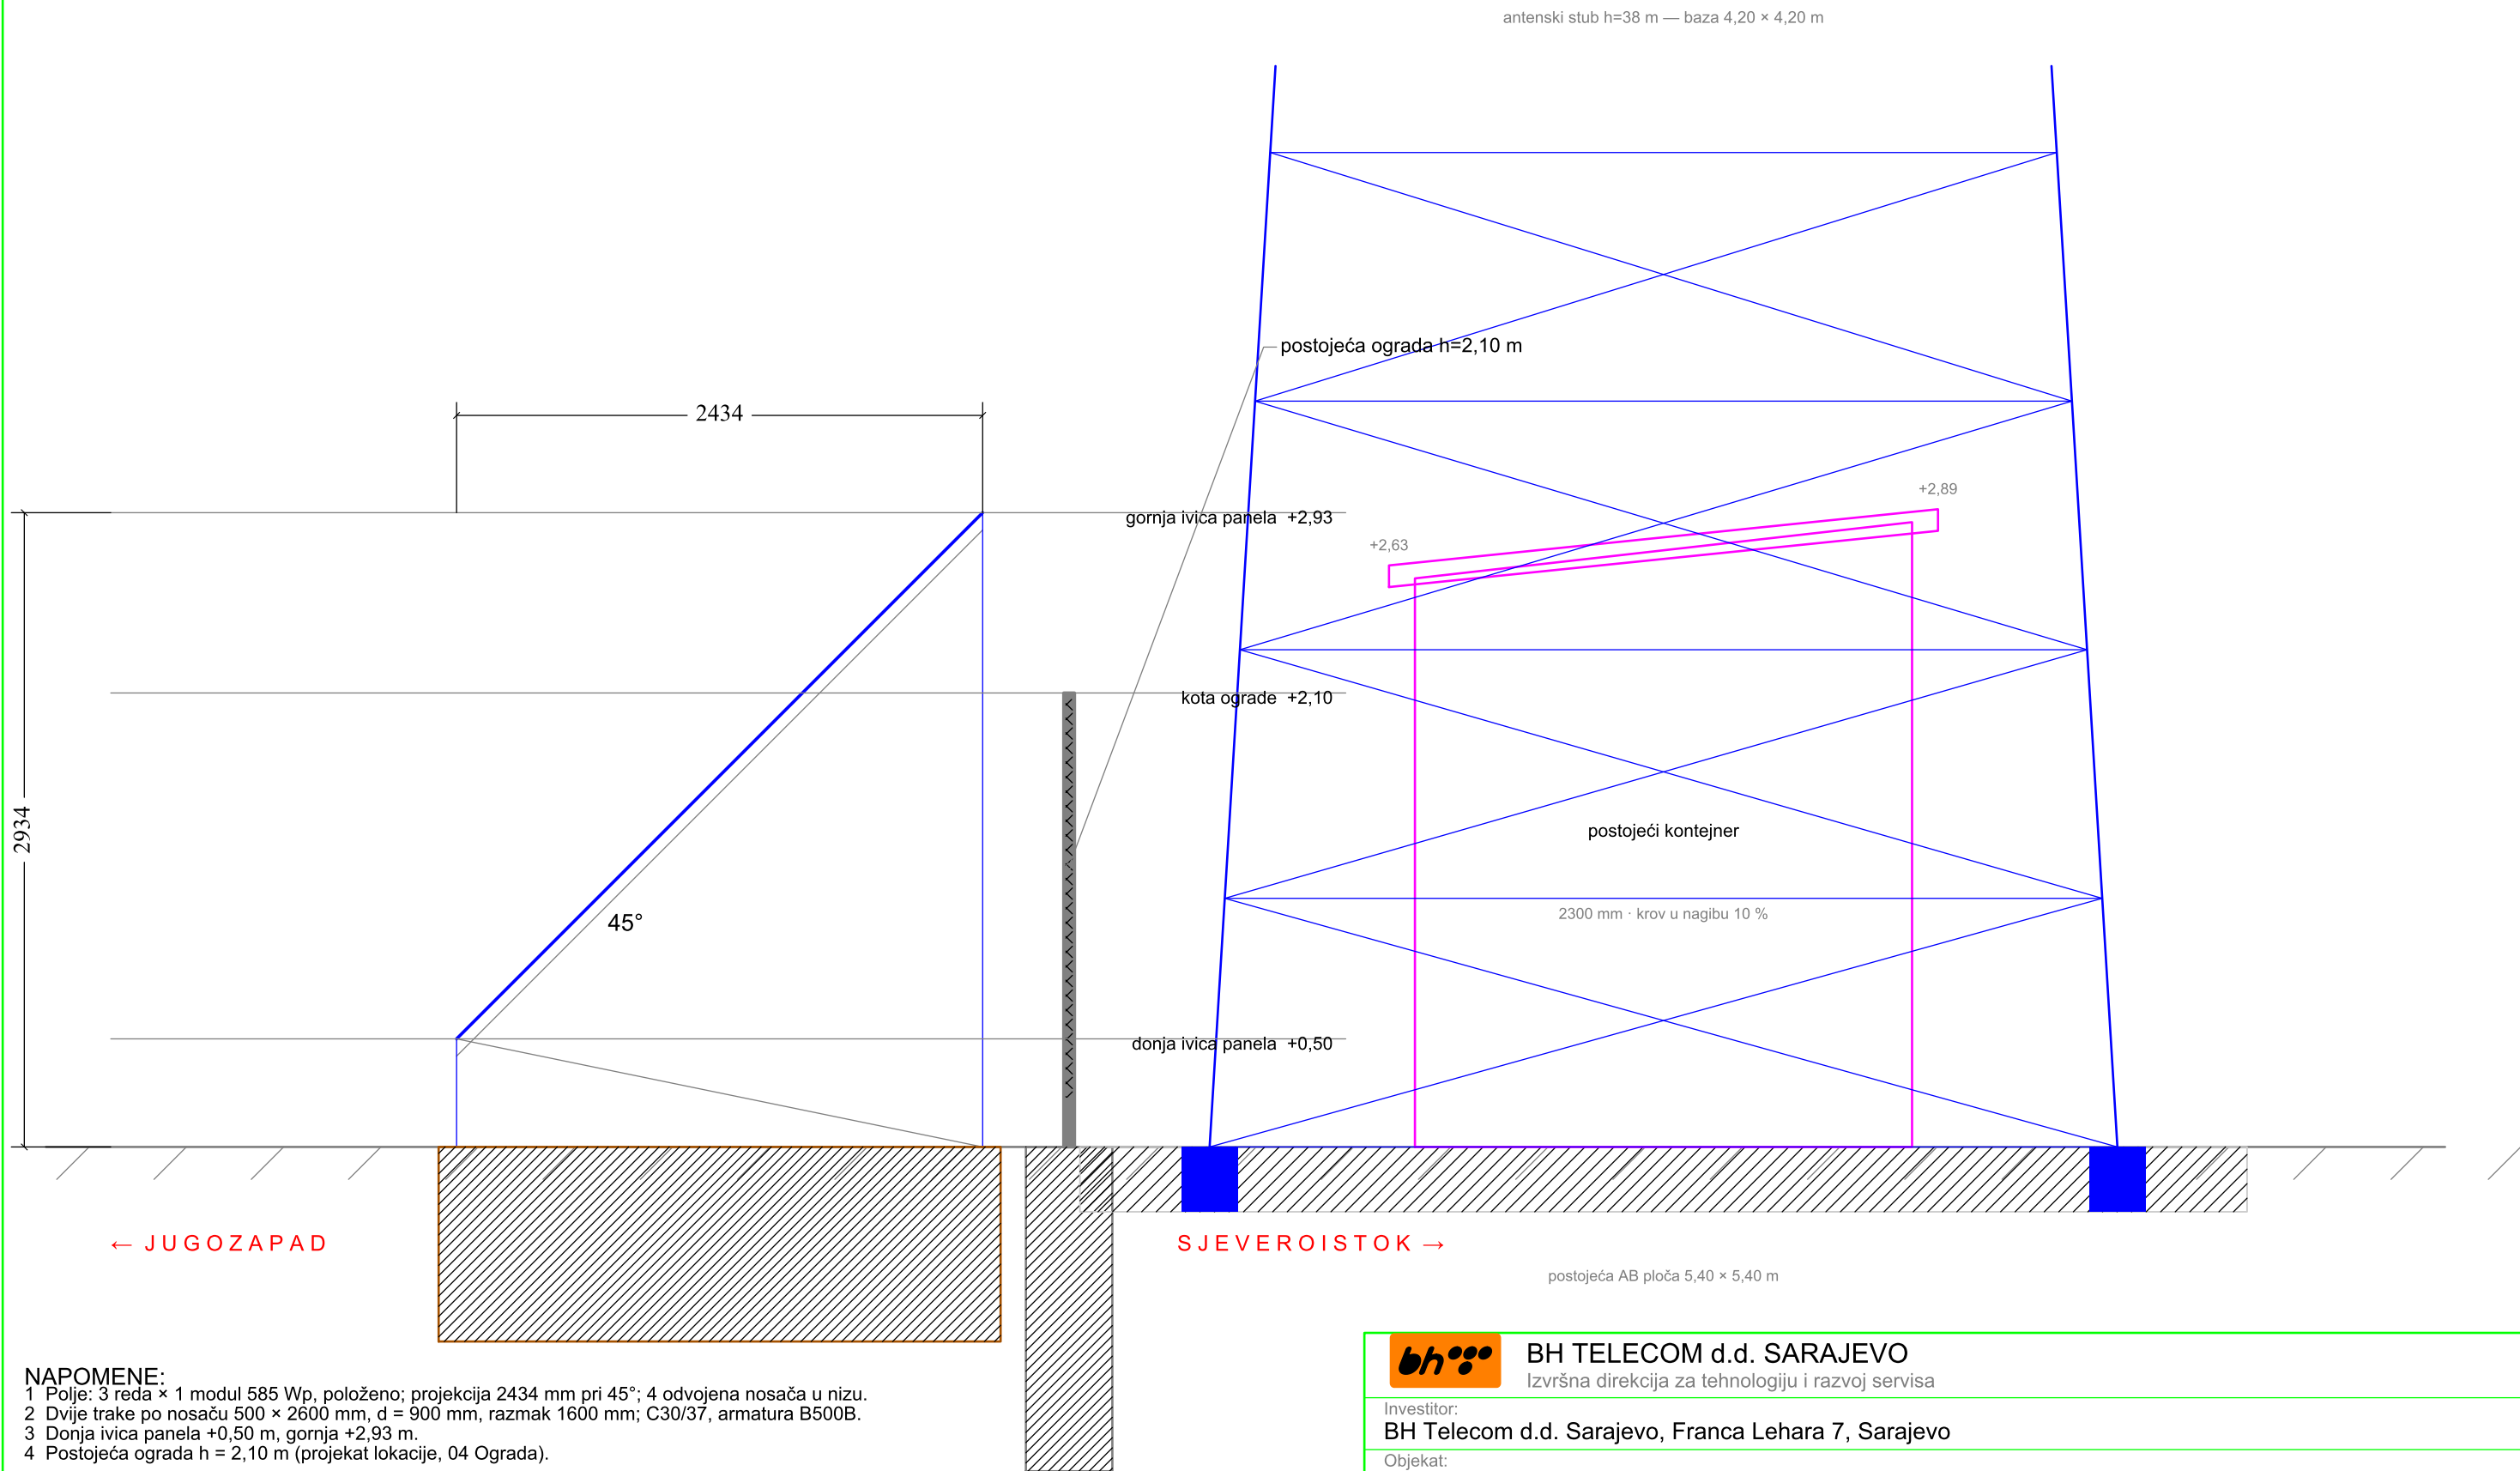

NAPOMENE:

1 Polje: 3 reda × 1 modul 585 Wp, položeno; projekcija 2434 mm pri 45°; 4 odvojena nosača u nizu.

2 Dvije trake po nosaču 500 × 2600 mm, d = 900 mm, razmak 1600 mm; C30/37, armatura B500B.

3 Donja ivica panela +0,50 m, gornja +2,93 m.

4 Postojeća ograda h = 2,10 m (projekat lokacije, 04 Ograda).

BH TELECOM d.d. SARAJEVO Izvršna direkcija za tehnologiju i razvoj servisa		
Investitor: BH Telecom d.d. Sarajevo, Franca Lehara 7, Sarajevo		
Objekat: BS SJEDNICA (Bileća) — autonomni hibridni sistem napajanja		
Faza: Tenderska dokumentacija — Prilog III		šifra projekta: BHT-SJEDNICA-2026
Naziv crteža: Presjek A–A kroz nosač FN panela		razmjera: 1:30
Projektant: Rusmir Skopljak, dipl. ing. el.	ovjerio: Rusmir Skopljak, dipl. ing. el.	godina / broj crteža: 2026. S-03