



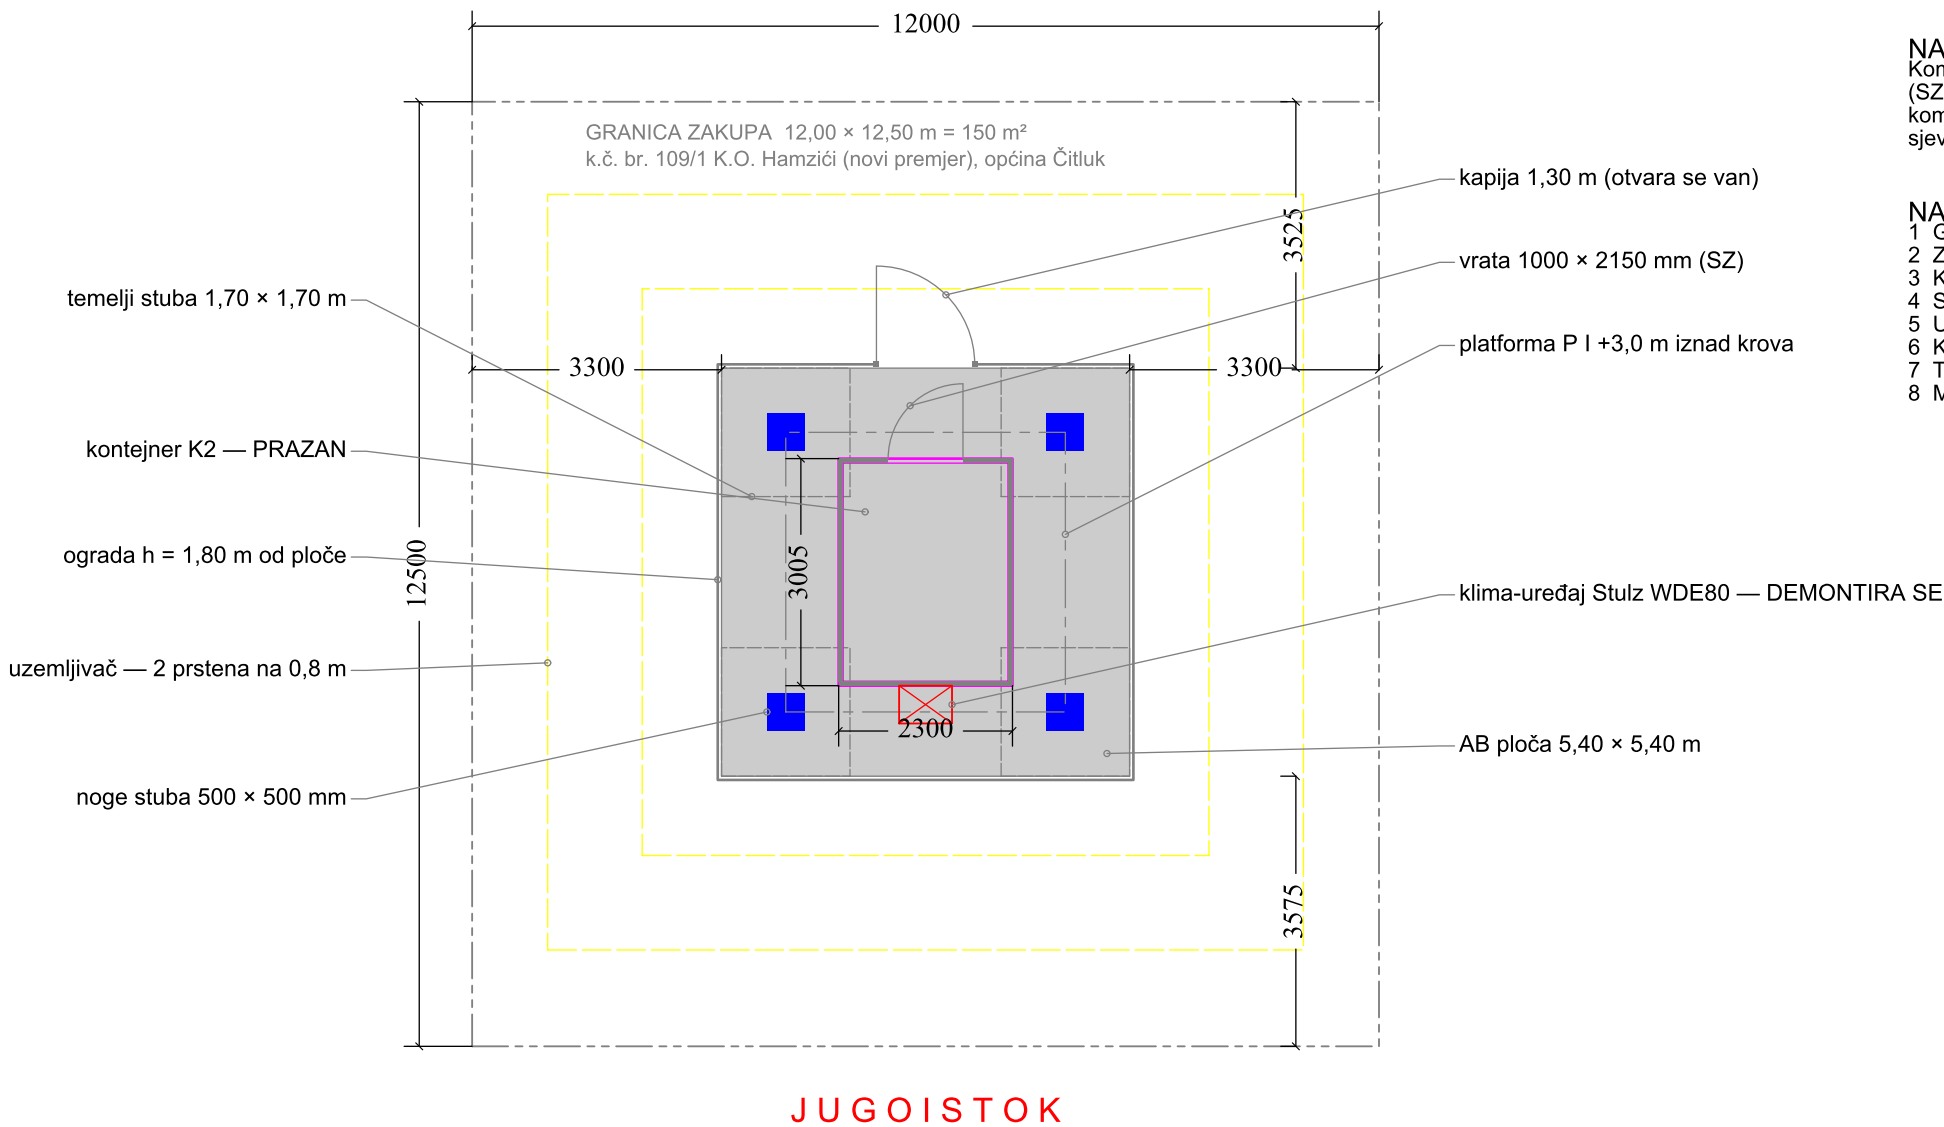

NAPOMENA — ORIJENTACIJA:
Kompleks je zakrenut 45°: vrata kontejnera i kapija gledaju na SJEVEROZAPAD (SZ), klima-uređaj Stulz na JI, FN polje na JZ. Crtež je pravougaon na kompleks (gore SZ, desno SI, dolje JI, lijevo JZ); strelica pokazuje pravi sjever. Orijentaciju potvrđuje Ponuđač obilaskom lokacije.

NAPOMENE:
1 Geometrija iz ovjerenog projekta lokacije GP-BS-10472-291 (2017).
2 Zakup 12,00 x 12,50 m = 150 m², k.č. br. 109/1, općina Čitluk.
3 Kontejner je PRAZAN; u sredini JI zida je Stulz WDE80 (≈700 x 500 x 2200).
4 Stub h = 32 m; platforma P I (+3,0 m) je iznad krova (+2,63 / +2,89 m).
5 Uzemljivač FeZn 25x4: prsten u temeljima stopa i dva prstena na 0,8 m.
6 Kapija se otvara prema van; krilo 1,30 m.
7 Teren uz ploču je na -0,20 m; ograda 1,80 m iznad ploče, 2,00 m iznad terena.
8 Mjere uređaja i otvora uzimaju se na obaveznom obilasku lokacije.

- LEGENDA**
- postojeća ograda 5,50 x 5,50 m, h = 1,80 m od ploče (2,00 m od terena) — kapija 1,30 m na SZ strani
 - postojeća AB ploča 5,40 x 5,40 m
 - postojeći kontejner K2 2300 x 3005 mm — vrata na SZ strani
 - noge rešetkastog stuba h = 32 m, baza 3,70 x 3,70 m
 - klima-uređaj Stulz WDE80 (JI zid, u sredini) — demontira se
 - postojeći uzemljivač FeZn 25x4 mm (isprekidano — u tlu)

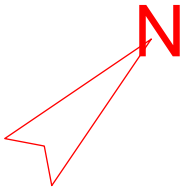

bh BH TELECOM d.d. SARAJEVO Izvršna direkcija za tehnologiju i razvoj servisa		
Investitor: BH Telecom d.d. Sarajevo, Franca Lehara 7, Sarajevo		
Objekat: BS HAMZIĆI (ČITLUK) — autonomni hibridni sistem napajanja		
Faza: Tenderska dokumentacija — Prilog III		šifra projekta: BHT-HAMZICI-2026
Naziv crteža: Situacija — POSTOJEĆE STANJE		razmjera: 1:100
Projektant: Rusmir Skopljak, dipl. ing. el.	ovjerio: Rusmir Skopljak, dipl. ing. el.	godina / broj crteža: 2026. H-01