


POGLED SA JUGOZAPADA (pravac gledanja azimut 45°)

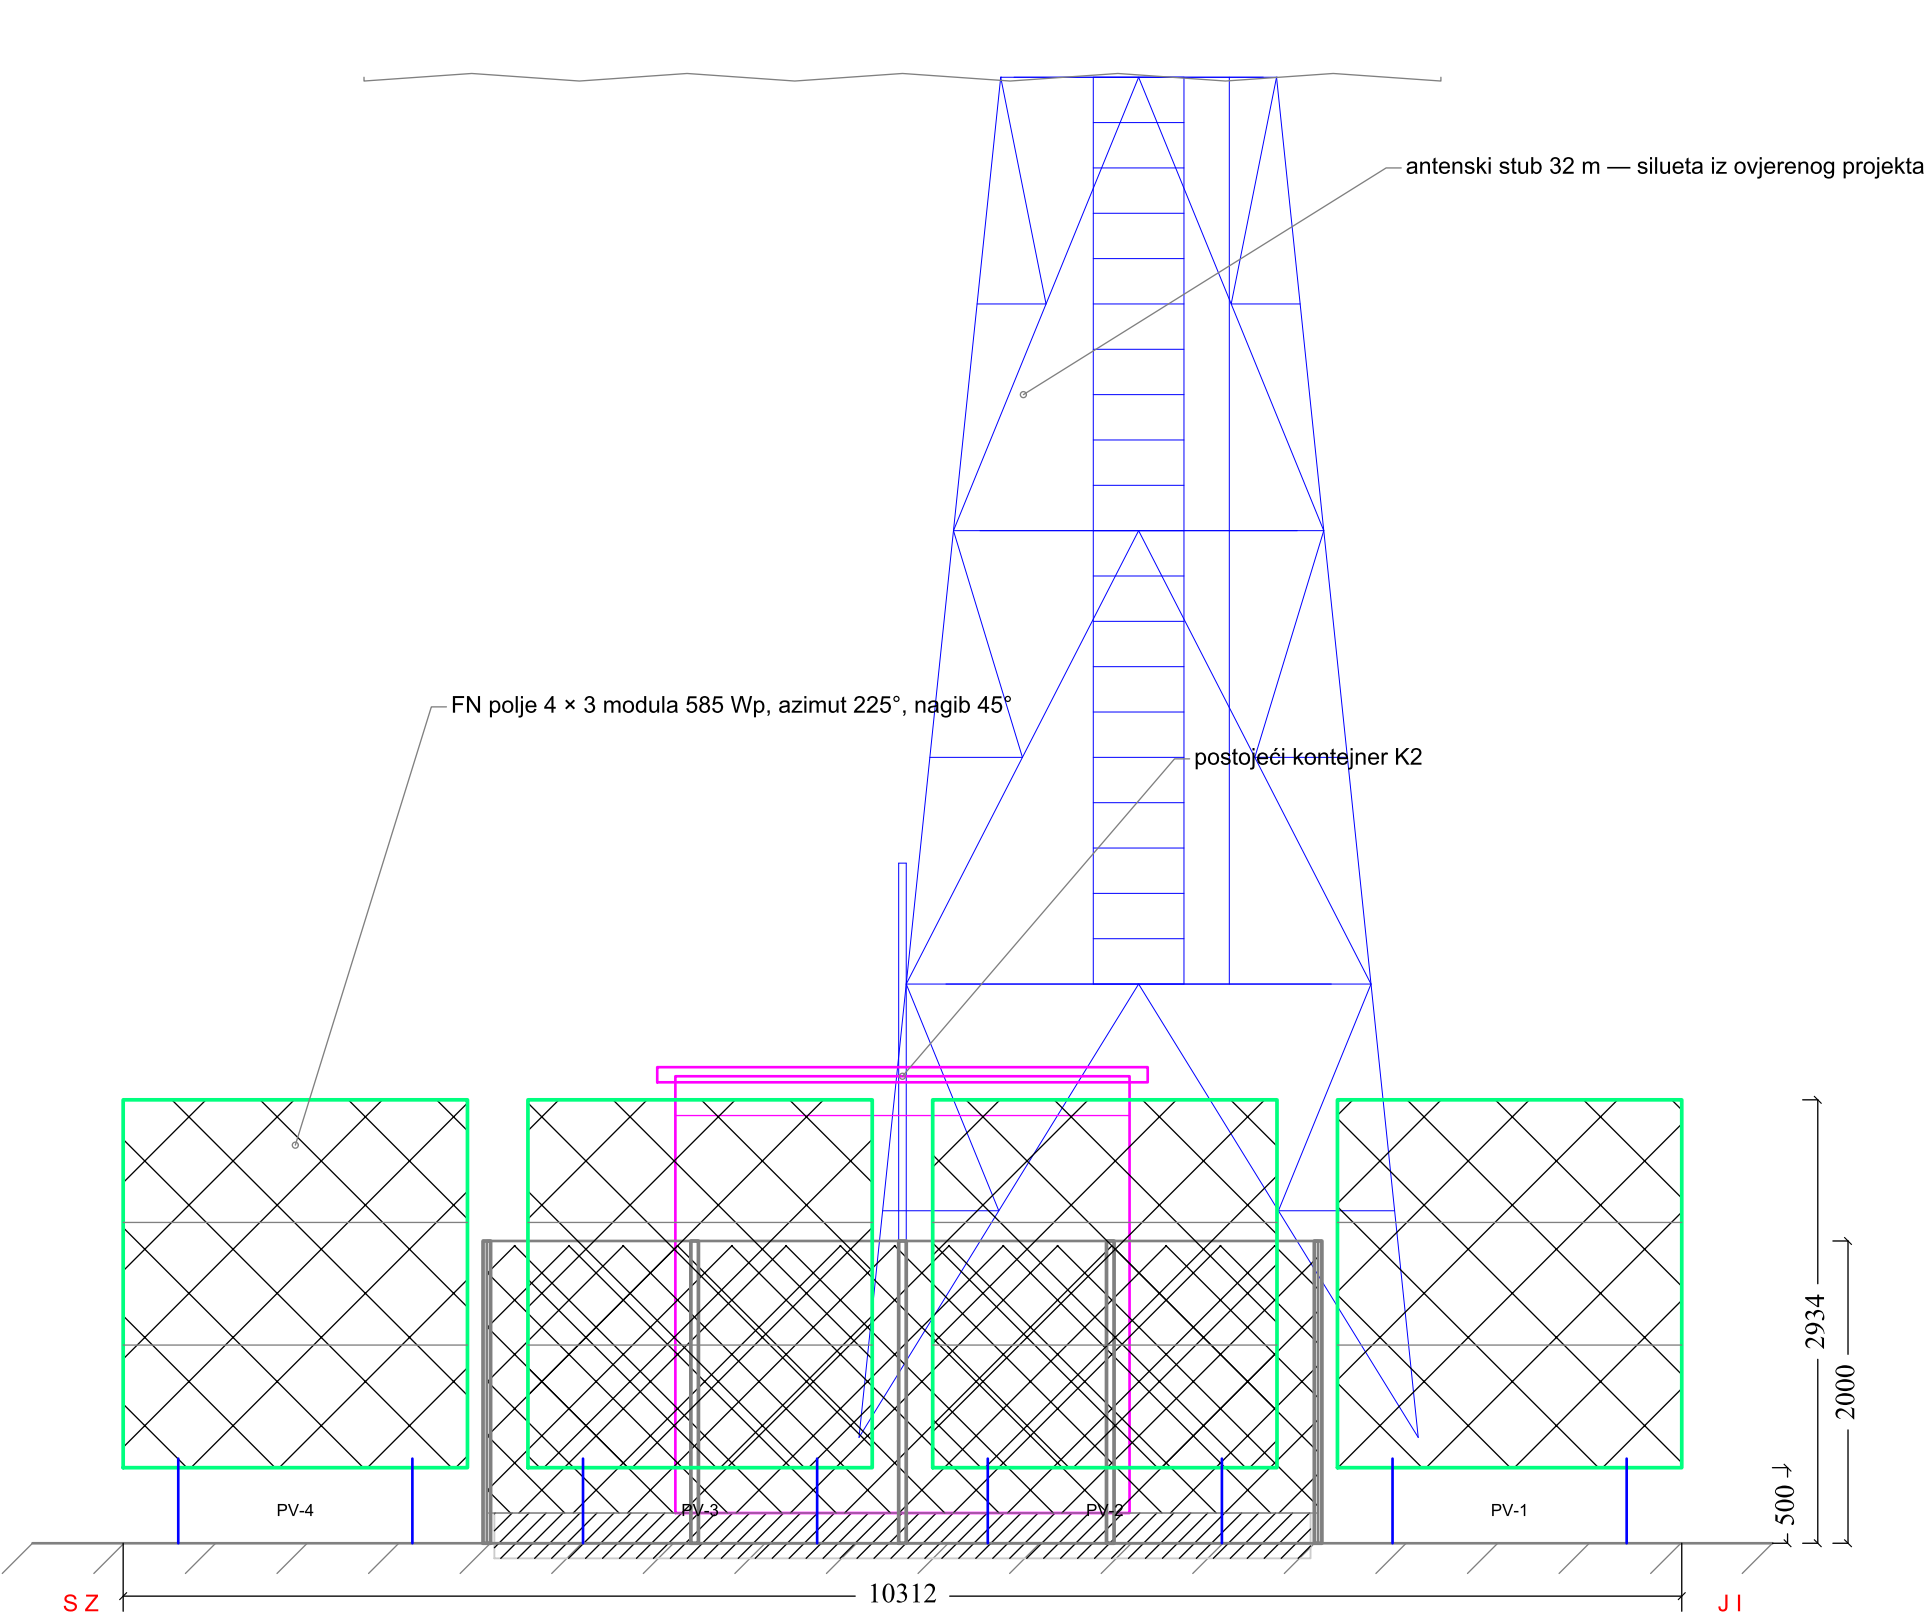

LEGENDA

- LOT 1 — FN moduli i nosači (ispred ograde, JZ)
- postojeći antenski stub — silueta iz ovjerenog projekta
- postojeći kontejner K2 na postojećoj ploči
- postojeća ograda 1,80 m iznad ploče

NAPOMENE:

- Prava ortogonalna elevacija u pravcu azimuta 45°; visine i širine su mjerljive.
- Paneli gledaju u posmatrača pod 45°, pa se po visini vide skraćeno: +0,50 do +2,93 m od terena.
- Teren uz FN polje je -0,20 m ispod ploče; ograda je 2,00 m iznad terena.
- Stub je prikazan do +9,50 m i prekinut; h = 32 m prema ovjerenom projektu (list 462 — 01_Dispozicija S32 m).
- Zahtjevi: Prilog I, Tačke 3 i 4.

bh BH TELECOM d.d. SARAJEVO Izvršna direkcija za tehnologiju i razvoj servisa		
Investitor: BH Telecom d.d. Sarajevo, Franca Lehara 7, Sarajevo		
Objekat: BS HAMZIĆI (ČITLUK) — autonomni hibridni sistem napajanja		
Faza: Tenderska dokumentacija — Prilog III		šifra projekta: BHT-HAMZICI-2026
Naziv crteža: Pogled sa JUGOZAPADA — kompleks sa FN poljem		razmjera: 1:50
Projektant: Rusmir Skopljak, dipl. ing. el.	ovjerio: Rusmir Skopljak, dipl. ing. el.	godina / broj crteža: 2026. H-06