


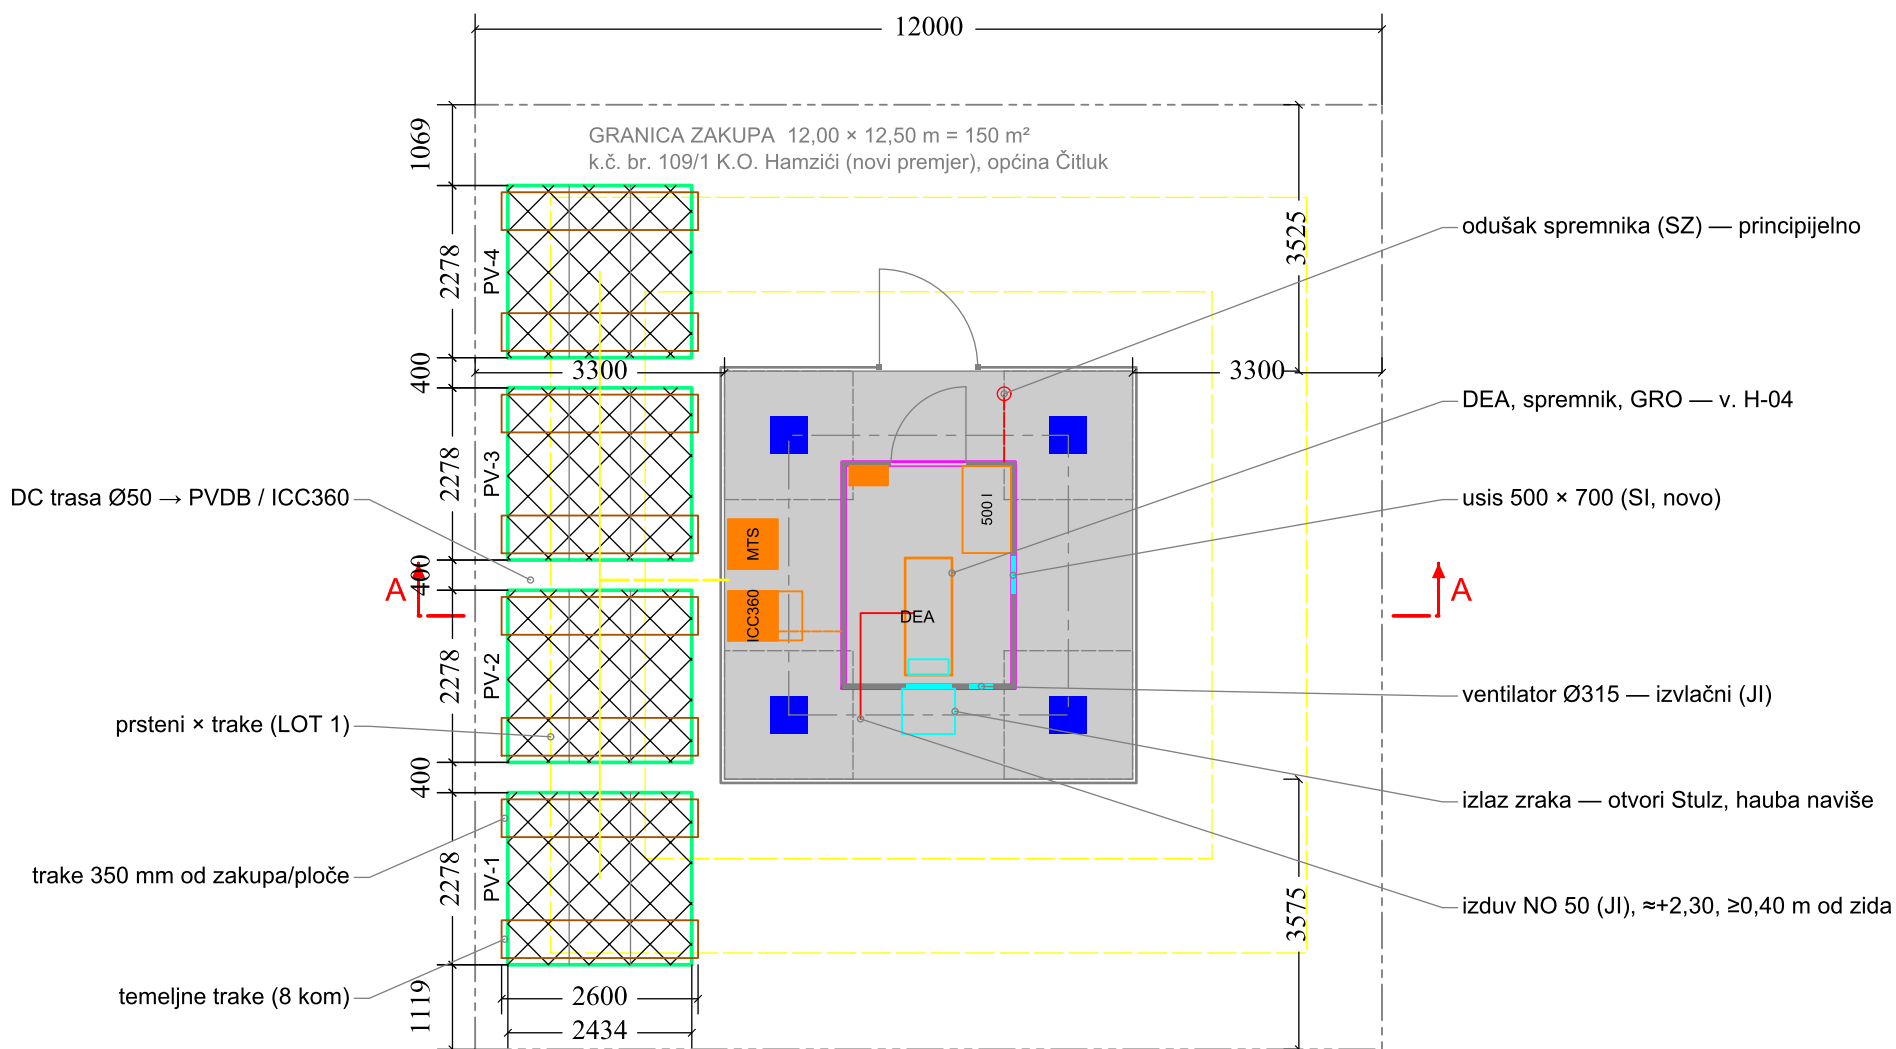

- FN nosači PV-1..PV-4 — po 3 × 585 Wp (1 × 3, položeno), 45°, azimut 225° (JZ) — 2 stringa × 6
- AB temeljne trake 500 × 2600 mm, d = 900 mm, razmak 1600 mm — 8 kom
- DC trasa u PEHD Ø50 (isprekidano) — od polja do PVDB uz ICC360
- DEA 18 kVA (skid), spremnik 500 l u koritu, novi GRO
- usis 500 × 700 (SI), izlaz zraka kroz otvore Stulz (JI) i haubu naviše, ventilator Ø315 (JI)
- izdub NO 50 (JI, ≈2,30 m); odušak spremnika (SZ, isprekidano); presjek A–A
- Huawei ICC360-HA1-C1 u MTS vani na ploči (SZ), iza FN polja — principijelno



Kompleks je zakrenut 45°: vrata kontejnera i kapija gledaju na SJEVEROZAPAD (SZ), klima-uređaj Stulz na JI, FN polje na JZ. Crtež je pravougaon na kompleks (gore SZ, desno SI, dolje JI, lijevo JZ); strelica pokazuje pravi sjever. Orientaciju potvrđuje Punaččā obilaskom lokacije.

- 1 Nosači na JUGOZAPAD (azimut 225°), nagib 45°; ivica panela +0,50 / +2,93 m.
- 2 4 odvojena nosača u nizu: $4 \times 2278 + 3 \times 400 = 10312$ mm, u pojasu JZ.
- 3 Temeljne trake 500×2600 mm, d = 900 mm, na podložnom betonu 50 mm.
- 4 Postojeći prsteni uzemljivača (0,8 m) ukrštaju temeljne trake — LOT 1.
- 5 Nosač i temelji — tehničko rješenje i statički proračun Ponudača.
- 6 Raspored u kontejneru prema H-04.
- 7 Ormari ICC360-HA1-C1 i MTS iz FN polja — principijelno.

 BH TELECOM d.d. SARAJEVO Izvršna direkcija za tehnologiju i razvoj servisa	
Investitor:	
BH Telecom d.d. Sarajevo, Franca Lehara 7, Sarajevo	
Objekat:	
BS HAMZIĆI (ČITLUK) — autonomni hibridni sistem napajanja	
Faza:	šifra projekta:
Tenderska dokumentacija — Prilog III	BHT-HAMZICI-2026
Naziv crteža:	razmjera:
Situacija — BUDUĆE STANJE	1:100
Projektant:	godina / broj crteža:
Rusmir Skopljak, dipl. inq. el.	2026. H-02
ovjerio:	
Rusmir Skopljak, dipl. inq. el.	