


PRESJEK A–A (osa SZ trake nosača PV-2 — pogled prema SJEVEROZAPADU)

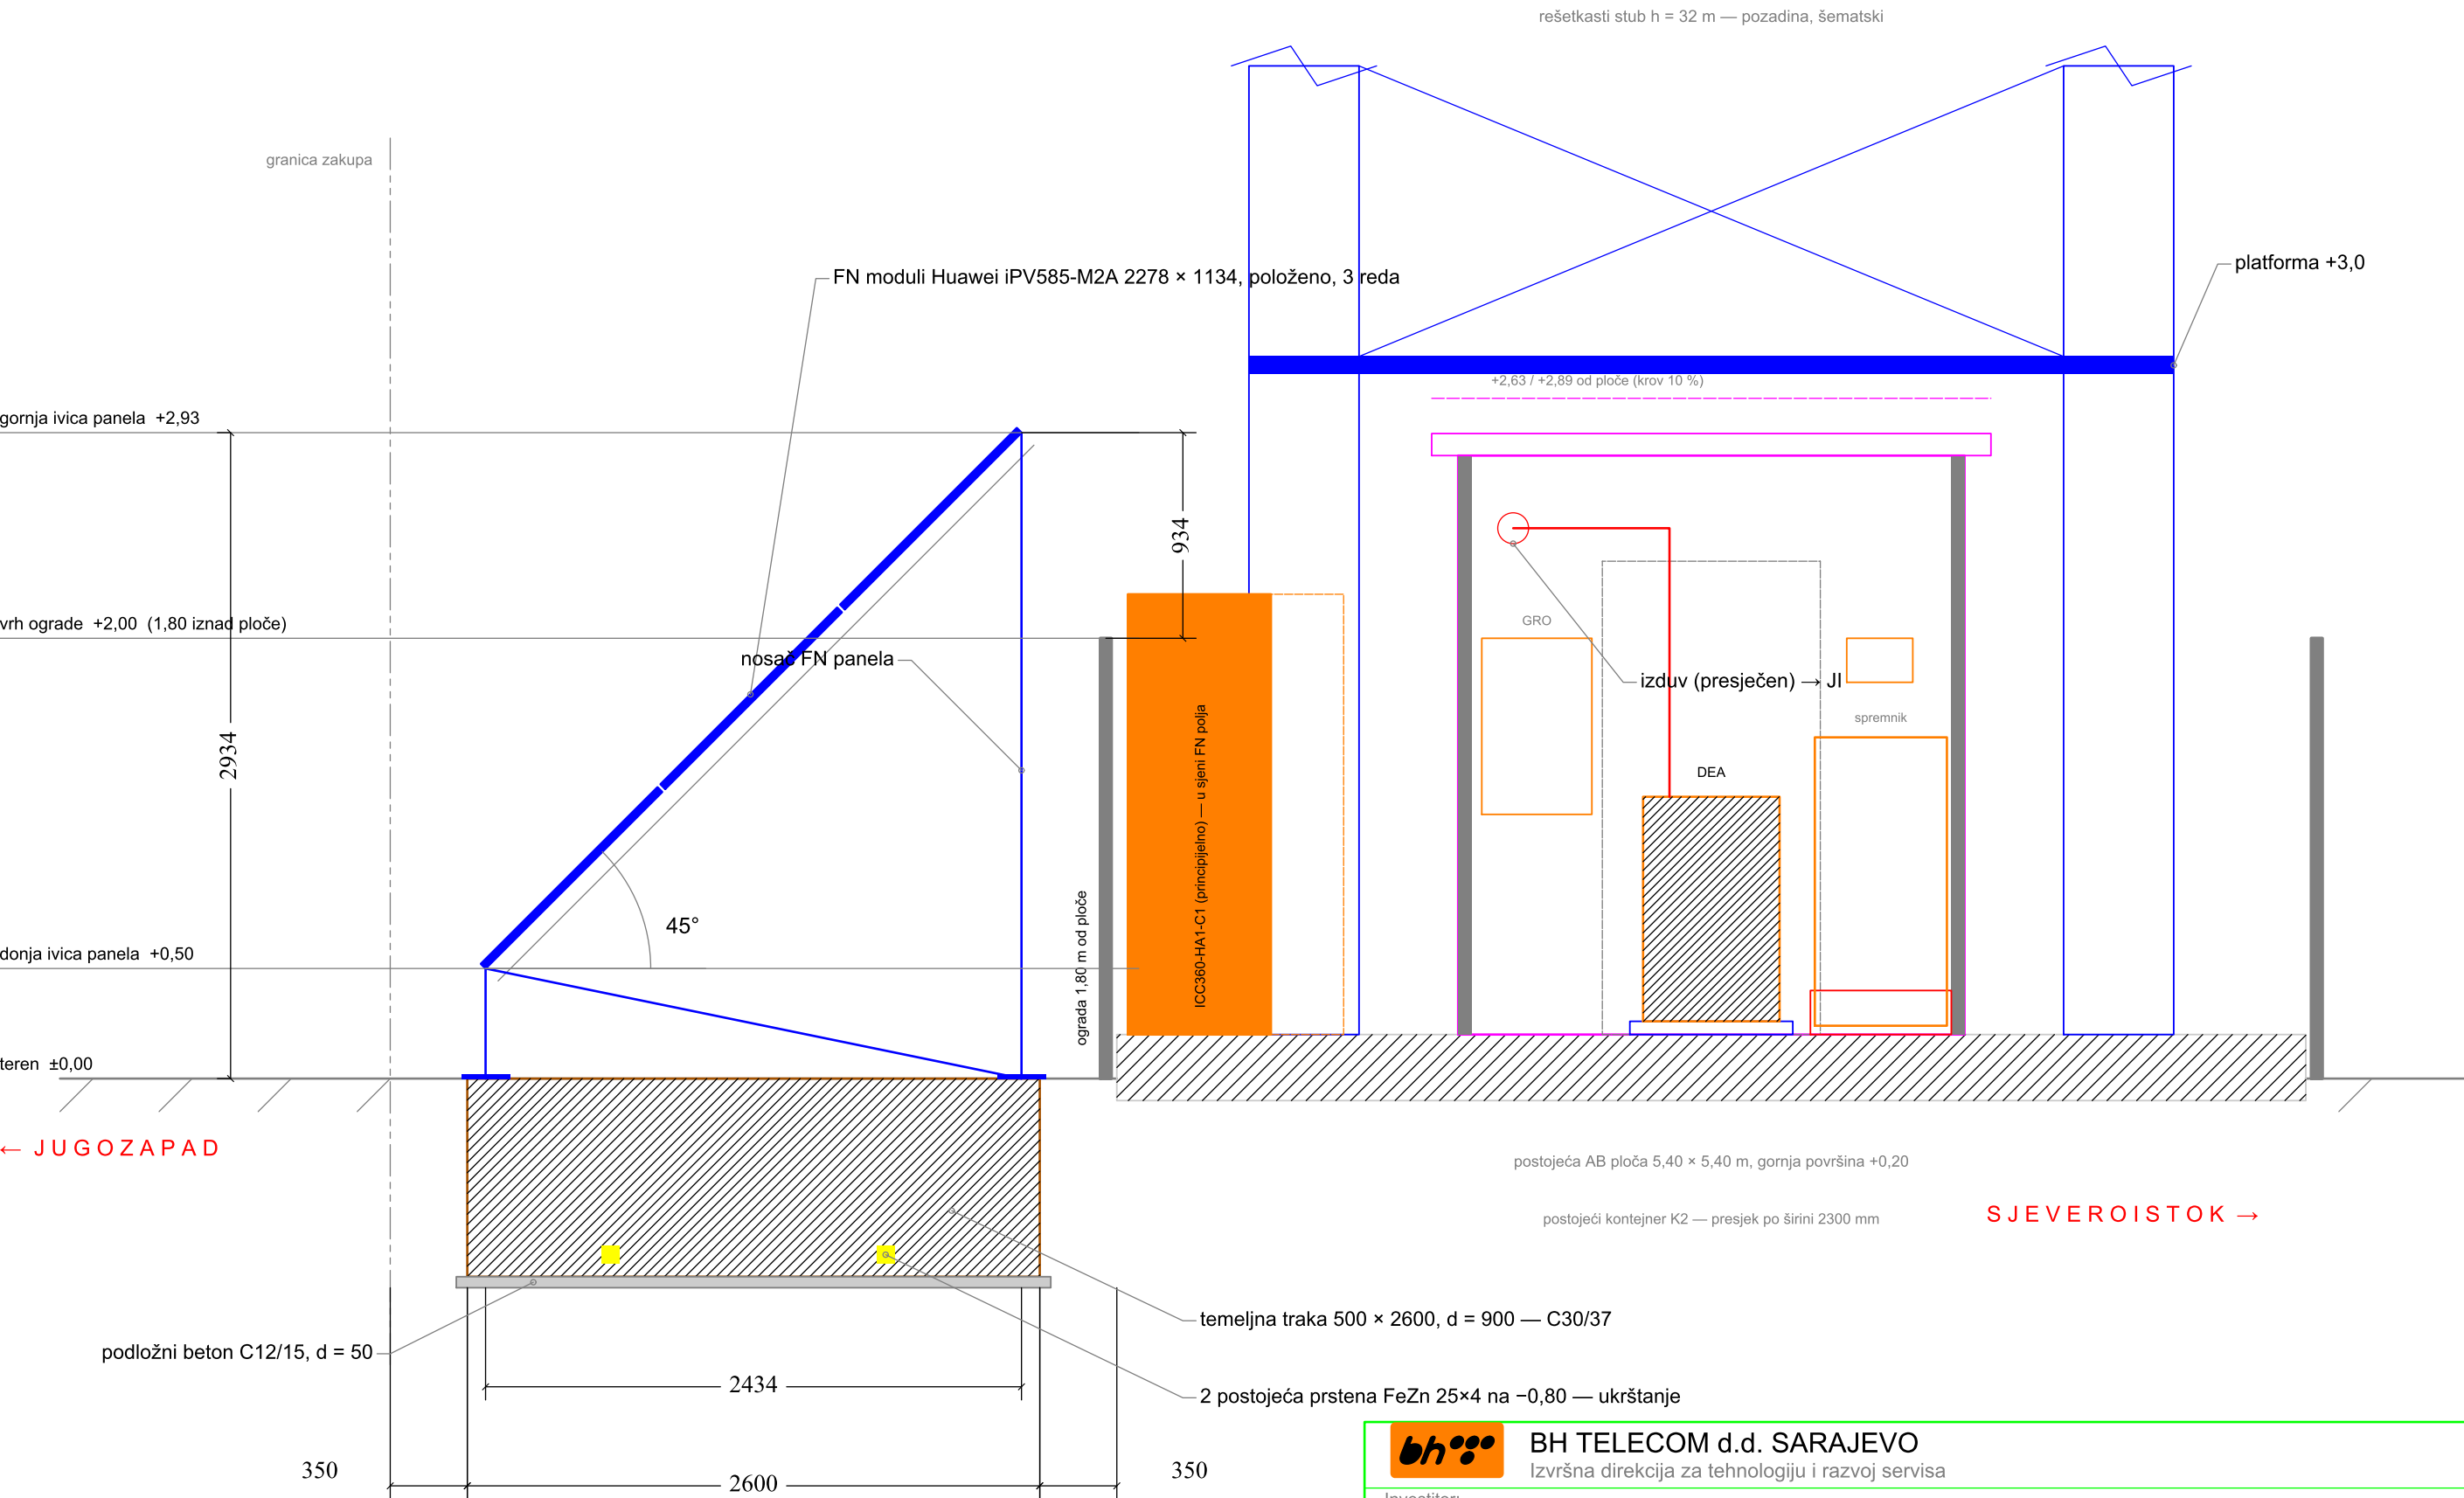

- NAPOMENE:**
- Polje: 3 reda × 1 modul 585 Wp, položeno; nagib 45°, projekcija 2434 mm; 4 odvojena nosača u nizu (H-02).
  - Dvije temeljne trake po nosaču 500 × 2600 mm, dubina 900 mm, razmak 1600 mm (druga iza ravni presjeka); beton C30/37 (XC4+XF3), armatura B500B, na podložnom betonu C12/15 d = 50 mm.
  - Kote od terena uz FN polje; teren je −0,20 m ispod ploče (04\_Ograda). Donja ivica panela +0,50, gornja +2,93; vrh ograde +2,00 (1,80 m iznad ploče) — gornja ivica je 0,93 m iznad ograde.
  - Postojeći prsteni uzemljivača na 0,8 m presijecaju traku: lociranje, otkopavanje i premještanje ili premoštavanje prstena (LOT 1).
  - Trake su 350 mm od granice zakupa (JZ) i od ploče (SI); položaj presjeka na H-02.
  - Stub, platforma P I (+3,0 m), kontejner i ormari šematski; ICC360 i MTS su iza FN polja.

|   |                                             |                                     |
|---|---------------------------------------------|-------------------------------------|
| <div><div>bh</div><div>BH TELECOM d.d. SARAJEVO</div><div>Izvršna direkcija za tehnologiju i razvoj servisa</div></div> |                                             |                                     |
| Investitor:<br>BH Telecom d.d. Sarajevo, Franca Lehara 7, Sarajevo                                                      |                                             |                                     |
| Objekat:<br>BS HAMZIĆI (ČITLUK) — autonomni hibridni sistem napajanja                                                   |                                             |                                     |
| Faza:<br>Tenderska dokumentacija — Prilog III                                                                           |                                             | šifra projekta:<br>BHT-HAMZICI-2026 |
| Naziv crteža:<br>Presjek A–A kroz FN polje                                                                              |                                             | razmjera:<br>1:30                   |
| Projektant:<br>Rusmir Skopljak, dipl. ing. el.                                                                          | ovjerio:<br>Rusmir Skopljak, dipl. ing. el. | godina / broj crteža:<br>2026. H-03 |