



OSNOVA — kontejner je PRAZAN; klima-uređaj Stulz se demontira

PRESJEK 1-1 (os agregata — pogled prema SI, SZ lijevo)

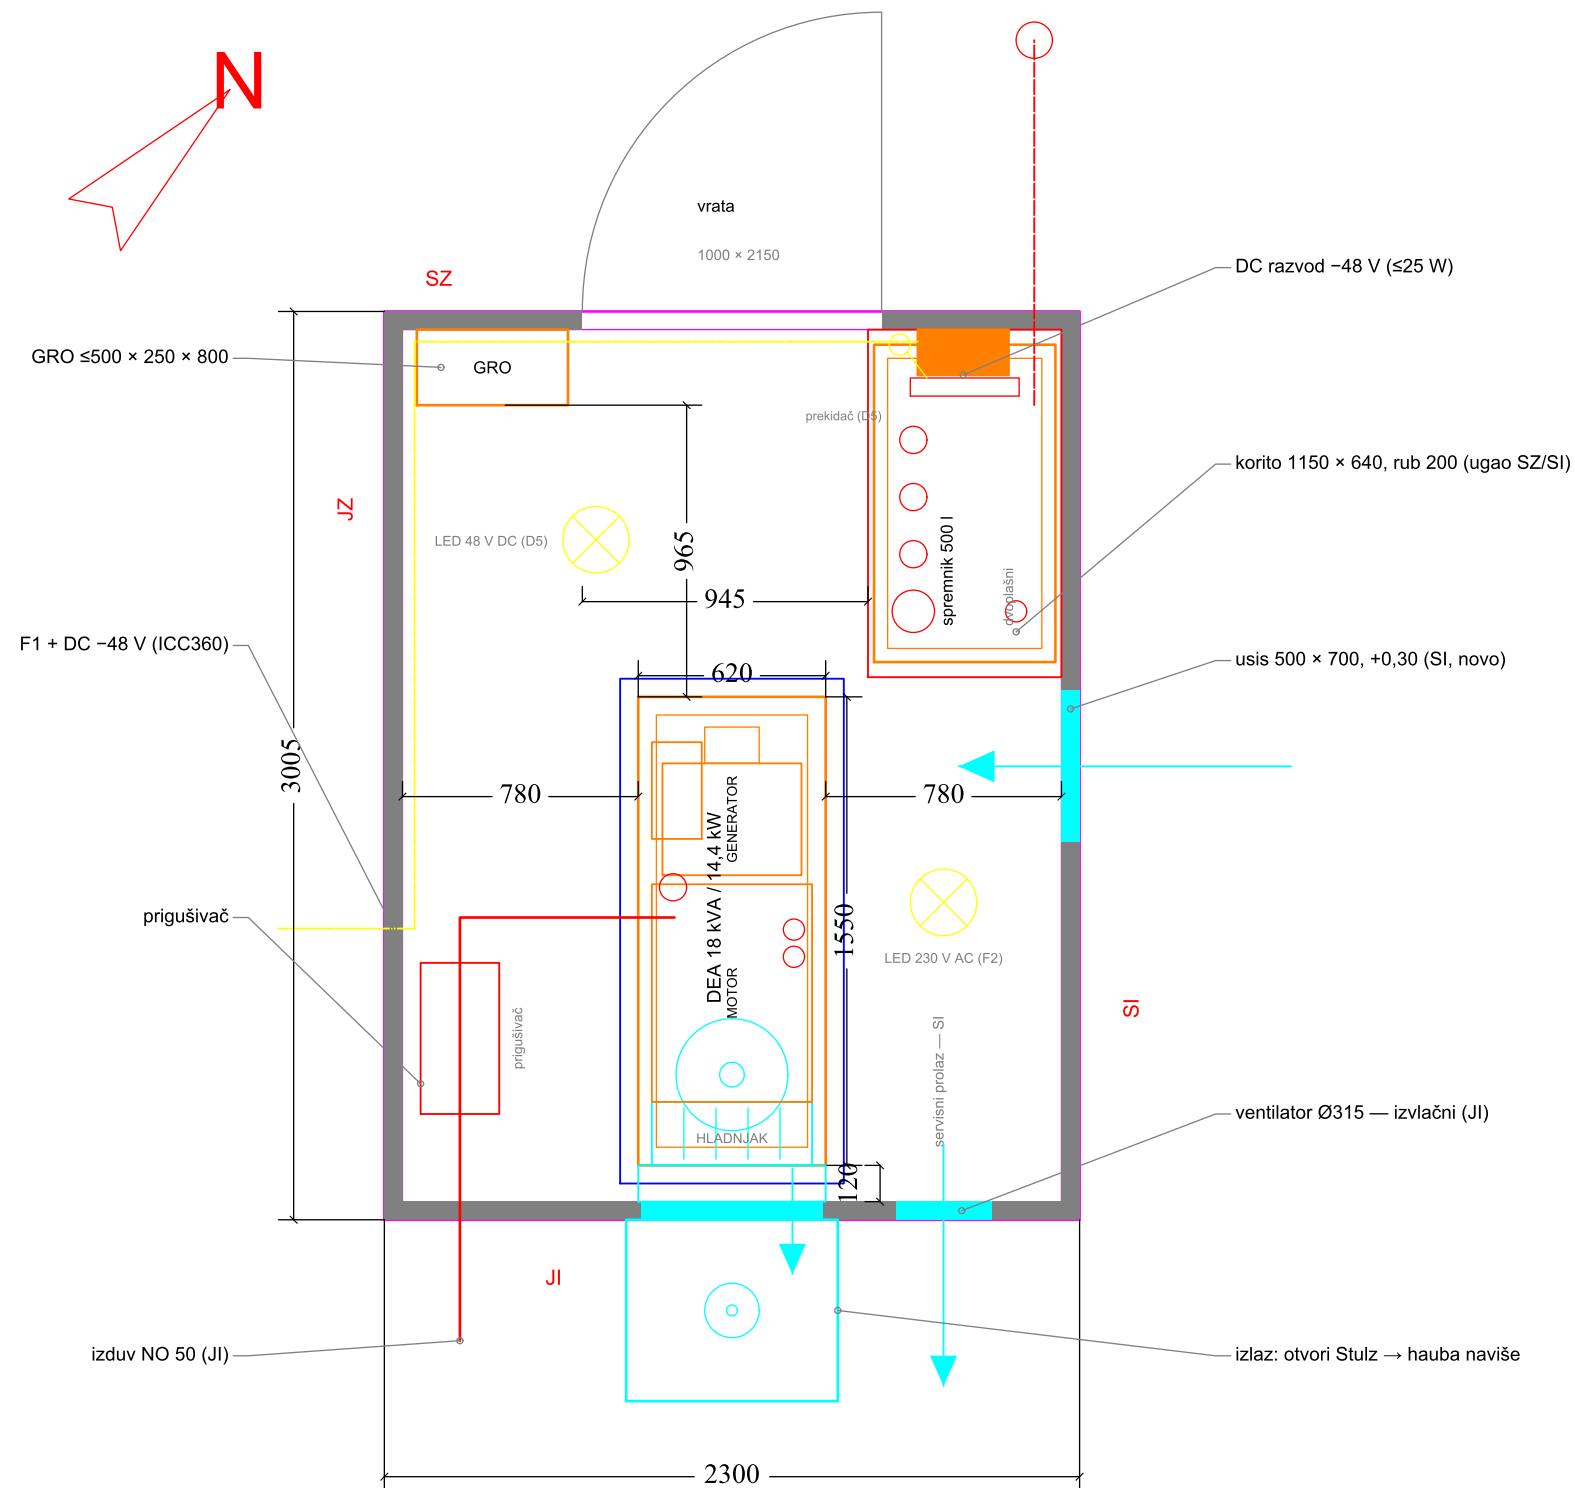

NAPOMENE:

1. DEA FG Wilson P18-6 (skid) ili ekv., 18 kVA / 14,4 kW; os SZ-JI, hladnjak JI.
2. Izlaz zraka kroz postojeće otvore Stulz (sredina JI zida), $\geq 0,36 \text{ m}^2$ bruto, limeni plenum i hauba 700×600 — topli zrak NAVIŠE.
3. Uis 500 $\times$ 700 na SI zidu (+0,30). Izludv NO 50 kroz JI zid na $\approx 2,30 \text{ m}$, ispod platforme stuba.
4. GRO $\leq 500 \times 250 \times 800$ na SZ zidu; spremnik 500 l dvoplašni u koritu 1150×640 ; roštilj OBAVEZAN pod skidom i koritom.
5. Servisni prolazi $780 / 780 \text{ mm}$ i 965 mm do GRO; unos skida 620 mm kroz vrata 990 mm .
6. Ventilator Ø315 (JI, izvlačni, D4) i DC razvod -48 V istočno od vrata — H-05.
7. Raspored je principijelan; mjere otvora i servisne tačke potvrđuje Ponuđač na licu mjesta. Zahtjevi: Prilog I, Tačka 4.

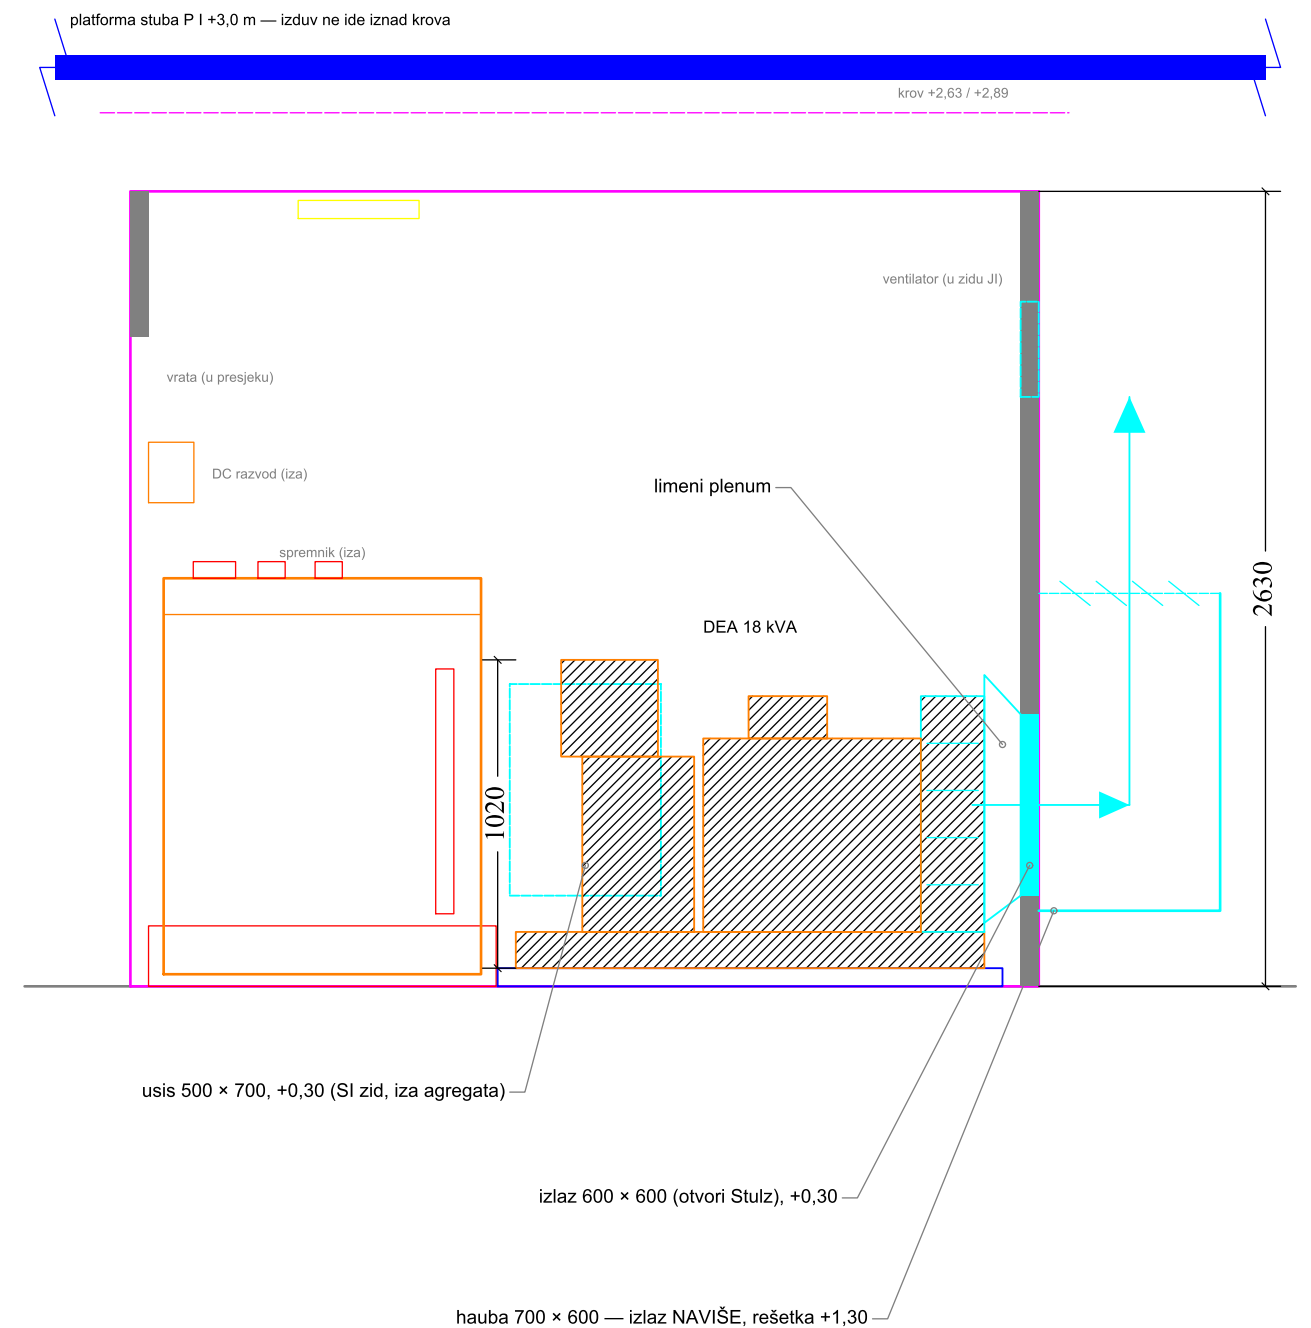

BH TELECOM d.d. SARAJEVO

Izvršna direkcija za tehnologiju i razvoj servisa

Investitor:

BH Telecom d.d. Sarajevo, Franca Lehara 7, Sarajevo

Objekat:

BS HAMZIĆI (ČITLUK) — autonomni hibridni sistem napajanja

Faza:

Tenderska dokumentacija — Prilog III

šifra projekta:

BHT-HAMZICI-2026

Naziv crteža:

Agregat u kontejneru — osnova i presjek 1–1

razmjera:

1:25

Projektant:

Rusmir Skopljak, dipl. ing. el.

ovjerio:

Rusmir Skopljak, dipl. ing. el.

godina / broj crteža:

2026. H-04