


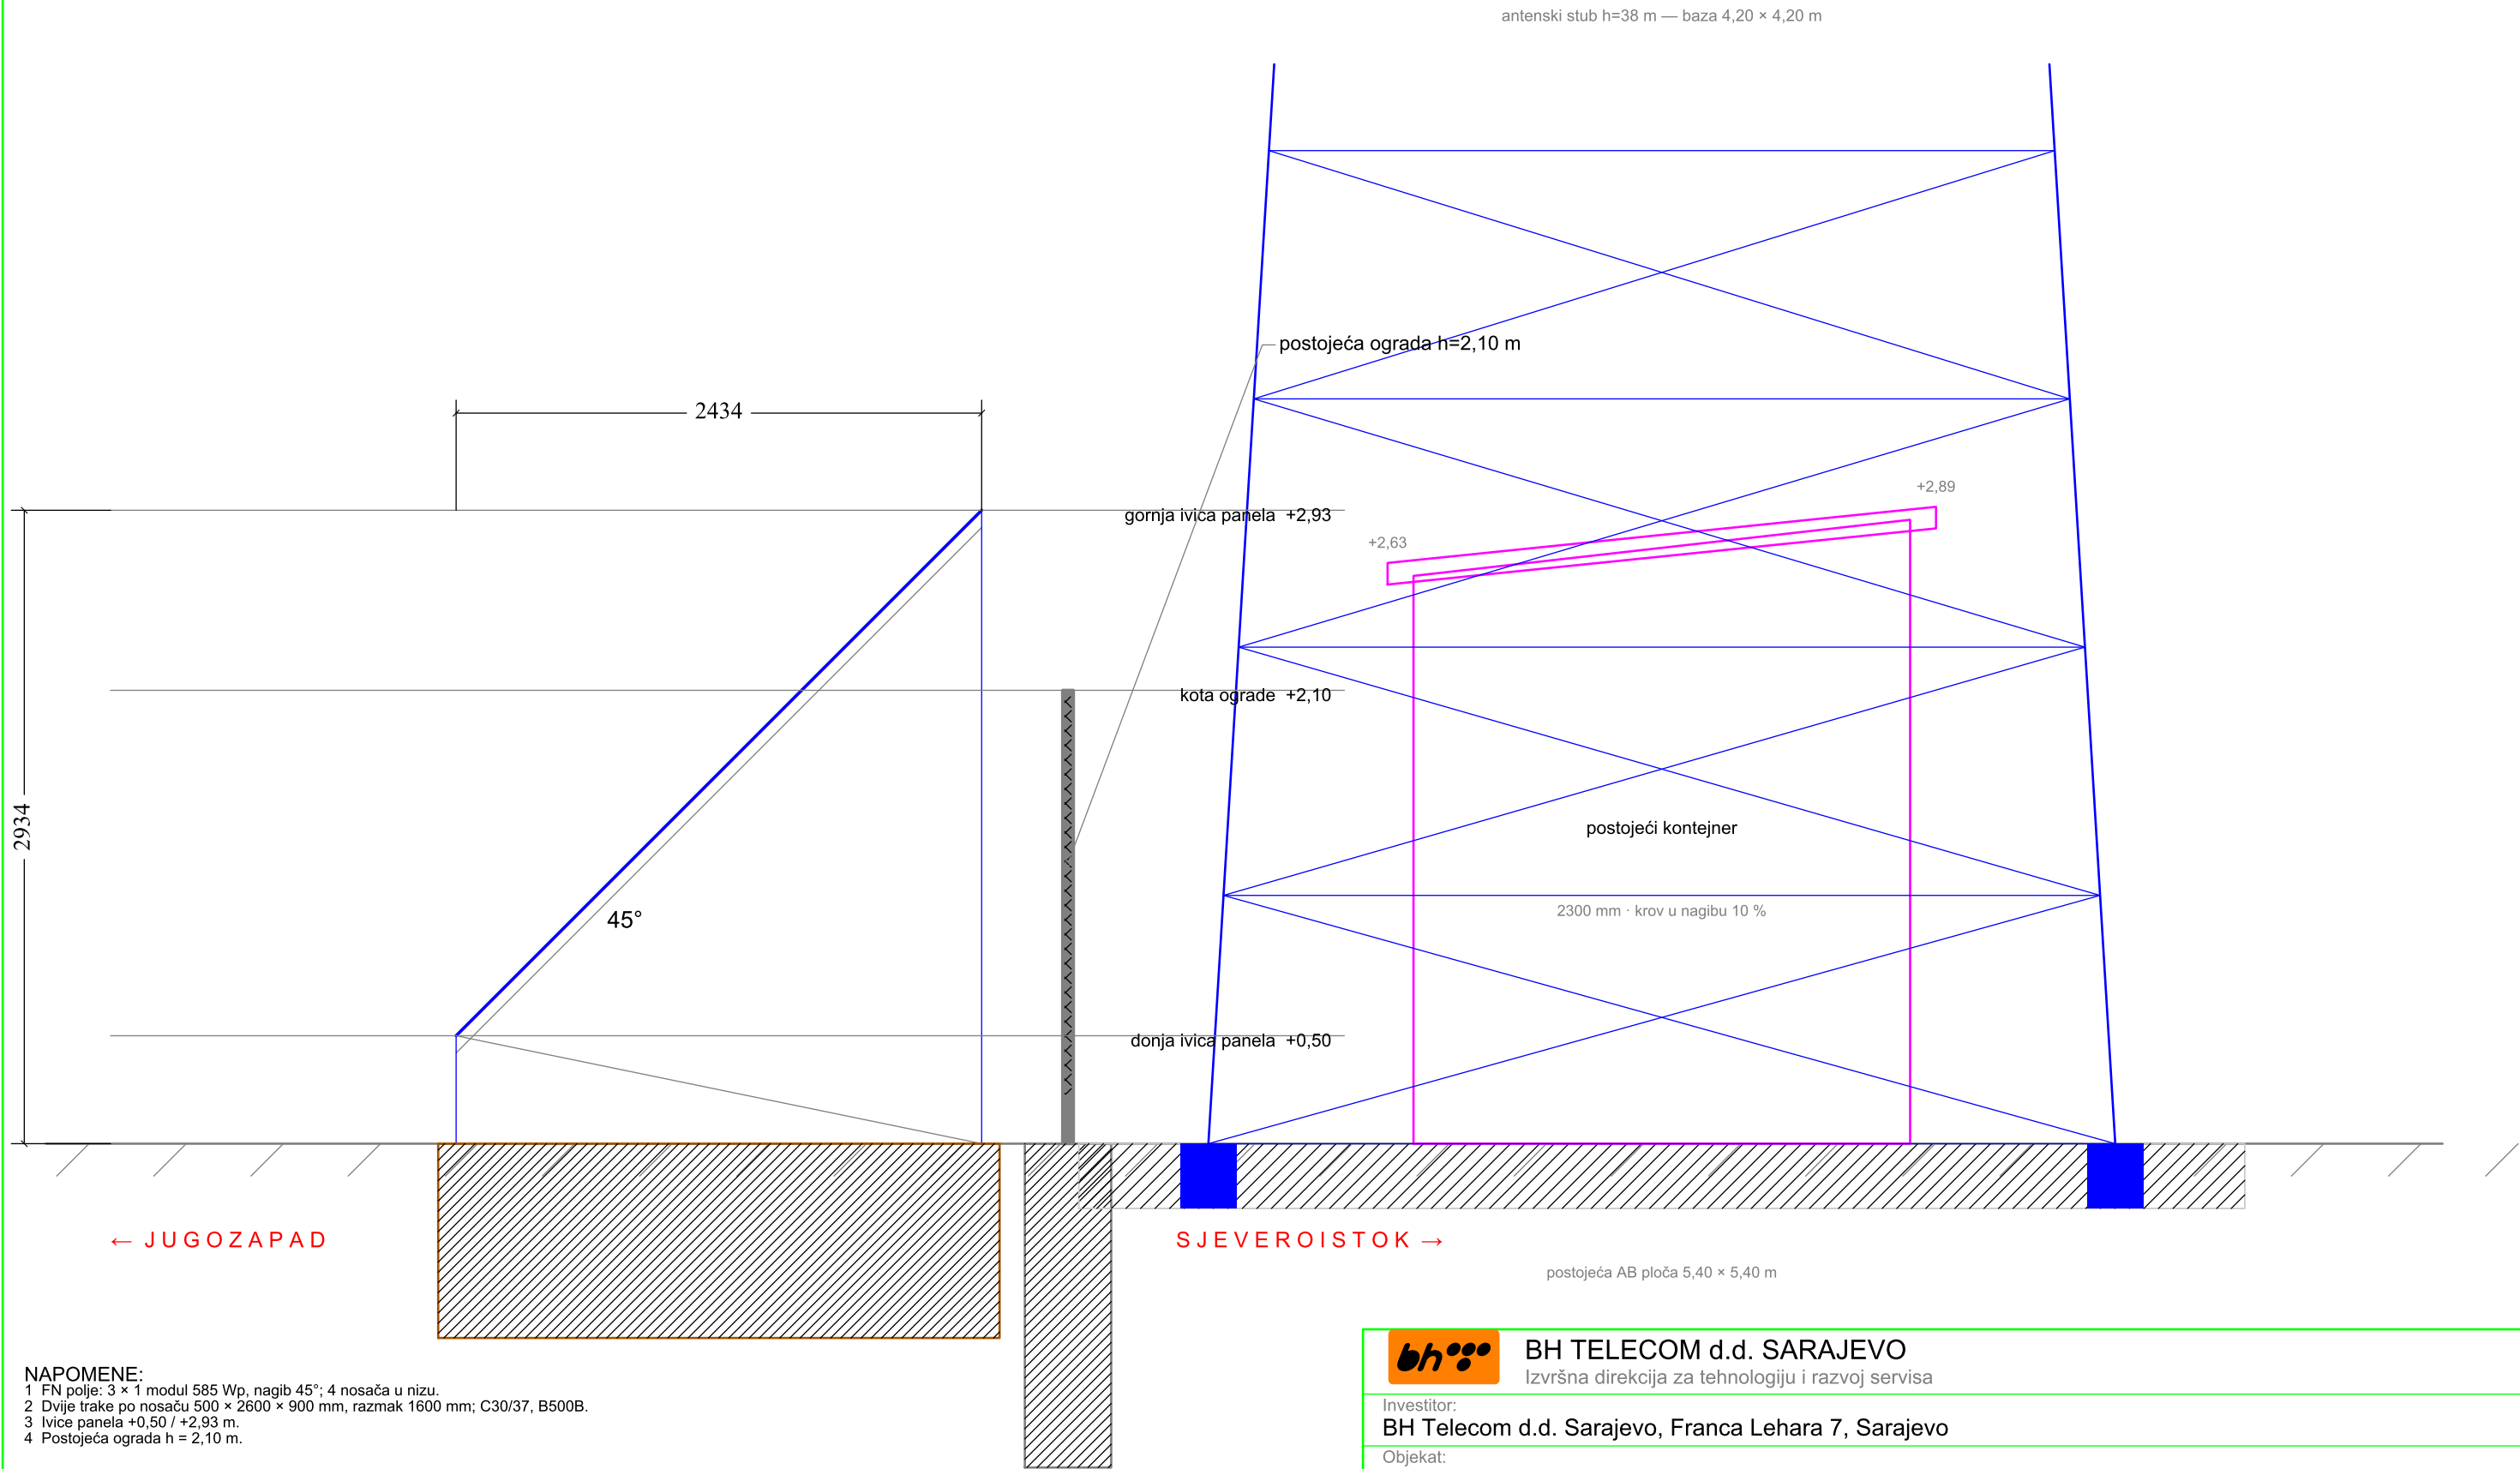

NAPOMENE:
1 FN polje: 3 × 1 modul 585 Wp, nagib 45°; 4 nosača u nizu.
2 Dvije trake po nosaču 500 × 2600 × 900 mm, razmak 1600 mm; C30/37, B500B.
3 Ivice panela +0,50 / +2,93 m.
4 Postojeća ograda h = 2,10 m.

BH TELECOM d.d. SARAJEVO Izvršna direkcija za tehnologiju i razvoj servisa		
Investitor: BH Telecom d.d. Sarajevo, Franca Lehara 7, Sarajevo		
Objekat: BS SJEDNICA (Bileća) — autonomni hibridni sistem napajanja		
Faza: Tenderska dokumentacija — Prilog III		šifra projekta: BHT-SJEDNICA-2026
Naziv crteža: Presjek A–A kroz nosač FN panela		razmjera: 1:30
Projektant: Rusmir Skopljak, dipl. ing. el.	ovjerio: Rusmir Skopljak, dipl. ing. el.	godina / broj crteža: 2026. S-03