


POGLED SA JUGOZAPADA (pravac gledanja azimut 45°)

LEGENDA

- LOT 1 — FN moduli i nosači (ispred ograde, JZ)
- postojeći antenski stub — silueta iz ovjerenog projekta
- postojeći kontejner K2 na postojećoj ploči
- postojeća oграда h = 2,10 m

NAPOMENE:

- Ortogonalni pogled u pravcu azimuta 45°.
- Paneli su prikazani skraćeno: +0,50 do +2,93 m.
- Stub je prekinut na +9,50 m; h = 38 m.
- Zahtjevi: Prilog I, Tačke 3 i 4.

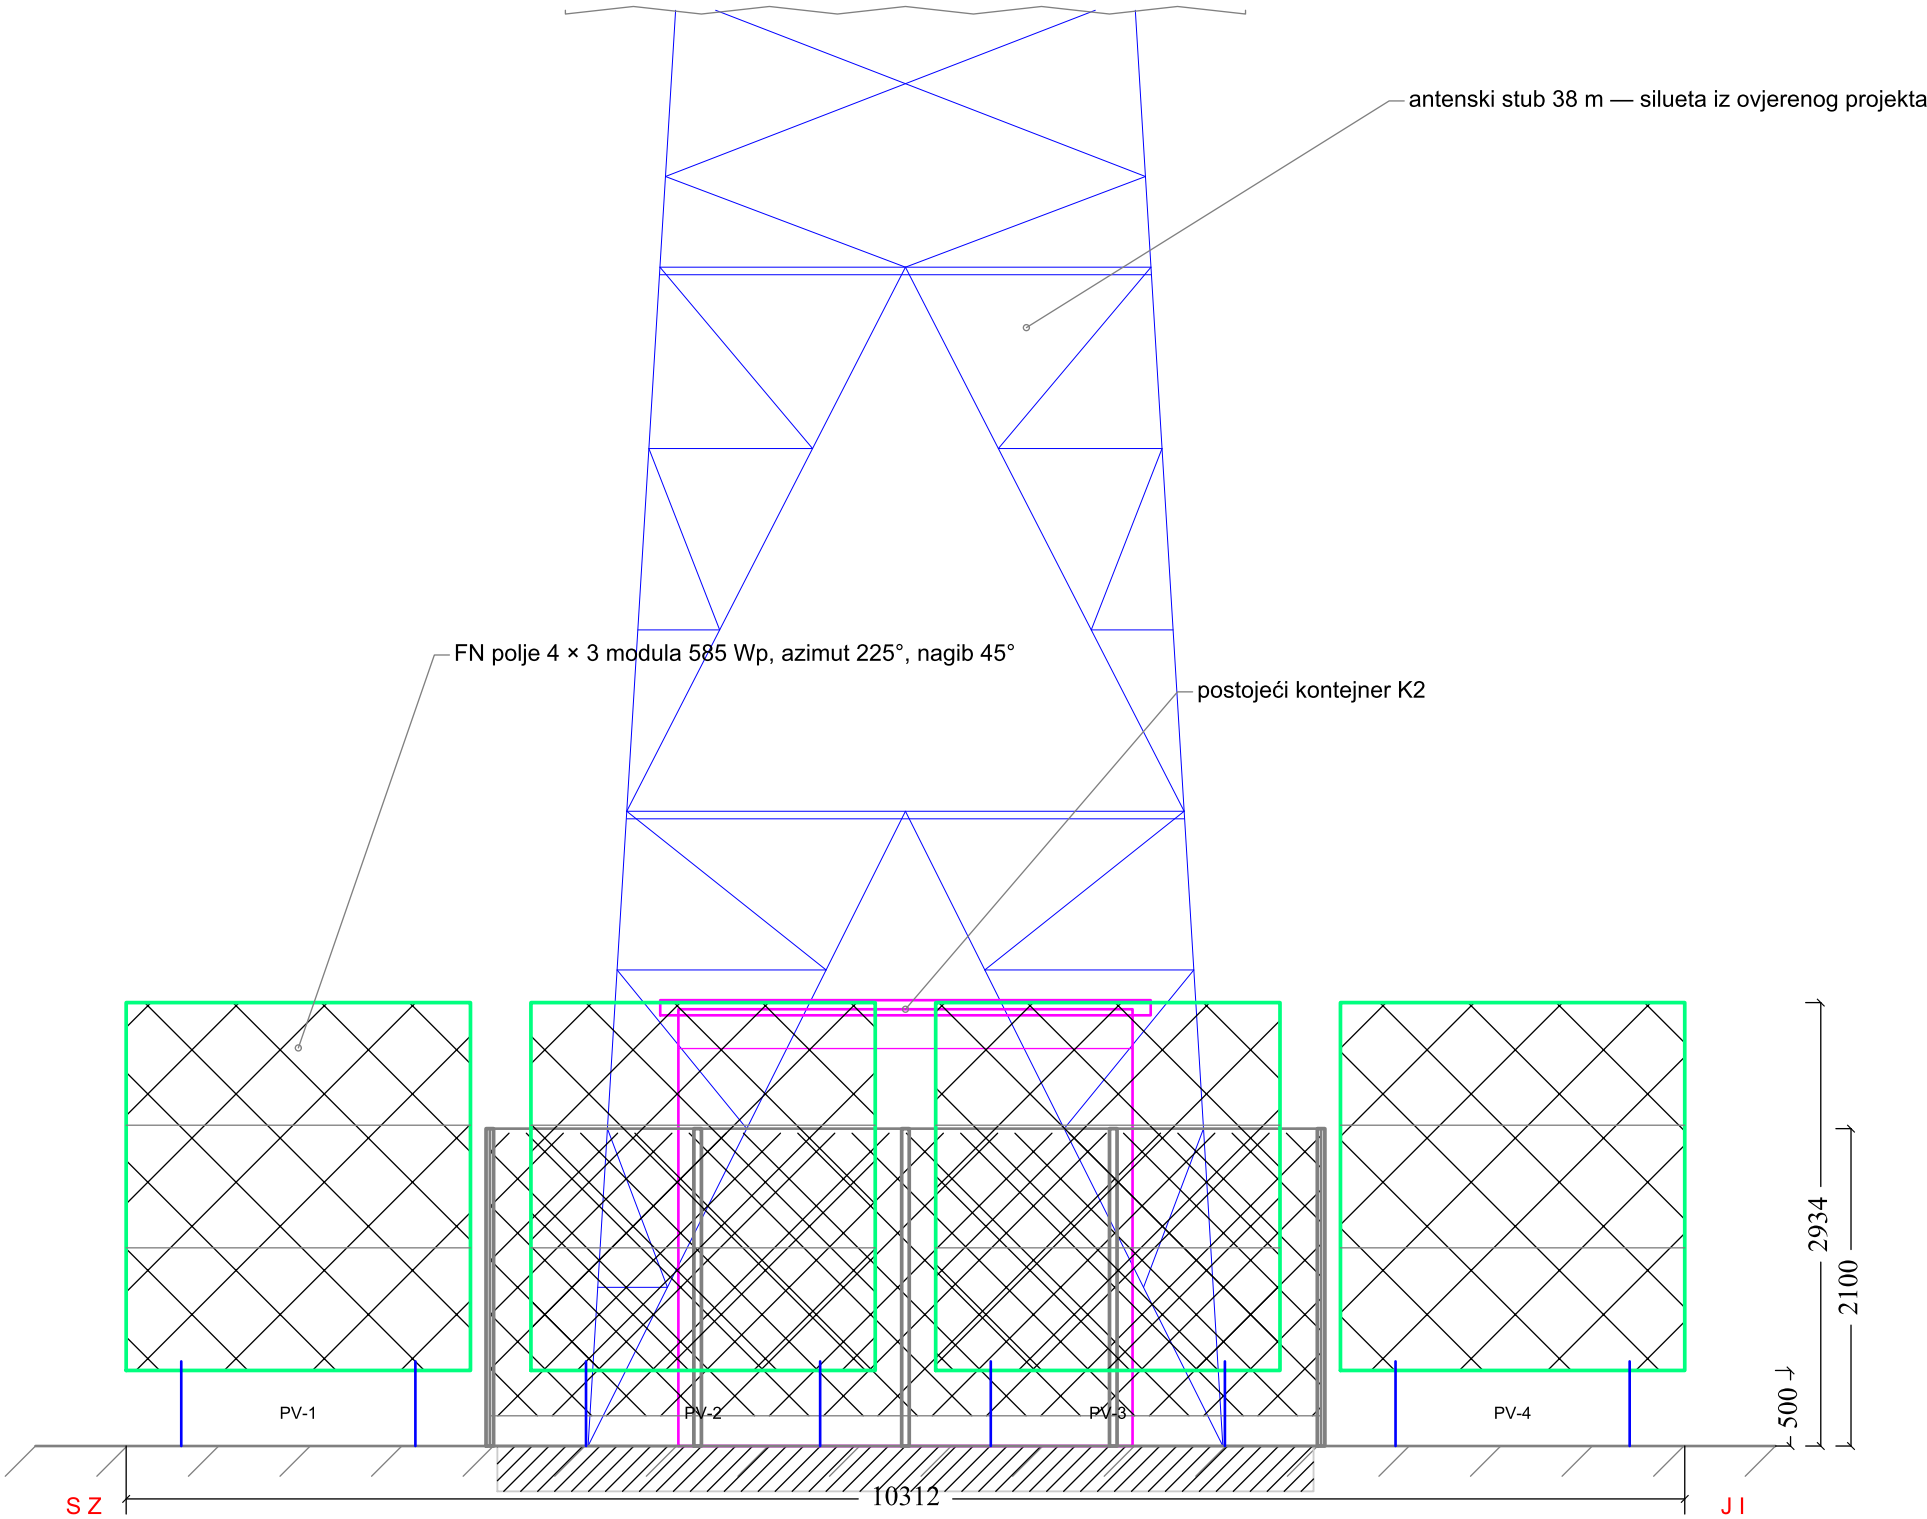

|   |                                             |                                      |
|---|---------------------------------------------|--------------------------------------|
| <div><div><div>bh</div></div><div><div>BH TELECOM d.d. SARAJEVO</div><div>Izvršna direkcija za tehnologiju i razvoj servisa</div></div></div> |                                             |                                      |
| Investitor:<br>BH Telecom d.d. Sarajevo, Franca Lehara 7, Sarajevo                                                                            |                                             |                                      |
| Objekat:<br>BS SJEDNICA (Bileća) — autonomni hibridni sistem napajanja                                                                        |                                             |                                      |
| Faza:<br>Tenderska dokumentacija — Prilog III                                                                                                 |                                             | šifra projekta:<br>BHT-SJEDNICA-2026 |
| Naziv crteža:<br>Pogled sa JUGOZAPADA — kompleks sa FN poljem                                                                                 |                                             | razmjera:<br>1:50                    |
| Projektant:<br>Rusmir Skopljak, dipl. ing. el.                                                                                                | ovjerio:<br>Rusmir Skopljak, dipl. ing. el. | godina / broj crteža:<br>2026. S-04  |