
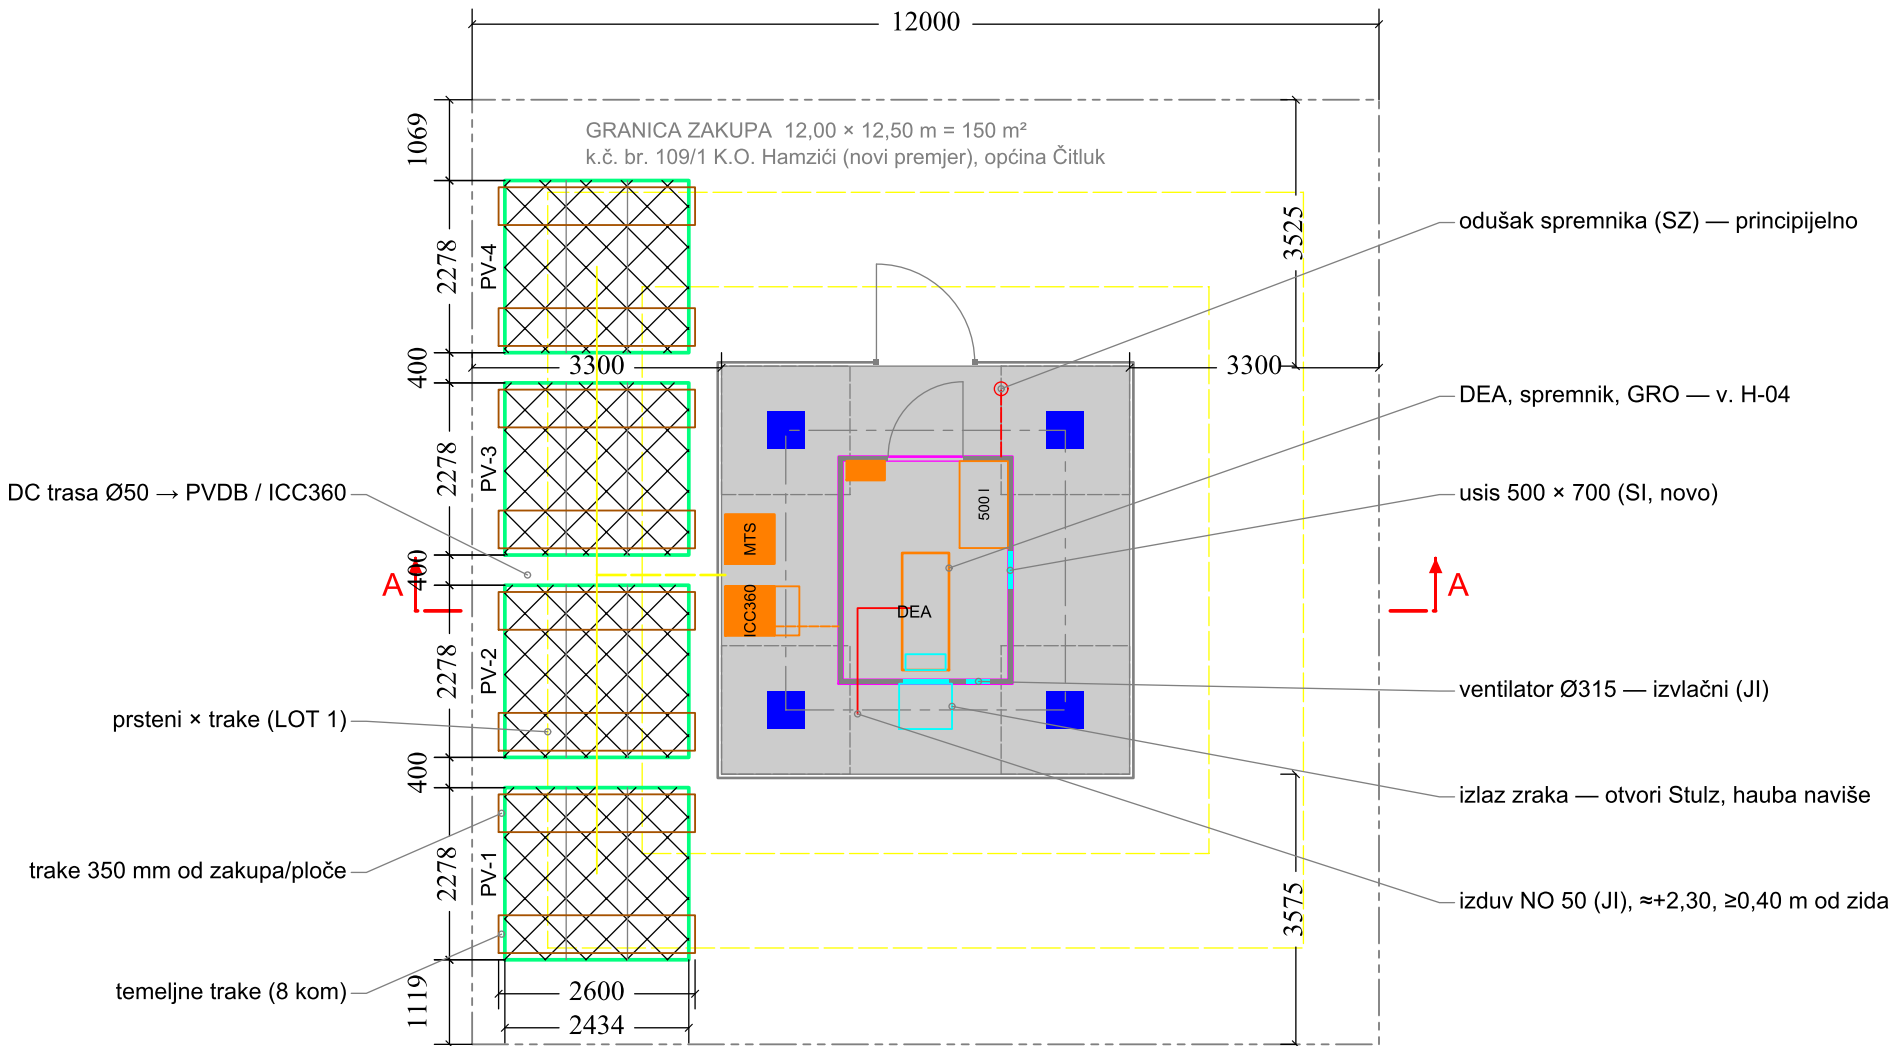


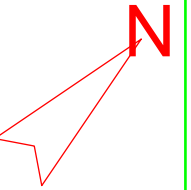

NAPOMENA — ORIJENTACIJA:
Kompleks je zakrenut za 45°; strelica označava pravi sjever.
Orijentaciju potvrđuje Ponuđač na lokaciji.

- NAPOMENE:**
- 1 Azimut 225°, nagib 45°; ivice panela +0,50 / +2,93 m od ploče.
 - 2 Niz od 4 nosača, ukupne dužine 10312 mm.
 - 3 Temeljne trake 500 x 2600 x 900 mm; vrh u nivou ploče.
 - 4 Postojeći prsteni uzemljivača se lociraju i štite (LOT 1).
 - 5 Nosači i temelji prema tehničkom rješenju Ponuđača.
 - 6 Raspored u kontejneru: H-04. Ormari ICC360 i MTS prikazani su principijelno.

LEGENDA

- FN nosači PV-1..PV-4 — po 3 x 585 Wp (1 x 3, položeno), 45°, azimut 225° (JZ) — 2 stringa x 6
- AB temeljne trake 500 x 2600 mm, d = 900 mm, razmak 1600 mm — 8 kom
- DC trasa u PEHD Ø50 (isprekidano) — od polja do PVDB uz ICC360
- DEA 18 kVA (skid), spremnik 500 l u koritu, novi GRO
- usis 500 x 700 (SI), izlaz zraka kroz otvore Stulz (JI) i haubu naviše, ventilator Ø315 (JI)
- izdub NO 50 (JI, ≈+2,30 m); odušak spremnika (SZ, isprekidano); presjek A–A
- Huawei ICC360-HA1-C1 i MTS vani na ploči (JZ), iza FN polja — principijelno



BH TELECOM d.d. SARAJEVO

Izvršna direkcija za tehnologiju i razvoj servisa

Investitor:

BH Telecom d.d. Sarajevo, Franca Lehara 7, Sarajevo

Objekat:

BS HAMZIĆI (ČITLUK) — autonomni hibridni sistem napajanja

Faza:

Tenderska dokumentacija — Prilog III

Naziv crteža:

Situacija — BUDUĆE STANJE

Projektant:

Rusmir Skopljak, dipl. ing. el.

ovjerio:

Rusmir Skopljak, dipl. ing. el.

šifra projekta:

BHT-HAMZICI-2026

razmjera:

1:100

godina / broj crteža:

2026. H-02