


PRESJEK A-A (osa SZ trake nosača PV-2 — pogled prema SJEVEROZAPADU)

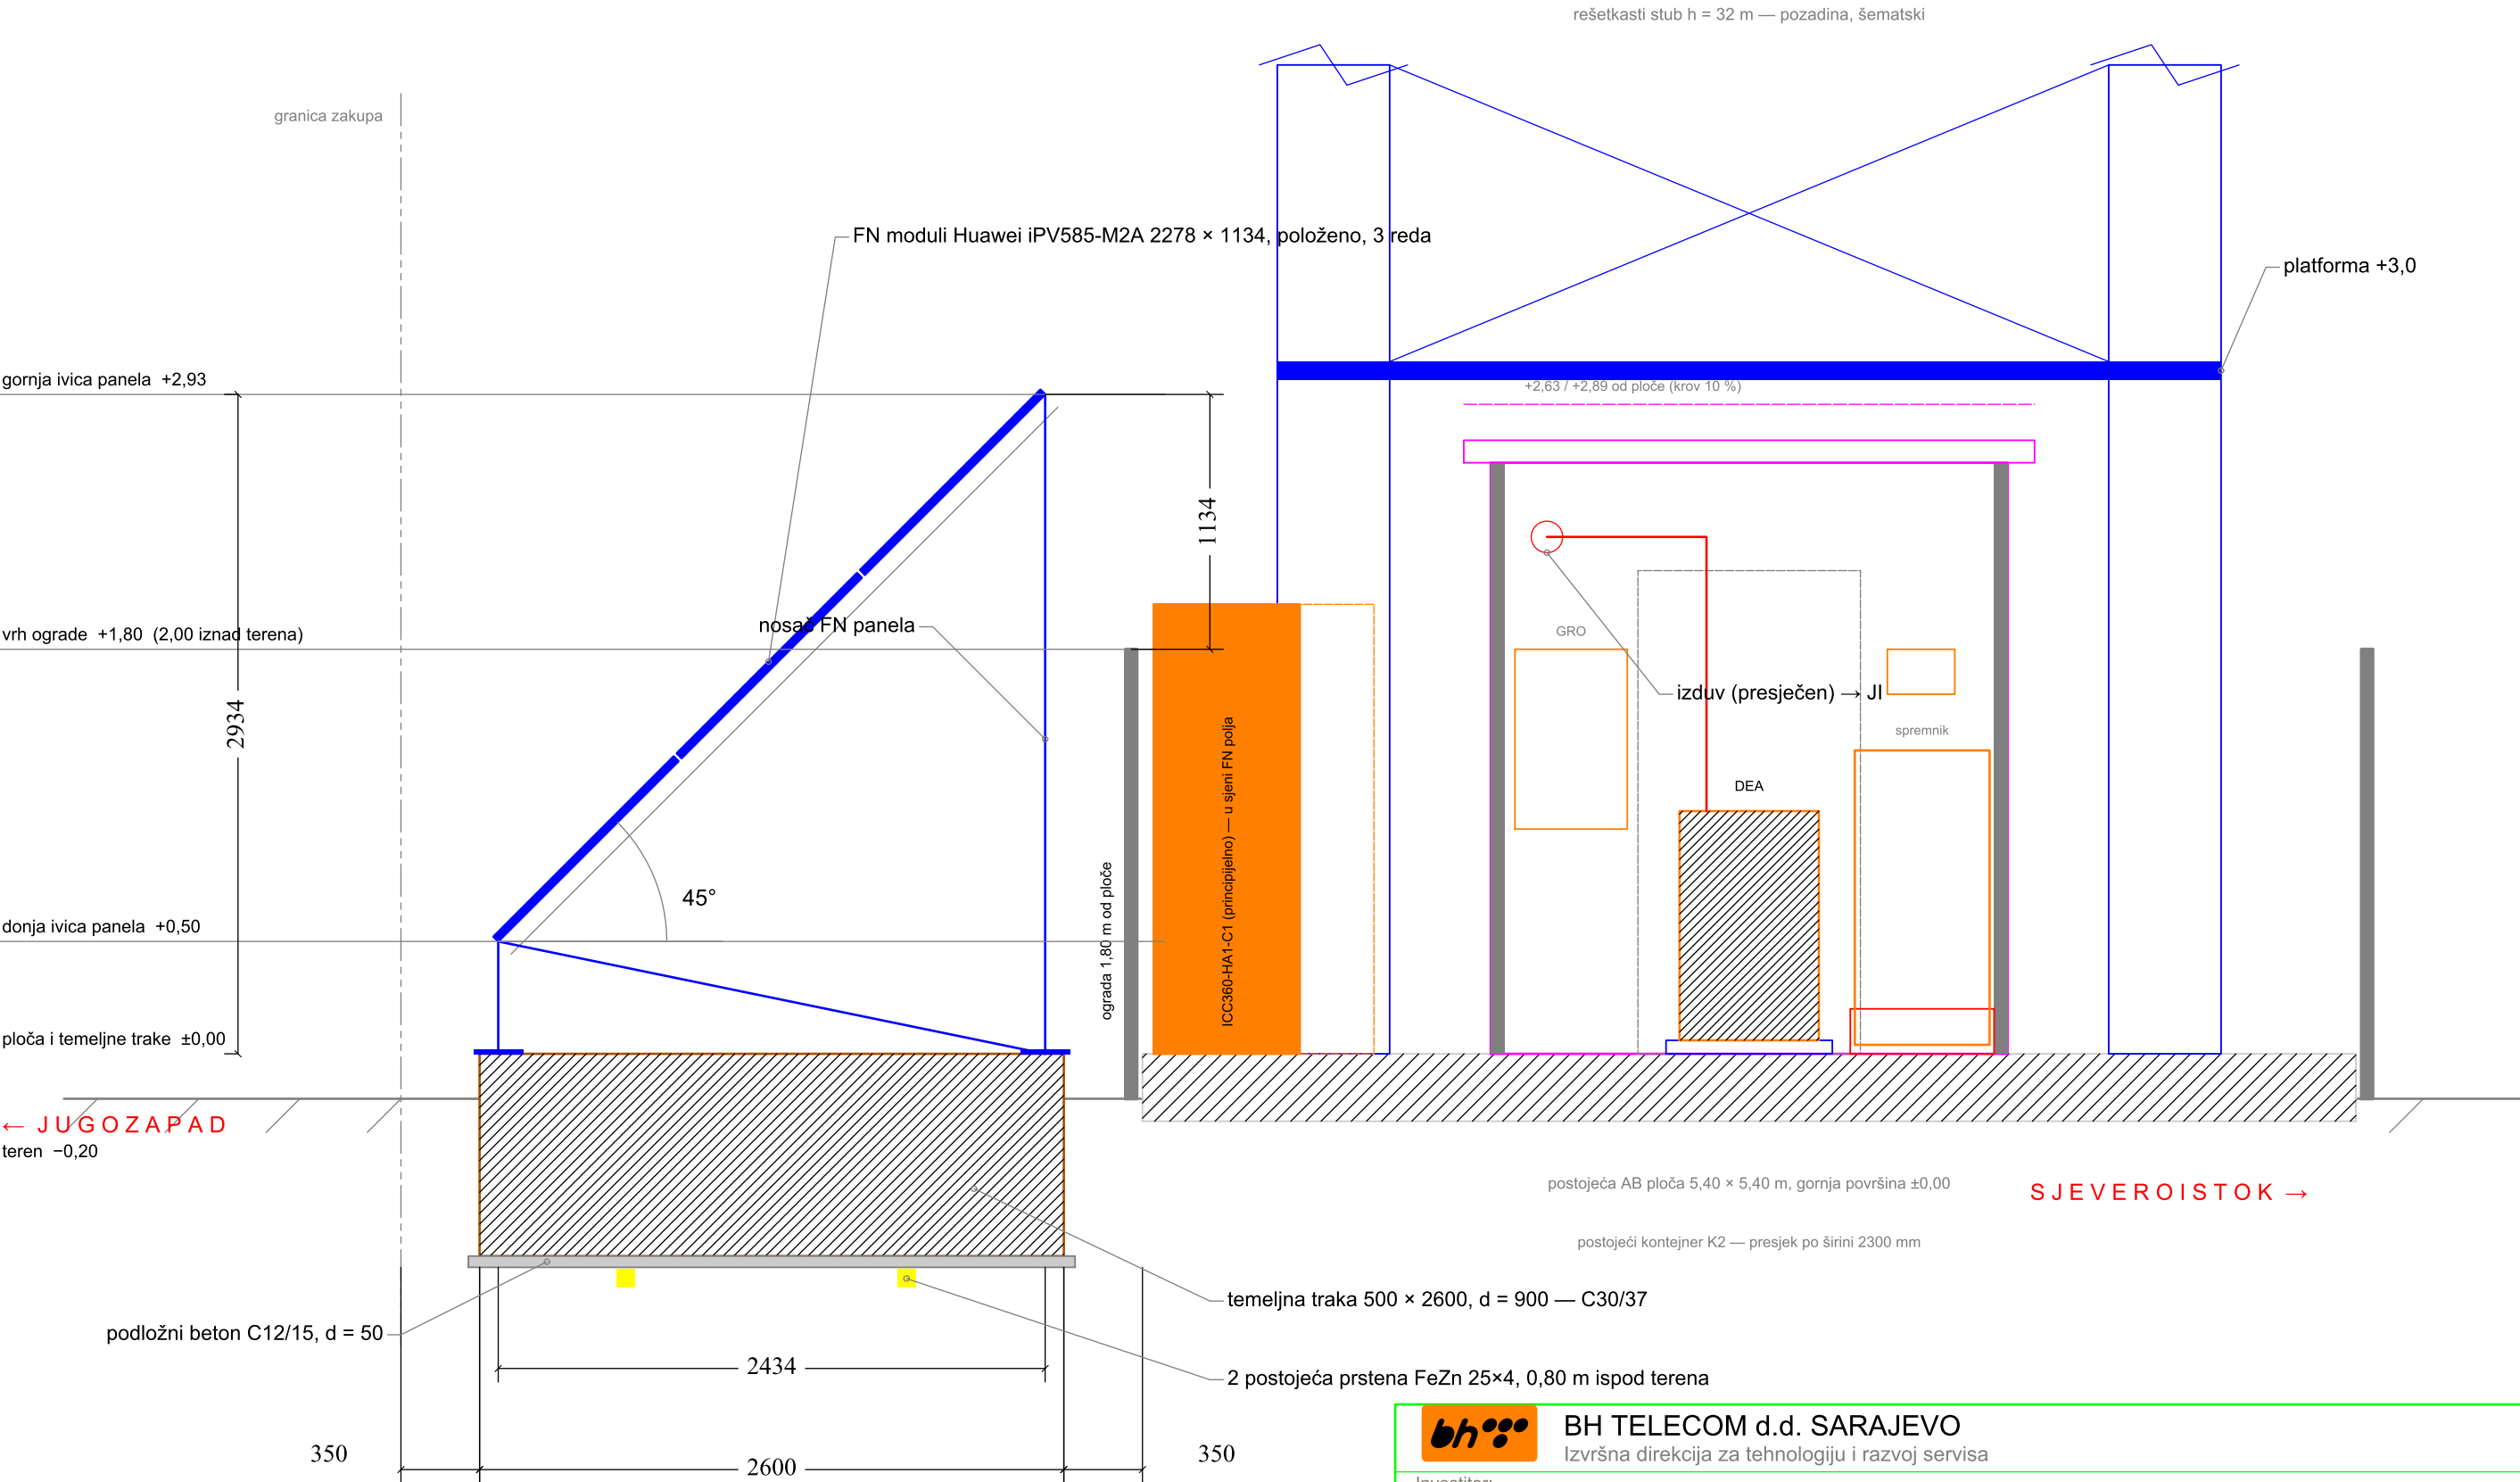

NAPOMENE:
1 FN polje: 3 × 1 modul 585 Wp, nagib 45°; 4 nosača u nizu (H-02).
2 Dvije trake po nosaču 500 × 2600 × 900 mm, razmak 1600 mm; C30/37, B500B.
3 Kote od ploče (±0,00); vrh traka je u nivou ploče, teren na -0,20 m.
4 Gornja ivica panela je 1,13 m iznad ograde.
5 Postojeći prsteni uzemljivača se lociraju i štite (LOT 1).
6 Stub, kontejner i ormari prikazani su šematski.



BH TELECOM d.d. SARAJEVO

Izvršna direkcija za tehnologiju i razvoj servisa

Investitor:

BH Telecom d.d. Sarajevo, Franca Lehara 7, Sarajevo

Objekat:

BS HAMZIĆI (ČITLUK) — autonomni hibridni sistem napajanja

Faza:

Tenderska dokumentacija — Prilog III

Naziv crteža:

Presjek A-A kroz FN polje

Projektant:

Rusmir Skopljak, dipl. ing. el.

ovjerio:

Rusmir Skopljak, dipl. ing. el.

šifra projekta:

BHT-HAMZICI-2026

razmjera:

1:30

godina / broj crteža:

2026. H-03