


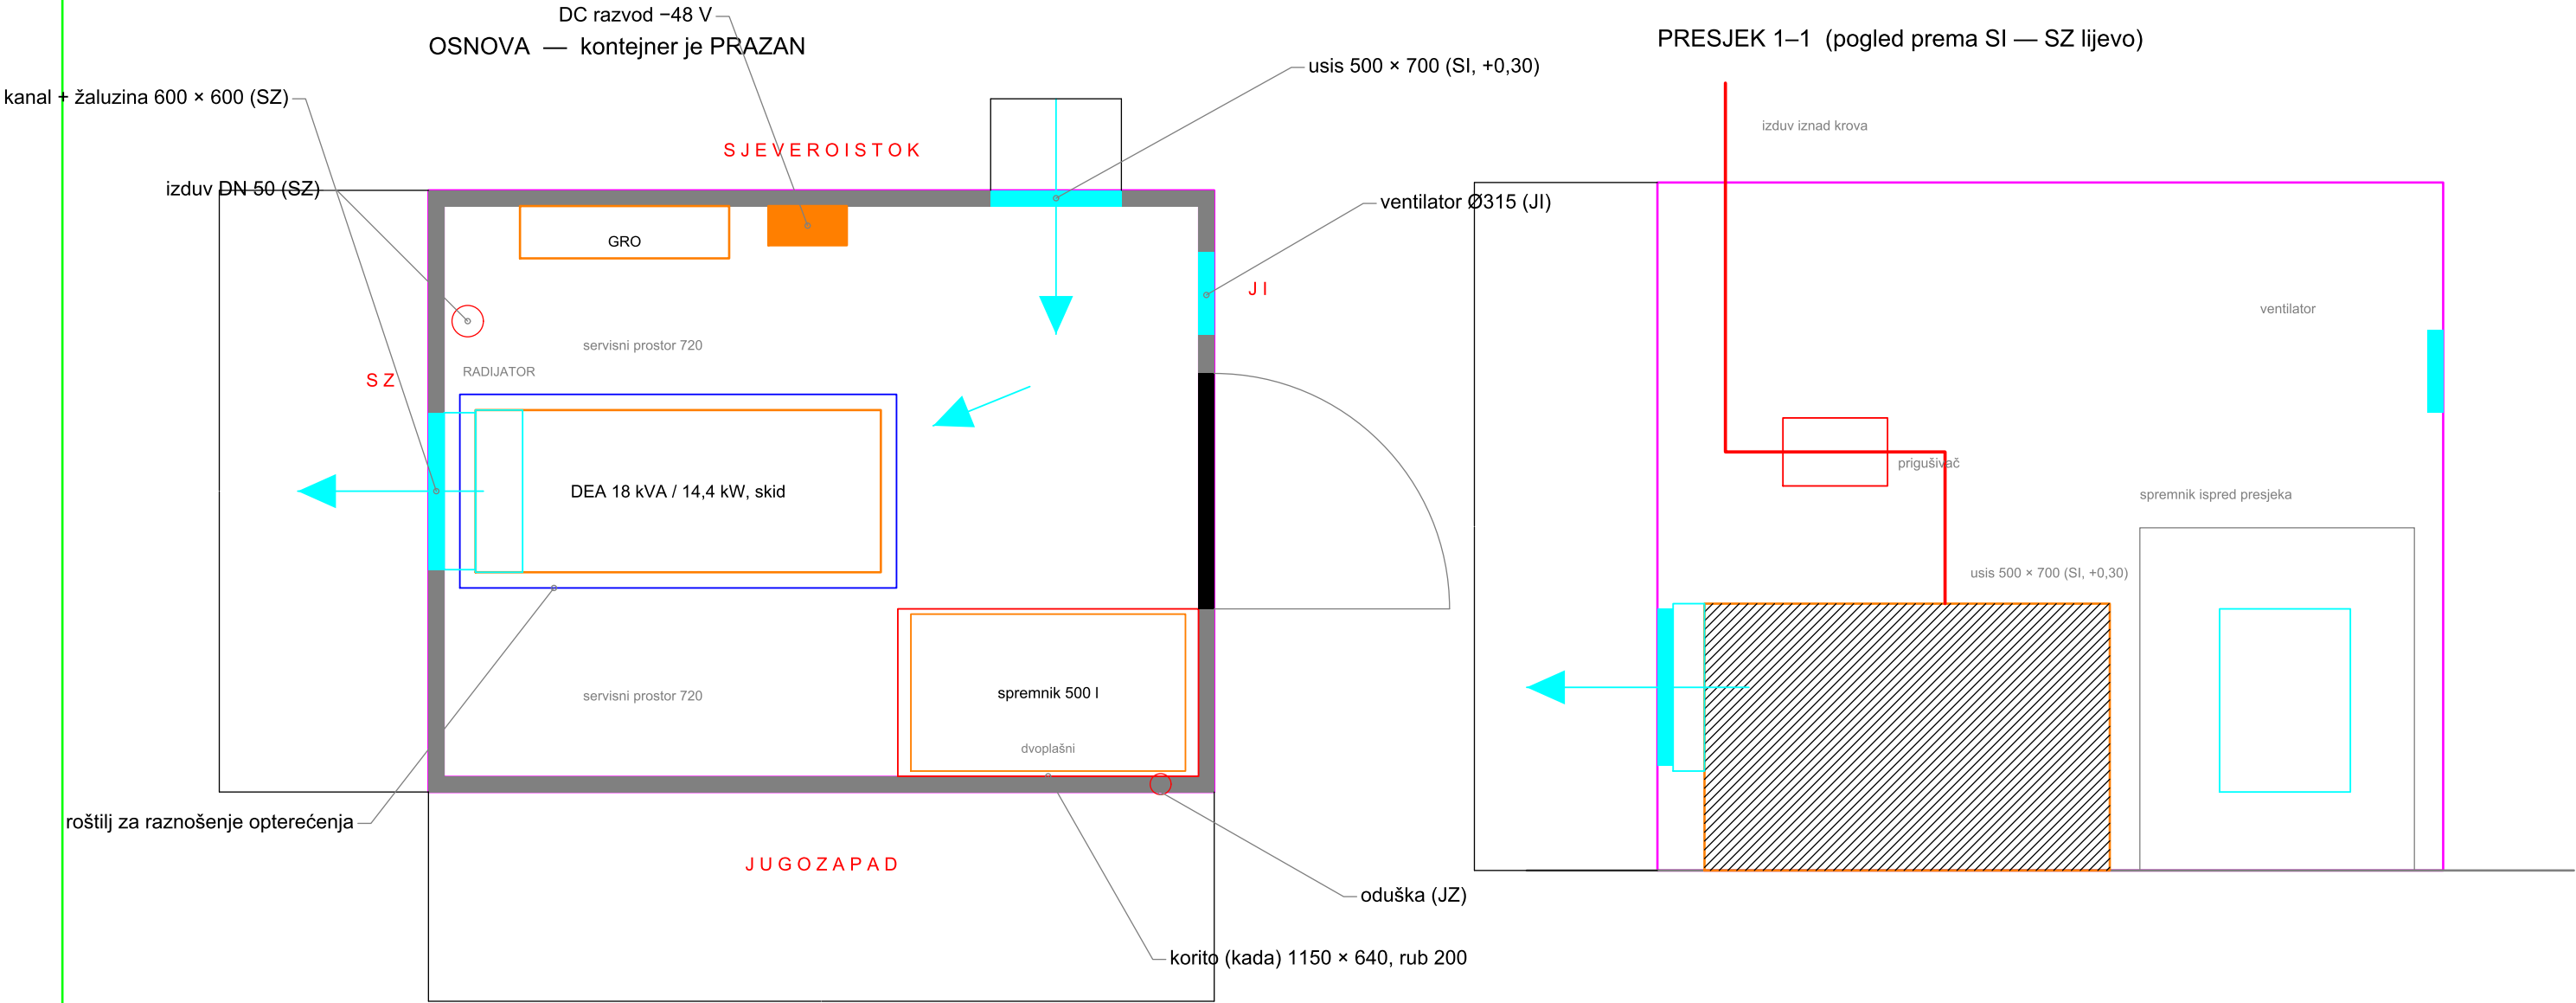

- NAPOMENE:**
- 1 Agregat FG Wilson P18-6 (Skid) ili ekvivalent, 18 kVA / 14,4 kW.
 - 2 RASPORED (obavezujući): usis 500 × 700 SI (+0,30); kanal i žaluzina 600 × 600 te izduv DN 50 SZ; oduška JZ; ventilator JI. ≥3 m između usisa, izduva i oduške.
 - 3 Roštilj za raznošenje opterećenja OBAVEZAN ispod skida i ispod korita.
 - 4 Spremnik je DVOPLAŠNI; ispod njega korito (kada) 1150 × 640, rub 200 mm.
 - 5 SERVISNI PROSTOR (obavezujući): 720 mm JZ, 720 mm SI, 1155 mm JI — ne zauzimati opremom ni skladištenjem.
 - 6 Unos skida 620 mm kroz vrata 900 mm. Kontejner je PRAZAN.
 - 7 DC razvod –48 V (≈300 × 200 × 150) na SI zidu uz GRO: trajni potrošači D1–D6 (E-01).

BH TELECOM d.d. SARAJEVO Izvršna direkcija za tehnologiju i razvoj servisa		
Investitor: BH Telecom d.d. Sarajevo, Franca Lehara 7, Sarajevo		
Objekat: BS SJEDNICA (Bileća) — autonomni hibridni sistem napajanja		
Faza: Tenderska dokumentacija — Prilog III		šifra projekta: BHT-SJEDNICA-2026
Naziv crteža: DEA u postojećem kontejneru — osnova i presjek		razmjera: 1:25
Projektant: Rusmir Skopljak, dipl. ing. el.	ovjerio: Rusmir Skopljak, dipl. ing. el.	godina / broj crteža: 2026. M-01