


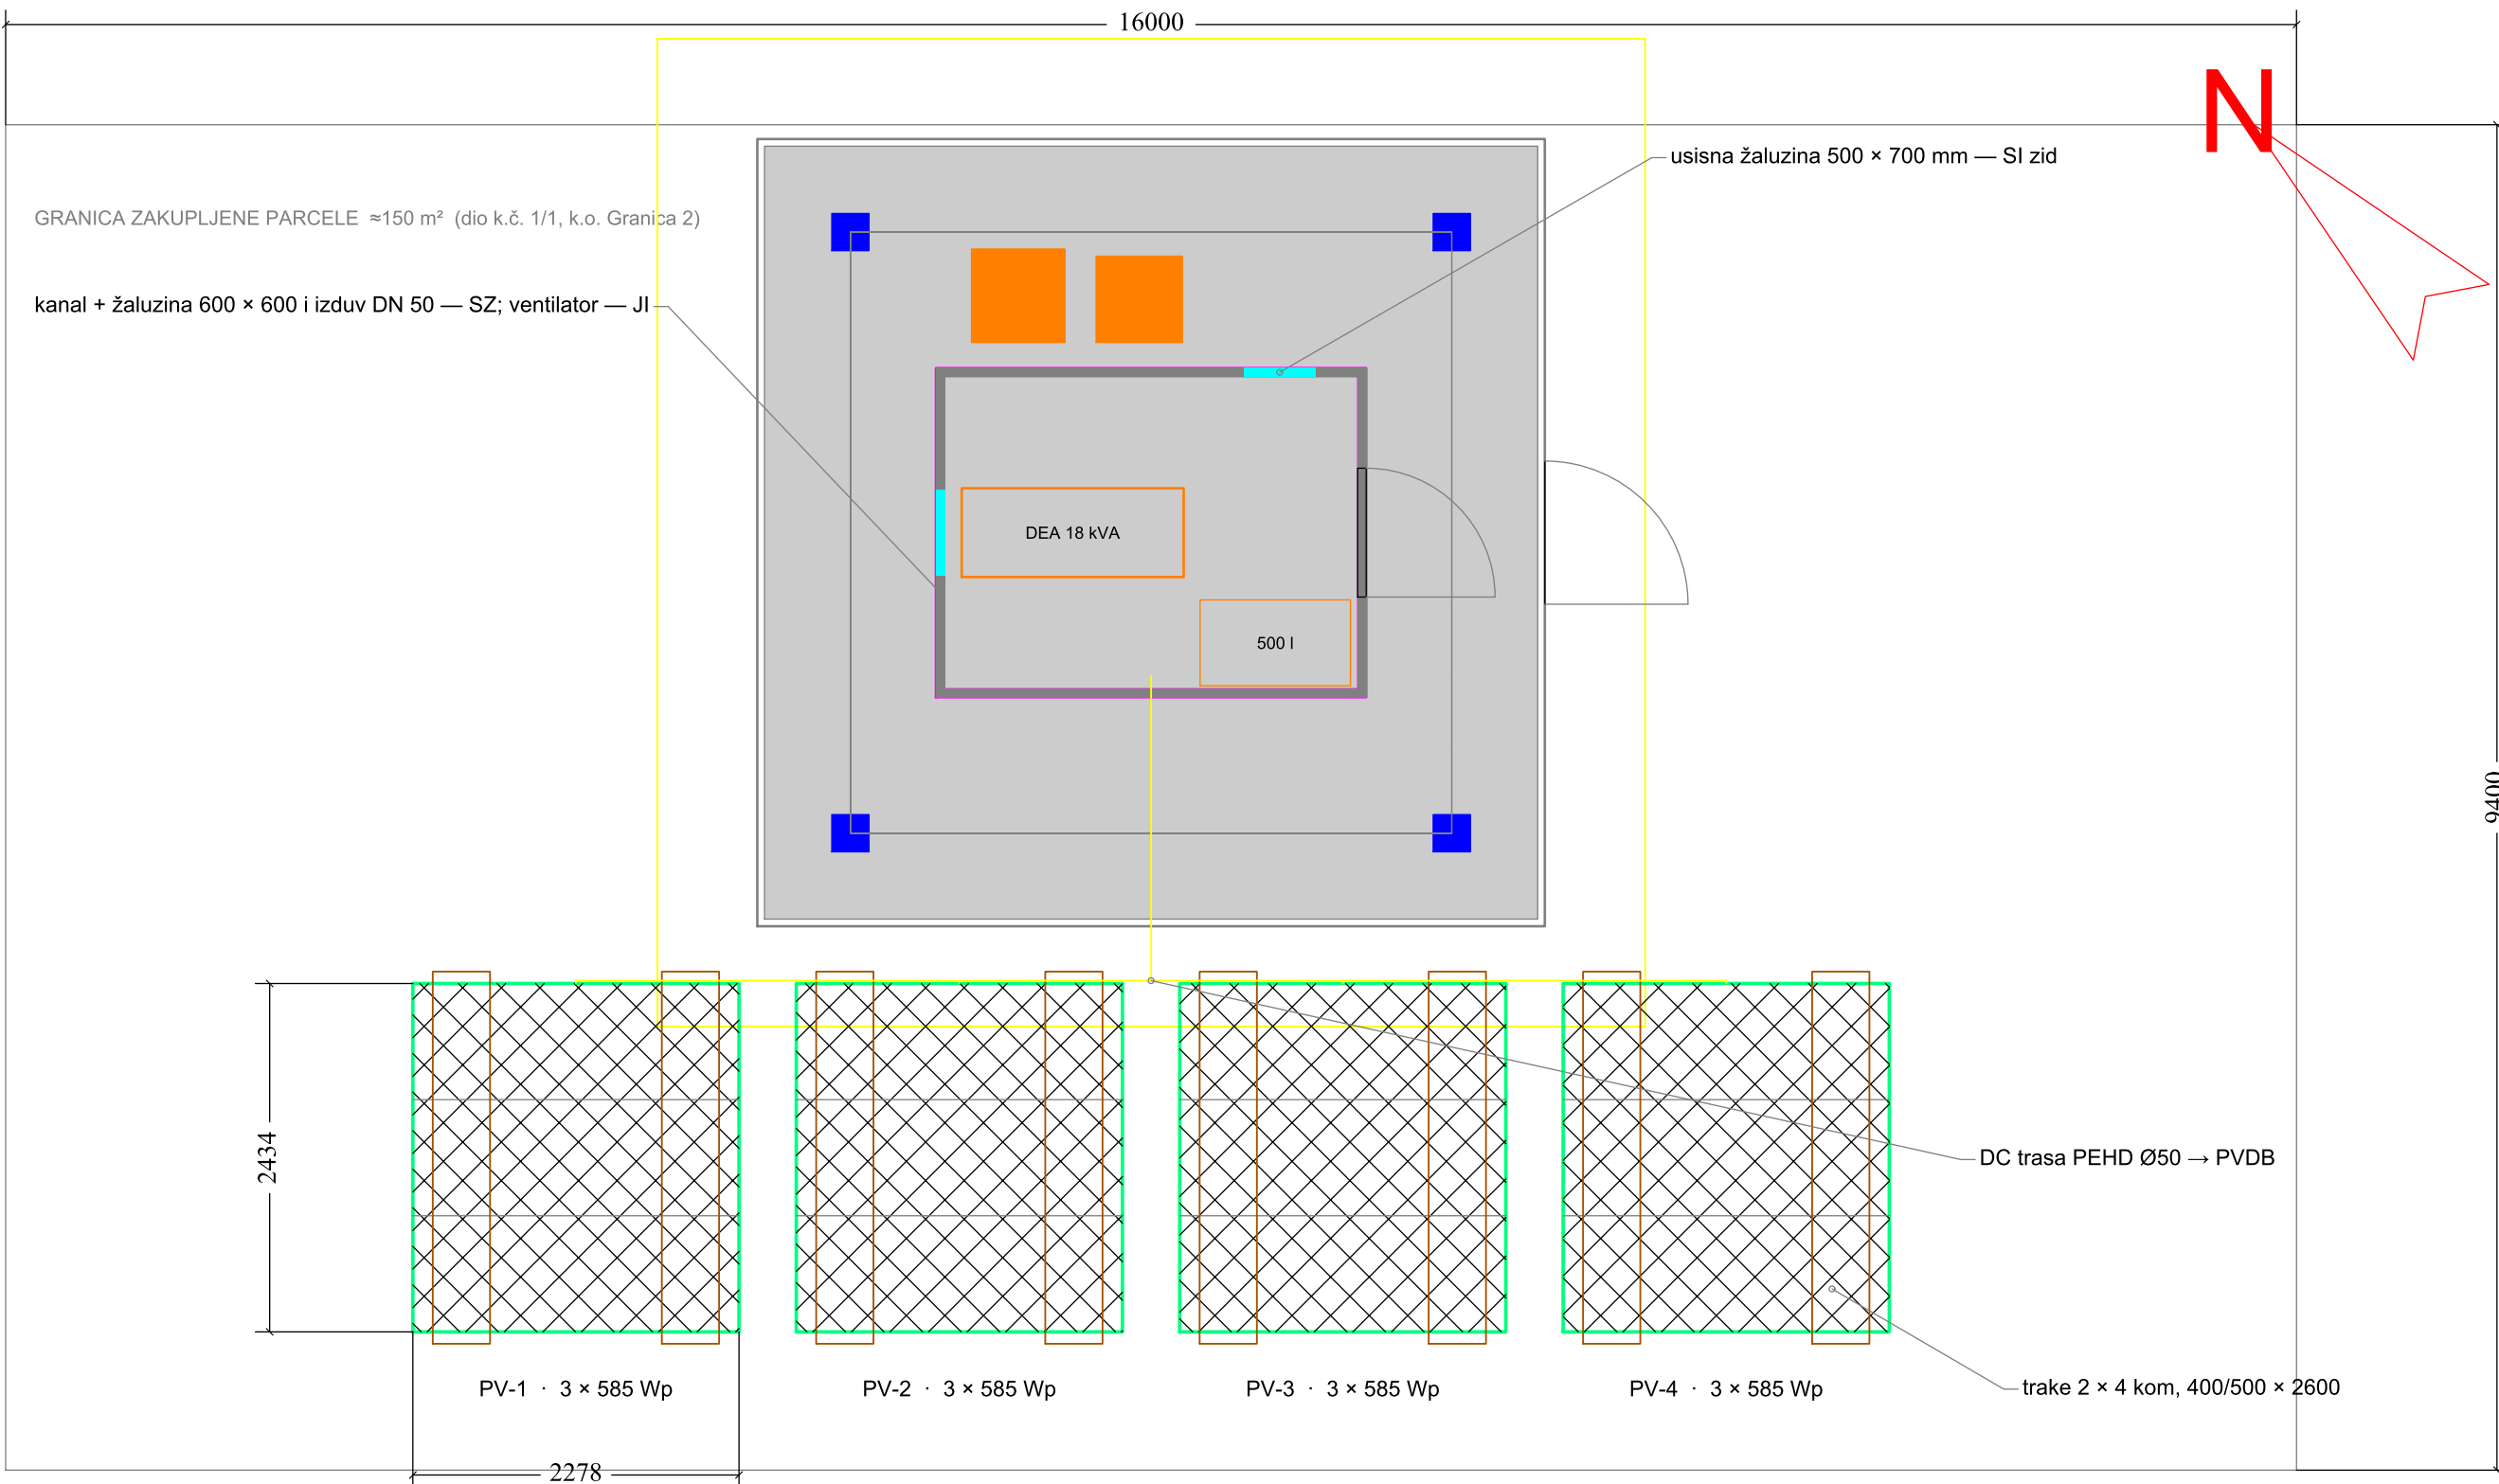

- LEGENDA**
- LOT 1 — nosači FN panela PV-1..PV-4 (po 3 x 585 Wp, položeno, 45°, azimut 225° JZ) — 2 stringa x 6
 - LOT 1 — AB temeljne trake 400/500 x 2600 mm, dubina 900, razmak 1600 mm
 - LOT 1 — DC trasa u PEHD Ø50 do PVDB
 - LOT 2 — DEA 18 kVA u skid izvedbi i dvoplašni spremnik 500 l
 - LOT 2 — usisna žaluzina (SI); kanal, žaluzina i izduv (SZ); ventilator (JI)

NAPOMENA — PRORAČUNSKO OPTEREĆENJE:
Vjetar qp ≥ 1,20 kN/m² — CUSTOM IZRADA nosača; ovjereni statički proračun dostavlja ponuđač (Prilog II, 1.3).
Temelji IZVAN ograde; gornja ivica panela +2,93 m, donja +0,50 m.



BH TELECOM d.d. SARAJEVO
Izvršna direkcija za tehnologiju i razvoj servisa

Investitor:
BH Telecom d.d. Sarajevo, Franca Lehara 7, Sarajevo

Objekat:
BS SJEDNICA (Bileća) — autonomni hibridni sistem napajanja

Faza:
Tenderska dokumentacija — Prilog III

Naziv crteža:
Situacija — BUDUĆE STANJE (LOT 1 + LOT 2)

Projektant:
Rusmir Skopljak, dipl. ing. el.

ovjerio:
Rusmir Skopljak, dipl. ing. el.

šifra projekta:
BHT-SJEDNICA-2026

razmjera:
1:50

godina / broj crteža:
2026. S-02