


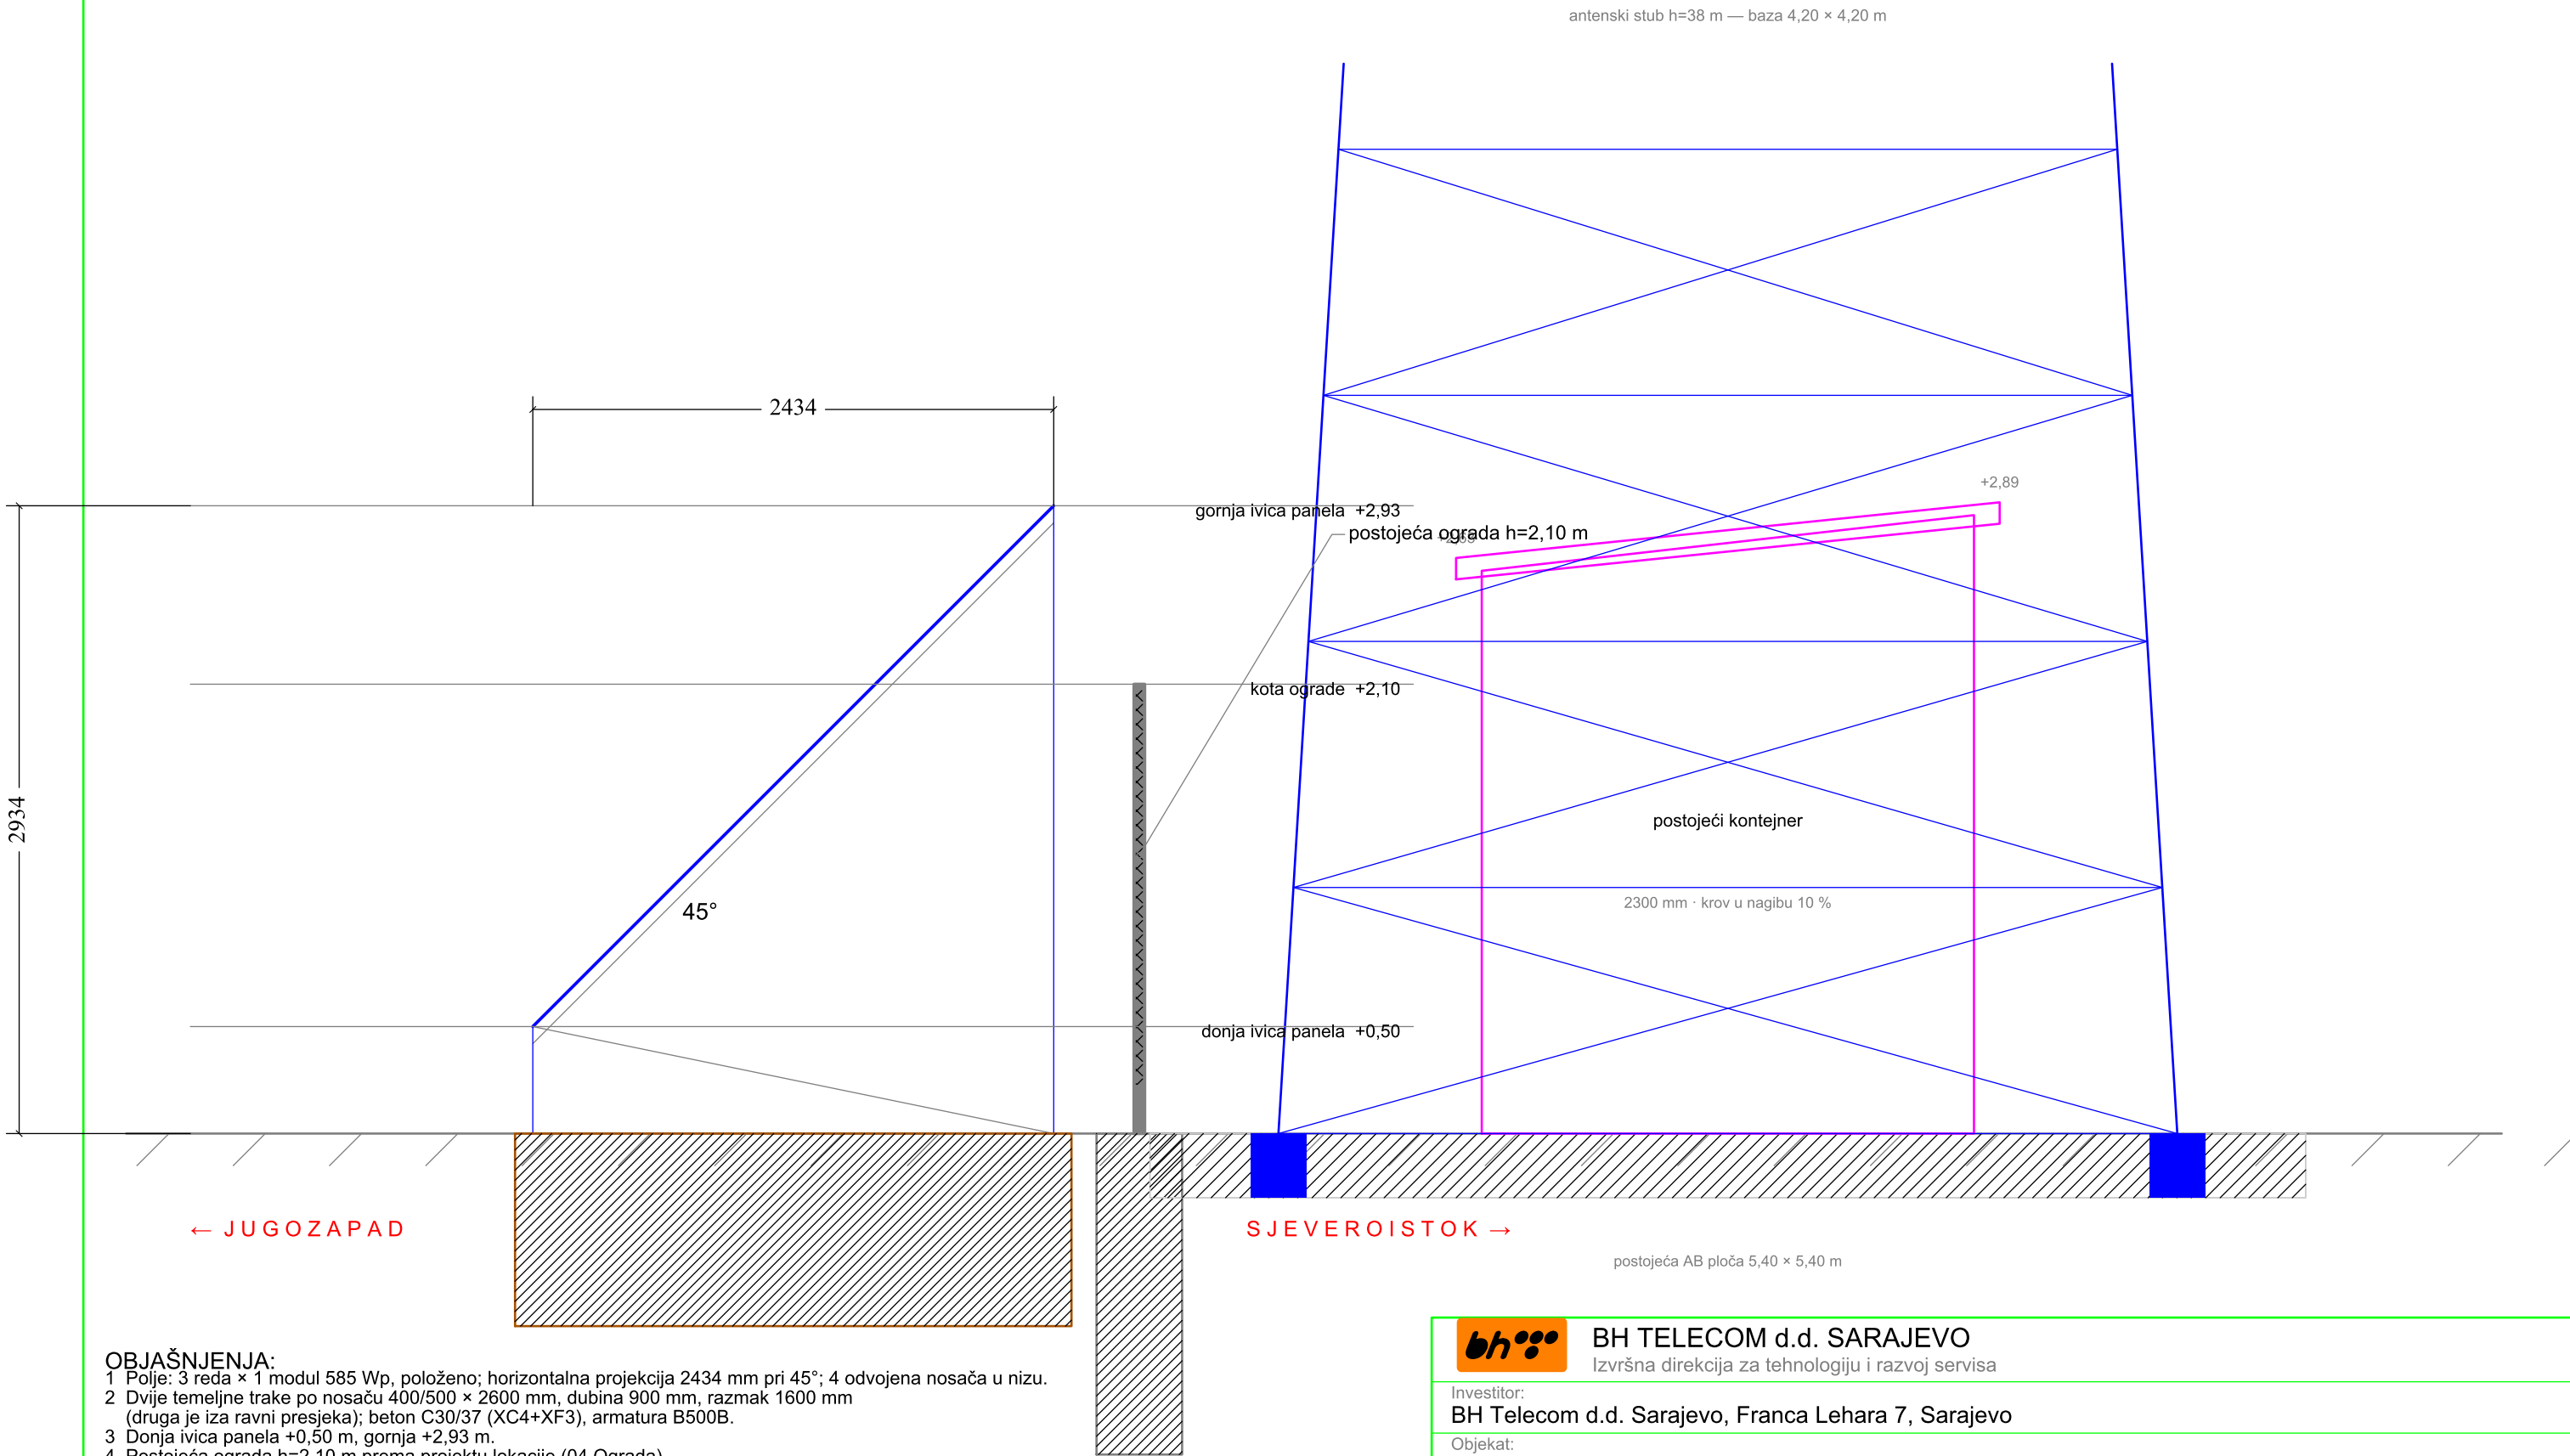

OBJAŠNJENJA:

- Polje: 3 reda × 1 modul 585 Wp, položeno; horizontalna projekcija 2434 mm pri 45°; 4 odvojena nosača u nizu.
- Dvije temeljne trake po nosaču 400/500 × 2600 mm, dubina 900 mm, razmak 1600 mm (druga je iza ravni presjeka); beton C30/37 (XC4+XF3), armatura B500B.
- Donja ivica panela +0,50 m, gornja +2,93 m.
- Postojeća ograda h=2,10 m prema projektu lokacije (04 Ograda).



BH TELECOM d.d. SARAJEVO

Izvršna direkcija za tehnologiju i razvoj servisa

Investitor:

BH Telecom d.d. Sarajevo, Franca Lehara 7, Sarajevo

Objekat:

BS SJEDNICA (Bileća) — autonomni hibridni sistem napajanja

Faza:

Tenderska dokumentacija — Prilog III

Naziv crteža:

Presjek A—A kroz nosač FN panela

Projektant:

Rusmir Skopljak, dipl. ing. el.

ovjerio:

Rusmir Skopljak, dipl. ing. el.

šifra projekta:

BHT-SJEDNICA-2026

razmjera:

1:30

godina / broj crteža:

2026. S-03