



OSNOVA — kontejner je PRAZAN; klima-uređaj Stulz se demontira

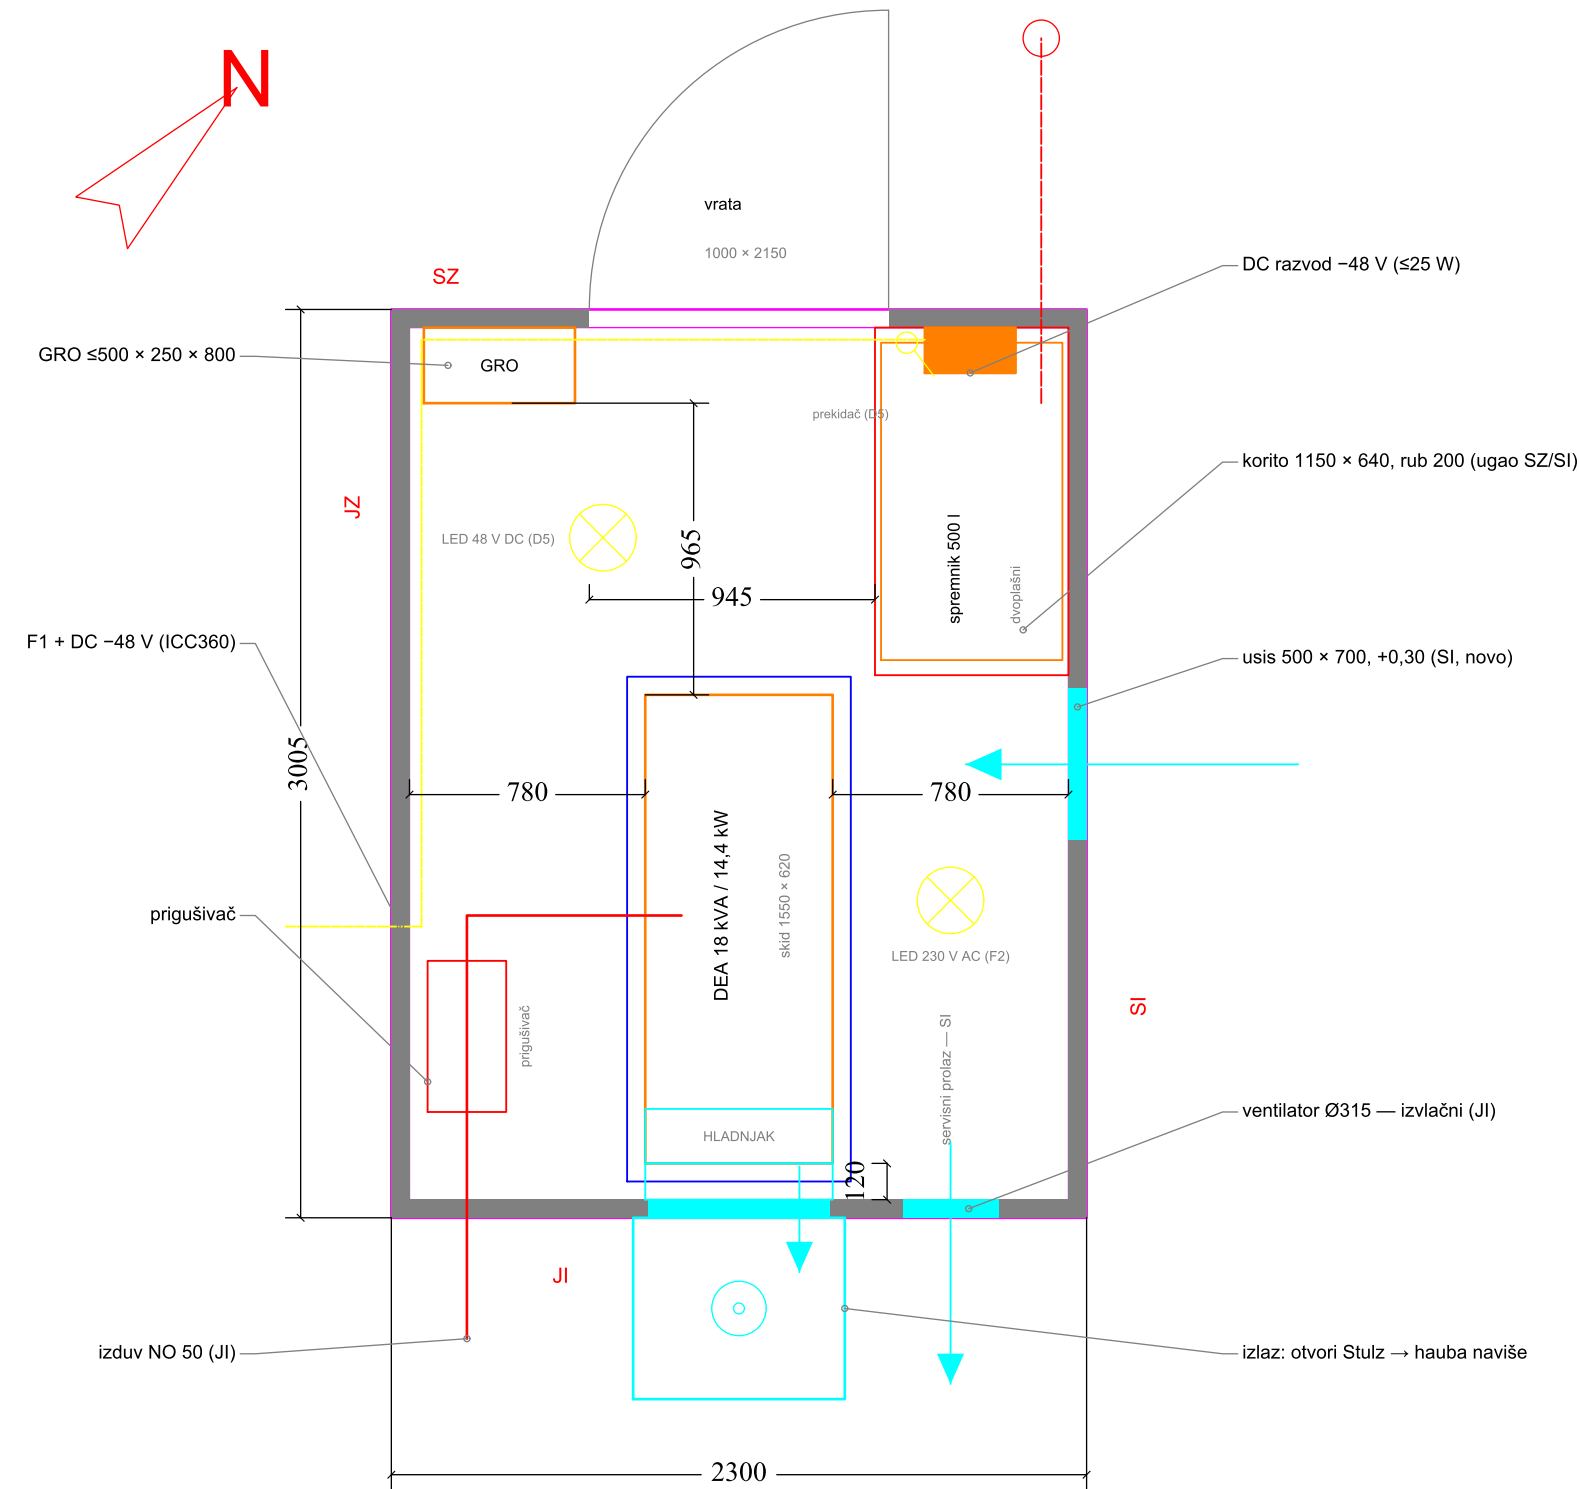

- NAPOMENE:**
- 1 DEA FG Wilson P18-6 (Skid) ili ekv., 18 kVA / 14,4 kW, pobuda PMG ili AREP/AUX; os SZ–JI u sredini, hladnjak JI.
 - 2 RASPORED (obavezujući): Stulz je u sredini JUGOISTOČNOG (JI) zida — izlaz zraka hladnjaka kroz njegove otvore, spojene/proširene na ≥0,36 m² bruto (npr. 600 x 600), limeni plenum; višak otvora zatvoriti panelom 60 mm.
 - 3 Vani hauba 700 x 600, zatvorenih bočnih strana, rešetka na vrhu (+1,30): topli zrak ide NAVIŠE.
 - 4 Usis 500 x 700 na SI zidu (+0,30, novo, uz alternator). Izduv NO 50 iz JZ prolaza kroz JI zid na ≈+2,30 m, ispod platforme stuba; prigušivač, hvatač iskri, kapa; završetak ≥0,40 m od zida (3,25 m od usisa).
 - 5 GRO ≤500 x 250 x 800 mm na SZ zidu, jugozapadno od vrata (zid 595 mm); roštilj OBAVEZAN pod skidom i koritom.
 - 6 Spremnik 500 l DVOPLAŠNI u koritu 1150 x 640, rub 200 mm, u SJEVERNOM uglu (SZ x SI zid).
 - 7 SERVIS: prolazi JZ / SI po 780 / 780 mm, 965 mm do GRO; od vrata do korita 945 mm slobodno.
 - 8 Unos: skid 620 mm kroz vrata svijetle širine 990 mm, pravo po osi; najprije agregat, zatim spremnik.
 - 9 Ventilator Ø315 na JI zidu gore je IZVLAČNI (EC 48 V DC, D4). ICC360-HA1-C1 i MTS vani na JZ strani (H-02).
 - 10 Odušak spremnika kroz SZ zid — principijelno: 4,73 m od izduva, 3,23 m od usisa; konačno prema elaboratu ŽOP.
 - 11 DC razvod -48 V ≈300 x 200 x 150 istočno od vrata: rasvjeta prepreke, vatrodajava, punjač aku., ventilator, predgrijač, D5.
 - 12 Rasvjeta: LED 230 V AC iz GRO (F2, radi dok DEA radi) i LED 48 V DC (D5) sa prekidačem uz vrata.
 - 13 Raspored je principijelan — Ponuđač ga potvrđuje na licu mjesta (mjere otvora Stulz, servisne tačke agregata).

PRESJEK 1–1 (os agregata — pogled prema SI, SZ lijevo)

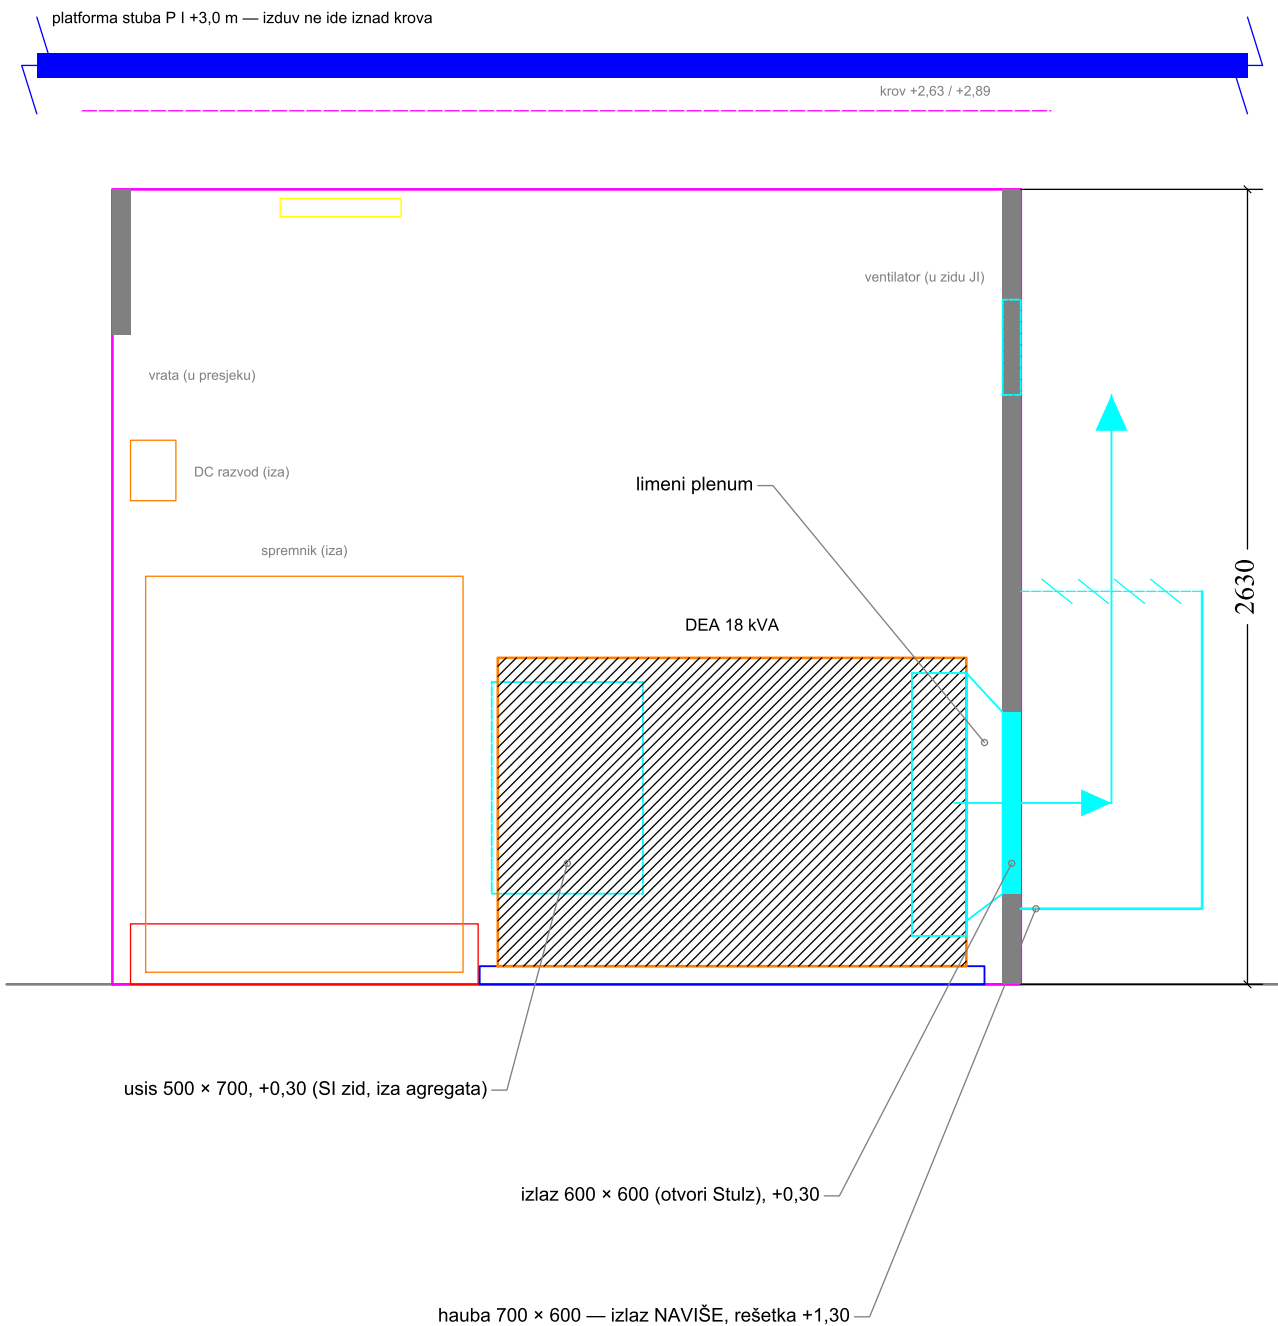

BH TELECOM d.d. SARAJEVO

Izvršna direkcija za tehnologiju i razvoj servisa

Investitor:

BH Telecom d.d. Sarajevo, Franca Lehara 7, Sarajevo

Objekat:

BS HAMZIĆI (ČITLUK) — autonomni hibridni sistem napajanja

Faza:

Tenderska dokumentacija — Prilog III

Naziv crteža:

Agregat u kontejneru — osnova i presjek 1–1

Projektant:

Rusmir Skopljak, dipl. ing. el.

ovjerio:

Rusmir Skopljak, dipl. ing. el.

šifra projekta:

BHT-HAMZICI-2026

razmjera:

1:25

godina / broj crteža:

2026. H-04