
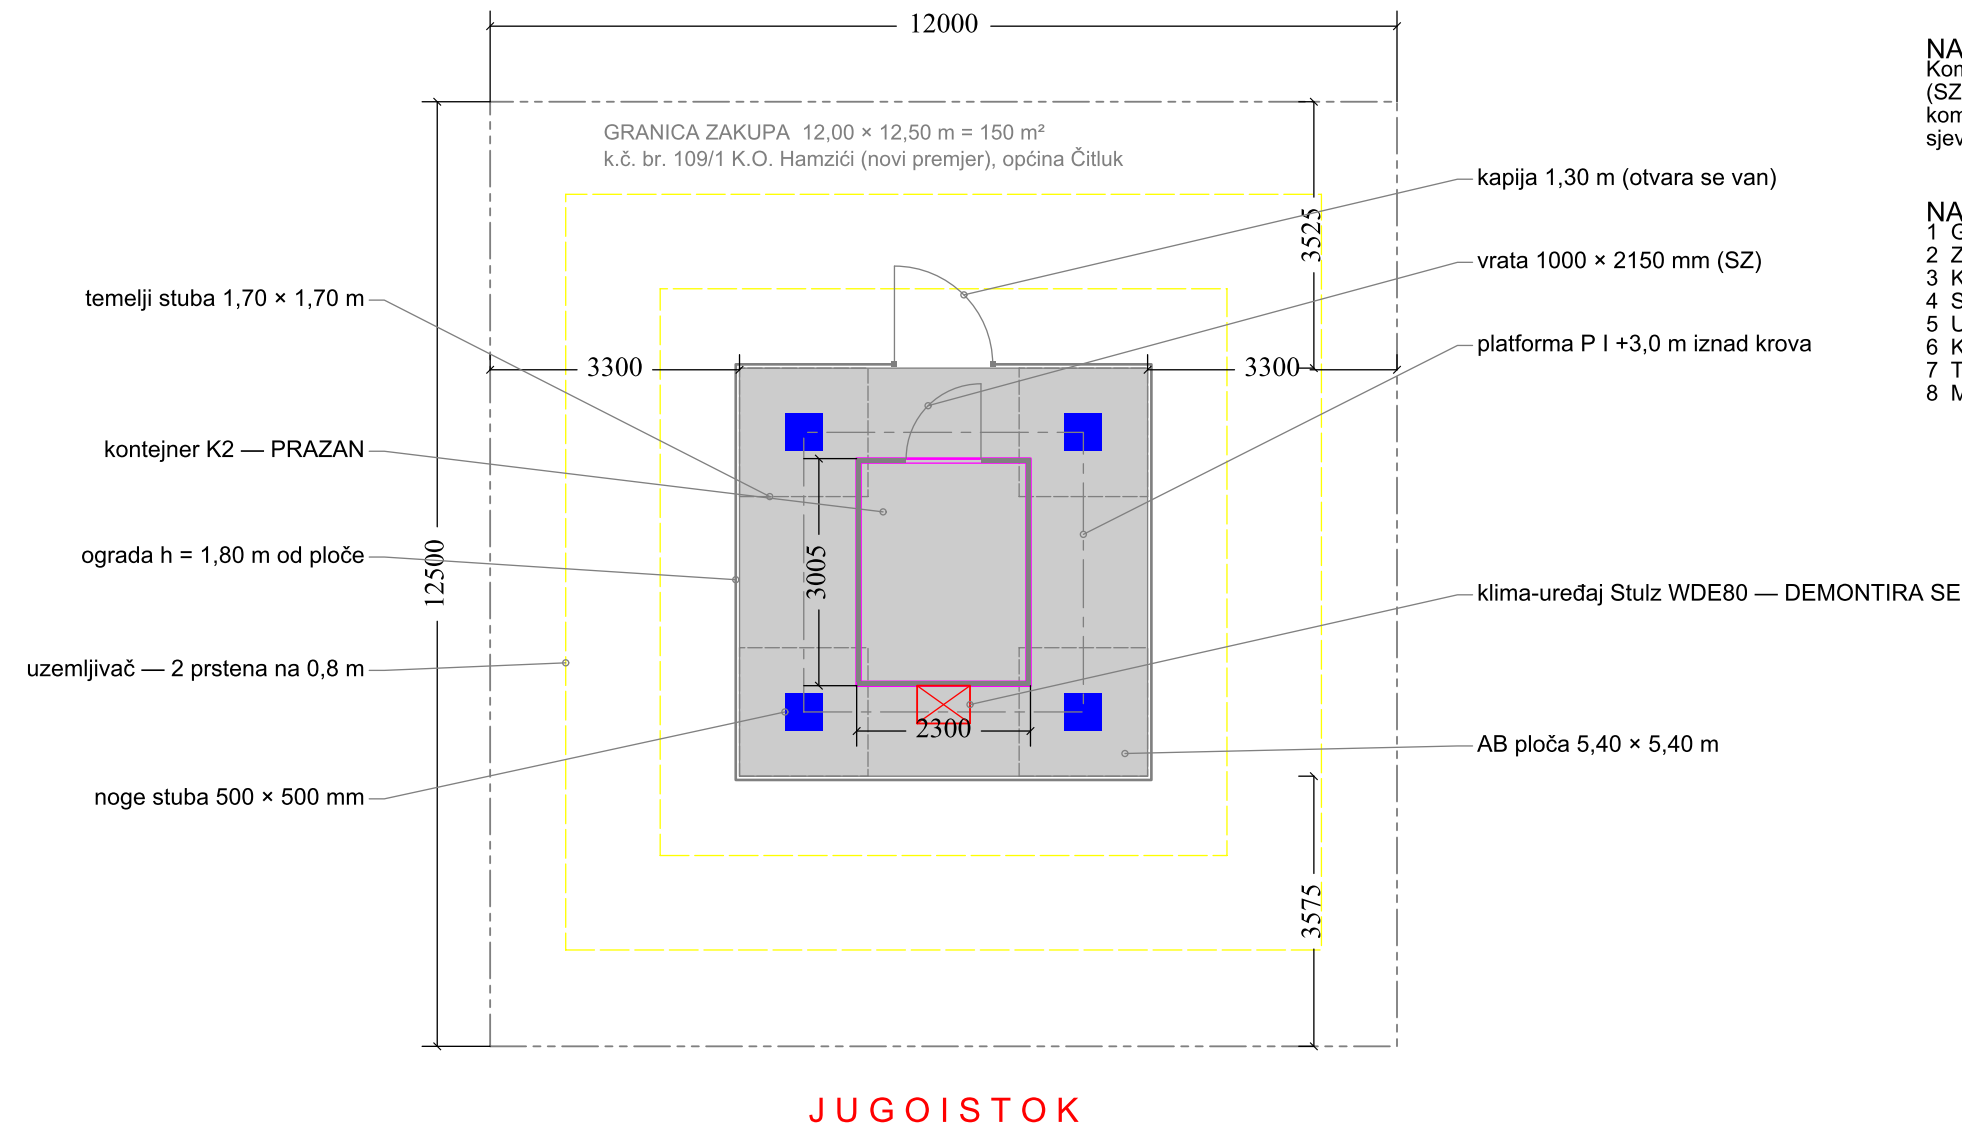


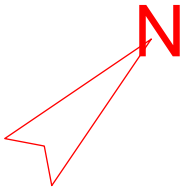

**NAPOMENA — ORIJENTACIJA:**  
Kompleks je zakrenut 45°: vrata kontejnera i kapija gledaju na SJEVEROZAPAD (SZ), klima-uređaj Stulz na JI, FN polje na JZ. Crtež je pravougaon na kompleks (gore SZ, desno SI, dolje JI, lijevo JZ); strelica pokazuje pravi sjever. Orijentaciju potvrđuje Ponuđač obilaskom lokacije.

**NAPOMENE:**  
1 Geometrija iz ovjerenog projekta lokacije GP-BS-10472-291 (2017).  
2 Zakup 12,00 x 12,50 m = 150 m², k.č. br. 109/1, općina Čitluk.  
3 Kontejner je PRAZAN; u sredini JI zida je Stulz WDE80 (≈700 x 500 x 2200).  
4 Stub h = 32 m; platforma P I (+3,0 m) je iznad krova (+2,63 / +2,89 m).  
5 Uzemljivač FeZn 25x4: prsten u temeljima stopa i dva prstena na 0,8 m.  
6 Kapija se otvara prema van; krilo 1,30 m.  
7 Teren uz ploču je na -0,20 m; ograda 1,80 m iznad ploče, 2,00 m iznad terena.  
8 Mjere uređaja i otvora uzimaju se na obaveznom obilasku lokacije.

## LEGENDA

- postojeća ograda 5,50 x 5,50 m, h = 1,80 m od ploče (2,00 m od terena) — kapija 1,30 m na SZ strani
- postojeća AB ploča 5,40 x 5,40 m
- postojeći kontejner K2 2300 x 3005 mm — vrata na SZ strani
- noge rešetkastog stuba h = 32 m, baza 3,70 x 3,70 m
- klima-uređaj Stulz WDE80 (JI zid, u sredini) — demontira se
- postojeći uzemljivač FeZn 25x4 mm (isprekidano — u tlu)



|                                                                                         |                                             |                                     |
|-----------------------------------------------------------------------------------------|---------------------------------------------|-------------------------------------|
| <b>bh</b> BH TELECOM d.d. SARAJEVO<br>Izvršna direkcija za tehnologiju i razvoj servisa |                                             |                                     |
| Investitor:<br>BH Telecom d.d. Sarajevo, Franca Lehara 7, Sarajevo                      |                                             |                                     |
| Objekat:<br>BS HAMZIĆI (ČITLUK) — autonomni hibridni sistem napajanja                   |                                             |                                     |
| Faza:<br>Tenderska dokumentacija — Prilog III                                           |                                             | šifra projekta:<br>BHT-HAMZICI-2026 |
| Naziv crteža:<br><b>Situacija — POSTOJEĆE STANJE</b>                                    |                                             | razmjera:<br><b>1:100</b>           |
| Projektant:<br>Rusmir Skopljak, dipl. ing. el.                                          | ovjerio:<br>Rusmir Skopljak, dipl. ing. el. | godina / broj crteža:<br>2026. H-01 |