

TENDERSKA DOKUMENTACIJA ZA NABAVKU

INFRASTRUKTURA I INSTALACIJA OPREME ZA AUTONOMNI HIBRIDNI SISTEM NAPAJANJA SJEDNICA, BILEĆA I HAMZIĆI, ČITLUK (LOT 1 i 2)

PROVOĐENJEM NABAVKE PUTEM PREGOVARAČKOG POSTUPKA NABAVKE SA OBJAVOM
OBAVJEŠTENJA

PRILOG III

SITUACIJE, DISPOZICIJA OPREME I GRAFIČKI PRILOZI (NACRTI)

Lokacije

A. BS Sjednica, Bileća — 42,9448° N · 18,3236° E · 1076 m n.v.

B. BS Hamzići, Čitluk — 43,2880° N · 17,6248° E · 493 m n.v.

Sarajevo, septembar 2026. godine

A. BS SJEDNICA (BILEĆA)



BH TELECOM d.d. SARAJEVO | BS SJEDNICA (BILEĆA) | PRILOG III


Fotografija postojećeg stanja lokacije


Antenski stub, kontejner, ograda — stanje prije izvođenja radova

Crtež br.
INFO-01

1. OPŠTI PODACI O LOKACIJI

Investitor	BH Telecom d.d. Sarajevo, Franca Lehara 7, 71000 Sarajevo
Objekat	Bazna stanica SJEDNICA
Općina	Bileća
Koordinate	42,9448° N, 18,3236° E
Nadmorska visina	1076 m
Zakupljena površina	≈150 m ² (dio k.č. 1/1, k.o. Granica 2)
Betonski temelj	5,40 × 5,40 m, sa metalnom ogradom visine 2,10 m
Antenski stub	Rešetkasta izvedba, visina 38 m; baza 4,20 m (dno) / 1,20 m (vrh)
Priključak na EES	Nema
TK oprema	Huawei RRU (3 kom) + BBU/MPLS, -48 VDC
Snaga potrošača	1.180 W nazivno / 1.330 W maksimalno
Sistem napajanja	Hibridni: FN moduli (primarni) + LFP baterije + DEA (rezervni)
FN konfiguracija	12 × iPV585-M2A (7,02 kWp) na 4 nosača po 3 modula (položeno), nagib 45°, azimut 225° (JZ)
DEA	18 kVA / 14,4 kW, skid u kontejneru; ulaz ispravljača ≤9,5 kW
Spremnik goriva	Dvoplašni, 500 l, sa nivo sondom i detekcijom curenja
Orijentacija	Vrata JI, hladnjak DEA SZ, FN polje JZ; ormari ICC360 i MTS SI
Očekivani rad agregata	300~360 h/god

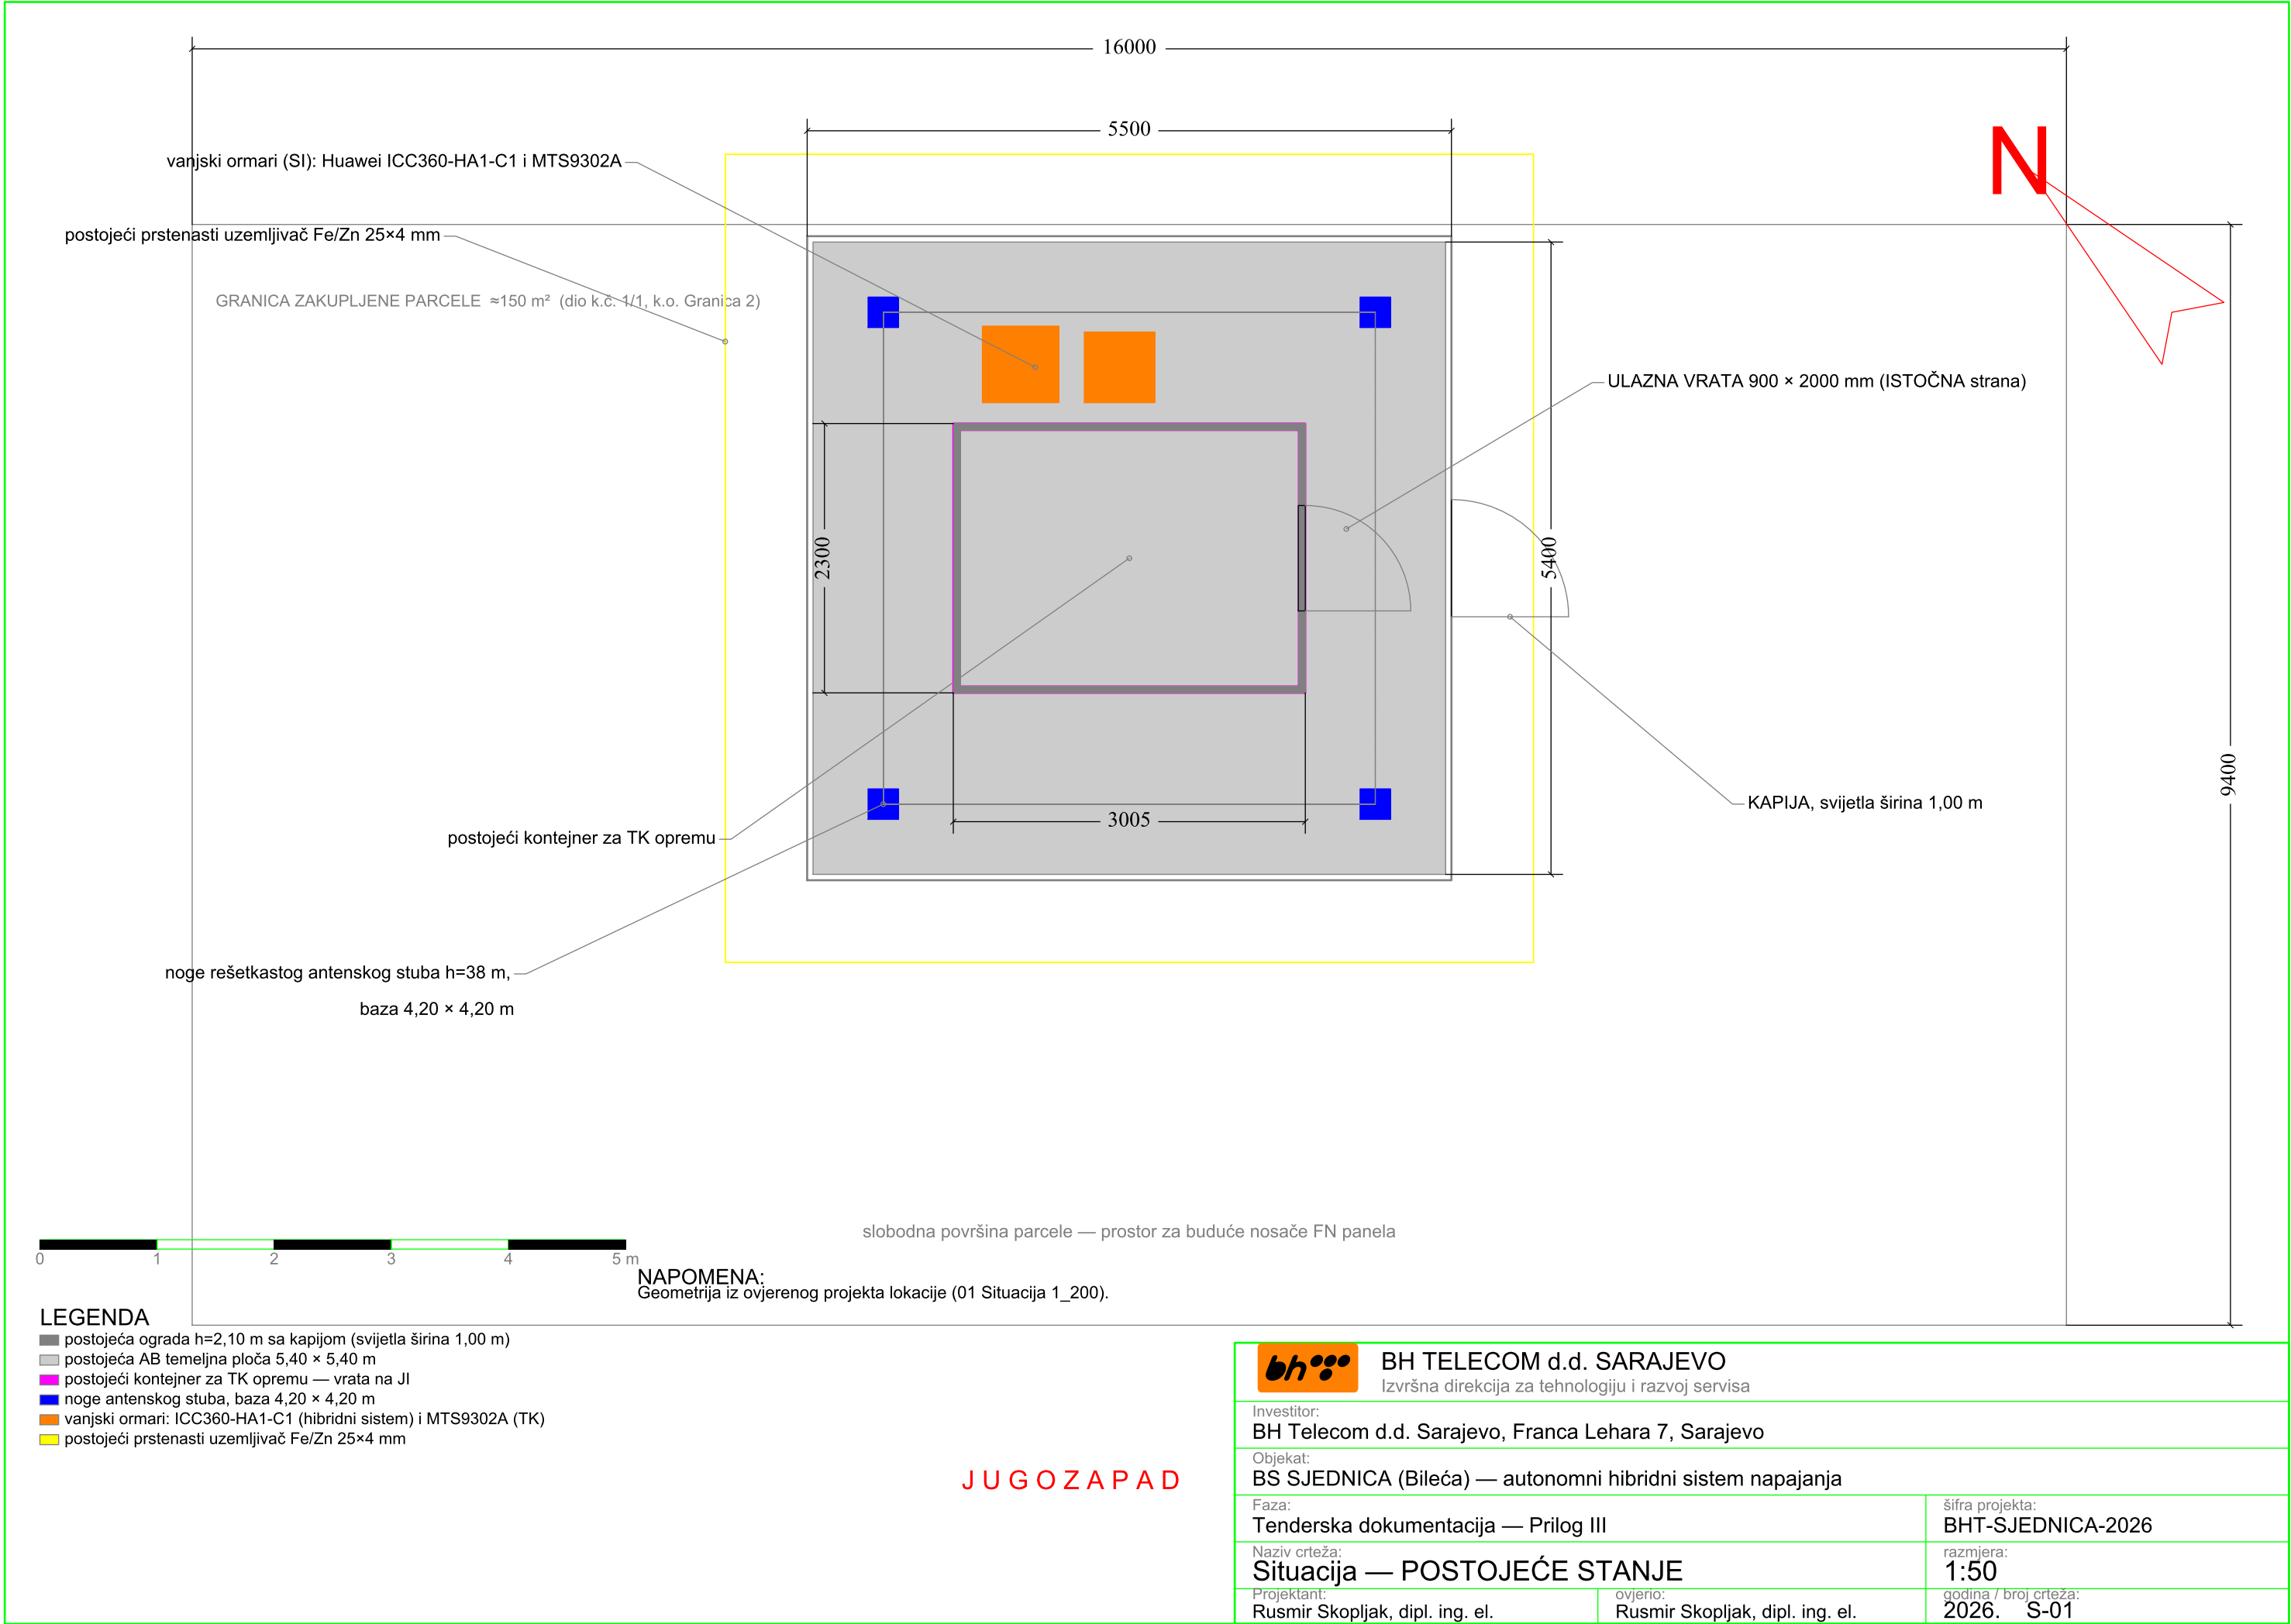

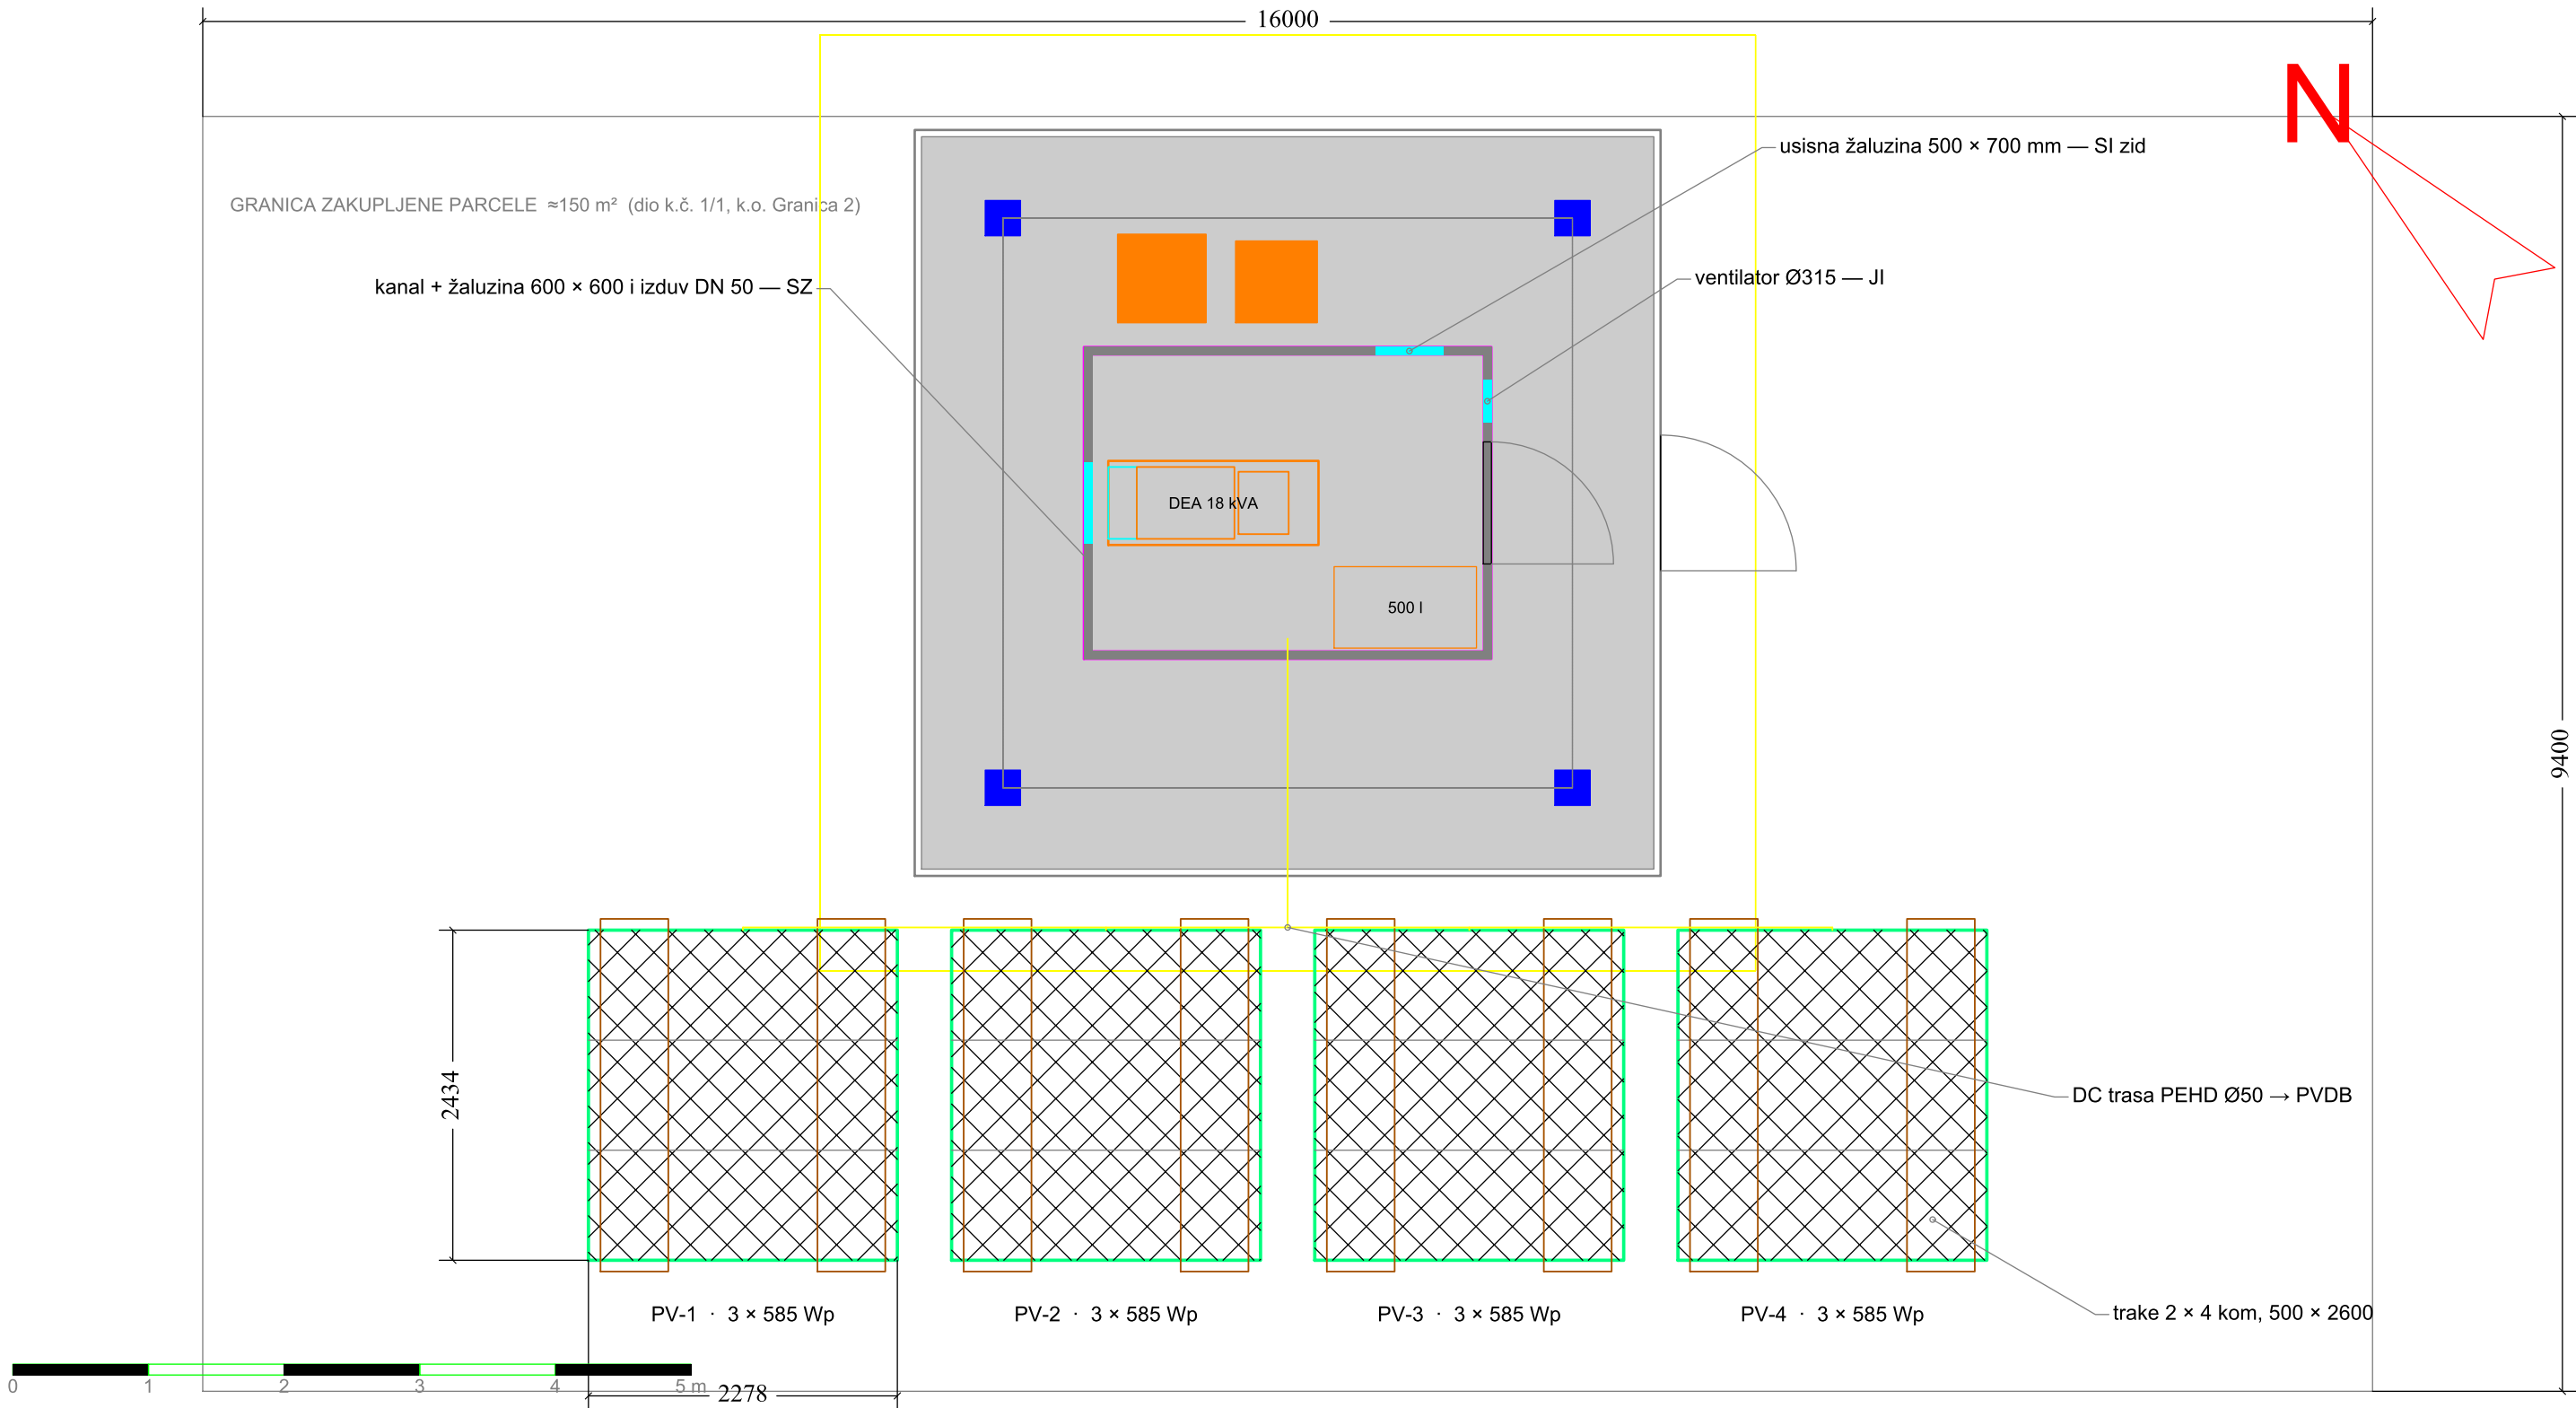

LEGENDA

- LOT 1 — nosači FN panela PV-1..PV-4 (po 3 × 585 Wp, položeno, 45°, azimut 225° JZ) — 2 stringa × 6
- LOT 1 — AB temeljne trake 500 × 2600 mm, dubina 900, razmak 1600 mm
- LOT 1 — DC trasa u PEHD Ø50 do PVDB
- LOT 2 — DEA 18 kVA u skid izvedbi i dvoplašni spremnik 500 l
- LOT 2 — usisna žaluzina (SI); kanal, žaluzina i izduv (SZ); ventilator (JI)

NAPOMENE:

- Nosač i temelji — tehničko rješenje i statički proračun Ponuđača.
- Temelji IZVAN ograde; ivica panela +0,50 / +2,93 m.
- Zahtjevi: Prilog I, Tačke 3 i 4.



BH TELECOM d.d. SARAJEVO

Izvršna direkcija za tehnologiju i razvoj servisa

Investitor:

BH Telecom d.d. Sarajevo, Franca Lehara 7, Sarajevo

Objekat:

BS SJEDNICA (Bileća) — autonomni hibridni sistem napajanja

Faza:

Tenderska dokumentacija — Prilog III

Naziv crteža:

Situacija — BUDUĆE STANJE (LOT 1 + LOT 2)

Projektant:

Rusmir Skopljak, dipl. ing. el.

ovjerio:

Rusmir Skopljak, dipl. ing. el.

šifra projekta:


BHT-SJEDNICA-2026

razmjera:

1:50

godina / broj crteža:


2026. S-02

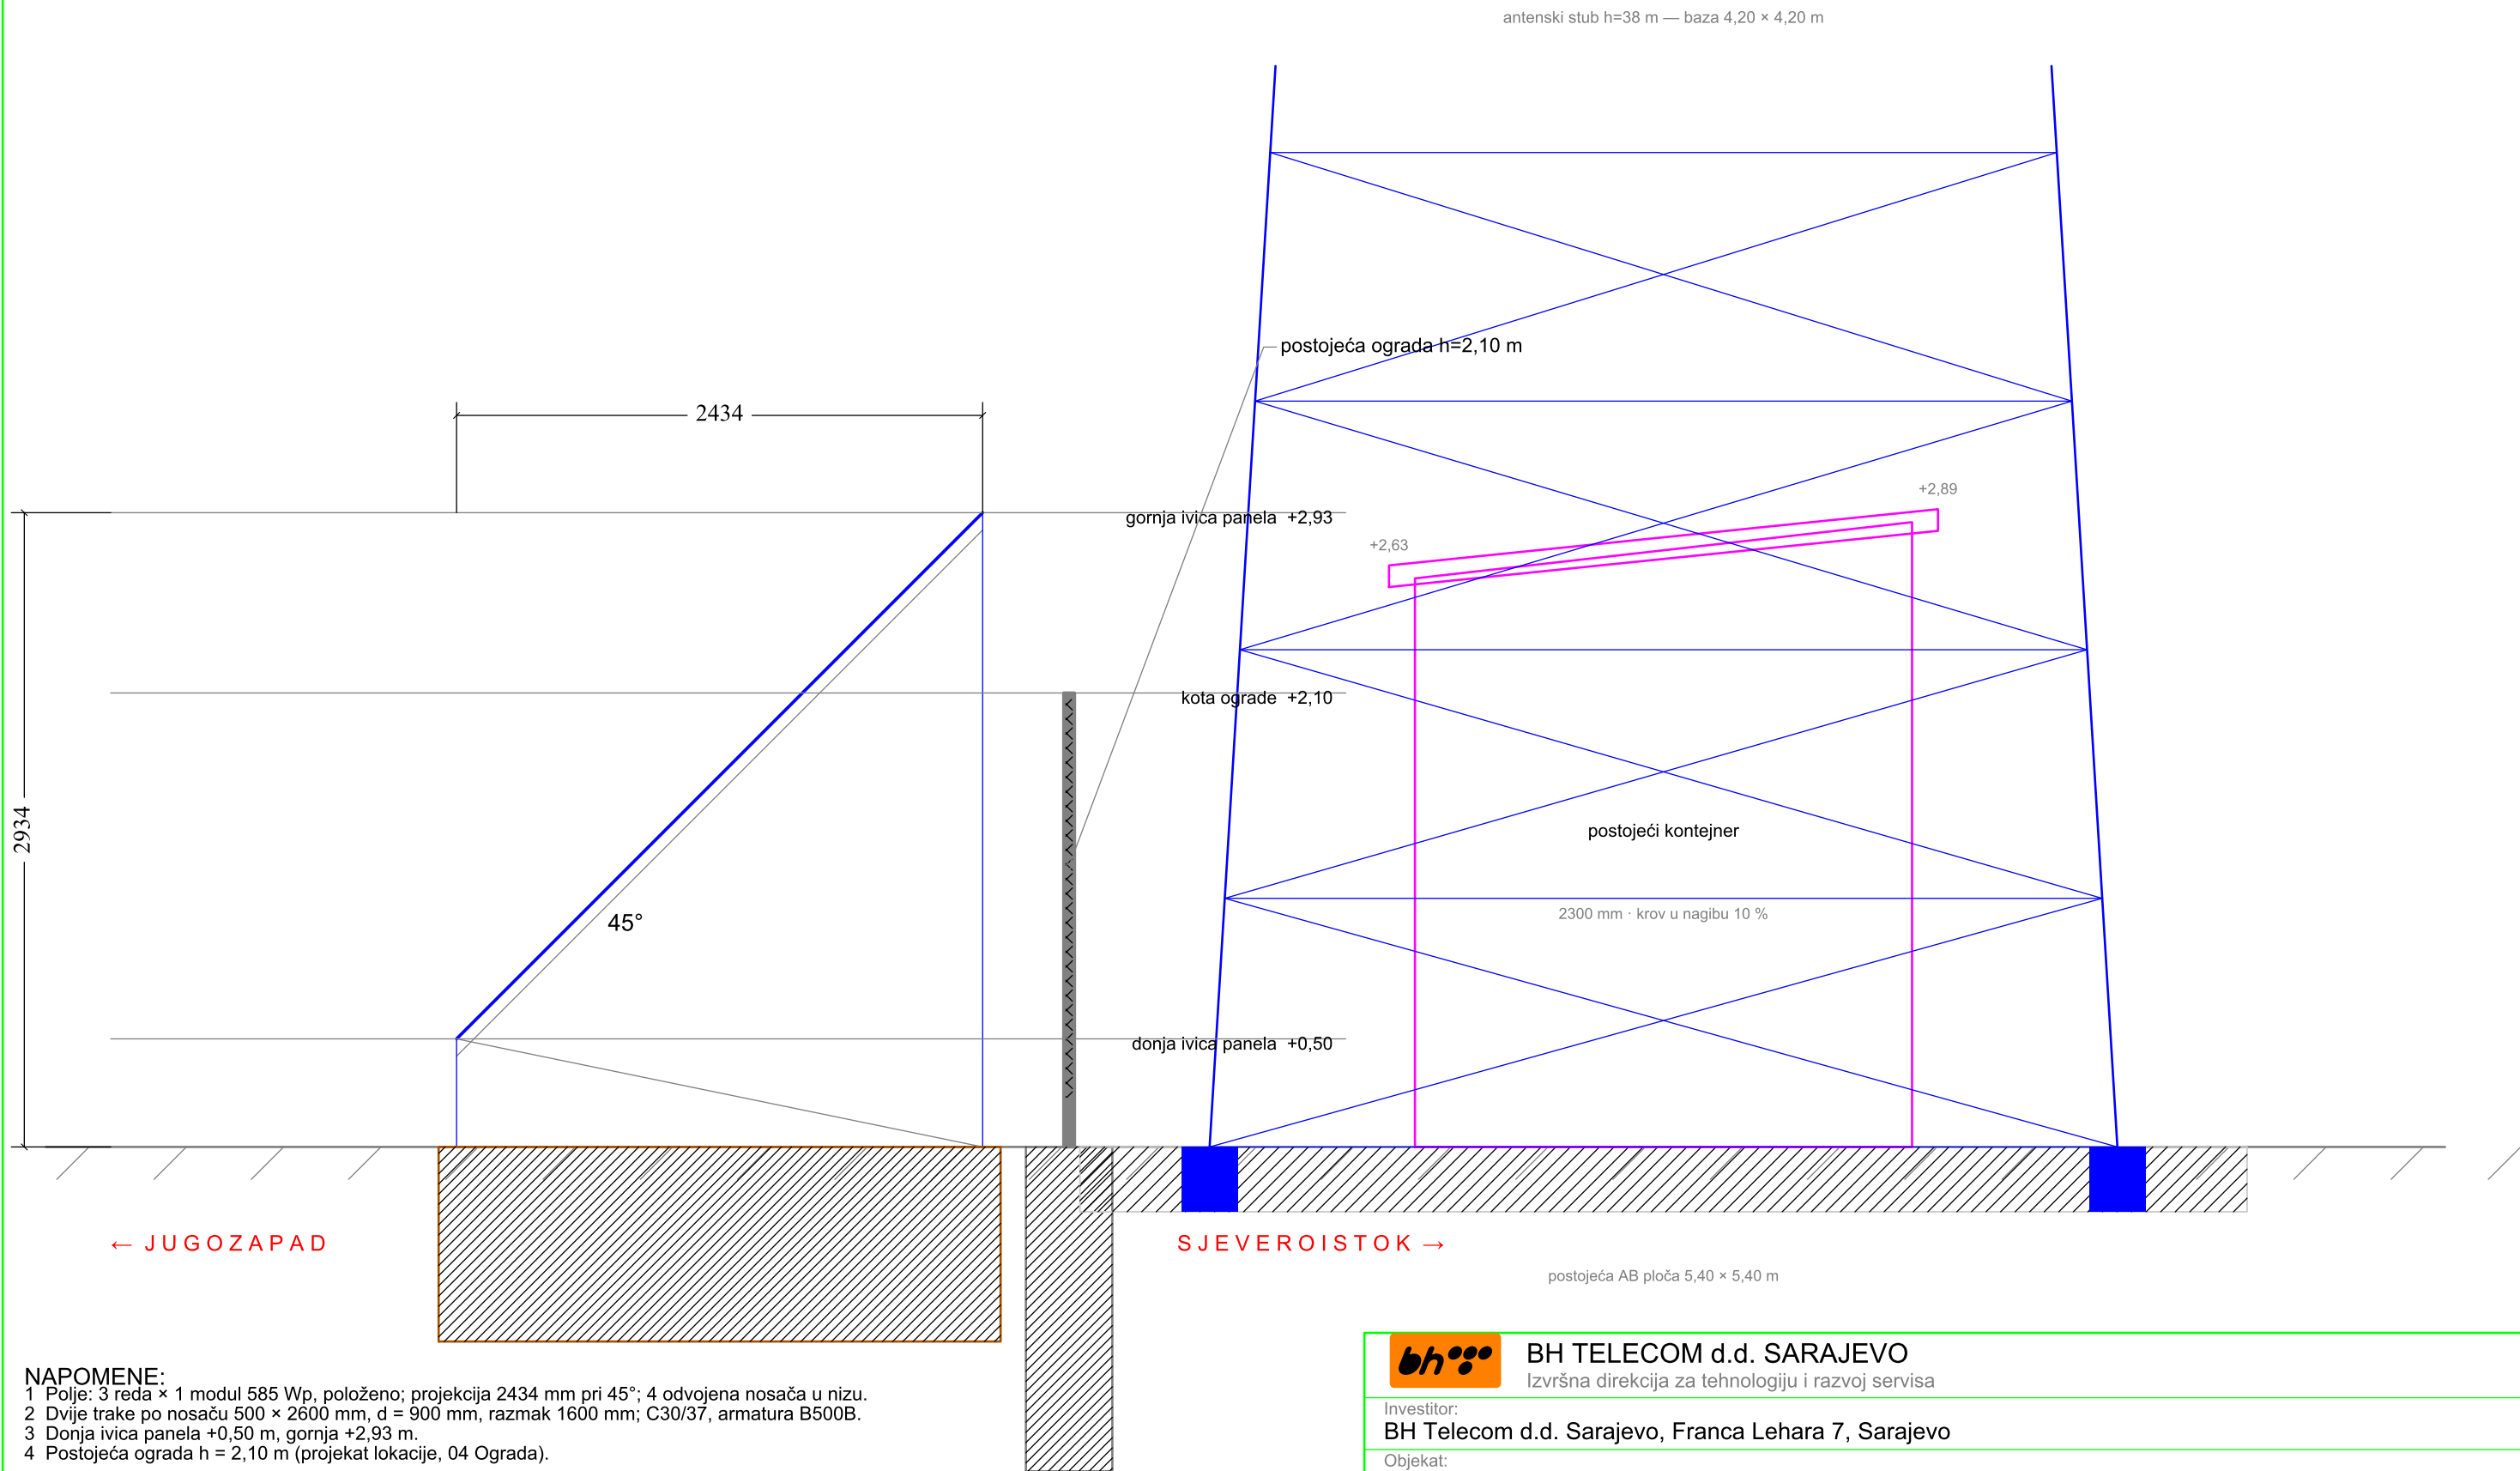

NAPOMENE:
1 Polje: 3 reda × 1 modul 585 Wp, položeno; projekcija 2434 mm pri 45°; 4 odvojena nosača u nizu.
2 Dvije trake po nosaču 500 × 2600 mm, d = 900 mm, razmak 1600 mm; C30/37, armatura B500B.
3 Donja ivica panela +0,50 m, gornja +2,93 m.
4 Postojeća ograda h = 2,10 m (projekat lokacije, 04 Ograda).

BH TELECOM d.d. SARAJEVO Izvršna direkcija za tehnologiju i razvoj servisa		
Investitor: BH Telecom d.d. Sarajevo, Franca Lehara 7, Sarajevo		
Objekat: BS SJEDNICA (Bileća) — autonomni hibridni sistem napajanja		
Faza: Tenderska dokumentacija — Prilog III		šifra projekta: BHT-SJEDNICA-2026
Naziv crteža: Presjek A–A kroz nosač FN panela		razmjera: 1:30
Projektant: Rusmir Skopljak, dipl. ing. el.	ovjerio: Rusmir Skopljak, dipl. ing. el.	godina / broj crteža: 2026. S-03

POGLED SA JUGOZAPADA (pravac gledanja azimut 45°)

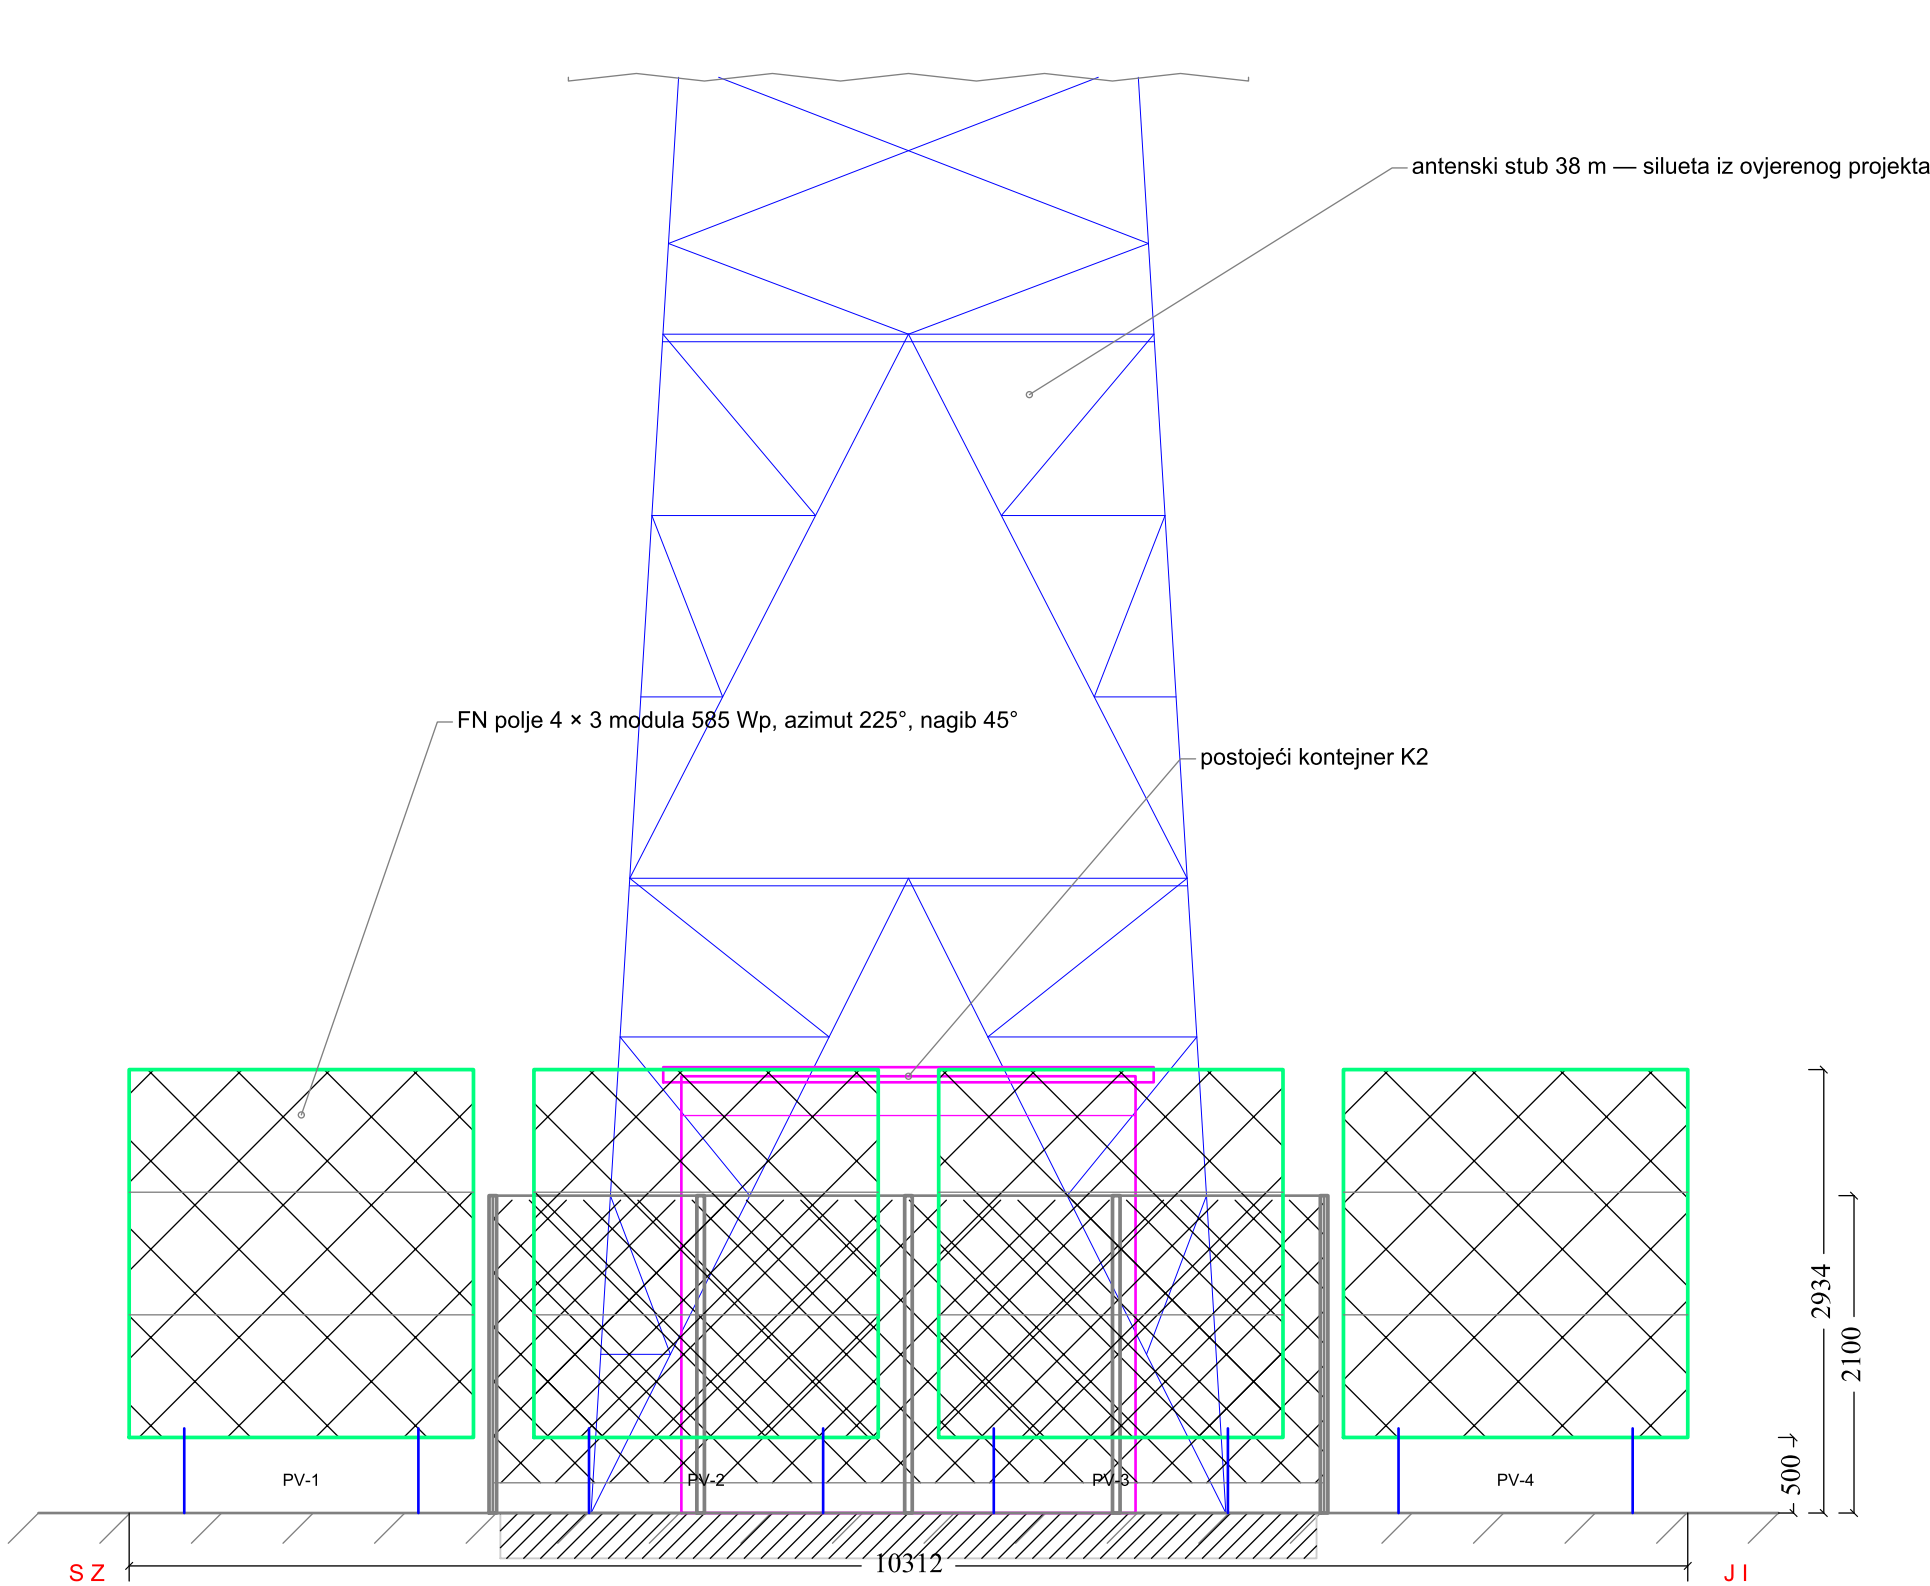


LEGENDA

- LOT 1 — FN moduli i nosači (ispred ograde, JZ)
- postojeći antenski stub — silueta iz ovjerenog projekta
- postojeći kontejner K2 na postojećoj ploči
- postojeća ograda h = 2,10 m

NAPOMENE:


- Prava ortogonalna elevacija u pravcu azimuta 45°; visine i širine su mjerljive.
- Paneli gledaju u posmatrača pod 45°, pa se po visini vide skraćeno: +0,50 do +2,93 m.
- Stub je prikazan do +9,50 m i prekinut; h = 38 m prema ovjerenom projektu (list 462 — 01_ANTENSKI STUB 38 m).
- Zahtjevi: Prilog I, Tačke 3 i 4.

BH TELECOM d.d. SARAJEVO Izvršna direkcija za tehnologiju i razvoj servisa		
Investitor: BH Telecom d.d. Sarajevo, Franca Lehara 7, Sarajevo		
Objekat: BS SJEDNICA (Bileća) — autonomni hibridni sistem napajanja		
Faza: Tenderska dokumentacija — Prilog III		šifra projekta: BHT-SJEDNICA-2026
Naziv crteža: Pogled sa JUGOZAPADA — kompleks sa FN poljem		razmjera: 1:50
Projektant: Rusmir Skopljak, dipl. ing. el.	ovjerio: Rusmir Skopljak, dipl. ing. el.	godina / broj crteža: 2026. S-04

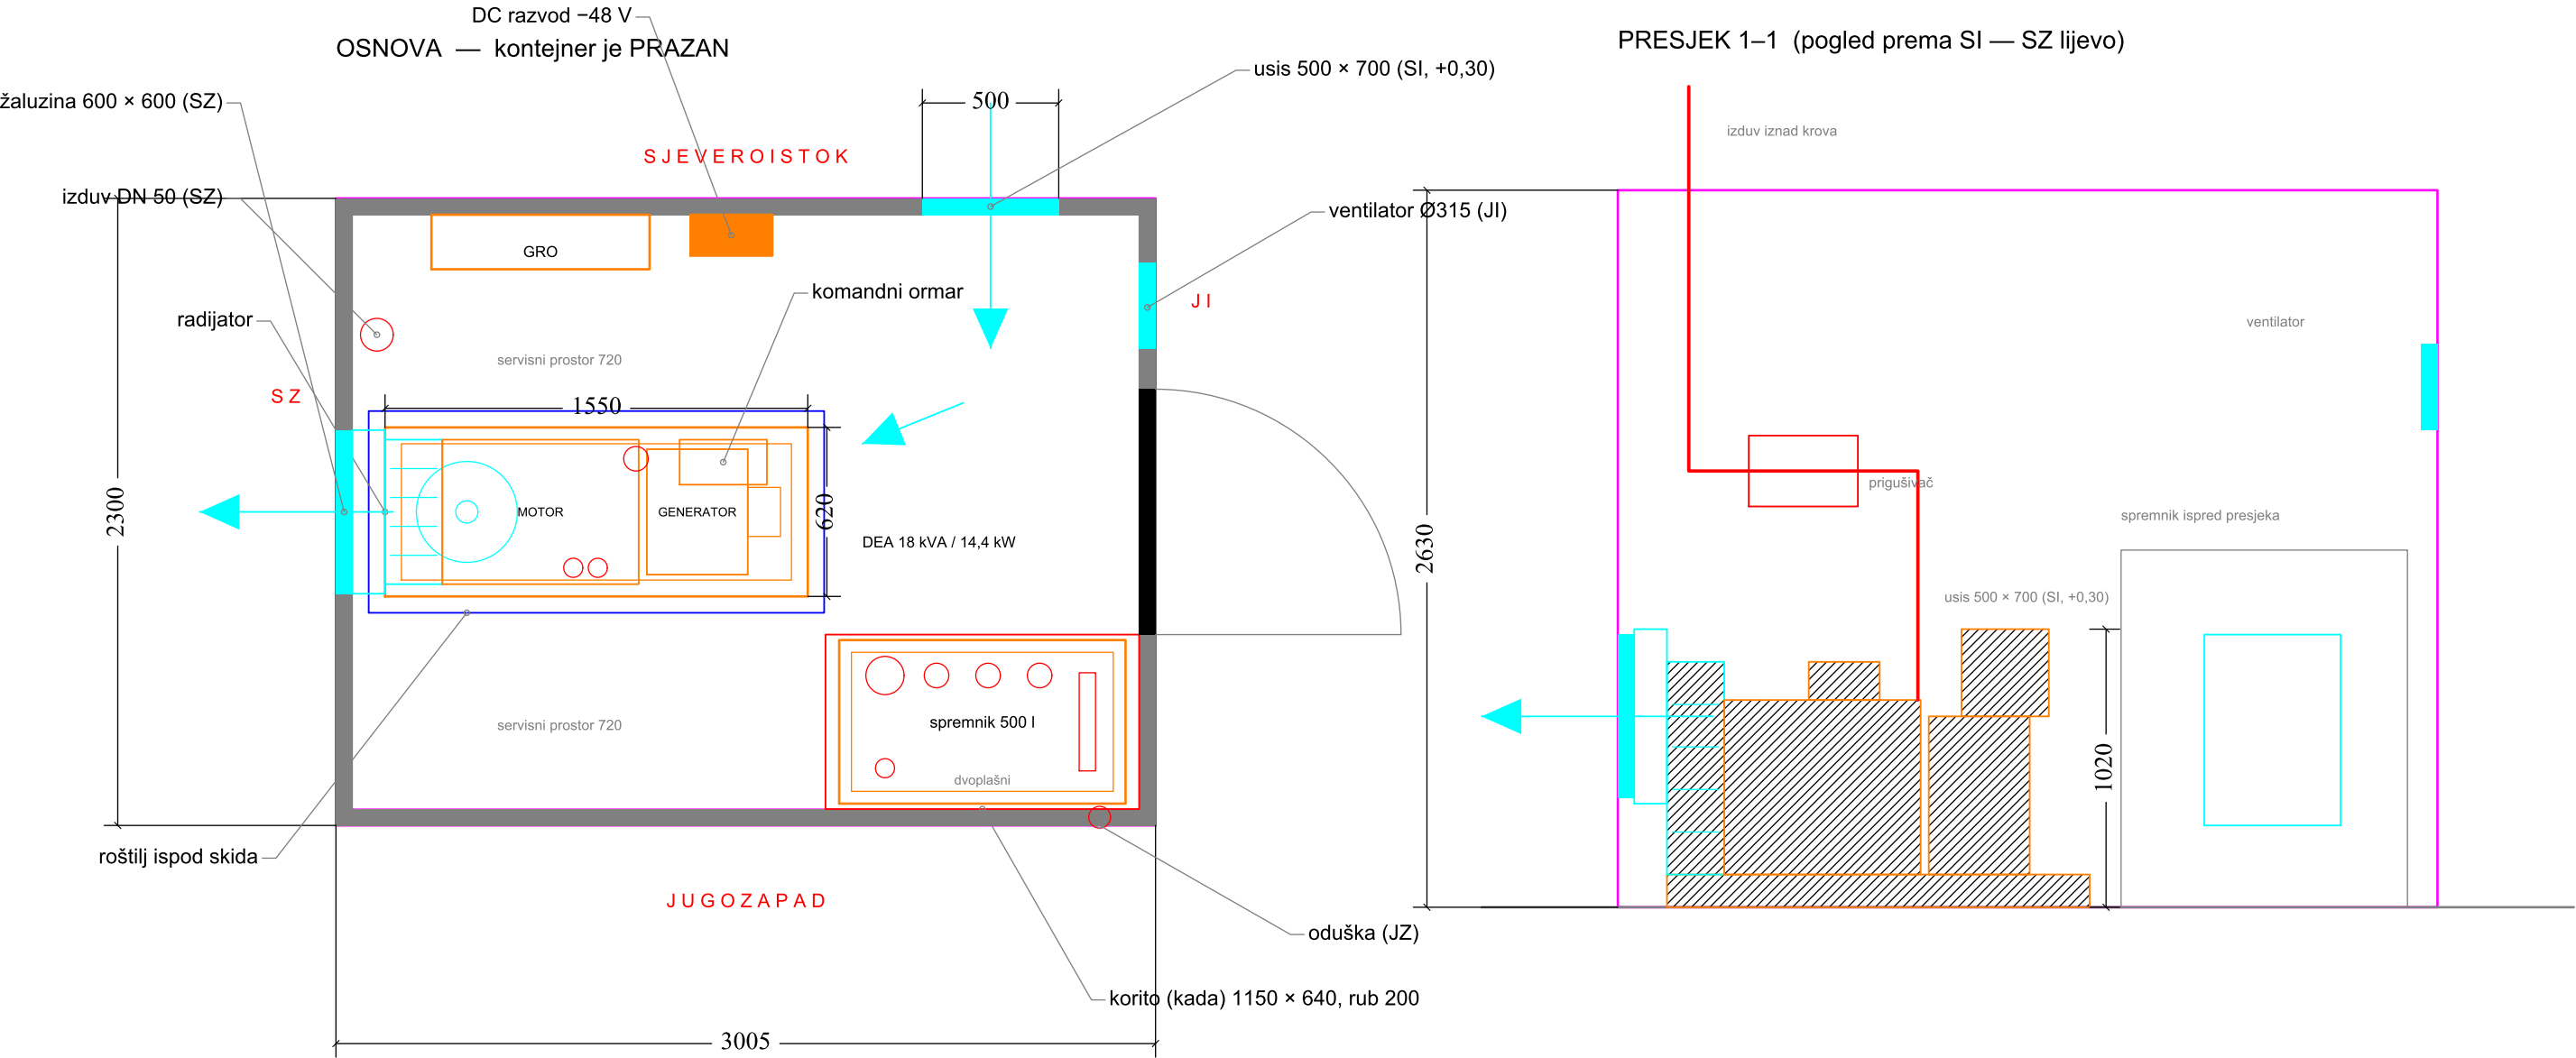

- NAPOMENE:
- 1 DEA FG Wilson P18-6 (skid) ili ekv., 18 kVA / 14,4 kW.
 - 2 Usis 500 × 700 SI (+0,30); kanal i žaluzina 600 × 600 te izduv DN 50 SZ; oduška JZ; ventilator Ø315 JI.
 - 3 Roštilj OBAVEZAN ispod skida i ispod korita.
 - 4 Spremnik DVOPLAŠNI; ispod njega korito 1150 × 640, rub 200 mm.
 - 5 Servisni prolazi 720 mm JZ / 720 mm SI / 1155 mm JI — ne zauzimati.
 - 6 Unos skida 620 mm kroz vrata 900 mm. Kontejner je PRAZAN.
 - 7 DC razvod -48 V na SI zidu uz GRO; trajni potrošači D1-D6 — E-01.
 - 8 Raspored je principijelan; potvrđuje se na licu mjesta. Zahtjevi: Prilog I, Tačka 4.

bh BH TELECOM d.d. SARAJEVO Izvršna direkcija za tehnologiju i razvoj servisa		
Investitor: BH Telecom d.d. Sarajevo, Franca Lehara 7, Sarajevo		
Objekat: BS SJEDNICA (Bileća) — autonomni hibridni sistem napajanja		
Faza: Tenderska dokumentacija — Prilog III		šifra projekta: BHT-SJEDNICA-2026
Naziv crteža: DEA u postojećem kontejneru — osnova i presjek		razmjera: 1:25
Projektant: Rusmir Skopljak, dipl. ing. el.	ovjerio: Rusmir Skopljak, dipl. ing. el.	godina / broj crteža: 2026. M-01

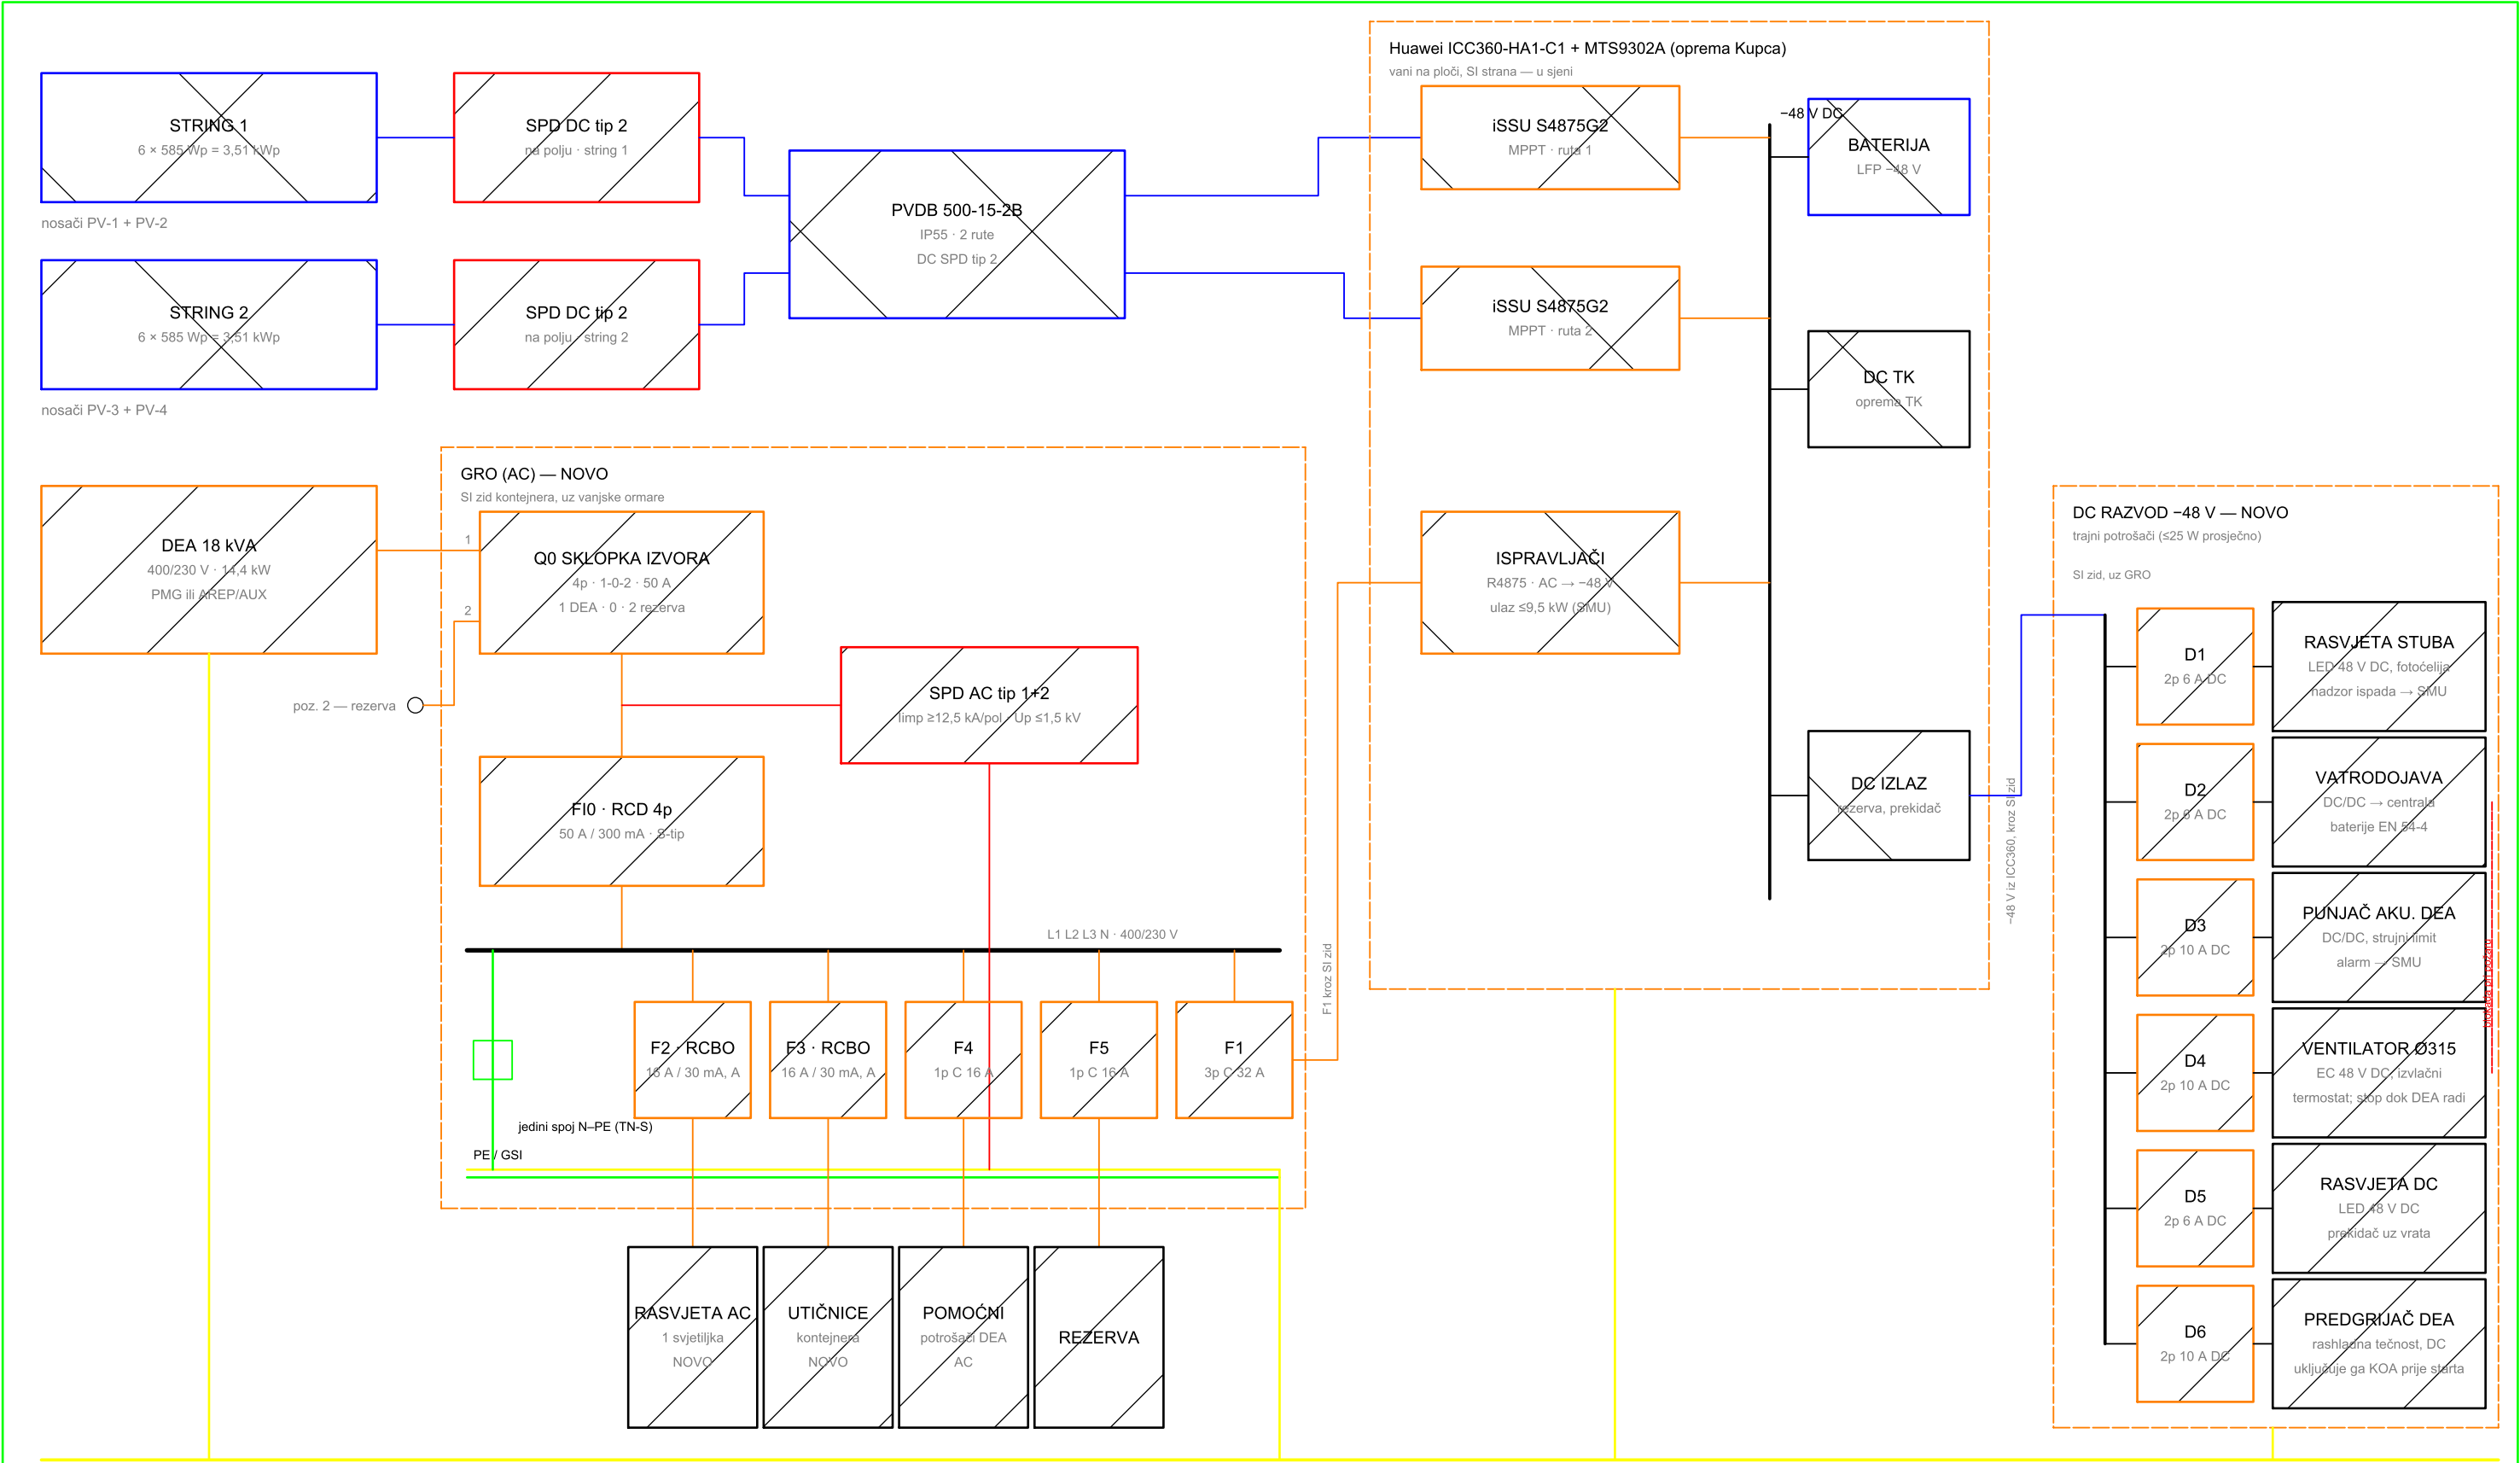

postojeći prstenasti uzemljivač Fe/Zn 25×4 · R ≤ 10 Ω · nosači FN vezani Cu užetom 50 mm² preko bimetalnih spojeva

NAPOMENE:

- DEA je jedini AC izvor; izvodi GRO su pod naponom samo dok DEA radi. Trajni potrošači su na DC razvodu -48 V.
- TN-S: jedini spoj N-PE je u novom GRO; R ≤ 10 Ω. Odvodnici: AC tip 1+2, DC tip 2 po stringu, signalni vodovi EN 61643-21.
- DEA sa nezavisnom pobudom PMG ili AREP/AUX (≥3 × In ≈ 78 A, ≥10 s); RCD 50 A / 300 mA S-tip je obavezan.
- Ulaz ispravljača ograničen na 9,5 kW dok radi DEA (SMU). Kontejner je prazan — nema zatečenih izvoda.
- FN: 12 modula = 2 stringa × 6; PVDB ima 2 rute → 2 × iSSU S4875G2. Požar: STOP DEA i isključenje ventilatora.
- Nazivne struje F4–F5 i D1–D6 su orijentacione; presjeke i selektivnost potvrđuje Izvođač. ICC360 — principijelno.

isporuka i montaža Izvođača (DEA, GRO, DC razvod -48 V)

oprema Kupca (FN, PVDB, iSSU, baterije, ICC360)



BH TELECOM d.d. SARAJEVO

Izvršna direkcija za tehnologiju i razvoj servisa

Investitor:

BH Telecom d.d. Sarajevo, Franca Lehara 7, Sarajevo

Objekat:

BS SJEDNICA (Bileća) — autonomni hibridni sistem napajanja

Faza:

Tenderska dokumentacija — Prilog III

Naziv crteža:

Jednopolna šema — novi GRO i DC razvod -48 V

Projektant:

Rusmir Skopljak, dipl. ing. el.

ovjerio:

Rusmir Skopljak, dipl. ing. el.

šifra projekta:


BHT-SJEDNICA-2026

razmjera:


—

godina / broj crteža:


2026. E-01

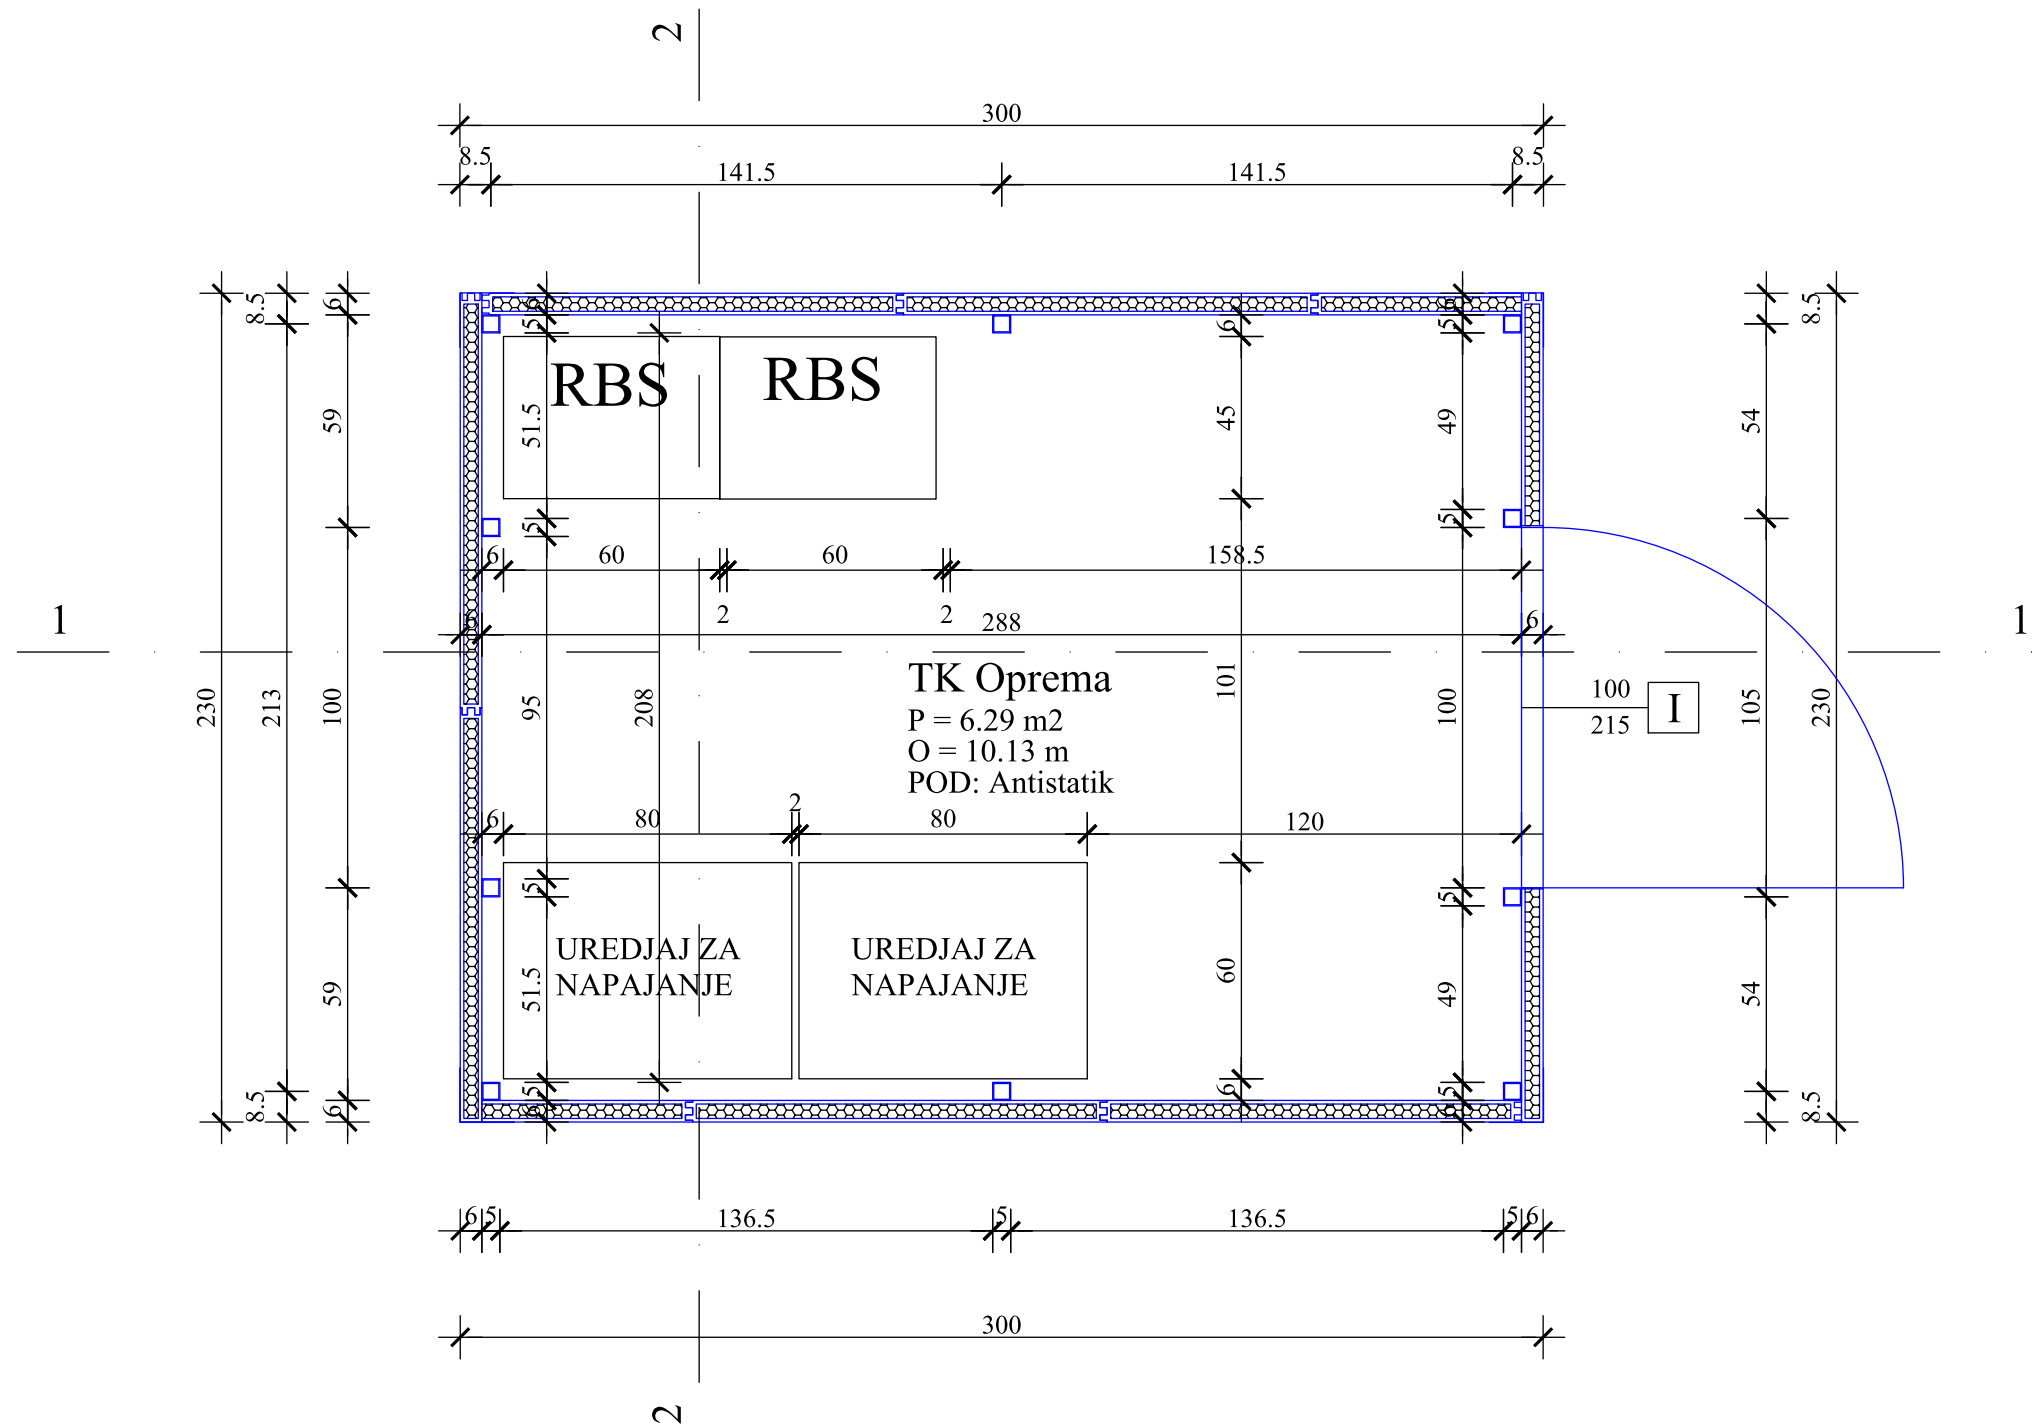





Investitor: BH TELECOM d.d.		Objekat: Infrastruktura bazne stanice mobilne telefonije		bh telecom Dioničko društvo Sarajevo	
Glavni projekat Knjiga 1/1	Faza: A	godina: 2018.	šifra projekta: GP-BS-10472-326	broj crteža: 1 - (148/177)	ovjerio:  Projektant:Dženadin Mušinović,d.i.g.
Naziv crteža: Osnova objekta za smještaj opreme			razmjera: 1:50		

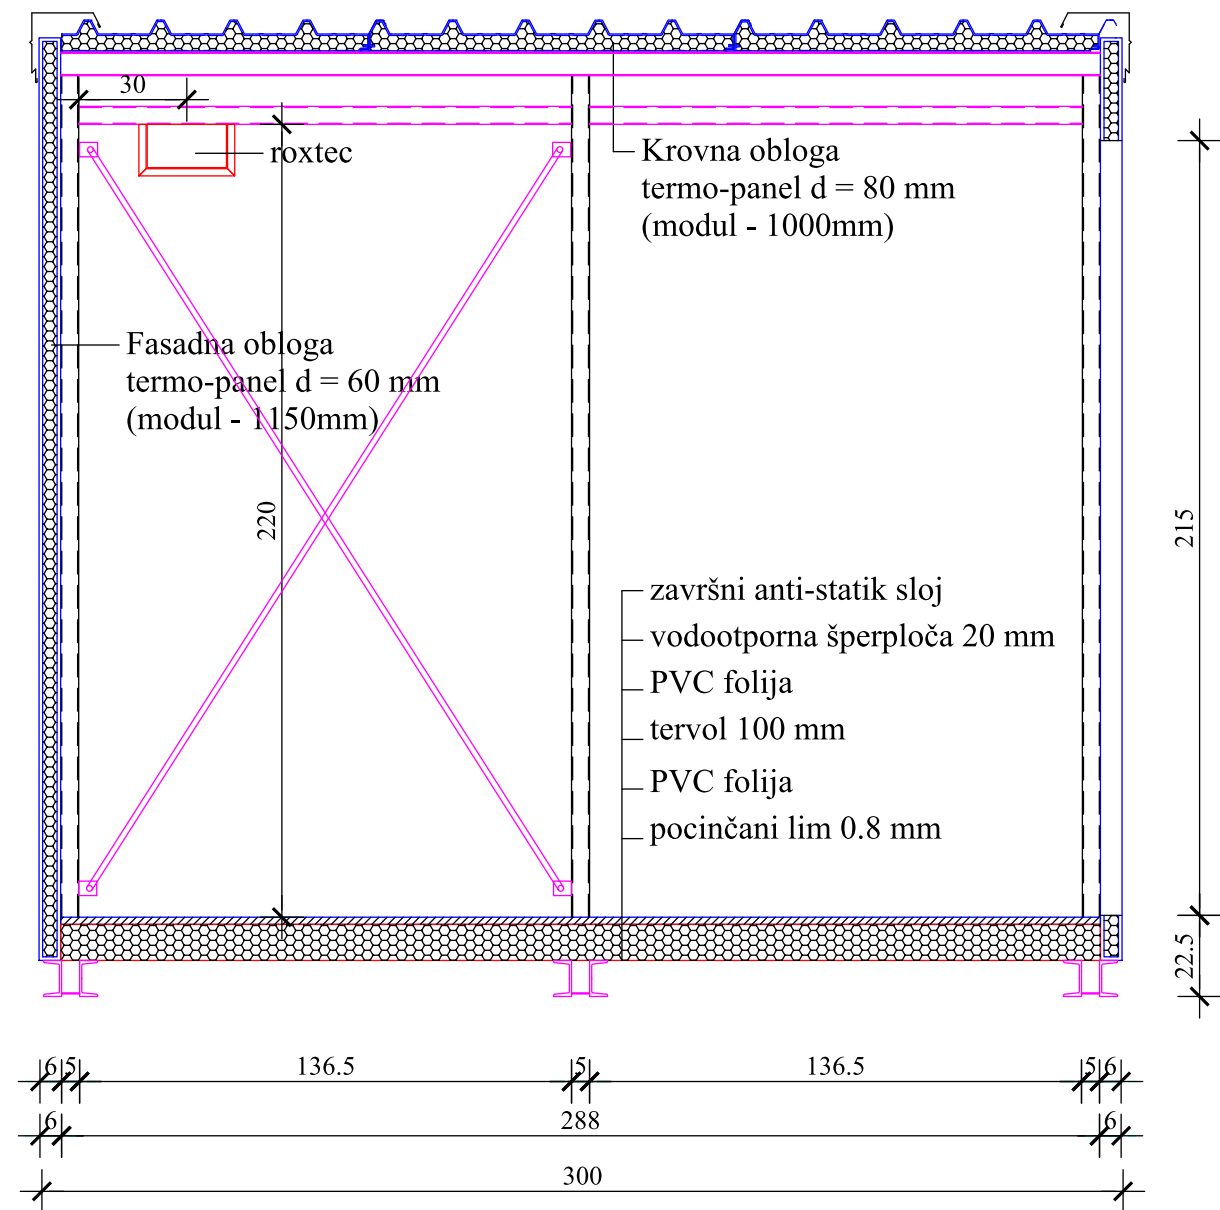

Investitor: BH TELECOM d.d.		Objekat: Infrastruktura bazne stanice mobilne telefonije		 Dioničko društvo Sarajevo	
Glavni projekat Knjiga 1/1	Faza: A	godina: 2018.	šifra projekta: GP-BS-10472-326		
Naziv crteža: Presjek 1-1 objekta za smještaj opreme		razmjera: 1:50	broj crteža: 2 - (149/177)	ovjerio:  Projektant: Dženadin Mušinović, d.i.g.	

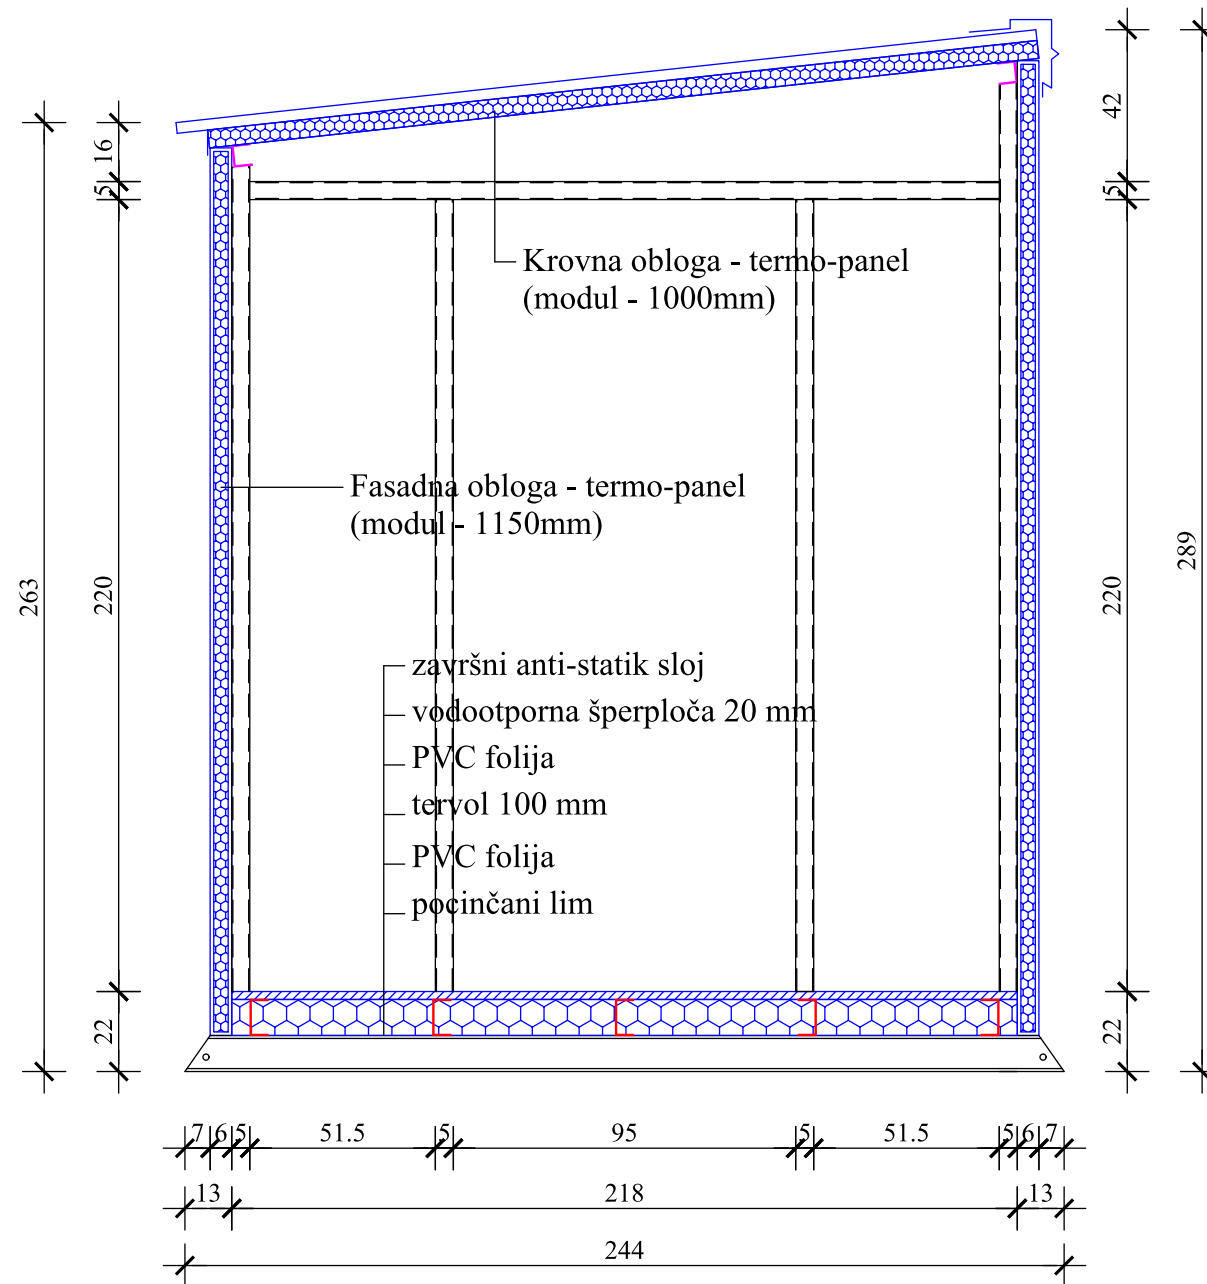


Investitor: BH TELECOM d.d.		Objekat: Infrastruktura bazne stanice mobilne telefonije		 Dioničko društvo Sarajevo	
Glavni projekat Knjiga 1/1	Faza: A	godina: 2018.	šifra projekta: GP-BS-10472-326		
Naziv crteža: Presjek 2-2 objekta za smještaj opreme			razmjera: 1:50	broj crteža: 3 - (150/177)	ovjerio: Projektant: Dženadin Mušinić, d.i.g.

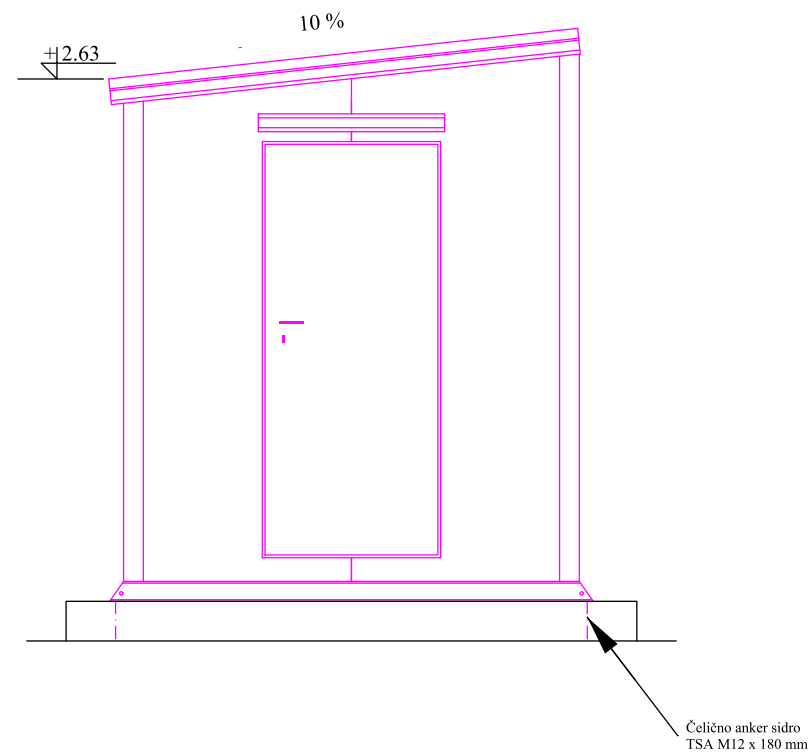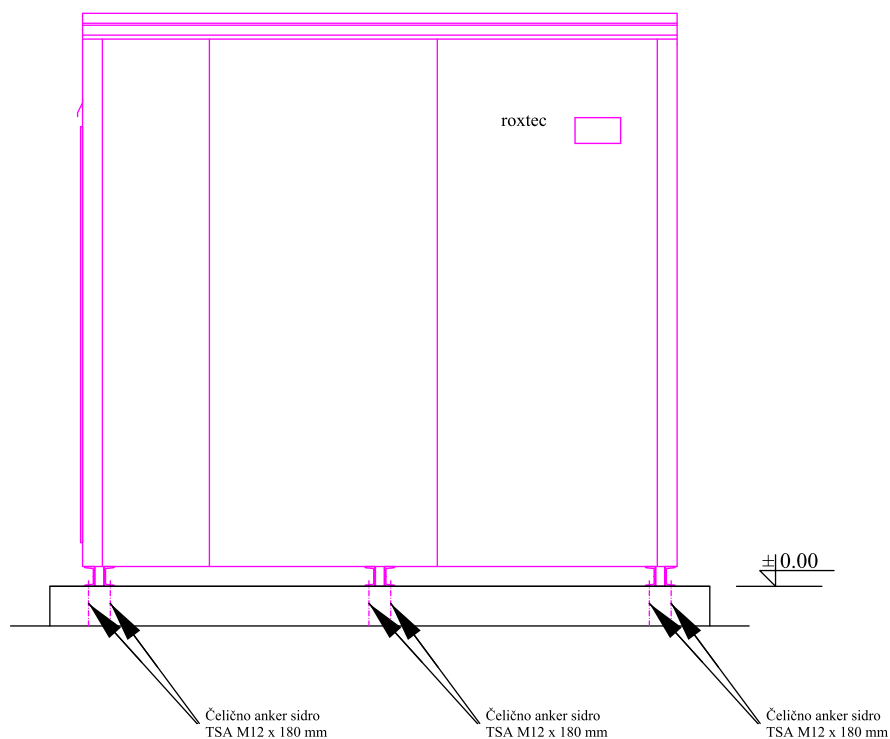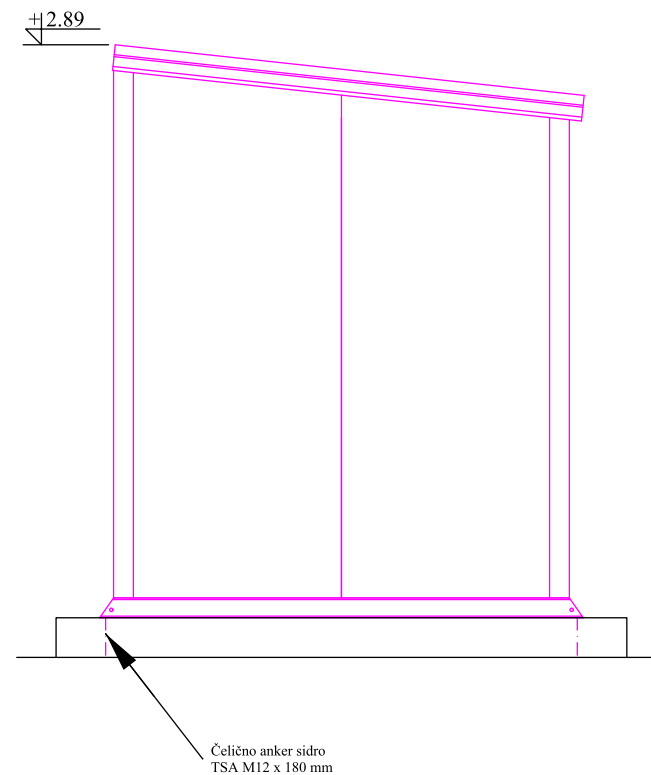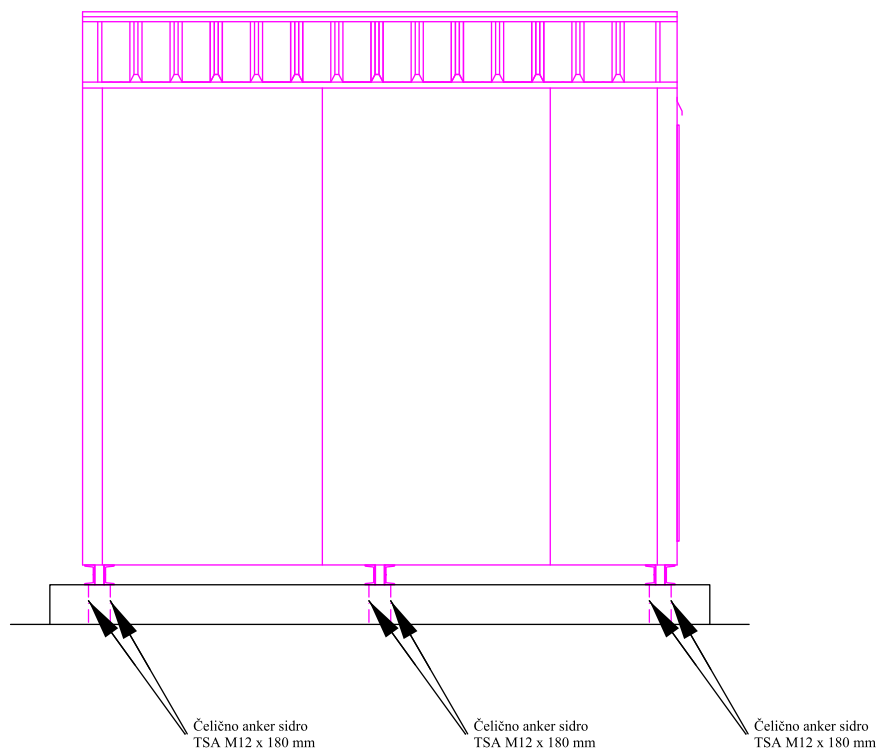


Investitor: BH TELECOM d.d.		Objekat: Infrastruktura bazne stanice mobilne telefonije		 Dioničko društvo Sarajevo	
Glavni projekat Knjiga 1/1	Faza: A	godina: 2018.	šifra projekta: GP-BS-10472-326		
Naziv crteža: Fasade objekta za smještaj opreme				razmjera: 1:50	broj crteža: 4 - (151/177)
				ovjerio: Projektant:Dženadin Mušinović,d.i.g.	


Ugaoni vanjski opšav

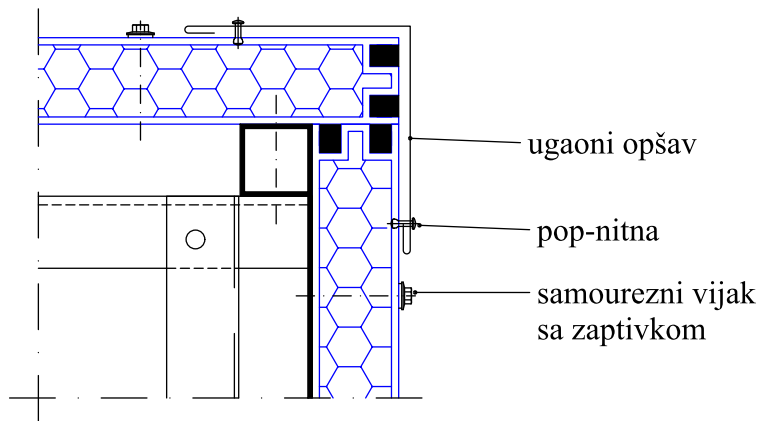


Čeoni lim na višem kraju krova

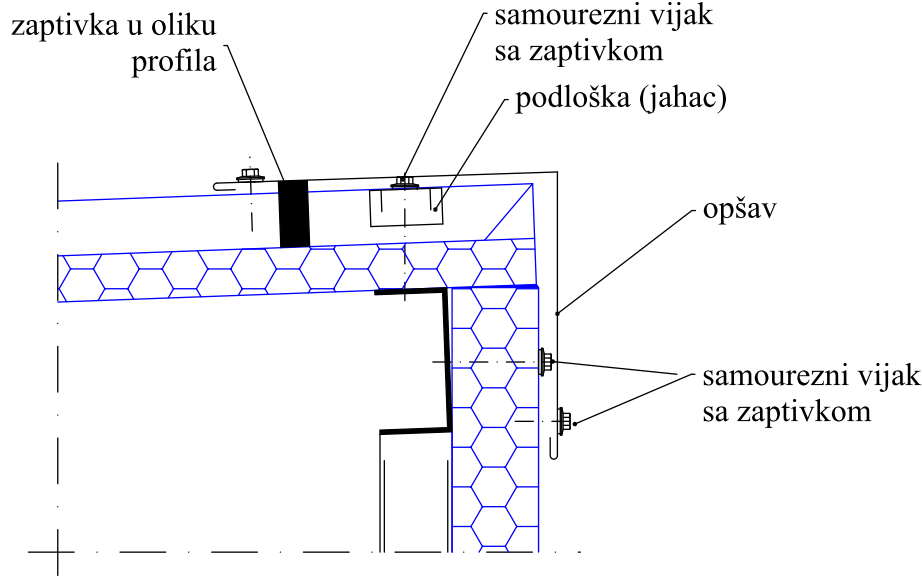

Čeoni lim na nižem kraju krova

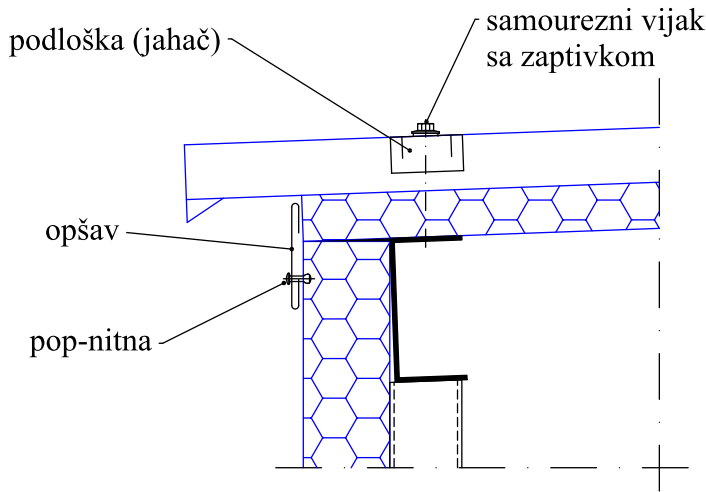


Bočni krovni opšav

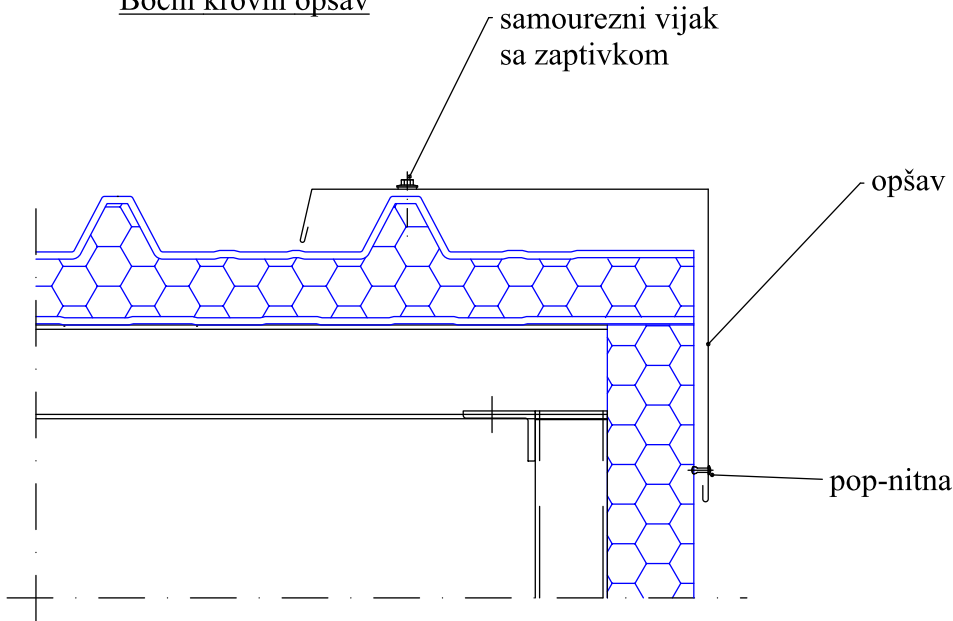


Investitor: BH TELECOM d.d.		Objekat: Infrastruktura bazne stanice mobilne telefonije		bh telecom Dioničko društvo Sarajevo	
Glavni projekat Knjiga 1/1	Faza: A	godina: 2018.	šifra projekta: GP-BS-10472-326	broj crteža: 5 - (152/177)	ovjerio: Projektant: Dženadin Mušinović, d.i.g.
Naziv crteža: DETalji objekta za smještaj opreme				razmjera: 1:50	

PLAN OPLATE TEMELJNOG BLOKA


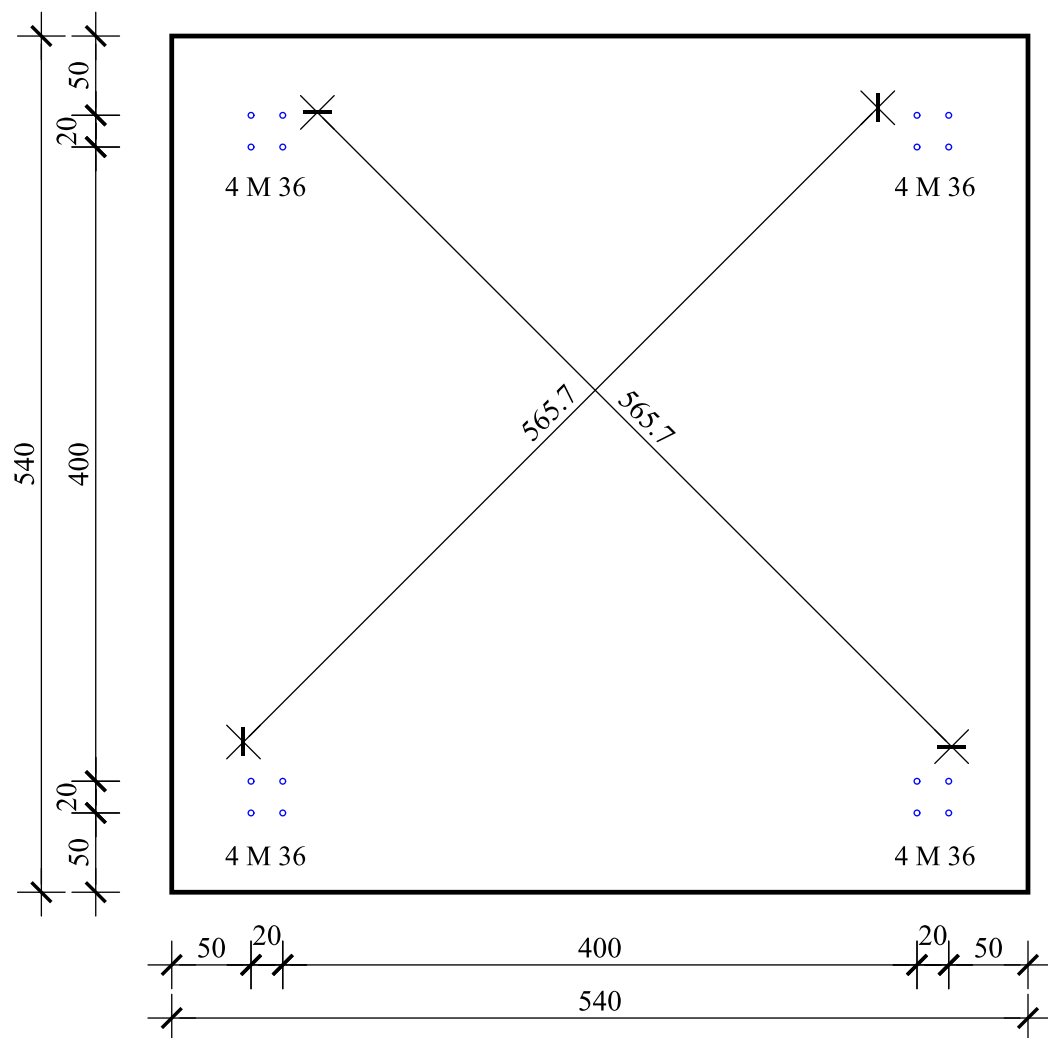


PLAN ARMATURE TEMELJNOG BLOKA

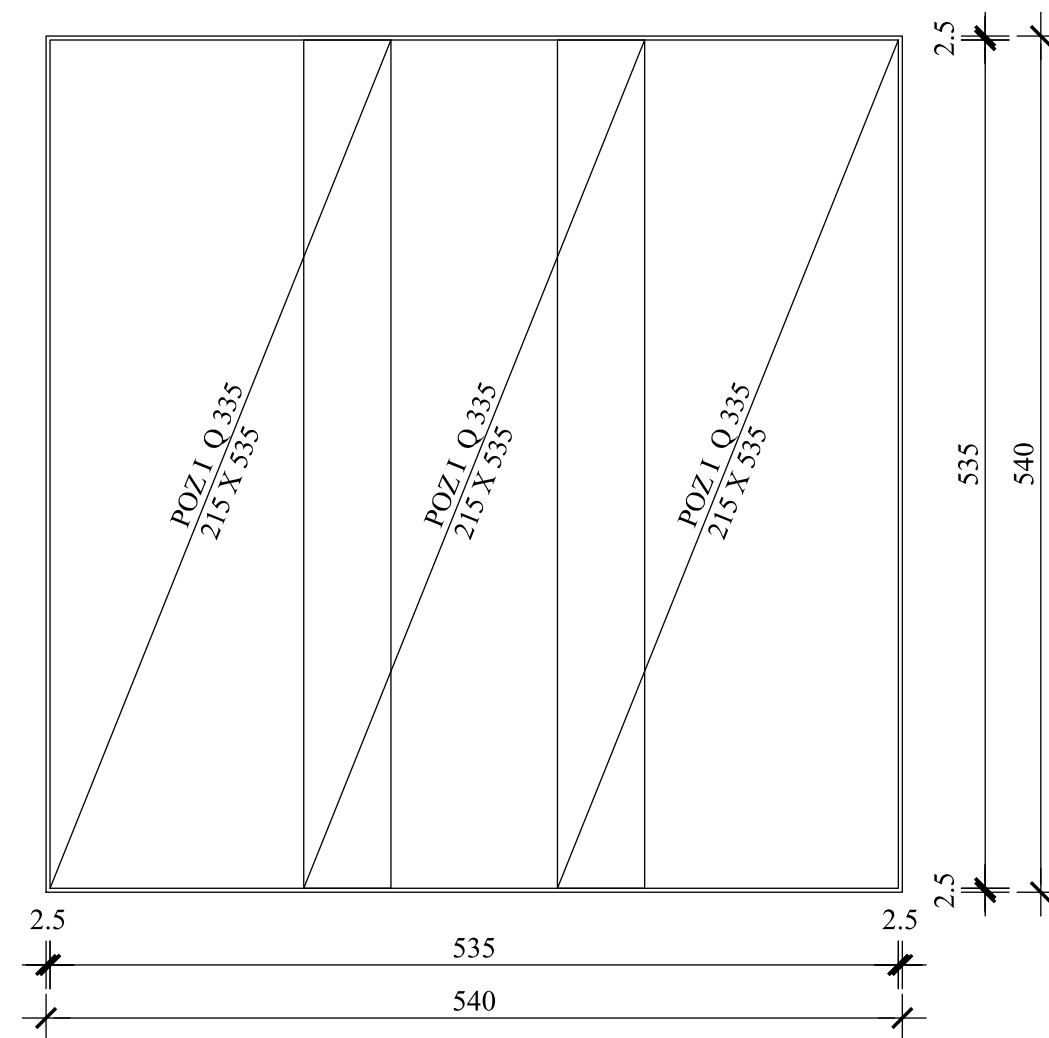


Ankeri Ø 36 mm l = 200 cm komada 4x4=16

Vilice Ø 10 mm/20 cm l = 116 cm komada 4x6=24

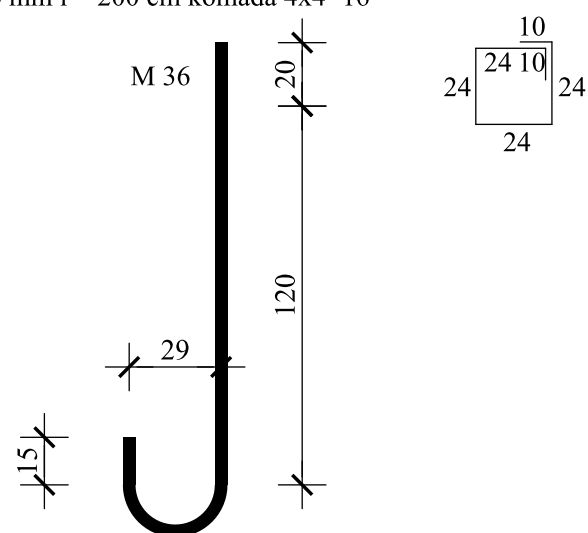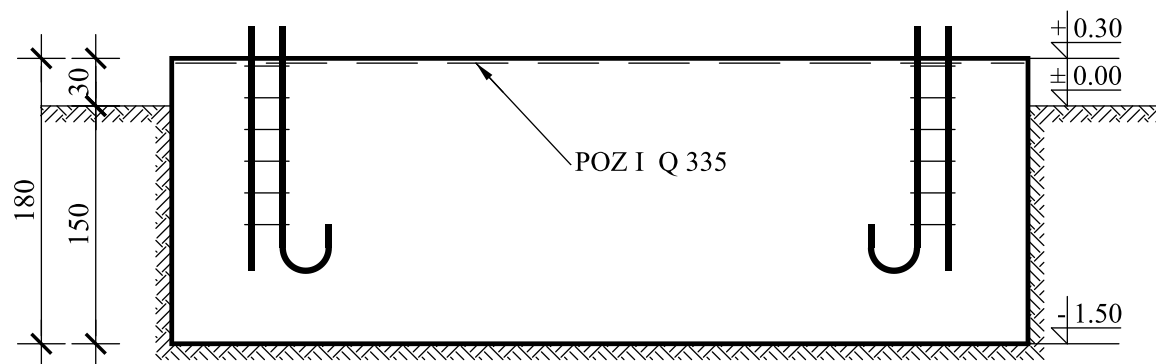



MB 25 (B.I, M-100)
RA 400/500
MA 500/560

Investitor: BH TELECOM d.d.		Objekat: Infrastruktura bazne stanice mobilne telefonije		 Dioničko društvo Sarajevo	
Glavni projekat Knjiga 1/1	Faza: K	godina: 2018.	šifra projekta: GP-BS-10472-326		
Naziv crteža: Plan oplata i armature temelja			razmjera: 1:50	broj crteža: 3 - (121/177)	ovjerio:  Projektant: Dženadin Mušinić, d.i.g.

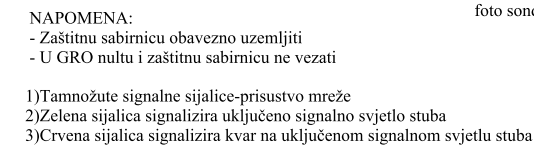

Investitor: BH TELECOM d.d.		Objekat: Infrastruktura bazne stanice mobilne mreže			
Glavni projekat Knjiga EI	izdanje: I	godina: 2018.	šifra projekta: GP-BS-10472-326	Dioničko društvo Sarajevo	
Naziv crteža: 3.5.2. Jednopolna šema GRO			razmjera:	broj crteža:	Projektant: Močević Džafer, d.e.i.
				48/69	ovjerio: 

FN simulacija — proizvodnja i energetska bilans (informativno)

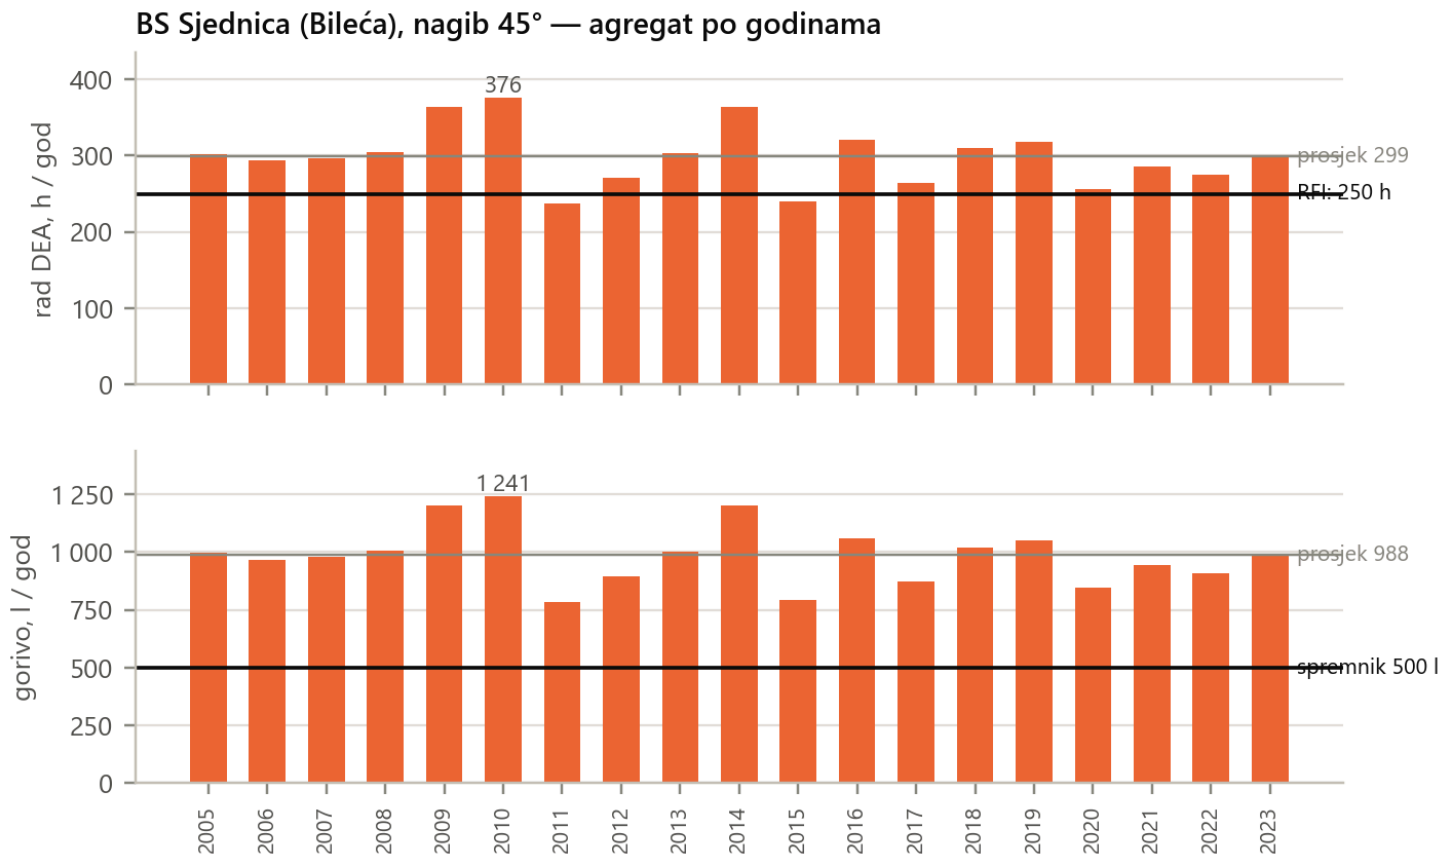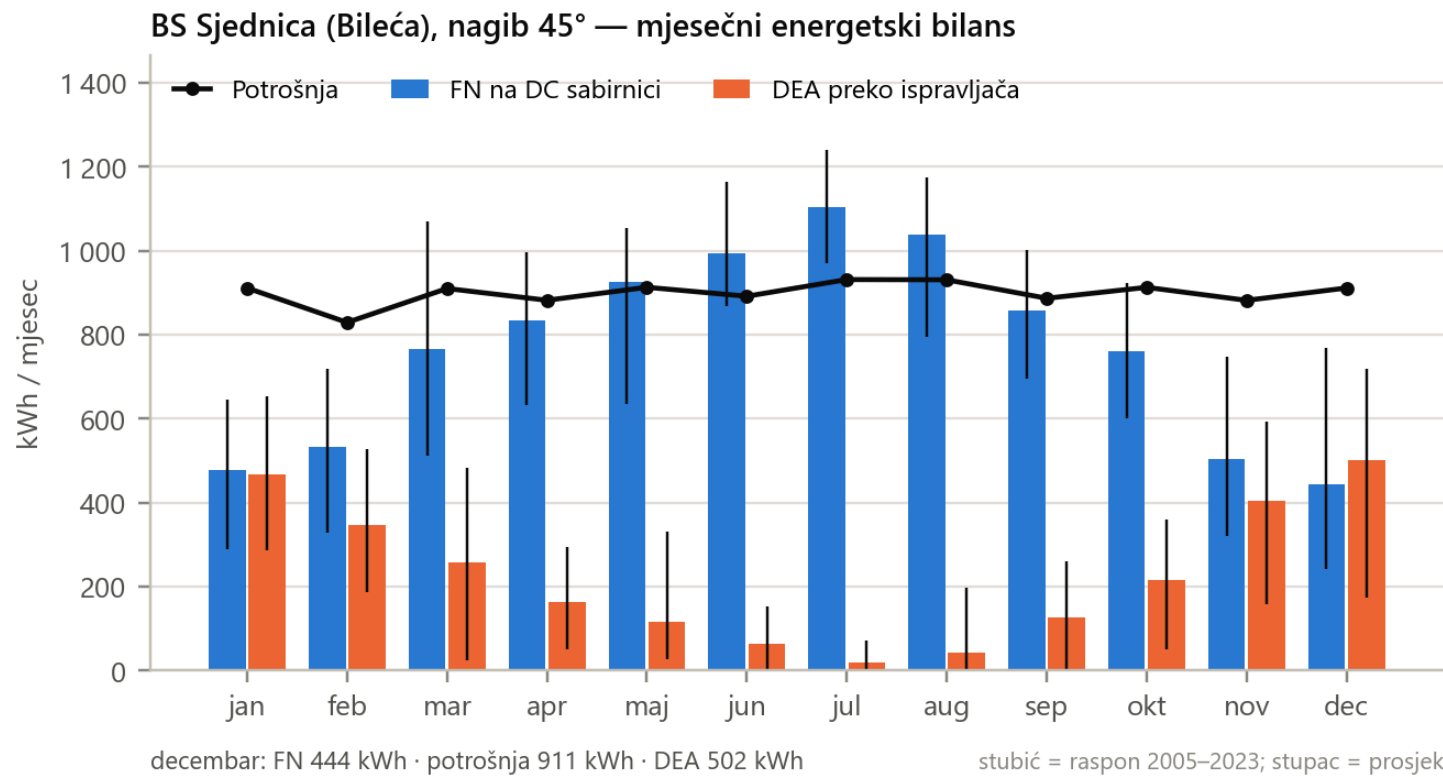

Polje	12 × iPV585-M2A = 7,02 kWp na 4 nosača, nagib 45°, azimut 225° (jugozapad)
FN na DC sabirnici (–48 V)	9 242 kWh/god · 1 317 kWh/kWp
Potrošnja	10 794 kWh/god (1180 W + hlađenje ormara i pomoćna potrošnja)
Decembar	FN 444 kWh prema potrošnji 911 kWh
Solarni udio u potrošnji	74,7 %
Rad DEA	prosjeck 299 h/god · 9 od 10 godina ≤364 h · najviše 376 h
Gorivo	prosjeck 988 l/god · dopuna spremnika 500 l 2,5 puta godišnje
Nepokrivena potrošnja	0 kWh u 19 godina
Provjera prema PVGIS-u	PVcalc 8 849 kWh/god, pvsim sa istim gubicima 8 785 kWh/god; najveće mjesečno odstupanje 2,2 %

Satna simulacija energetskog bilansa na –48 V DC sabirnici za 2005–2023 (pvlib + PVGIS-SARAH3), uz parametrisiranje SMU iz Priloga I, Tačka 4.6: start pri DOD 85 %, zaustavljanje pri SoC 60 %, ograničenje ispravljača 9,5 kW. Metoda, gubici, osjetljivost i pretpostavke: Proračuni, dio A.6. Vrijednosti su informativne i ne mijenjaju zahtjeve Priloga I. Izvor: review/pvsim/kpis.json (sha256 e9bd8e691f7e, pvsim commit e42bbaa).

B. BS HAMZIĆI (ČITLUK)

Fotografije postojećeg stanja lokacije, 08.09.2026.





Antenski stub i kontejner; pogled prema jugu-jugoistoku



Kontejner sa klima-uređajem Stulz WDE80 (demonтира se)

1. OPŠTI PODACI O LOKACIJI — BS HAMZIĆI

Investitor	BH Telecom d.d. Sarajevo, Franca Lehara 7, 71000 Sarajevo
Objekat	Bazna stanica HAMZIĆI
Općina	Čitluk
Koordinate	43,2880° N, 17,6248° E
Nadmorska visina	493 m
Zakupljena površina	150 m ² (12,00 × 12,50 m), k.č. 109/1 K.O. Hamzići (novi premjer)
Betonski temelj	5,40 × 5,40 m, sa metalnom ogradom visine 1,80 m; kapija 1,30 m na SZ strani
Antenski stub	Rešetkasta izvedba, visina 32 m; baza 3,70 × 3,70 m; platforma na +3,0 m iznad krova kontejnera
Klima-uređaj	Stulz WDE80, 8 kW, u sredini JI zida; demontaža i odvoz u skladište Alipašino Polje (LOT 2)
Oprema Kupca	FN moduli, PVDB, iSSU, baterije, ICC360-HA1-C1 — nabavka Naručioca; preuzimanje u skladištu Azići, Bojnička bb, Sarajevo, prevoz i istovar u LOT 2 (Prilog I, Tačka 4.9)
Priključak na EES	Nema; priključak projektovan 2017. nije izveden
Snaga potrošača	1.180 W nazivno / 1.330 W maksimalno
Sistem napajanja	Hibridni: FN moduli + LFP baterije + DEA (rezervni)
FN konfiguracija	12 × iPV585-M2A (7,02 kWp) na 4 nosača po 3 modula (položeno), nagib 45°, azimut 225° (JZ)
DEA	18 kVA / 14,4 kW, skid u kontejneru; ulaz ispravljača ≤9,5 kW
Spremnik goriva	Dvoplašni, 500 l, sa nivo sandom i detekcijom curenja
Orijentacija	Vrata i kapija SZ, hladnjak DEA JI, FN polje JZ; ormari ICC360 i MTS na JZ strani, iza FN polja
Očekivani rad agregata	270~320 h/god

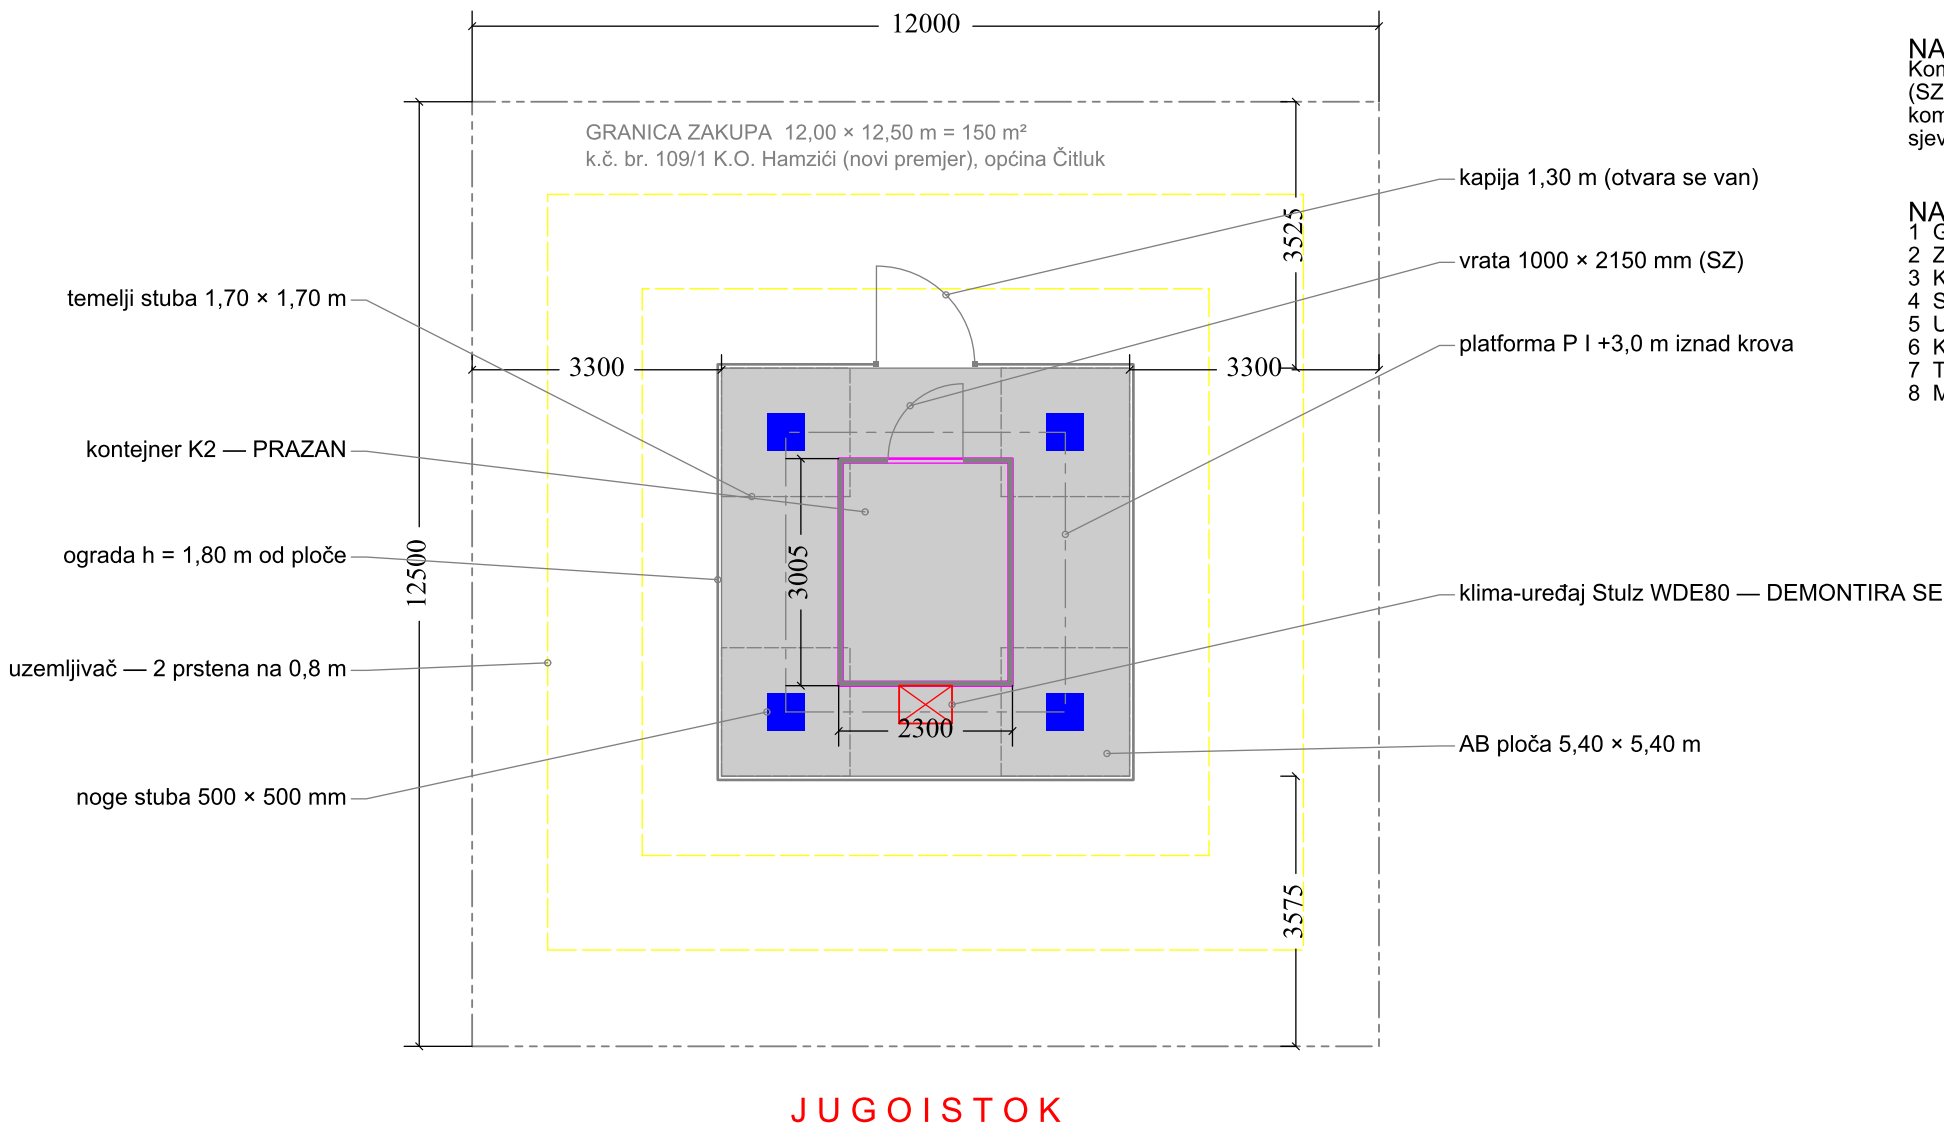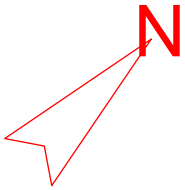



NAPOMENA — ORIJENTACIJA:
Kompleks je zakrenut 45°: vrata kontejnera i kapija gledaju na SJEVEROZAPAD (SZ), klima-uređaj Stulz na JI, FN polje na JZ. Crtež je pravougaon na kompleks (gore SZ, desno SI, dolje JI, lijevo JZ); strelica pokazuje pravi sjever. Orijentaciju potvrđuje Ponuđač obilaskom lokacije.

NAPOMENE:
1 Geometrija iz ovjerenog projekta lokacije GP-BS-10472-291 (2017).
2 Zakup 12,00 x 12,50 m = 150 m², k.č. br. 109/1, općina Čitluk.
3 Kontejner je PRAZAN; u sredini JI zida je Stulz WDE80 (≈700 x 500 x 2200).
4 Stub h = 32 m; platforma P I (+3,0 m) je iznad krova (+2,63 / +2,89 m).
5 Uzemljivač FeZn 25x4: prsten u temeljima stopa i dva prstena na 0,8 m.
6 Kapija se otvara prema van; krilo 1,30 m.
7 Teren uz ploču je na -0,20 m; ograda 1,80 m iznad ploče, 2,00 m iznad terena.
8 Mjere uređaja i otvora uzimaju se na obaveznom obilasku lokacije.

- LEGENDA**
- postojeća ograda 5,50 x 5,50 m, h = 1,80 m od ploče (2,00 m od terena) — kapija 1,30 m na SZ strani
 - postojeća AB ploča 5,40 x 5,40 m
 - postojeći kontejner K2 2300 x 3005 mm — vrata na SZ strani
 - noge rešetkastog stuba h = 32 m, baza 3,70 x 3,70 m
 - klima-uređaj Stulz WDE80 (JI zid, u sredini) — demontira se
 - postojeći uzemljivač FeZn 25x4 mm (isprekidano — u tlu)



bh BH TELECOM d.d. SARAJEVO Izvršna direkcija za tehnologiju i razvoj servisa		
Investitor: BH Telecom d.d. Sarajevo, Franca Lehara 7, Sarajevo		
Objekat: BS HAMZIĆI (ČITLUK) — autonomni hibridni sistem napajanja		
Faza: Tenderska dokumentacija — Prilog III		šifra projekta: BHT-HAMZICI-2026
Naziv crteža: Situacija — POSTOJEĆE STANJE		razmjera: 1:100
Projektant: Rusmir Skopljak, dipl. ing. el.	ovjerio: Rusmir Skopljak, dipl. ing. el.	godina / broj crteža: 2026. H-01

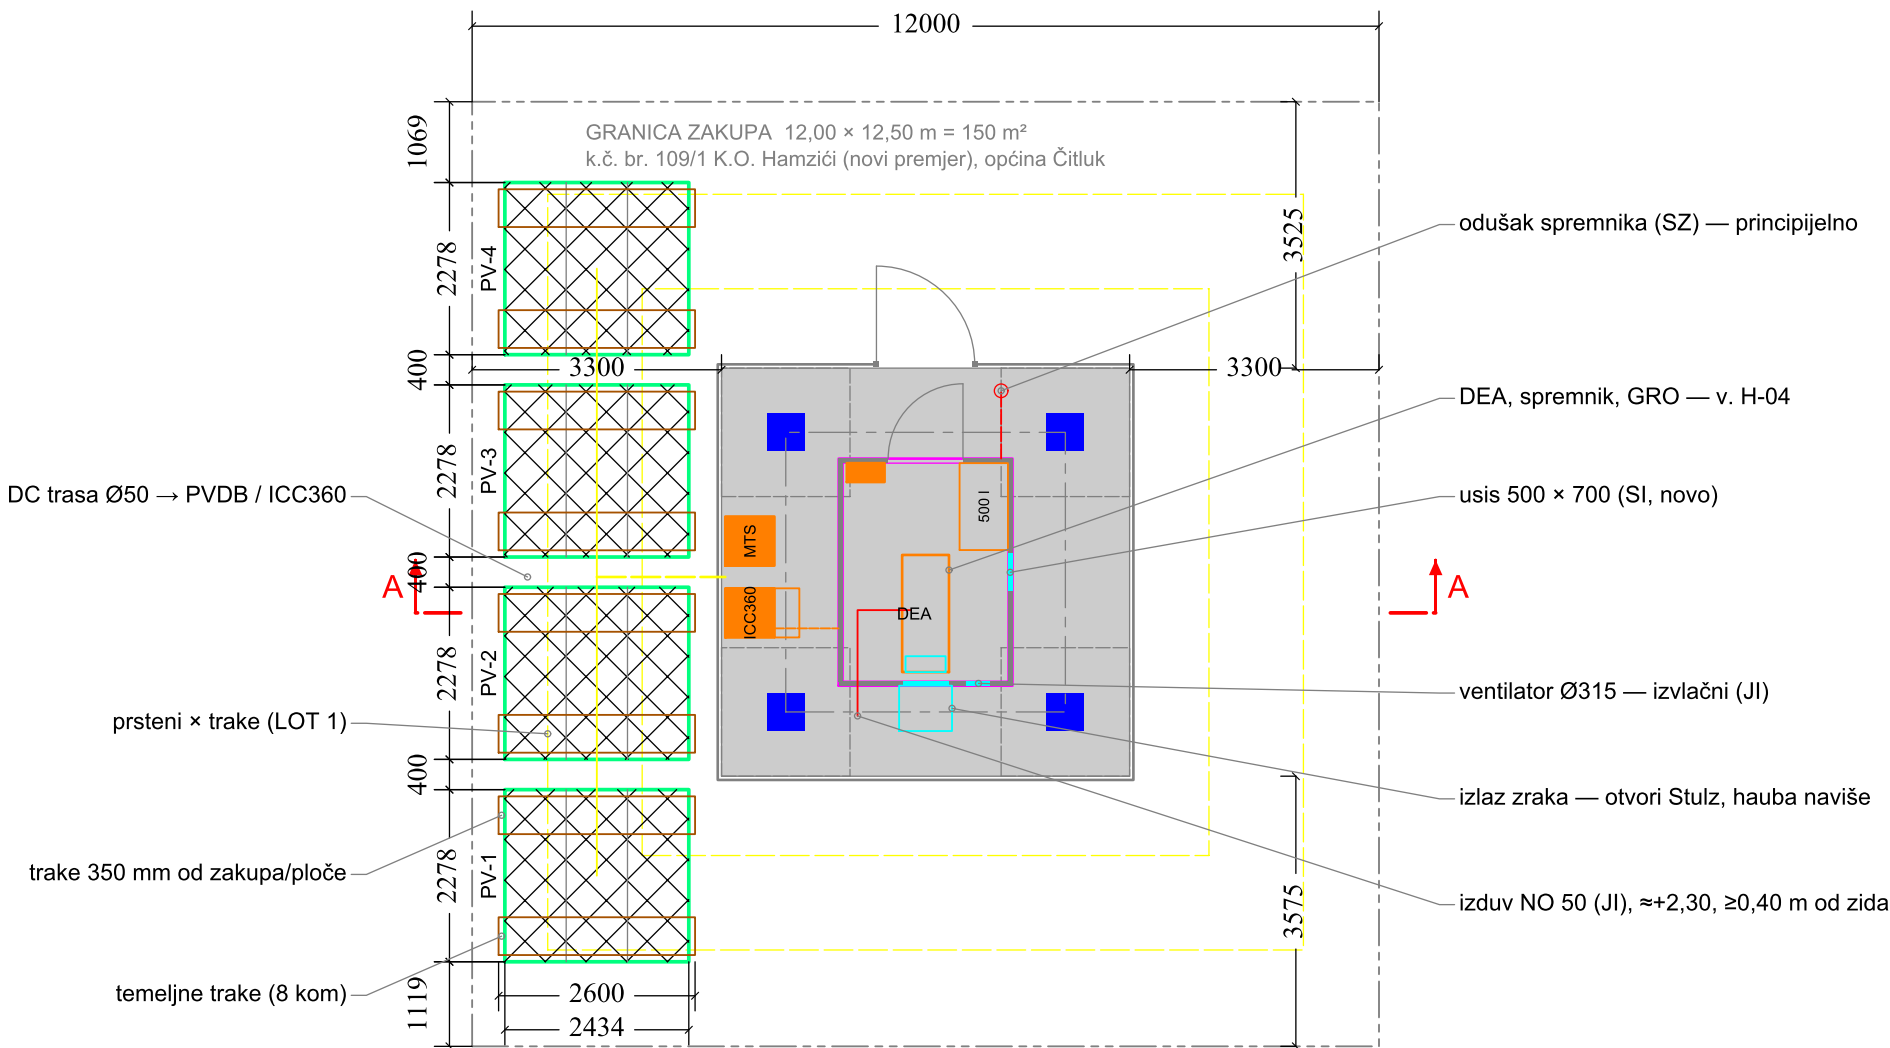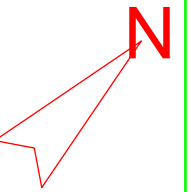

NAPOMENA — ORIJENTACIJA:
Kompleks je zakrenut 45°: vrata kontejnera i kapija gledaju na SJEVEROZAPAD (SZ), klima-uređaj Stulz na JI, FN polje na JZ. Crtež je pravougaon na kompleks (gore SZ, desno SI, dolje JI, lijevo JZ); strelica pokazuje pravi sjever. Orijentaciju potvrđuje Ponuđač obilaskom lokacije.

- NAPOMENE:**
- 1 Nosači na JUGOZAPAD (azimut 225°), nagib 45°; ivica panela +0,50 / +2,93 m.
 - 2 4 odvojena nosača u nizu: 4 × 2278 + 3 × 400 = 10312 mm, u pojasu JZ.
 - 3 Temeljne trake 500 × 2600 mm, d = 900 mm, na podložnom betonu 50 mm.
 - 4 Postojeći prsteni uzemljivača (0,8 m) ukrštaju temeljne trake — LOT 1.
 - 5 Nosač i temelji — tehničko rješenje i statički proračun Ponuđača.
 - 6 Raspored u kontejneru prema H-04.
 - 7 Ormari ICC360-HA1-C1 i MTS iza FN polja — principijelno.

LEGENDA

- FN nosači PV-1..PV-4 — po 3 × 585 Wp (1 × 3, položeno), 45°, azimut 225° (JZ) — 2 stringa × 6
- AB temeljne trake 500 × 2600 mm, d = 900 mm, razmak 1600 mm — 8 kom
- DC trasa u PEHD Ø50 (isprekidano) — od polja do PVDB uz ICC360
- DEA 18 kVA (skid), spremnik 500 l u koritu, novi GRO
- usis 500 × 700 (SI), izlaz zraka kroz otvore Stulz (JI) i haubu naviše, ventilator Ø315 (JI)
- izdub NO 50 (JI, ≈+2,30 m); odušak spremnika (SZ, isprekidano); presjek A–A
- Huawei ICC360-HA1-C1 i MTS vani na ploči (JZ), iza FN polja — principijelno



BH TELECOM d.d. SARAJEVO

Izvršna direkcija za tehnologiju i razvoj servisa

Investitor:

BH Telecom d.d. Sarajevo, Franca Lehara 7, Sarajevo

Objekat:

BS HAMZIĆI (ČITLUK) — autonomni hibridni sistem napajanja

Faza:

Tenderska dokumentacija — Prilog III

Naziv crteža:

Situacija — BUDUĆE STANJE

Projektant:

Rusmir Skopljak, dipl. ing. el.

ovjerio:

Rusmir Skopljak, dipl. ing. el.

šifra projekta:

BHT-HAMZICI-2026


razmjera:

1:100

godina / broj crteža:

2026. H-02


PRESJEK A–A (osa SZ trake nosača PV-2 — pogled prema SJEVEROZAPADU)

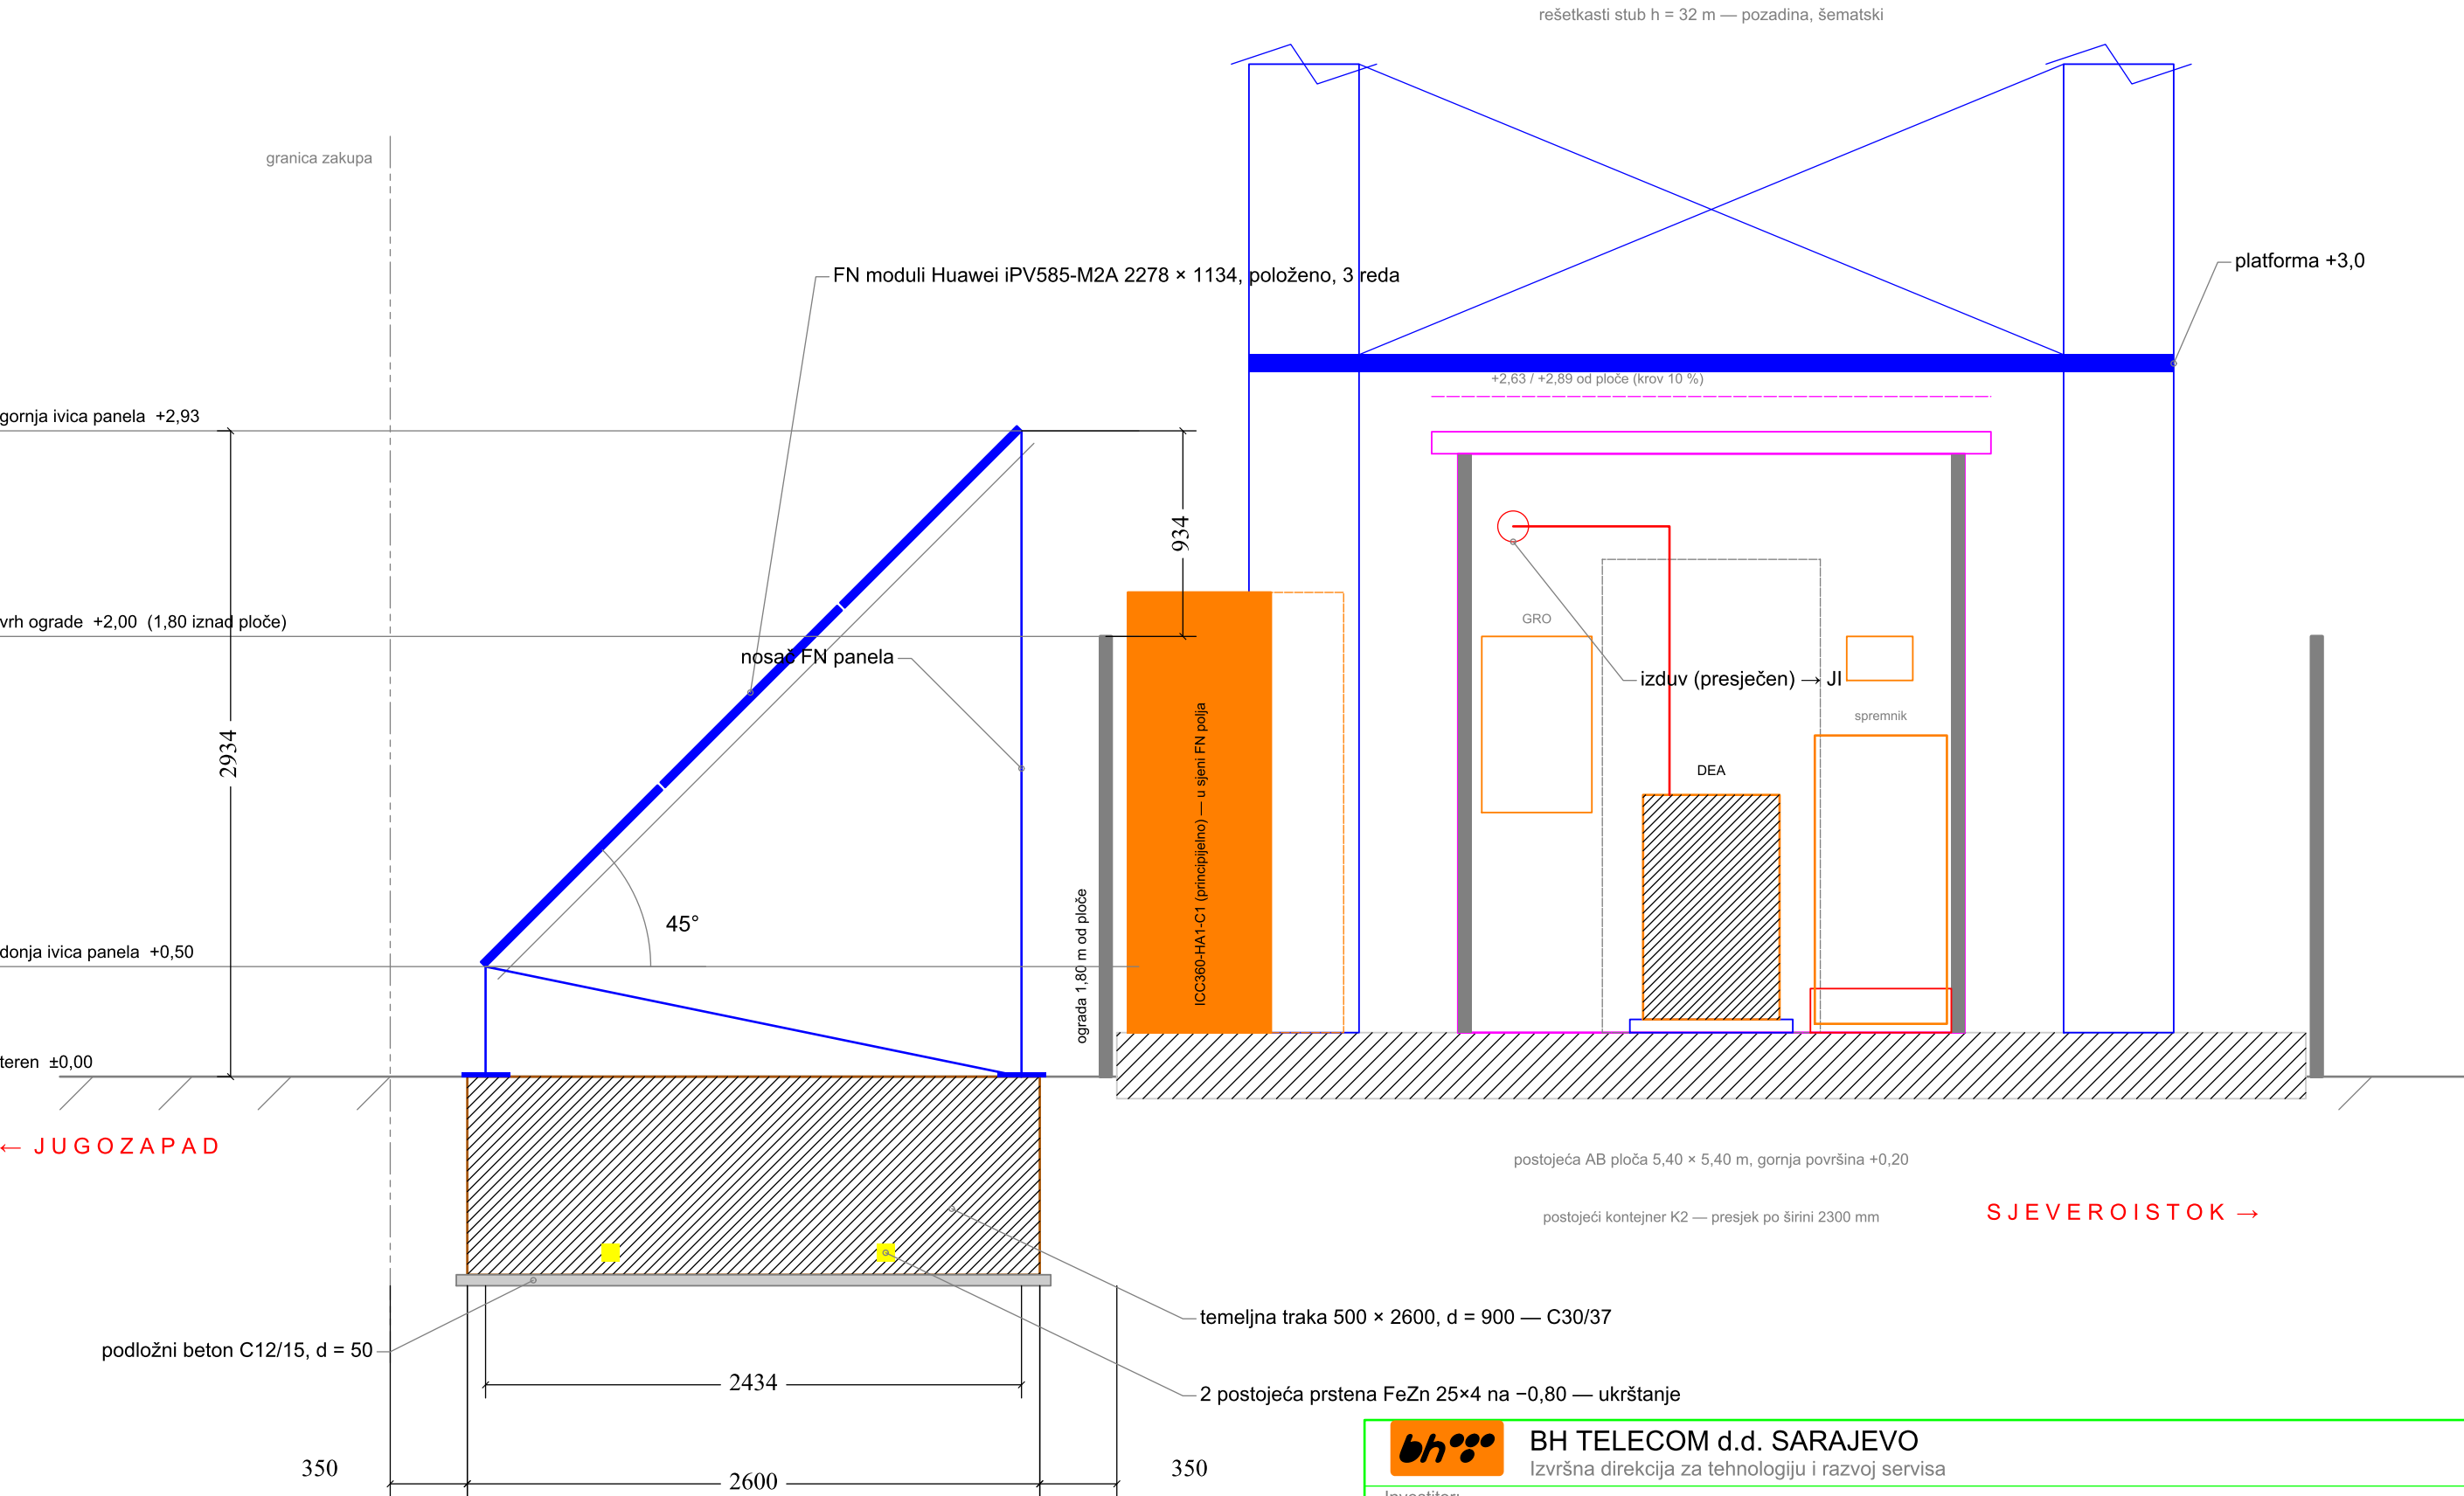

- NAPOMENE:**
- Polje: 3 reda × 1 modul 585 Wp, položeno; nagib 45°, projekcija 2434 mm; 4 odvojena nosača u nizu (H-02).
 - Dvije temeljne trake po nosaču 500 × 2600 mm, dubina 900 mm, razmak 1600 mm (druga iza ravni presjeka); beton C30/37 (XC4+XF3), armatura B500B, na podložnom betonu C12/15 d = 50 mm.
 - Kote od terena uz FN polje; teren je -0,20 m ispod ploče (04_Ograda). Donja ivica panela +0,50, gornja +2,93; vrh ograde +2,00 (1,80 m iznad ploče) — gornja ivica je 0,93 m iznad ograde.
 - Postojeći prsteni uzemljivača na 0,8 m presjecaju traku: lociranje, otkopavanje i premještanje ili premoštavanje prstena (LOT 1).
 - Trake su 350 mm od granice zakupa (JZ) i od ploče (SI); položaj presjeka na H-02.
 - Stub, platforma P I (+3,0 m), kontejner i ormari šematski; ICC360 i MTS su iza FN polja.


BH TELECOM d.d. SARAJEVO Izvršna direkcija za tehnologiju i razvoj servisa		
Investitor: BH Telecom d.d. Sarajevo, Franca Lehara 7, Sarajevo		
Objekat: BS HAMZIĆI (ČITLUK) — autonomni hibridni sistem napajanja		
Faza: Tenderska dokumentacija — Prilog III		šifra projekta: BHT-HAMZICI-2026
Naziv crteža: Presjek A–A kroz FN polje		razmjera: 1:30
Projektant: Rusmir Skopljak, dipl. ing. el.	ovjerio: Rusmir Skopljak, dipl. ing. el.	godina / broj crteža: 2026. H-03

OSNOVA — kontejner je PRAZAN; klima-uređaj Stulz se demontira

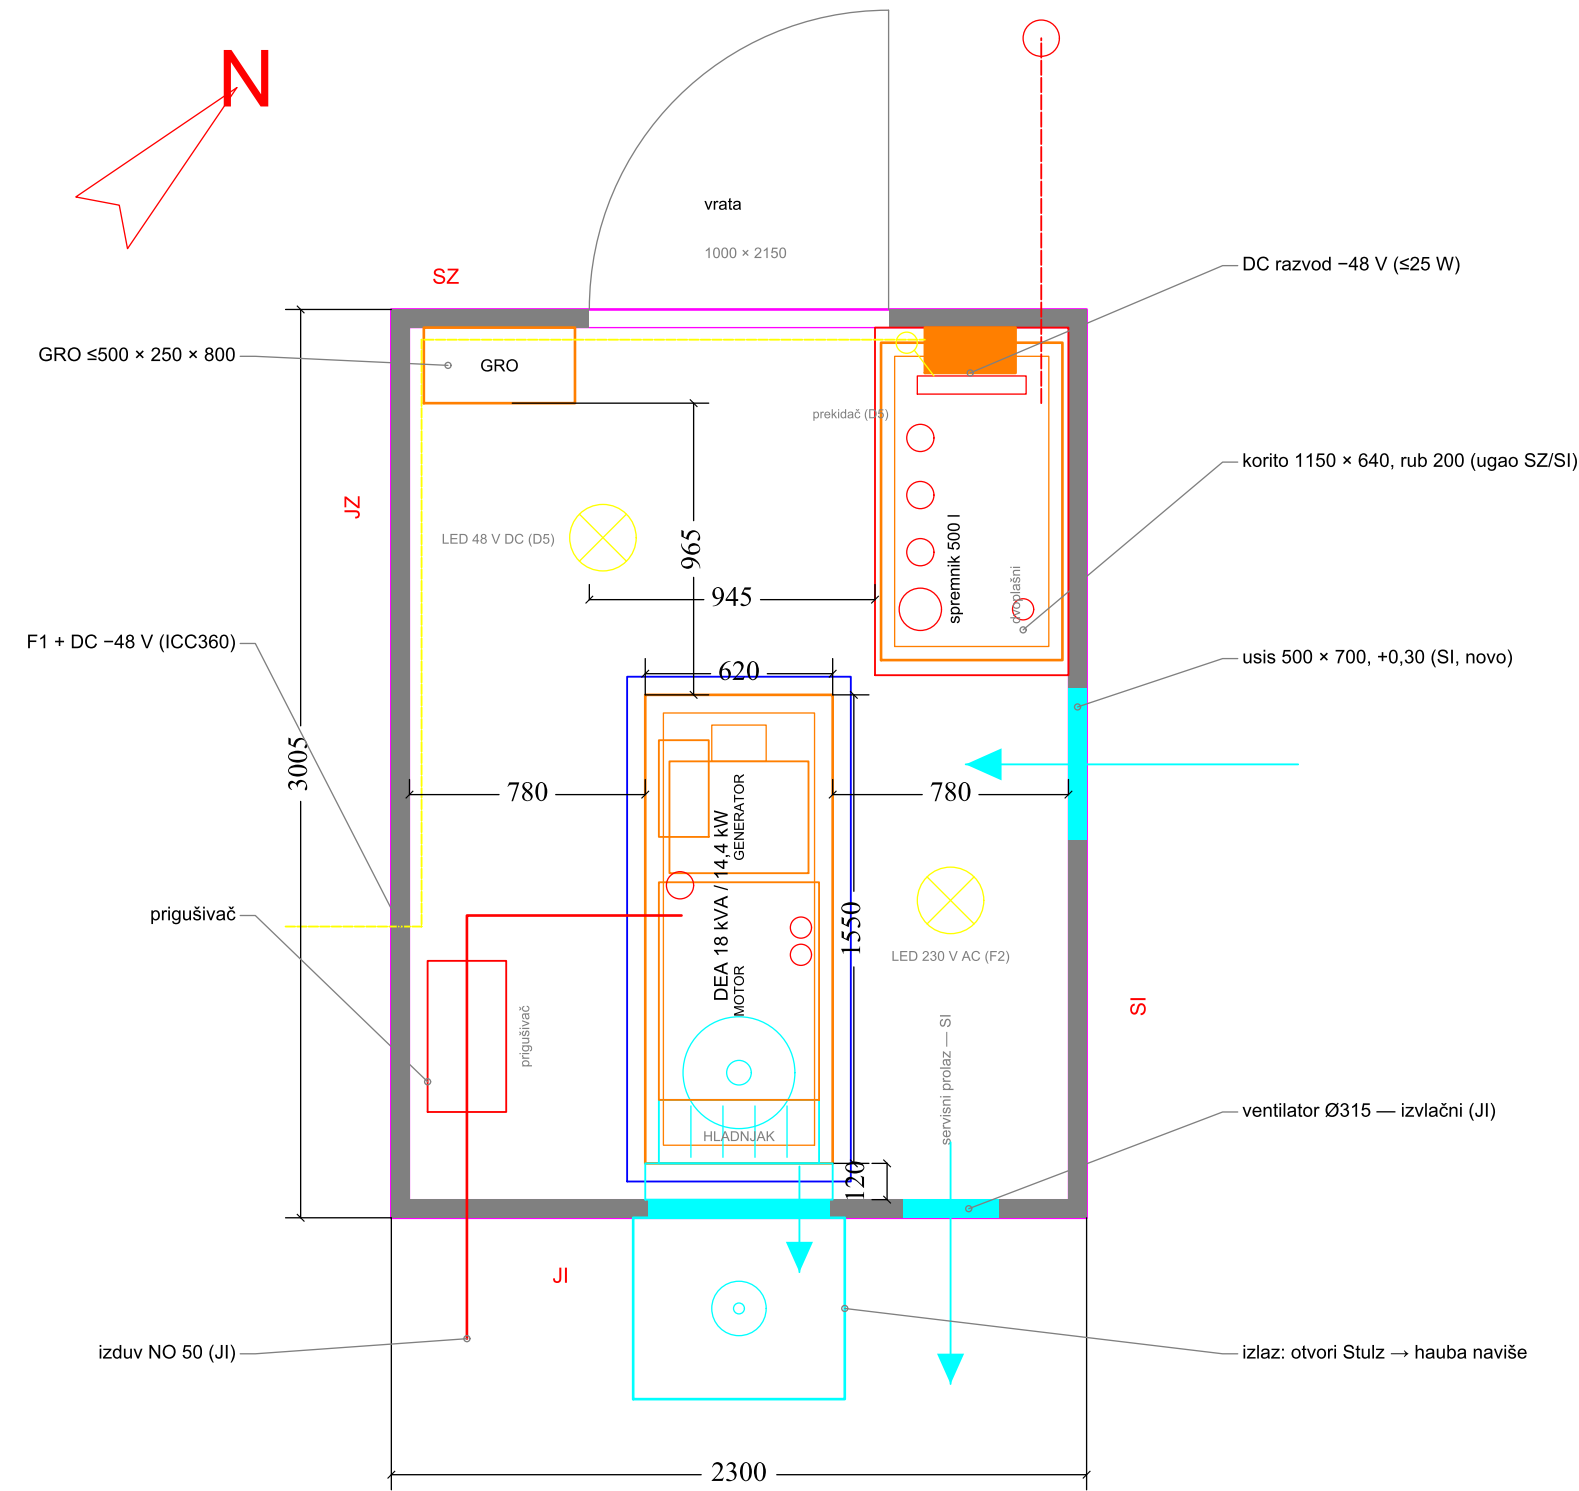

- NAPOMENE:**
- 1 DEA FG Wilson P18-6 (skid) ili ekv., 18 kVA / 14,4 kW; os SZ–JI, hladnjak JI.
 - 2 Izlaz zraka kroz postojeće otvore Stulz (sredina JI zida), $\geq 0,36 \text{ m}^2$ bruto, limeni plenum i hauba 700 × 600 — topli zrak NAVIŠE.
 - 3 Usis 500 × 700 na SI zidu (+0,30). Izdub NO 50 kroz JI zid na $\approx +2,30 \text{ m}$, ispod platforme stuba.
 - 4 GRO $\leq 500 \times 250 \times 800$ na SZ zidu; spremnik 500 l dvoplašni u koritu 1150 × 640; roštilj OBAVEZAN pod skidom i koritom.
 - 5 Servisni prolazi 780 / 780 mm i 965 mm do GRO; unos skida 620 mm kroz vrata 990 mm.
 - 6 Ventilator Ø315 (JI, izvlačni, D4) i DC razvod –48 V istočno od vrata — H-05.
 - 7 Raspored je principijelan; mjere otvora i servisne tačke potvrđuje Ponuđač na licu mjesta. Zahtjevi: Prilog I, Tačka 4.

PRESJEK 1–1 (os agregata — pogled prema SI, SZ lijevo)

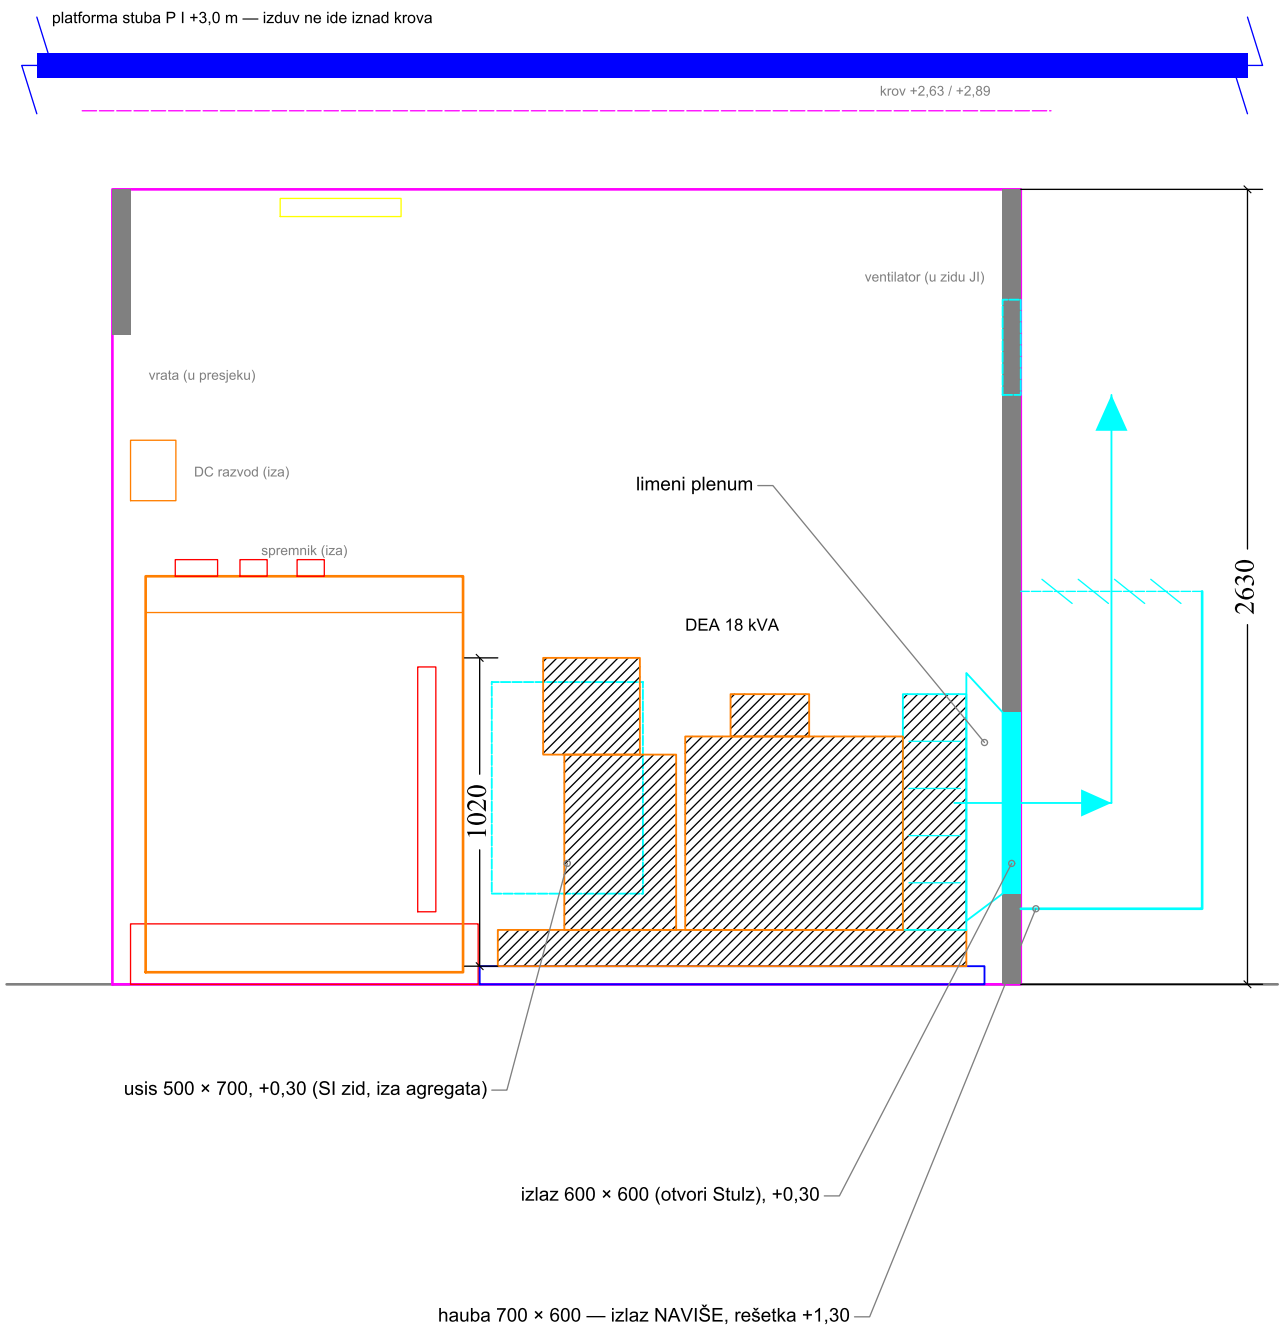

BH TELECOM d.d. SARAJEVO

Izvršna direkcija za tehnologiju i razvoj servisa

Investitor:

BH Telecom d.d. Sarajevo, Franca Lehara 7, Sarajevo

Objekat:

BS HAMZIĆI (ČITLUK) — autonomni hibridni sistem napajanja

Faza:

Tenderska dokumentacija — Prilog III

Naziv crteža:

Agregat u kontejneru — osnova i presjek 1–1

Projektant:

Rusmir Skopljak, dipl. ing. el.

ovjerio:

Rusmir Skopljak, dipl. ing. el.

šifra projekta:


BHT-HAMZICI-2026

razmjera:

1:25

godina / broj crteža:

2026. H-04

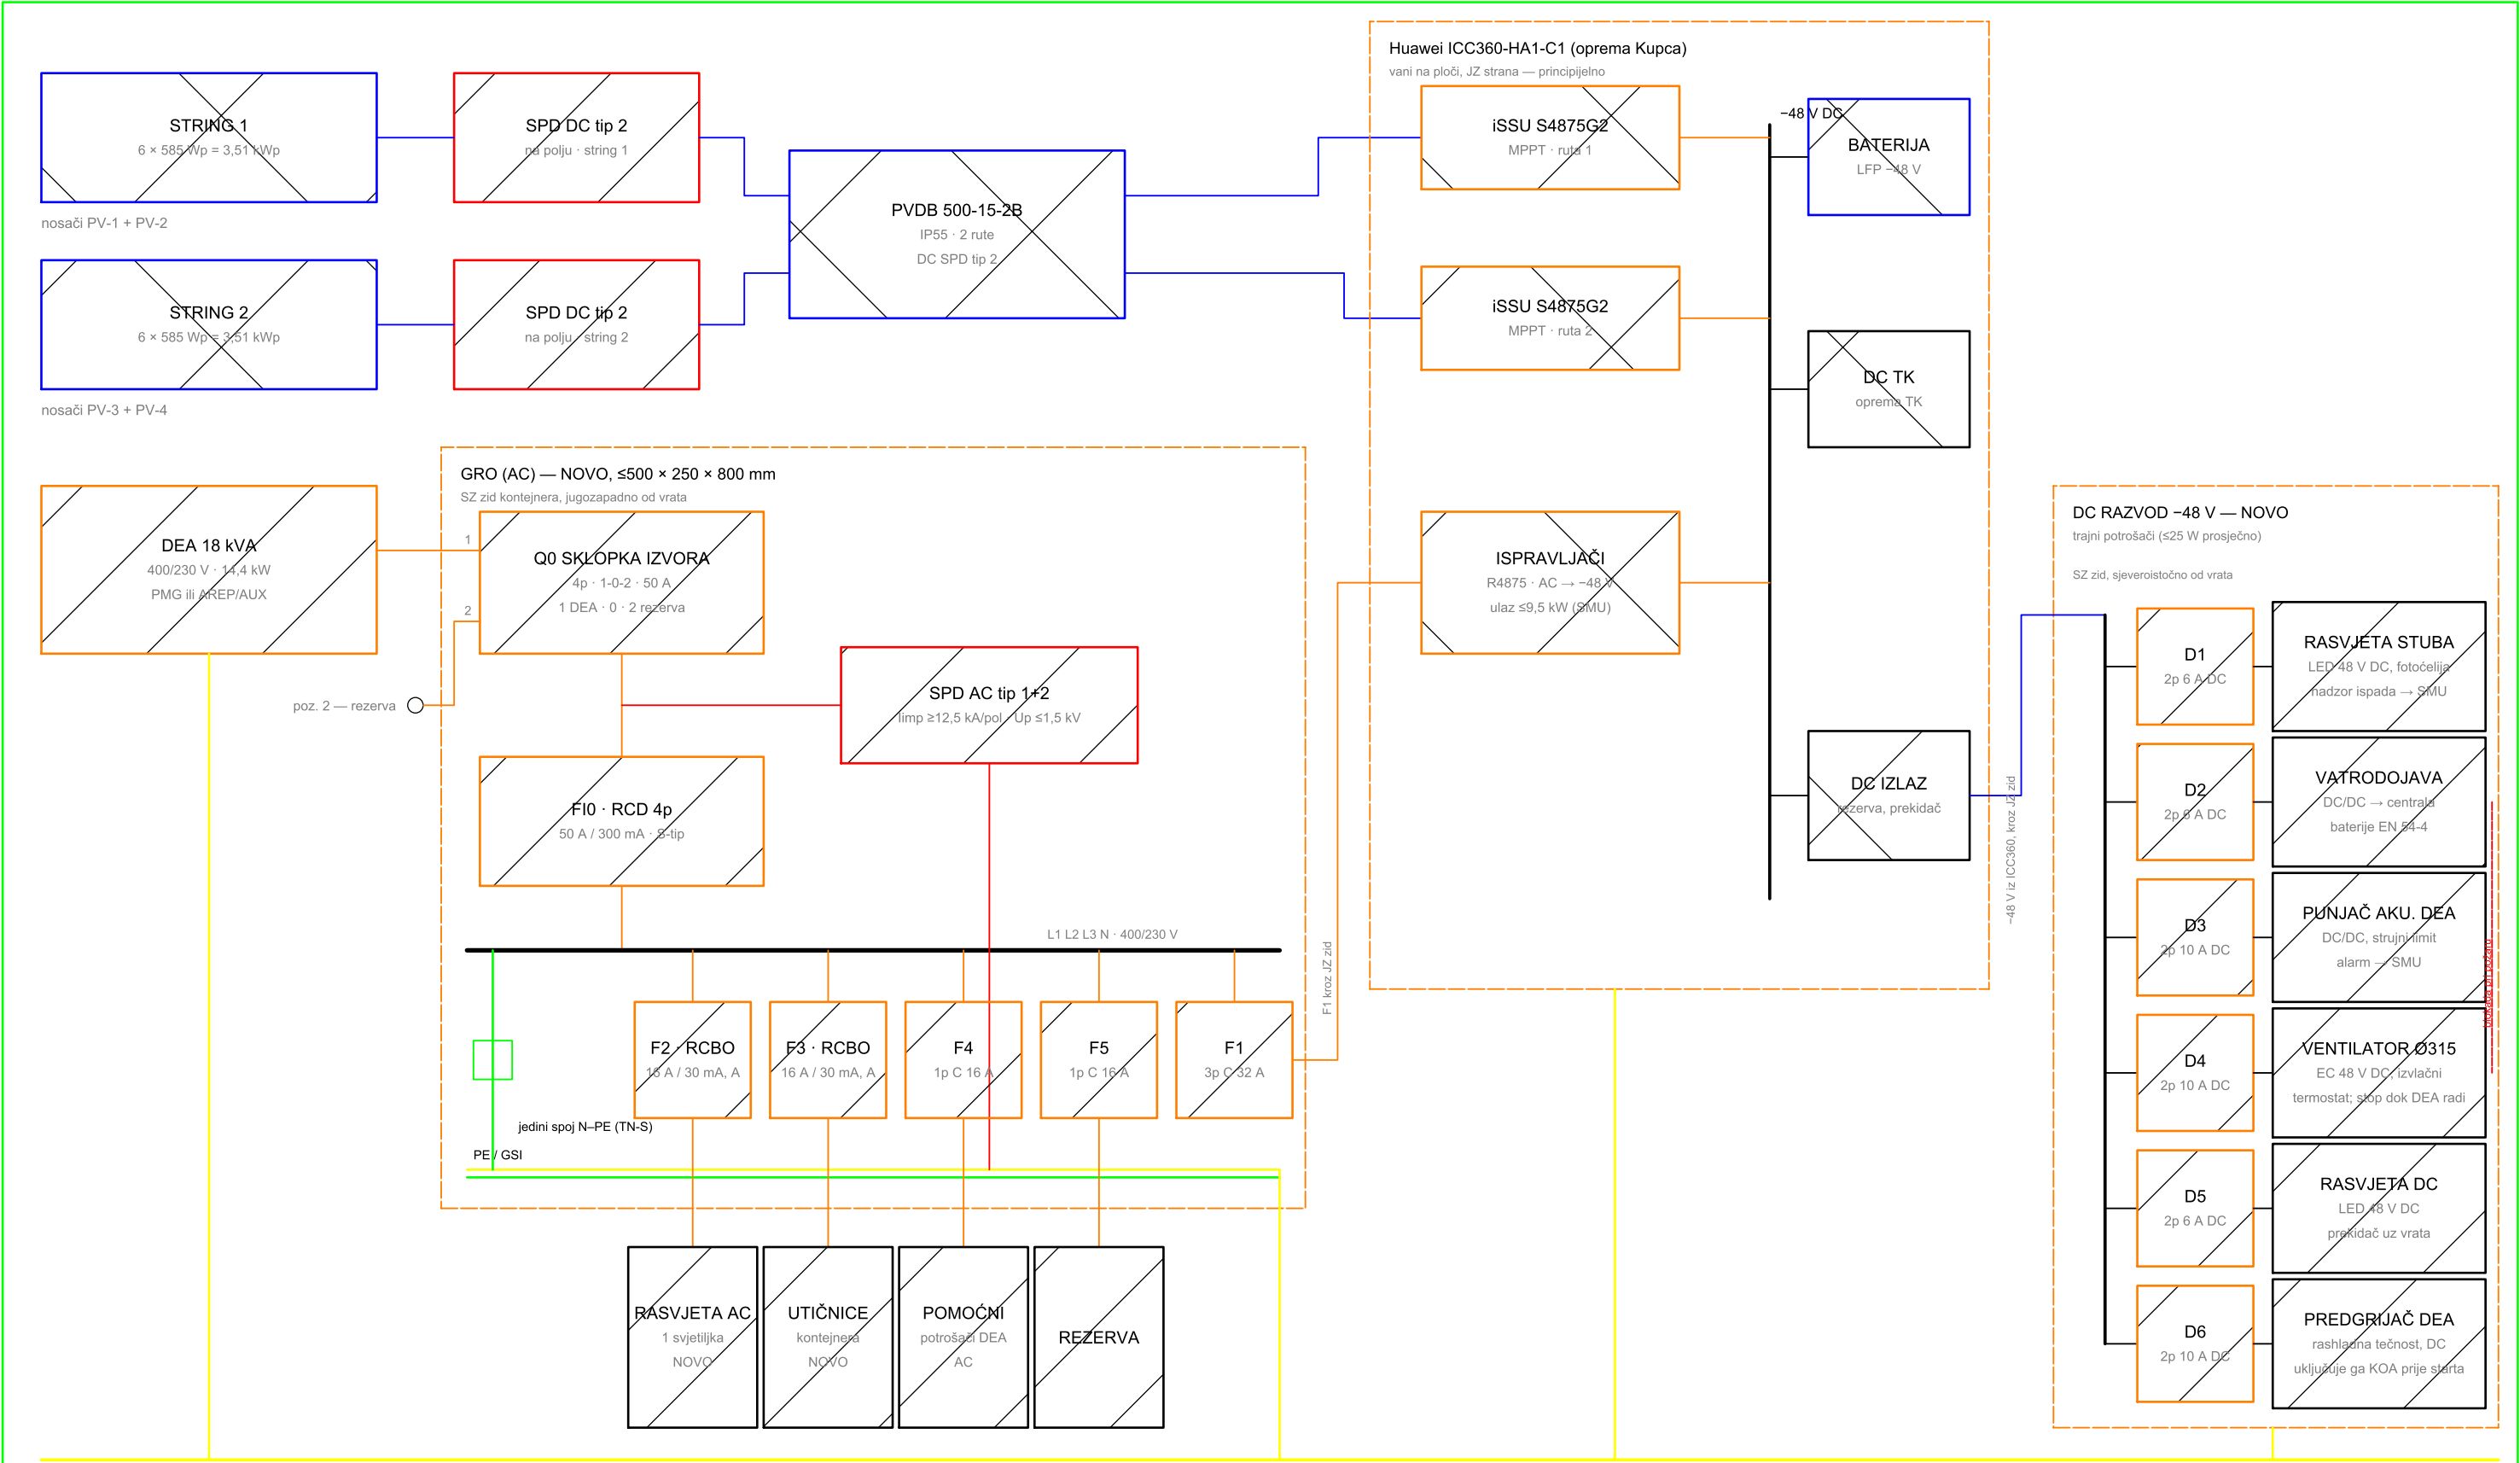

postojeći uzemljivač FeZn 25×4 (2 prstena na 0,8 m + temelji stuba) · R ≤ 10 Ω · nosači FN vezani Cu užetom 50 mm² preko bimetalnih spojeva

NAPOMENE:

- DEA je jedini AC izvor; izvodi GRO su pod naponom samo dok DEA radi. Trajni potrošači su na DC razvodu -48 V.
- TN-S: jedini spoj N-PE je u novom GRO; R ≤ 10 Ω. Odvodnici: AC tip 1+2, DC tip 2 po stringu, signalni vodovi EN 61643-21.
- DEA sa nezavisnom pobudom PMG ili AREP/AUX (≥3 × In ≈ 78 A, ≥10 s); RCD 50 A / 300 mA S-tip je obavezan.
- Ulaz ispravljača ograničen na 9,5 kW dok radi DEA (SMU). Klima-uređaj Stulz se demontira — nema izvoda za klimatizaciju.
- FN: 12 modula = 2 stringa × 6; PVDB ima 2 rute → 2 × iSSU S4875G2. Požar: STOP DEA i isključenje ventilatora.
- Nazivne struje F4–F5 i D1–D6 su orijentacione; presjeke i selektivnost potvrđuje Izvođač. ICC360 — principijelno.

isporuka i montaža Izvođača (DEA, GRO, DC razvod -48 V)

oprema Kupca (FN, PVDB, iSSU, baterije, ICC360)



BH TELECOM d.d. SARAJEVO

Izvršna direkcija za tehnologiju i razvoj servisa

Investitor:

BH Telecom d.d. Sarajevo, Franca Lehara 7, Sarajevo

Objekat:

BS HAMZIĆI (ČITLUK) — autonomni hibridni sistem napajanja

Faza:

Tenderska dokumentacija — Prilog III

Naziv crteža:

Jednopolna šema — novi GRO i DC razvod -48 V

Projektant:

Rusmir Skopljak, dipl. ing. el.

ovjerio:

Rusmir Skopljak, dipl. ing. el.

šifra projekta:

BHT-HAMZICI-2026


razmjera:

—

godina / broj crteža:

2026. H-05

POGLED SA JUGOZAPADA (pravac gledanja azimut 45°)

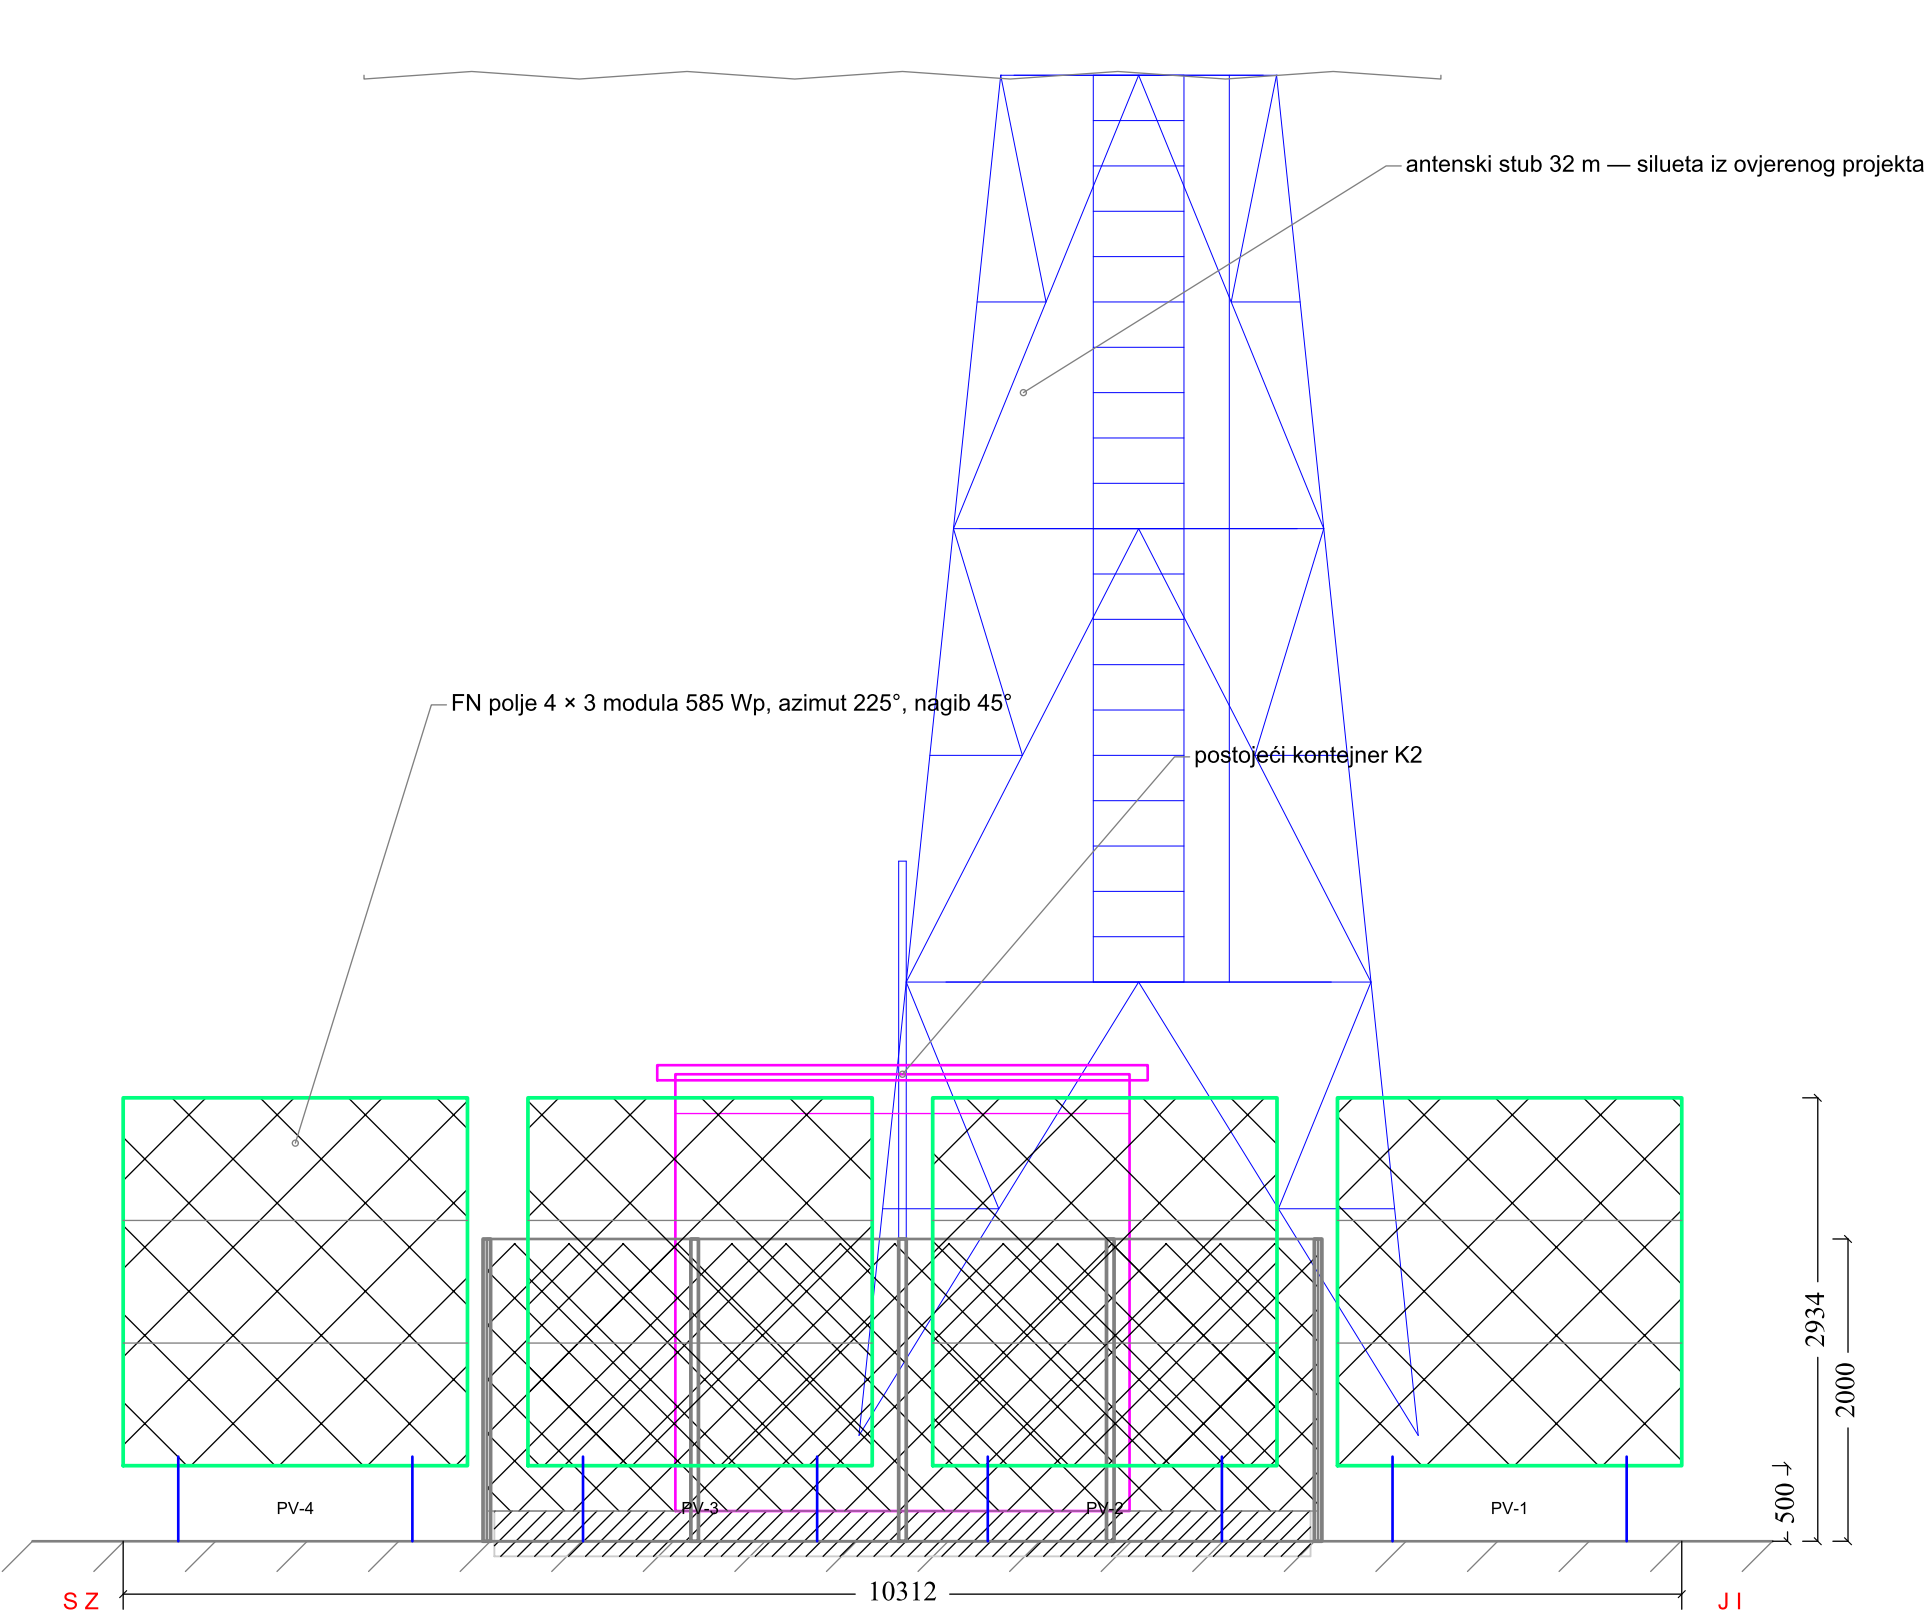



LEGENDA

- LOT 1 — FN moduli i nosači (ispred ograde, JZ)
- postojeći antenski stub — silueta iz ovjerenog projekta
- postojeći kontejner K2 na postojećoj ploči
- postojeća ograda 1,80 m iznad ploče

NAPOMENE:


- Prava ortogonalna elevacija u pravcu azimuta 45°; visine i širine su mjerljive.
- Paneli gledaju u posmatrača pod 45°, pa se po visini vide skraćeno: +0,50 do +2,93 m od terena.
- Teren uz FN polje je -0,20 m ispod ploče; ograda je 2,00 m iznad terena.
- Stub je prikazan do +9,50 m i prekinut; h = 32 m prema ovjerenom projektu (list 462 — 01_Dispozicija S32 m).
- Zahtjevi: Prilog I, Tačke 3 i 4.

bh BH TELECOM d.d. SARAJEVO Izvršna direkcija za tehnologiju i razvoj servisa		
Investitor: BH Telecom d.d. Sarajevo, Franca Lehara 7, Sarajevo		
Objekat: BS HAMZIĆI (ČITLUK) — autonomni hibridni sistem napajanja		
Faza: Tenderska dokumentacija — Prilog III		šifra projekta: BHT-HAMZICI-2026
Naziv crteža: Pogled sa JUGOZAPADA — kompleks sa FN poljem		razmjera: 1:50
Projektant: Rusmir Skopljak, dipl. ing. el.	ovjerio: Rusmir Skopljak, dipl. ing. el.	godina / broj crteža: 2026. H-06

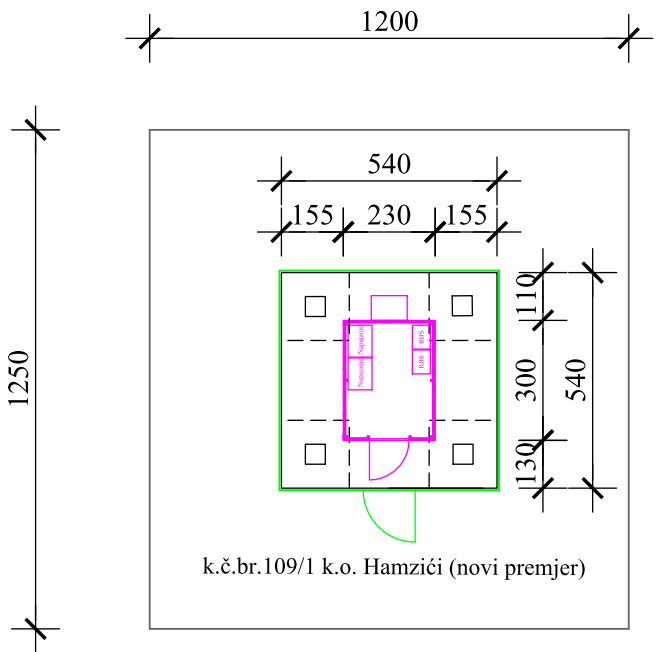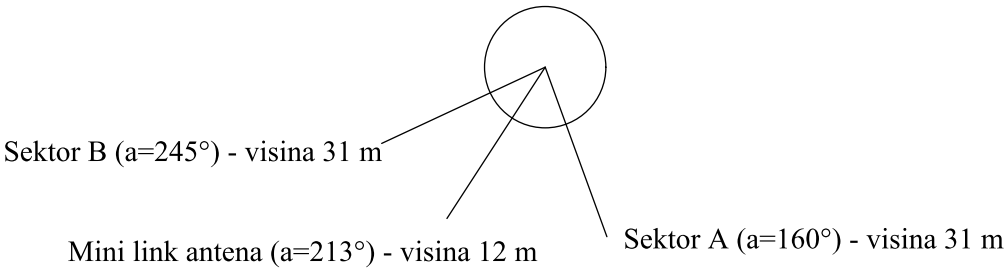


Investitor: BH TELECOM d.d.		Objekat: Infrastruktura bazne stanice mobilne mreže		bh telecom Dioničko društvo Sarajevo
Glavni projekat Knjiga 1/1	Faza: A	godina: 2017.	šifra projekta: GP-BS-10472-291	
Naziv crteža: Situacija		razmjera: 1:200	broj crteža: 1 - (85/131)	ovjerio:  Projektant:Dženadin Mušinić,d.i.g.

OSNOVA - OGRADA BAZNE STANICE

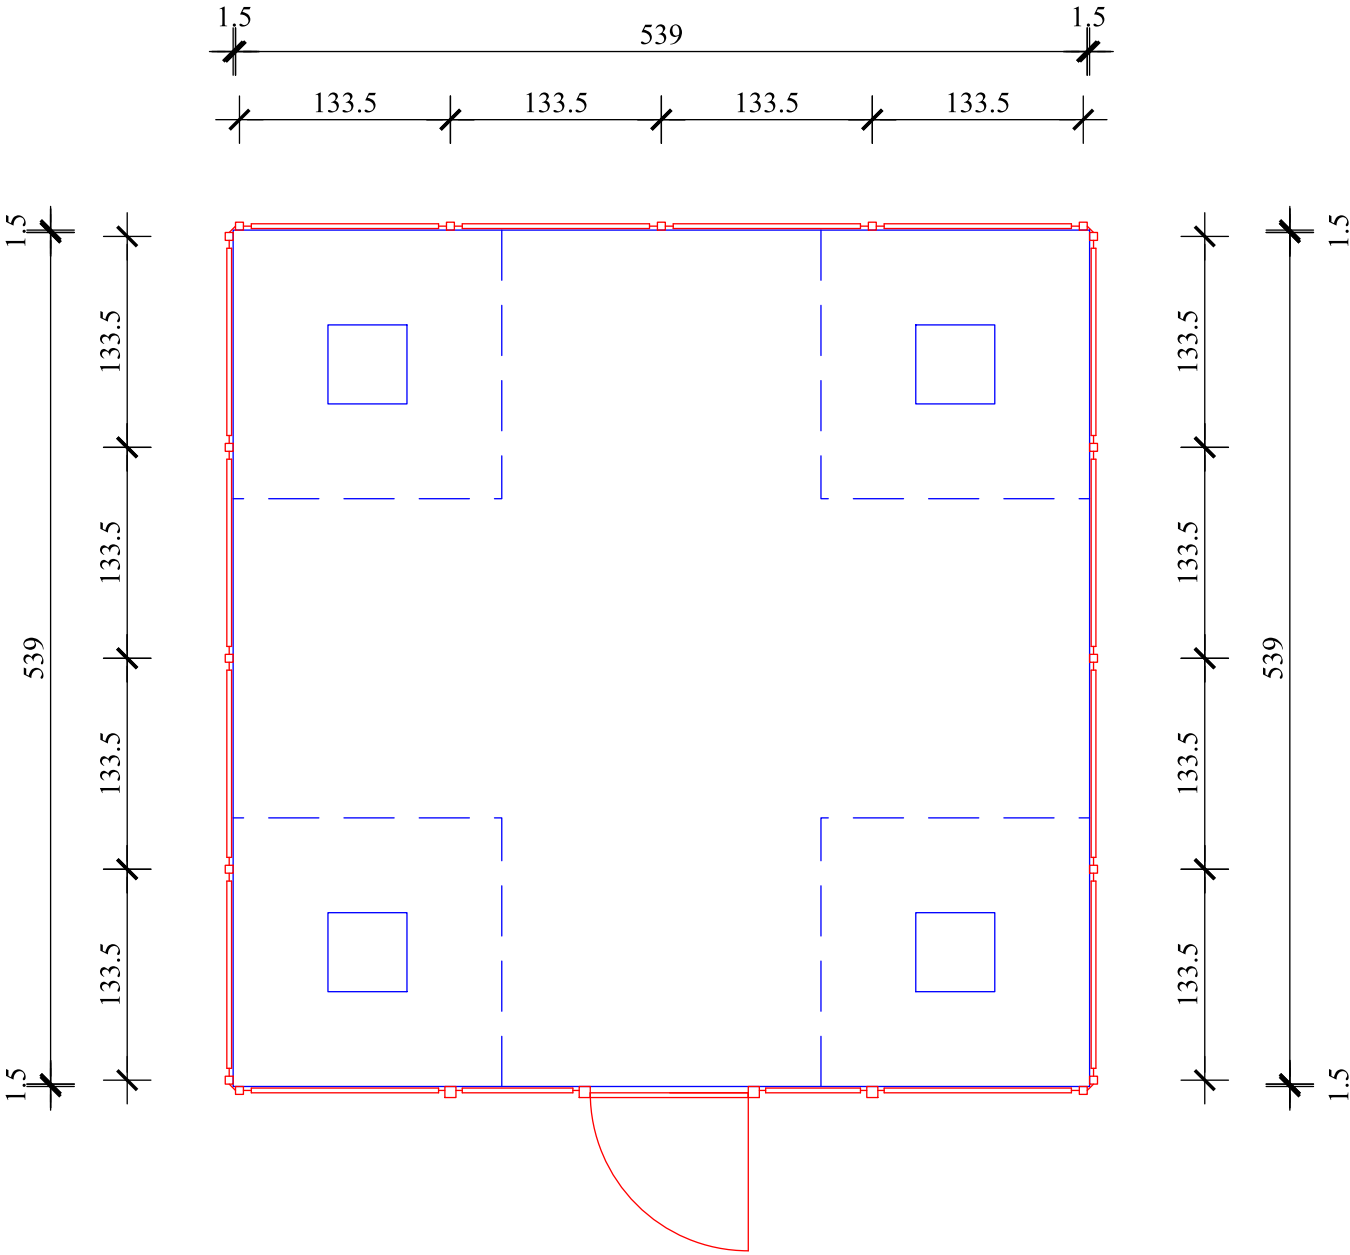


POGLED - OGRADA BAZNE STANICE

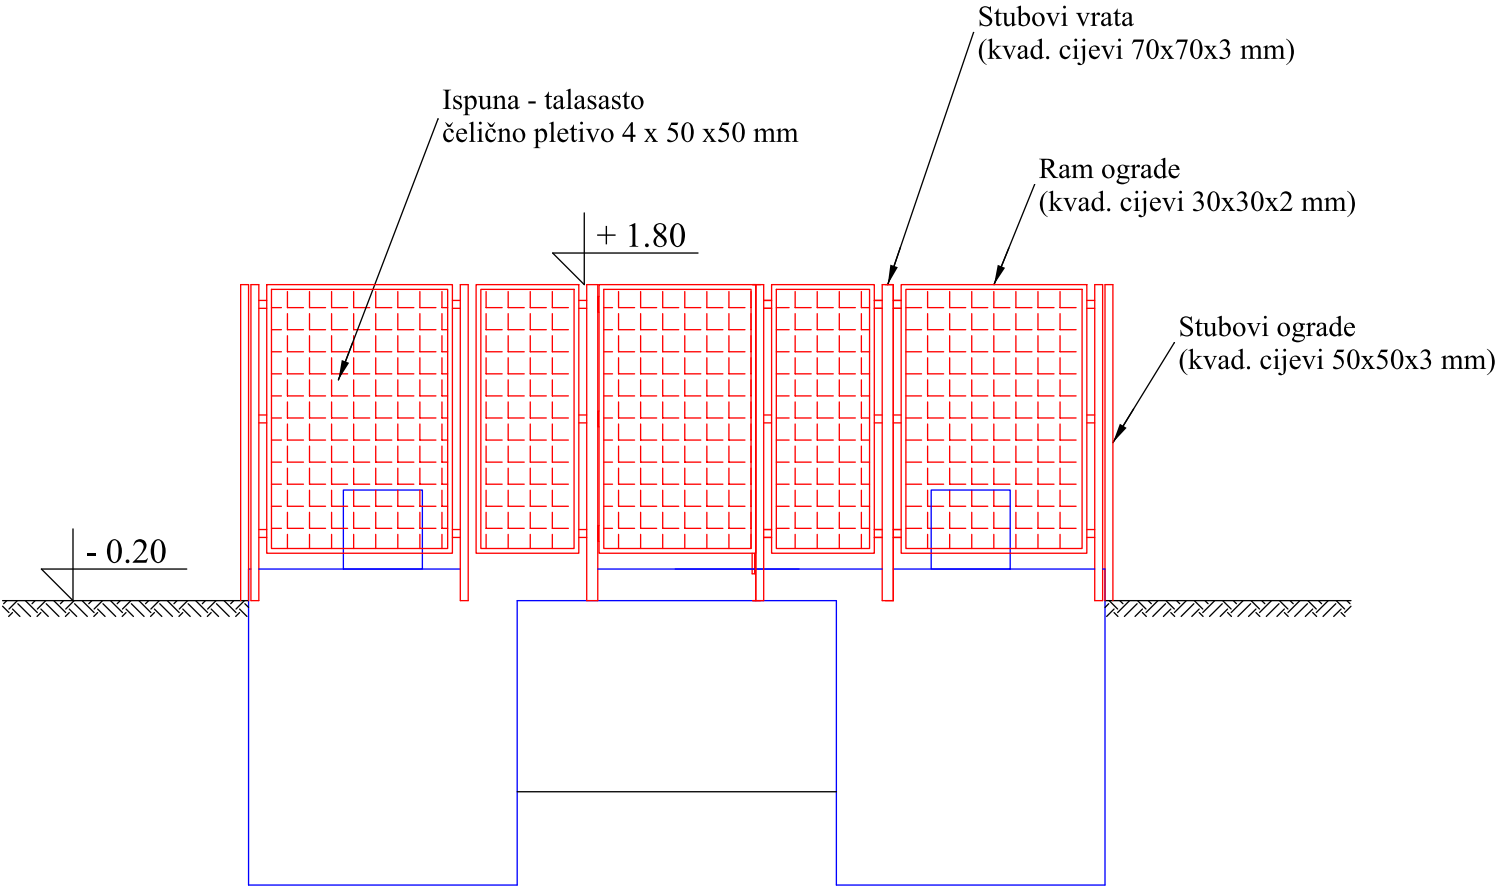


Stubovi - Č.0361
Antikoroziorna zaštita - vruće cinčanje prema
Pravilniku o zaštiti čeličnih konstrukcija
od korozije (Sl. list SFRJ 32/70)

Investitor: BH TELECOM d.d.		Objekat: Infrastruktura bazne stanice mobilne mreže		 Dioničko društvo Sarajevo	
Glavni projekat Knjiga 1/1	Faza: A	godina: 2017.	šifra projekta: GP-BS-10472-291		
Naziv crteža: Ograda bazne stanice			razmjera: 1:50	broj crteža: 4 - (88/131)	ovjerio: Projektant:Dženadin Mušinović,d.i.g.

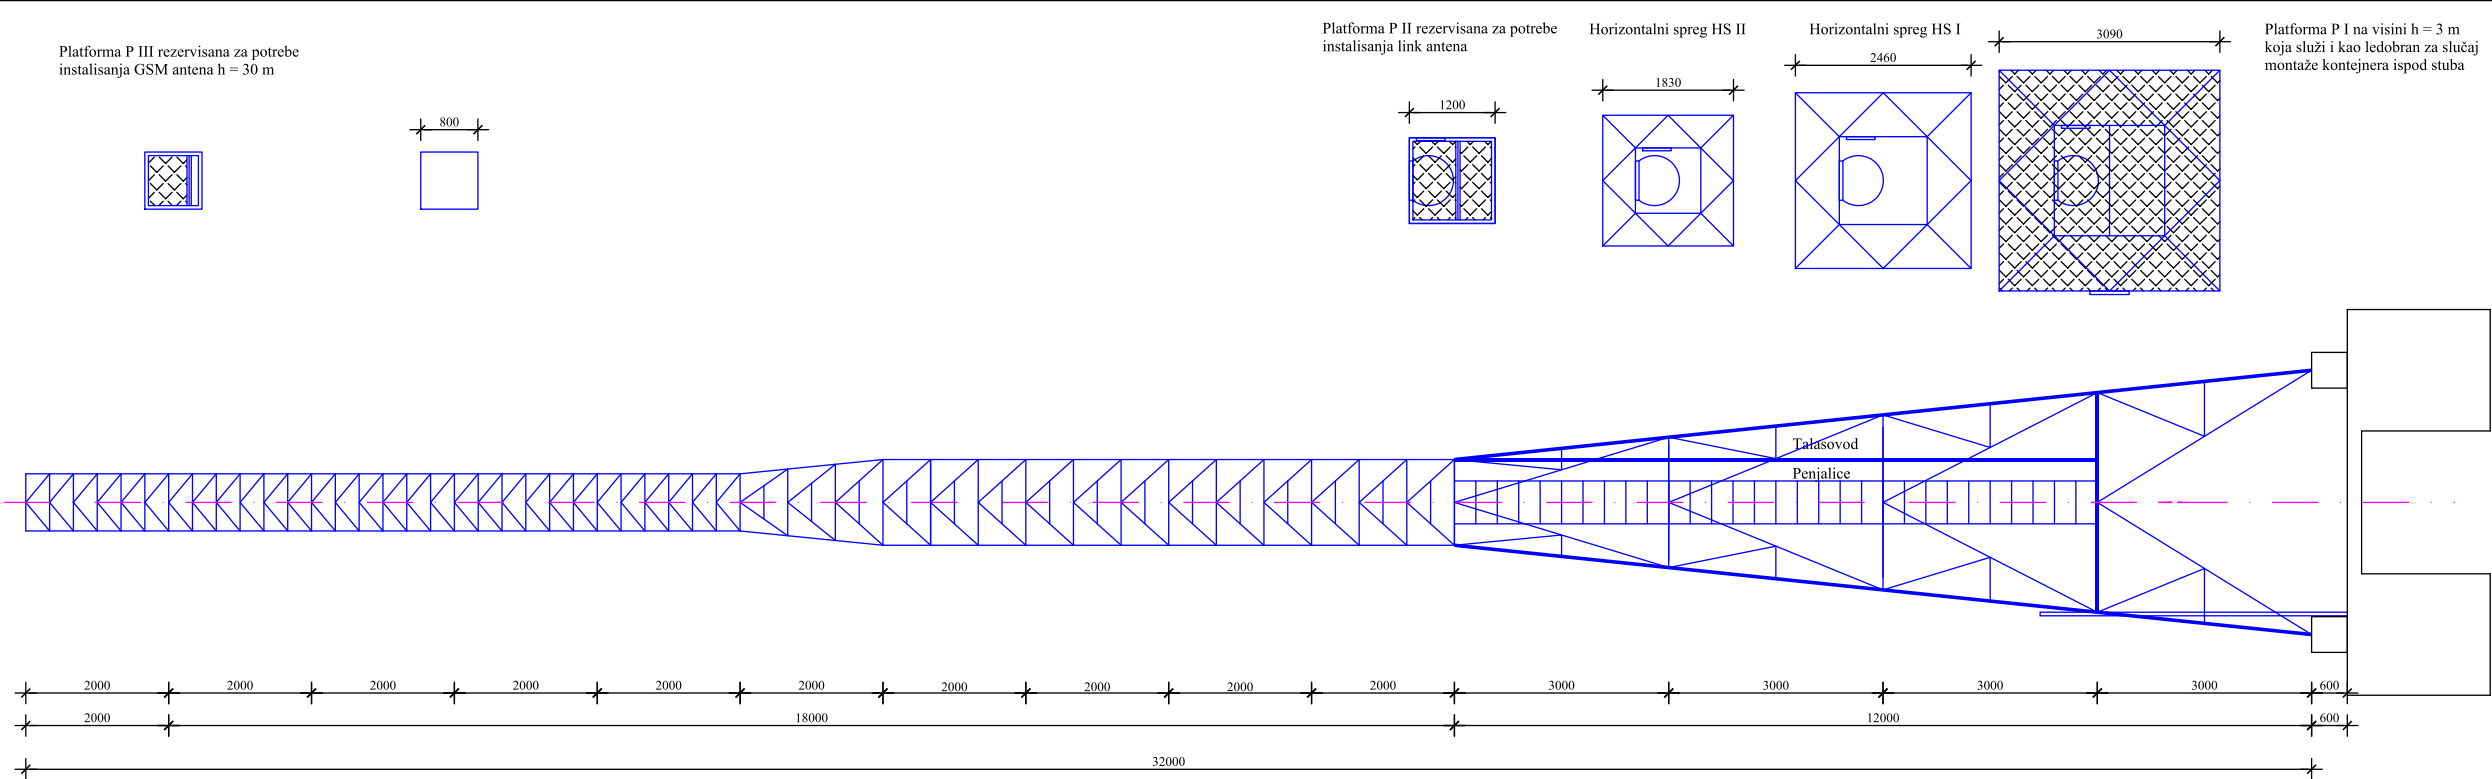

Ø 28	Ø 38	Ø 38	L 90x90x11	L 90x90x11	L 90x90x11	L 90x90x11	POJASNICI
Ø 12	Ø 16	Ø 16	L 50x50x5	L 50x50x5	L 60x60x6	L 60x60x6	HORIZONTALE
Ø 12	Ø 16	Ø 16	L 70x70x6	L 70x70x6	L 80x80x8	L 80x80x8	DIJAGONALE
-	-	-	L 40x40x4	L 40x40x4	L 50x50x5	L 50x50x5	SEKUND. ISPUNA
crvena	bijela	crvena	bijela	crvena	bijela	crvena	boja segmenta
S 8	S 8	S 8	S 8	S 8	S 12 / S 8	S 12	oznaka segmenta

Investitor: BH TELECOM d.d.	Objekat: Infrastruktura bazne stanice mobilne mreže	bh telecom	
Glavni projekat Knjiga 1/1	Faza: K	godina: 2017.	sifra projekta: GP-BS-10472-291
Naziv crteža: Dispozicija - Antenski stub h=32 m		razmjera: 1:50	broj crteža: 1 - (90/131)
		ovjerio: [Signature]	Projektant: Dženanin Mustinović.d1.g




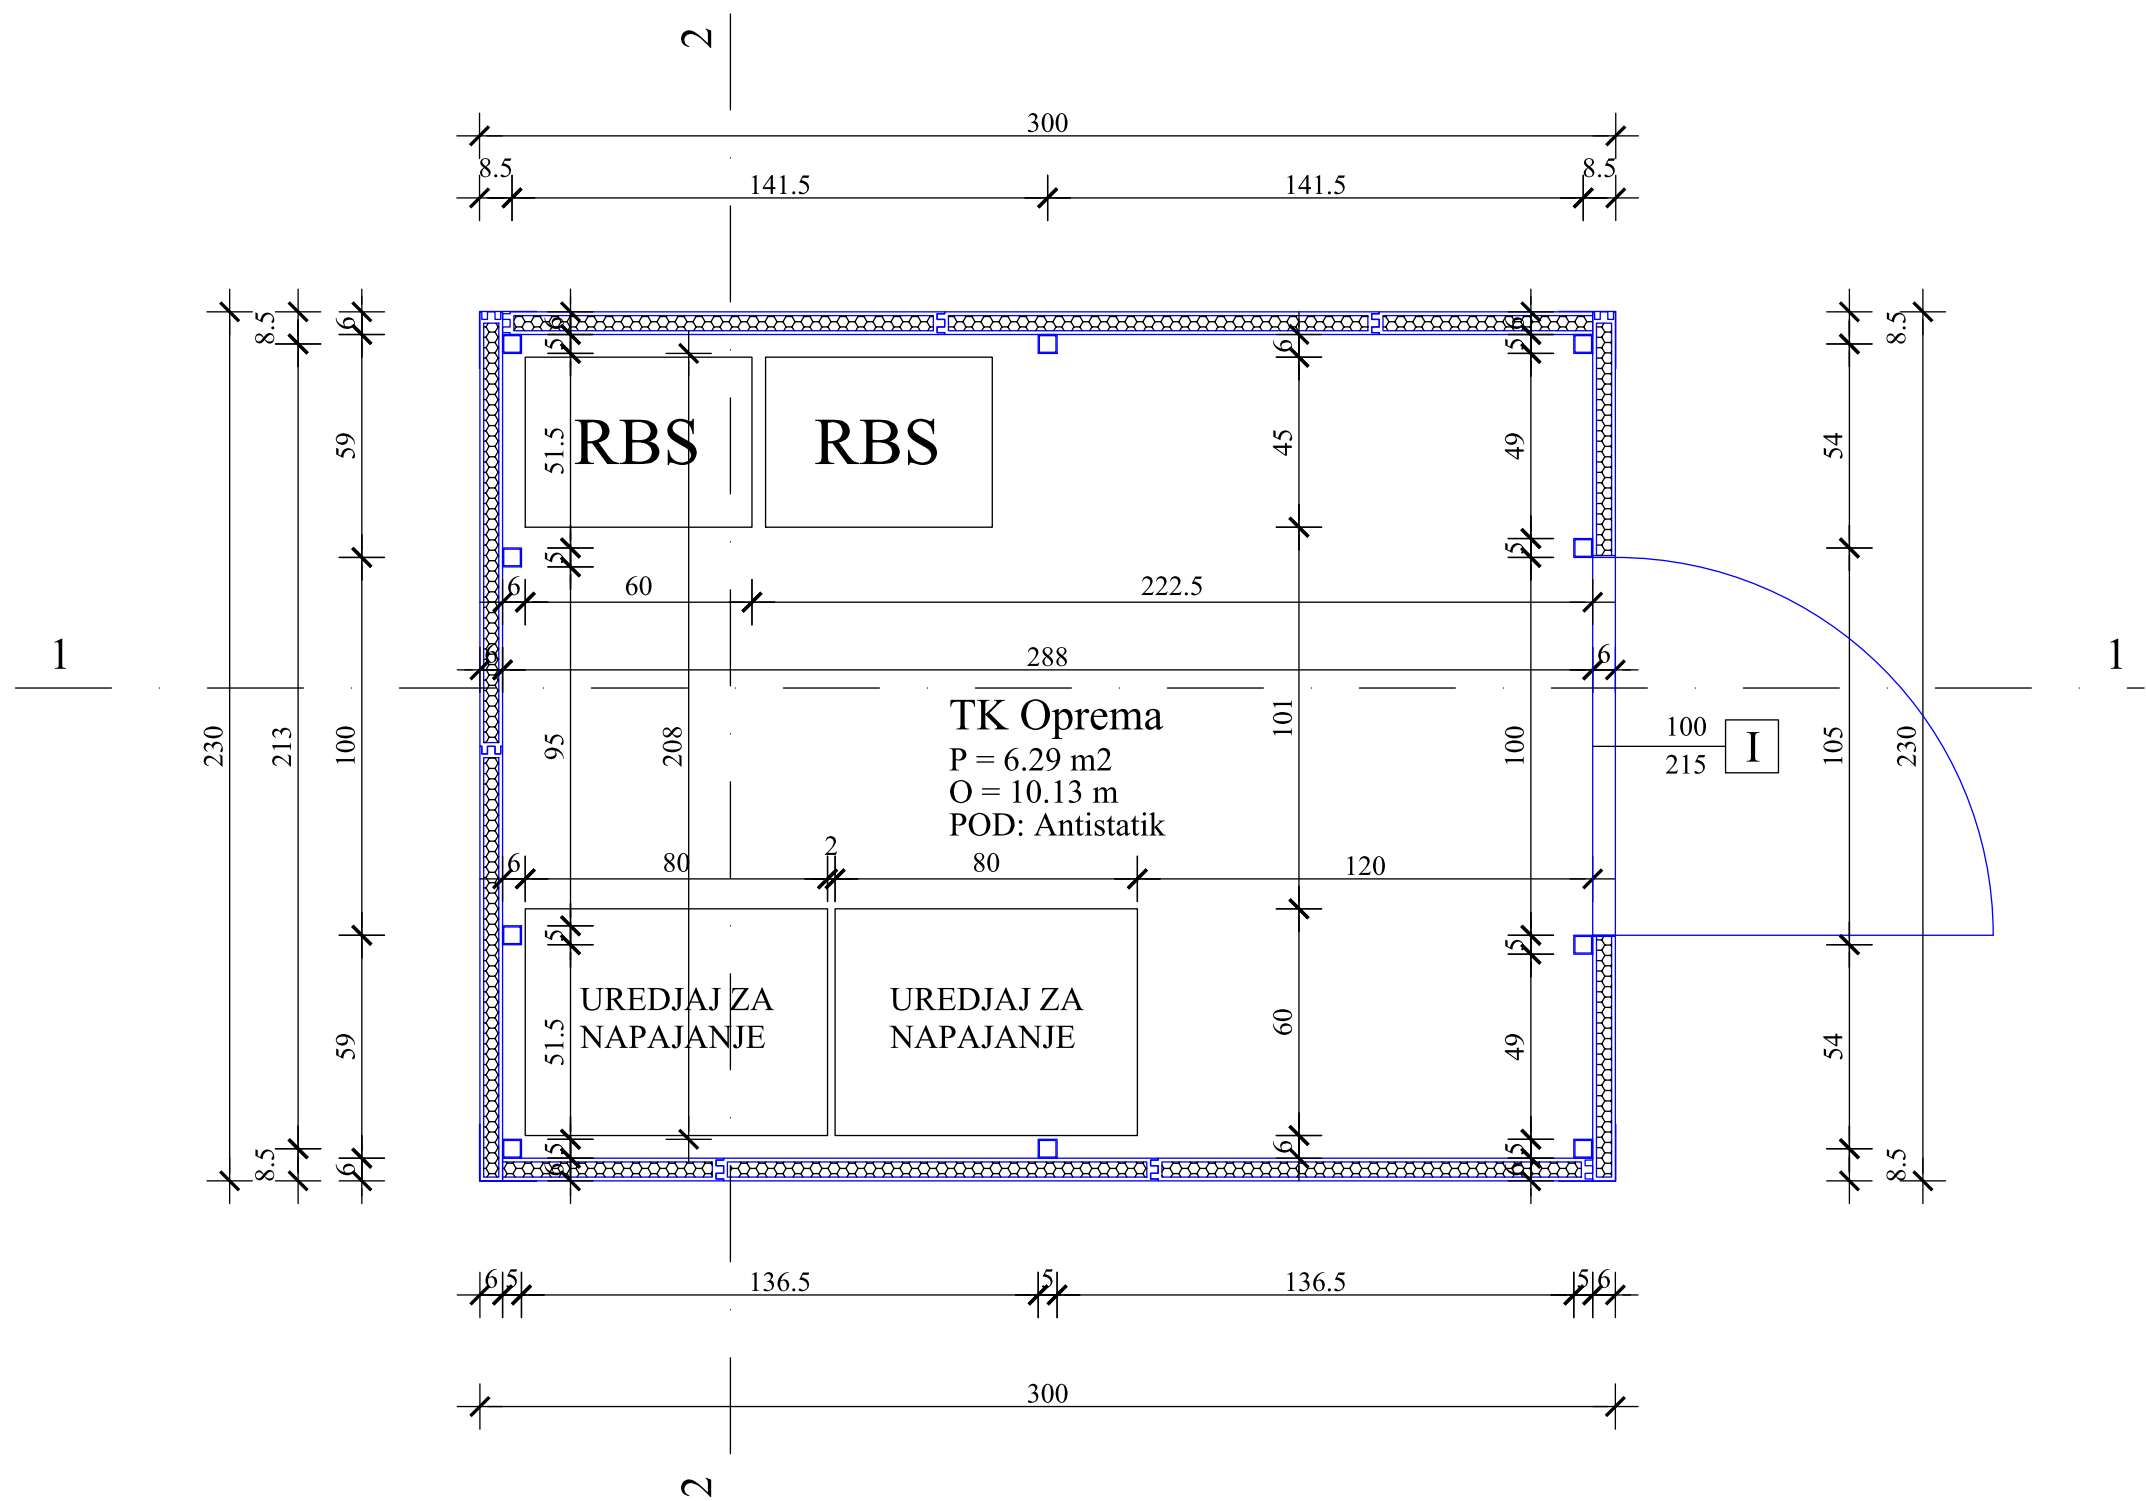


Investitor: BH TELECOM d.d.		Objekat: Infrastruktura bazne stanice mobilne mreže	
Glavni projekat Knjiga 1/1	Faza: A	godina: 2017.	šifra projekta: GP-BS-10472-291
Naziv crteža: Osnova objekta za smještaj GSM opreme		razmjera: 1:20	broj crteža: 1 - (106/131)
		ovjerio: <i>[Signature]</i>	Projektant: Mušinić Dženadin, d.i.g





Dioničko društvo Sarajevo

Kontejner K2 — fasade — preuzeto iz ovjerenog projekta GP-BS-10472-291 (2017), samo kao podloga. Crtež iz 2017. zakrenut je ≈180° prema stanju na terenu; vrata i kapija gledaju na SZ (vidi H-01).

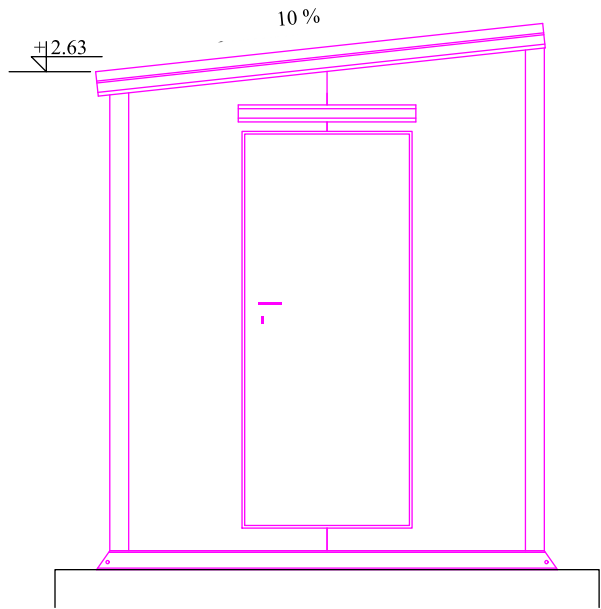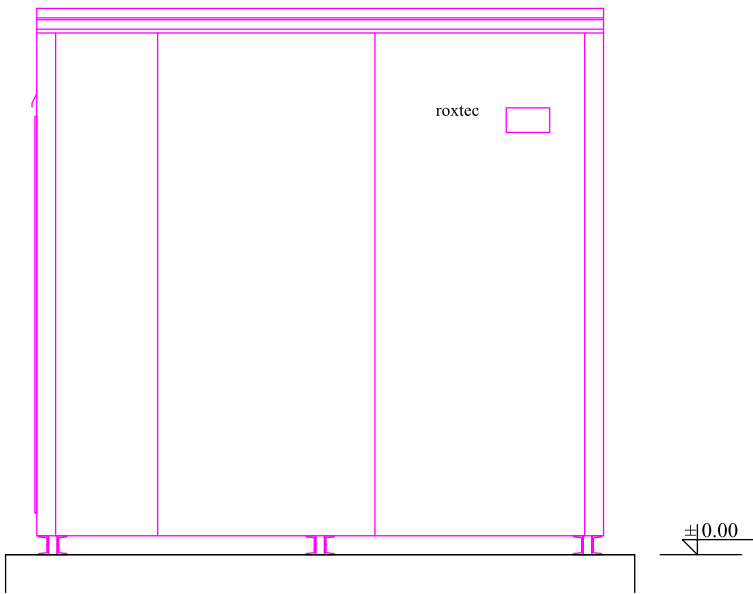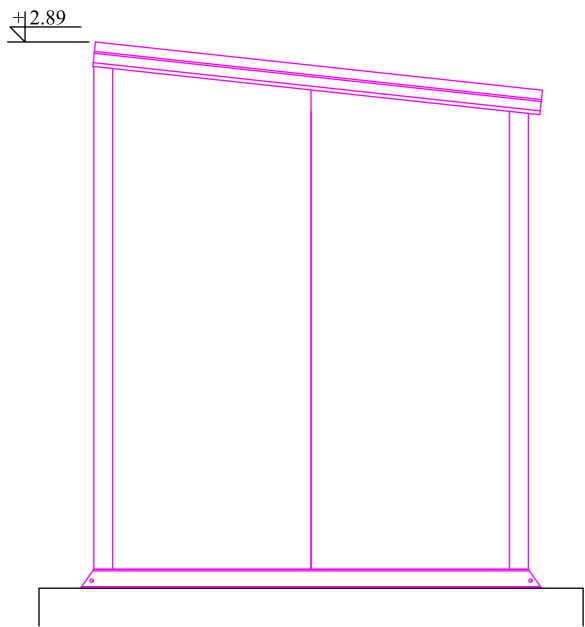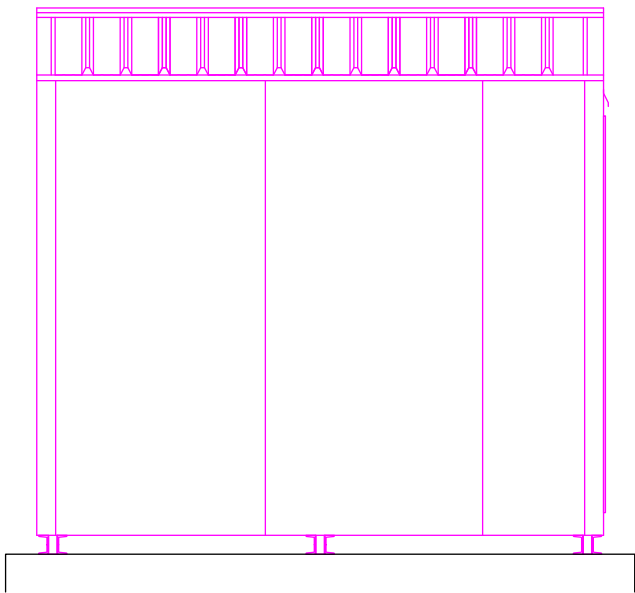


Investitor: BH TELECOM d.d.		Objekat: Infrastruktura bazne stanice mobilne mreže		 Dioničko društvo Sarajevo	
Glavni projekat Knjiga 1/1	Faza: A	godina: 2017.	šifra projekta: GP-BS-10472-291		
Naziv crteža: Fasade objekta za smještaj GSM opreme			razmjera: 1:50	broj crteža: 4 - (109/131)	ovjerio:  Projektant: Mušinić Dženadin, d.i.g.

pogled A- A

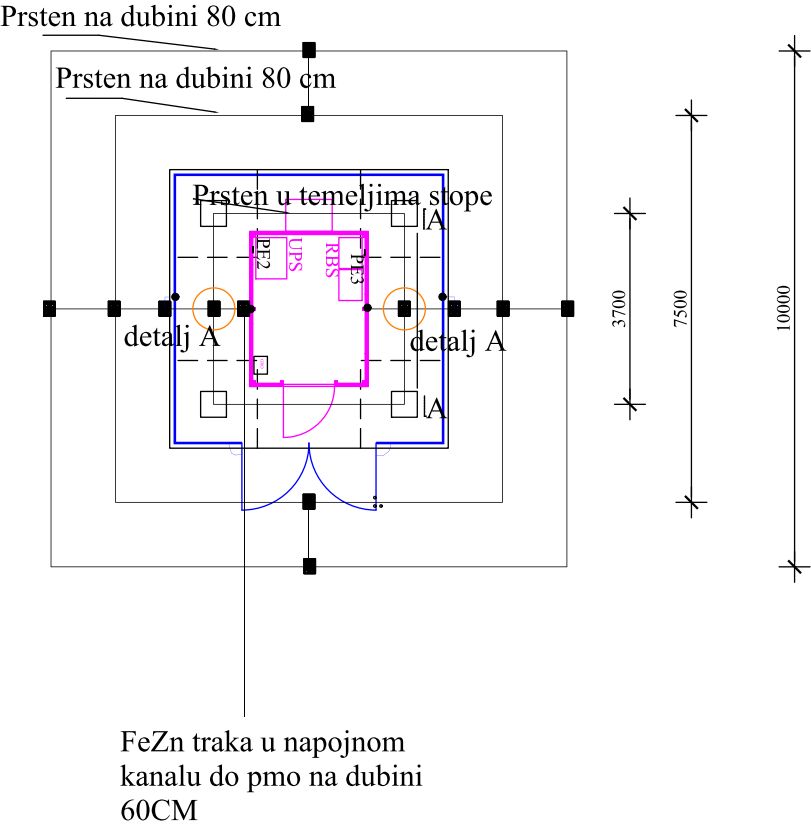
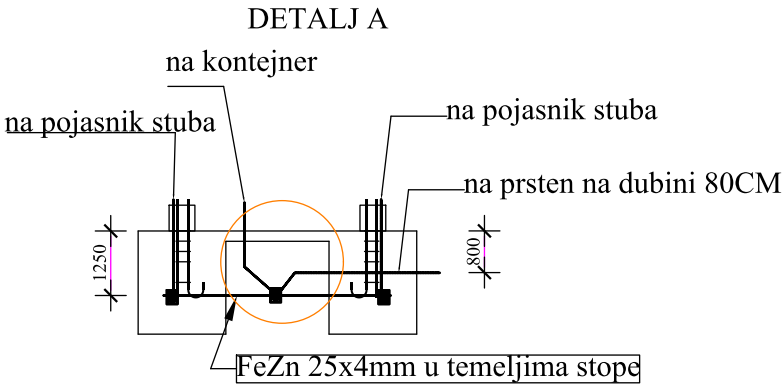


- LEGENDA
- uzemljenje fidera P/F 1x35 mm
 - Podzemna FeZn traka 25X4 mm
 - P/F 1x50mm
 - brikna za povezivanje segmenata na ogradi P/F 1x16mm²
 - Dozemni spust FeZn traka 25X4 mm

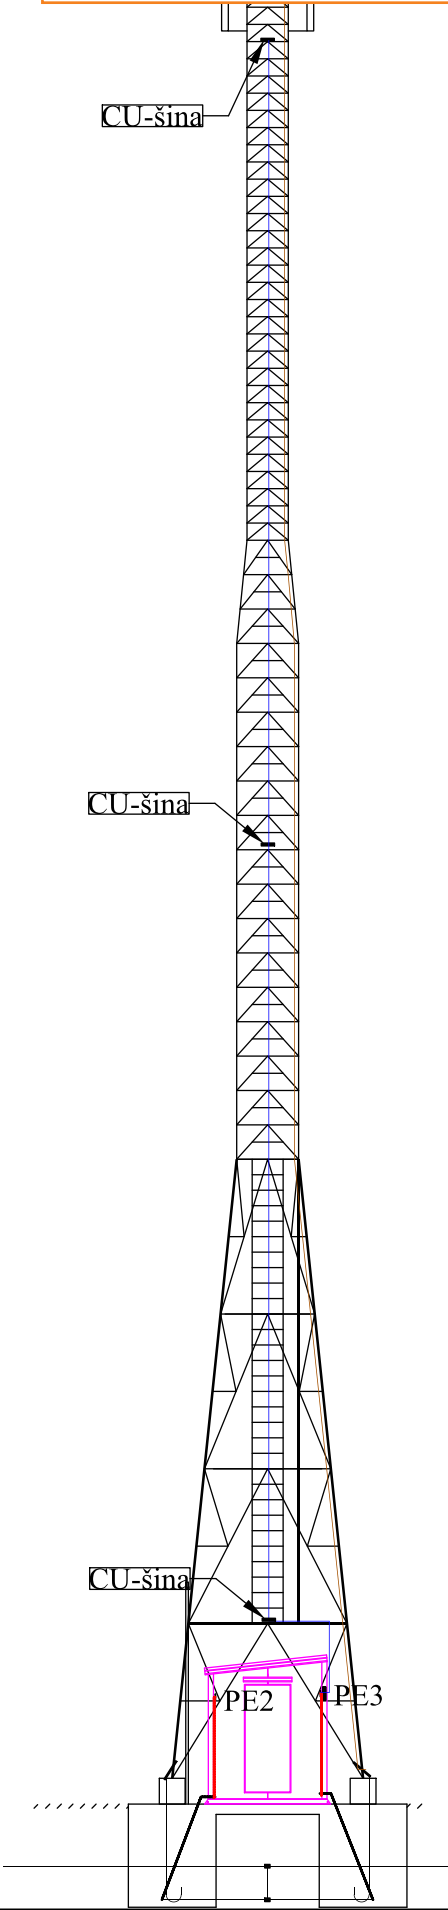

Investitor: BH TELECOM d.d.		Objekat: Infrastruktura bazne stanice mobilne mreže		 Dioničko društvo Sarajevo	
Glavni projekat Knjiga EI	izdanje: I	godina: 2017.	šifra projekta: GP-BS-10472-291		
Naziv crteža: Plan uzemljivača objekta		razmjera: 1:150	broj crteža: 5.6.9	Projektant: Moćević Džafer,d.e.i. ovjerio: 	

FN simulacija — proizvodnja i energetski bilans (informativno)

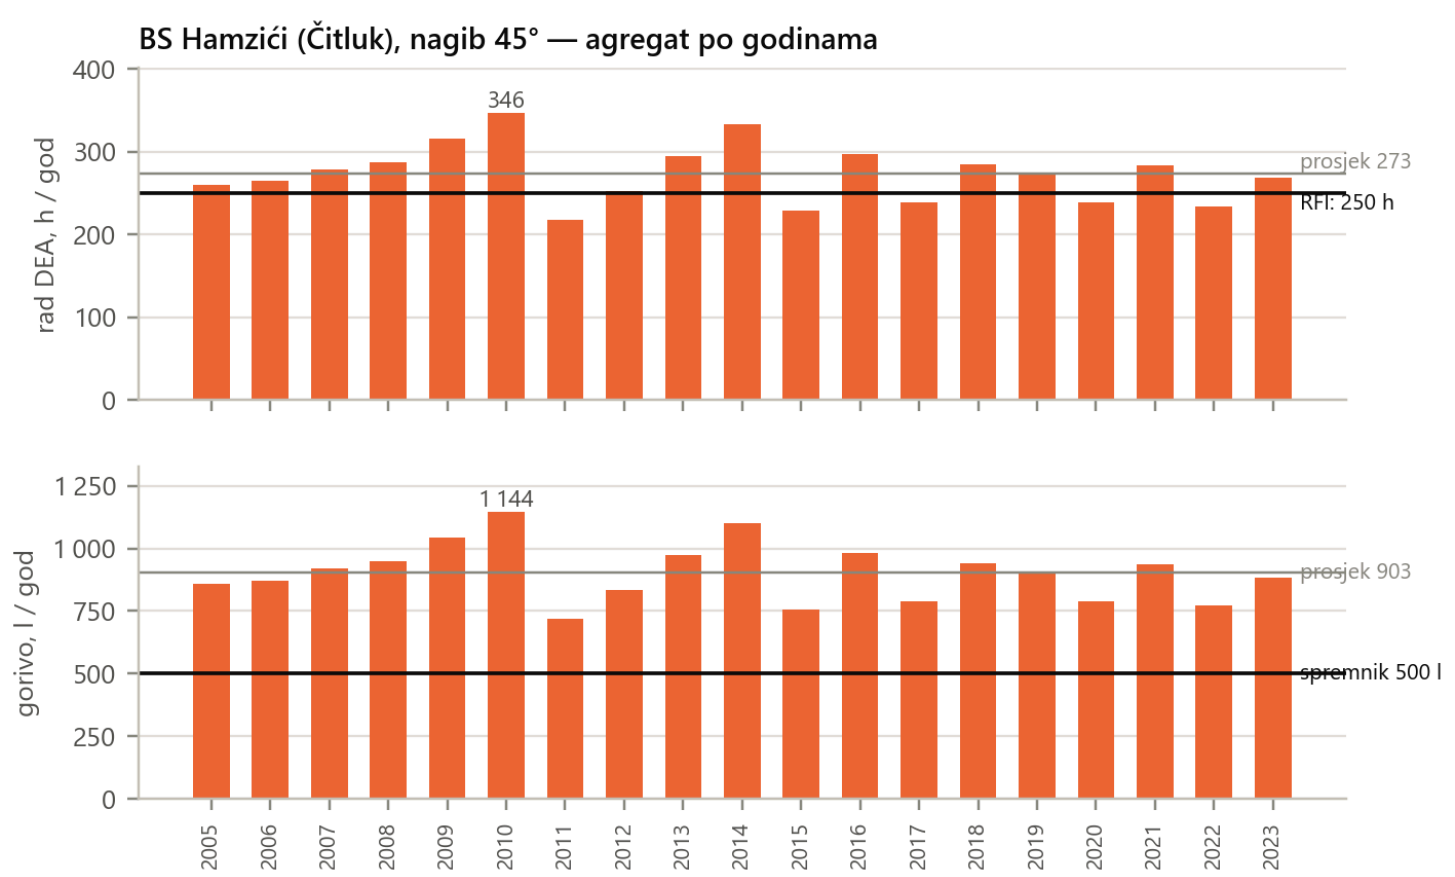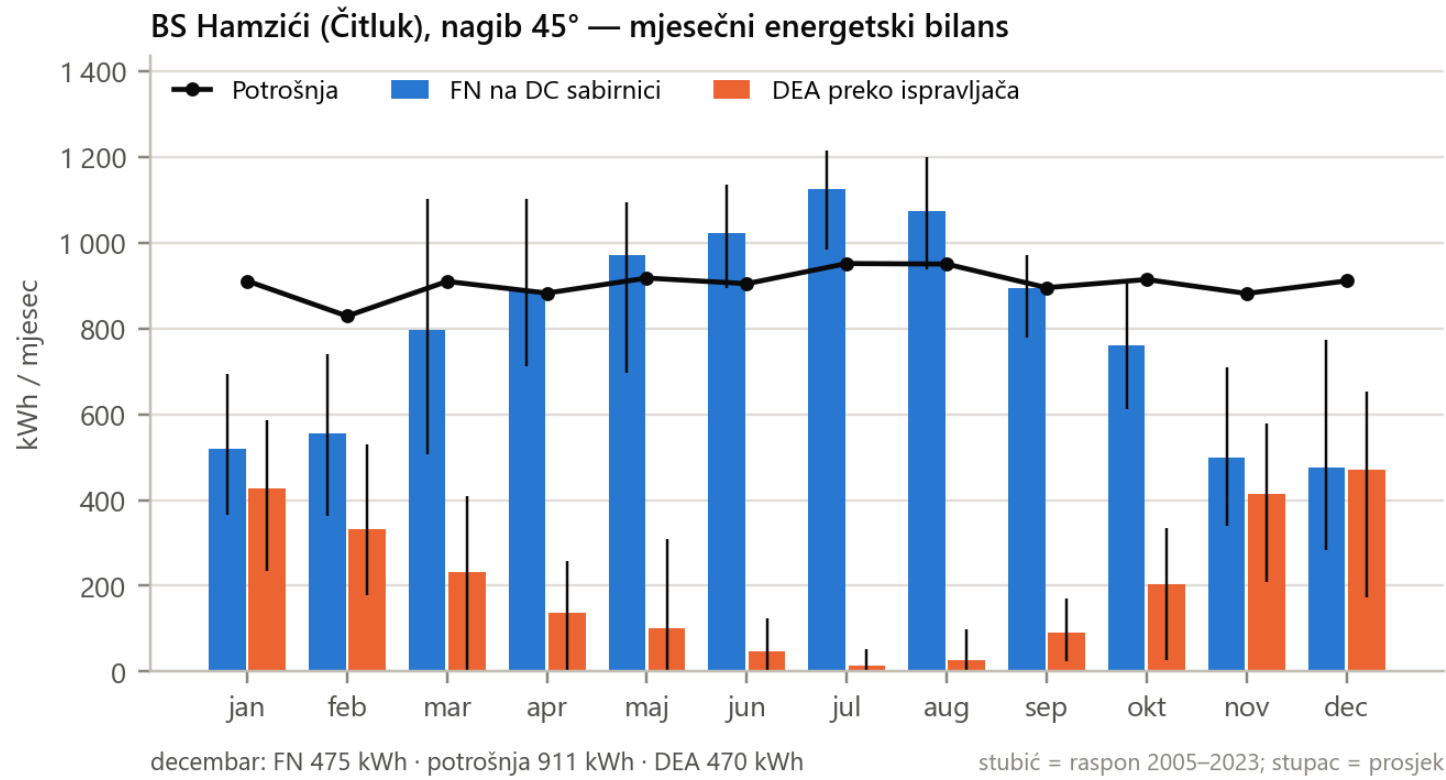

Polje	12 × iPV585-M2A = 7,02 kWp na 4 nosača, nagib 45°, azimut 225° (jugozapad)
FN na DC sabirnici (–48 V)	9 585 kWh/god · 1 365 kWh/kWp
Potrošnja	10 864 kWh/god (1180 W + hlađenje ormara i pomoćna potrošnja)
Decembar	FN 475 kWh prema potrošnji 911 kWh
Solarni udio u potrošnji	77,0 %
Rad DEA	prosjeak 273 h/god · 9 od 10 godina ≤319 h · najviše 346 h
Gorivo	prosjeak 903 l/god · dopuna spremnika 500 l 2,3 puta godišnje
Nepokrivena potrošnja	0 kWh u 19 godina
Provjera prema PVGIS-u	PVcalc 9 047 kWh/god, pvsim sa istim gubicima 8 996 kWh/god; najveće mjesečno odstupanje 2,3 %

Satna simulacija energetskog bilansa na –48 V DC sabirnici za 2005–2023 (pvlib + PVGIS-SARAH3), uz parametriranje SMU iz Priloga I, Tačka 4.6: start pri DOD 85 %, zaustavljanje pri SoC 60 %, ograničenje ispravljača 9,5 kW. Bez zasjenjenja stablom JJI–JI; sa stablom rad DEA raste za 1–10 h/god. Metoda, gubici, osjetljivost i pretpostavke: proračuni lokacije, dio A.6. Vrijednosti su informativne. Izvor: review/pvsim/kpis.json (sha256 e984c7a841c3, pvsim commit e42bbaa).