


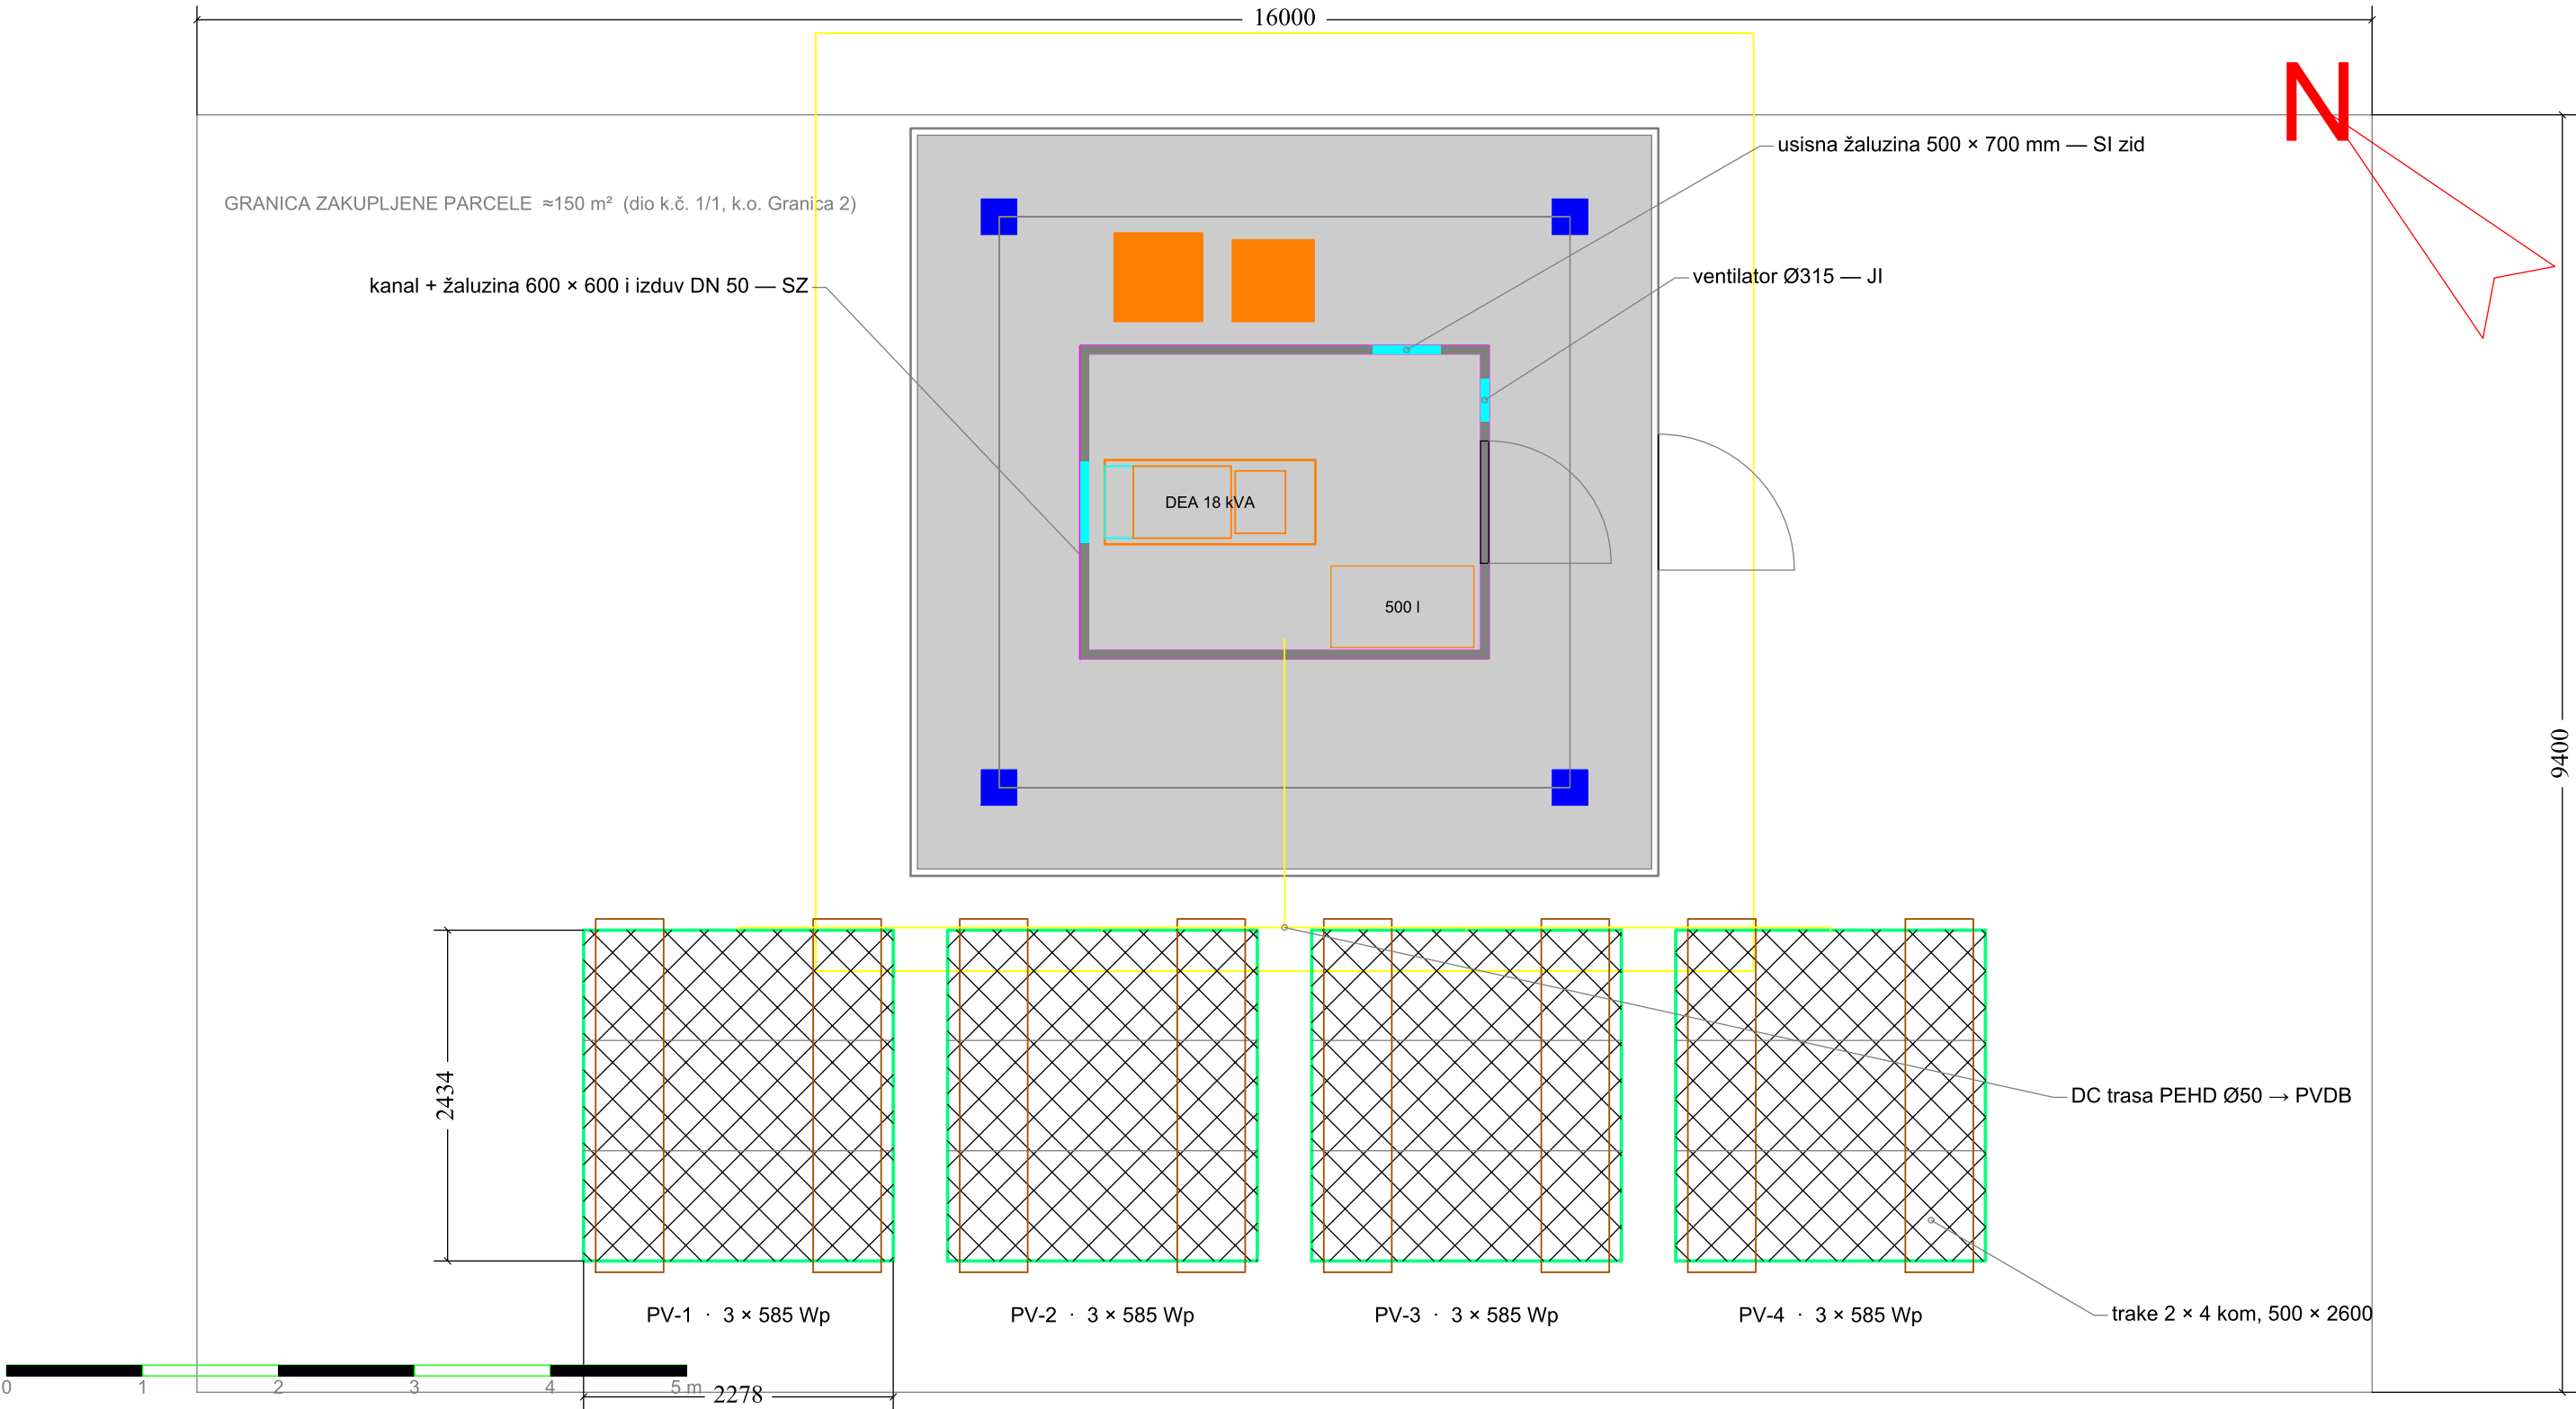

LEGENDA

- LOT 1 — nosači FN panela PV-1..PV-4 (po 3 x 585 Wp, položeno, 45°, azimut 225° JZ) — 2 stringa x 6
- LOT 1 — AB temeljne trake 500 x 2600 mm, dubina 900, razmak 1600 mm
- LOT 1 — DC trasa u PEHD Ø50 do PVDB
- LOT 2 — DEA 18 kVA u skid izvedbi i dvoplašni spremnik 500 l
- LOT 2 — usisna žaluzina (SI); kanal, žaluzina i izduv (SZ); ventilator (JI)

NAPOMENE:

- Nosač i temelji — tehničko rješenje i statički proračun Ponuđača.
- Temelji IZVAN ograde; ivica panela +0,50 / +2,93 m.
- Zahtjevi: Prilog I, Tačke 3 i 4.



BH TELECOM d.d. SARAJEVO

Izvršna direkcija za tehnologiju i razvoj servisa

Investitor:

BH Telecom d.d. Sarajevo, Franca Lebara 7, Sarajevo

Objekat:

BS SJEDNICA (Bileća) — autonomni hibridni sistem napajanja

Faza:

Tenderska dokumentacija — Prilog III

Naziv crteža:

Situacija — BUDUĆE STANJE (LOT 1 + LOT 2)

Projektant:

Rusmir Skopljak, dipl. ing. el.

ovjerio:

Rusmir Skopljak, dipl. ing. el.

šifra projekta:

BHT-SJEDNICA-2026

razmjera:

1:50

godina / broj crteža:

2026. S-02