


POGLED SA JUGOZAPADA (pravac gledanja azimut 45°)

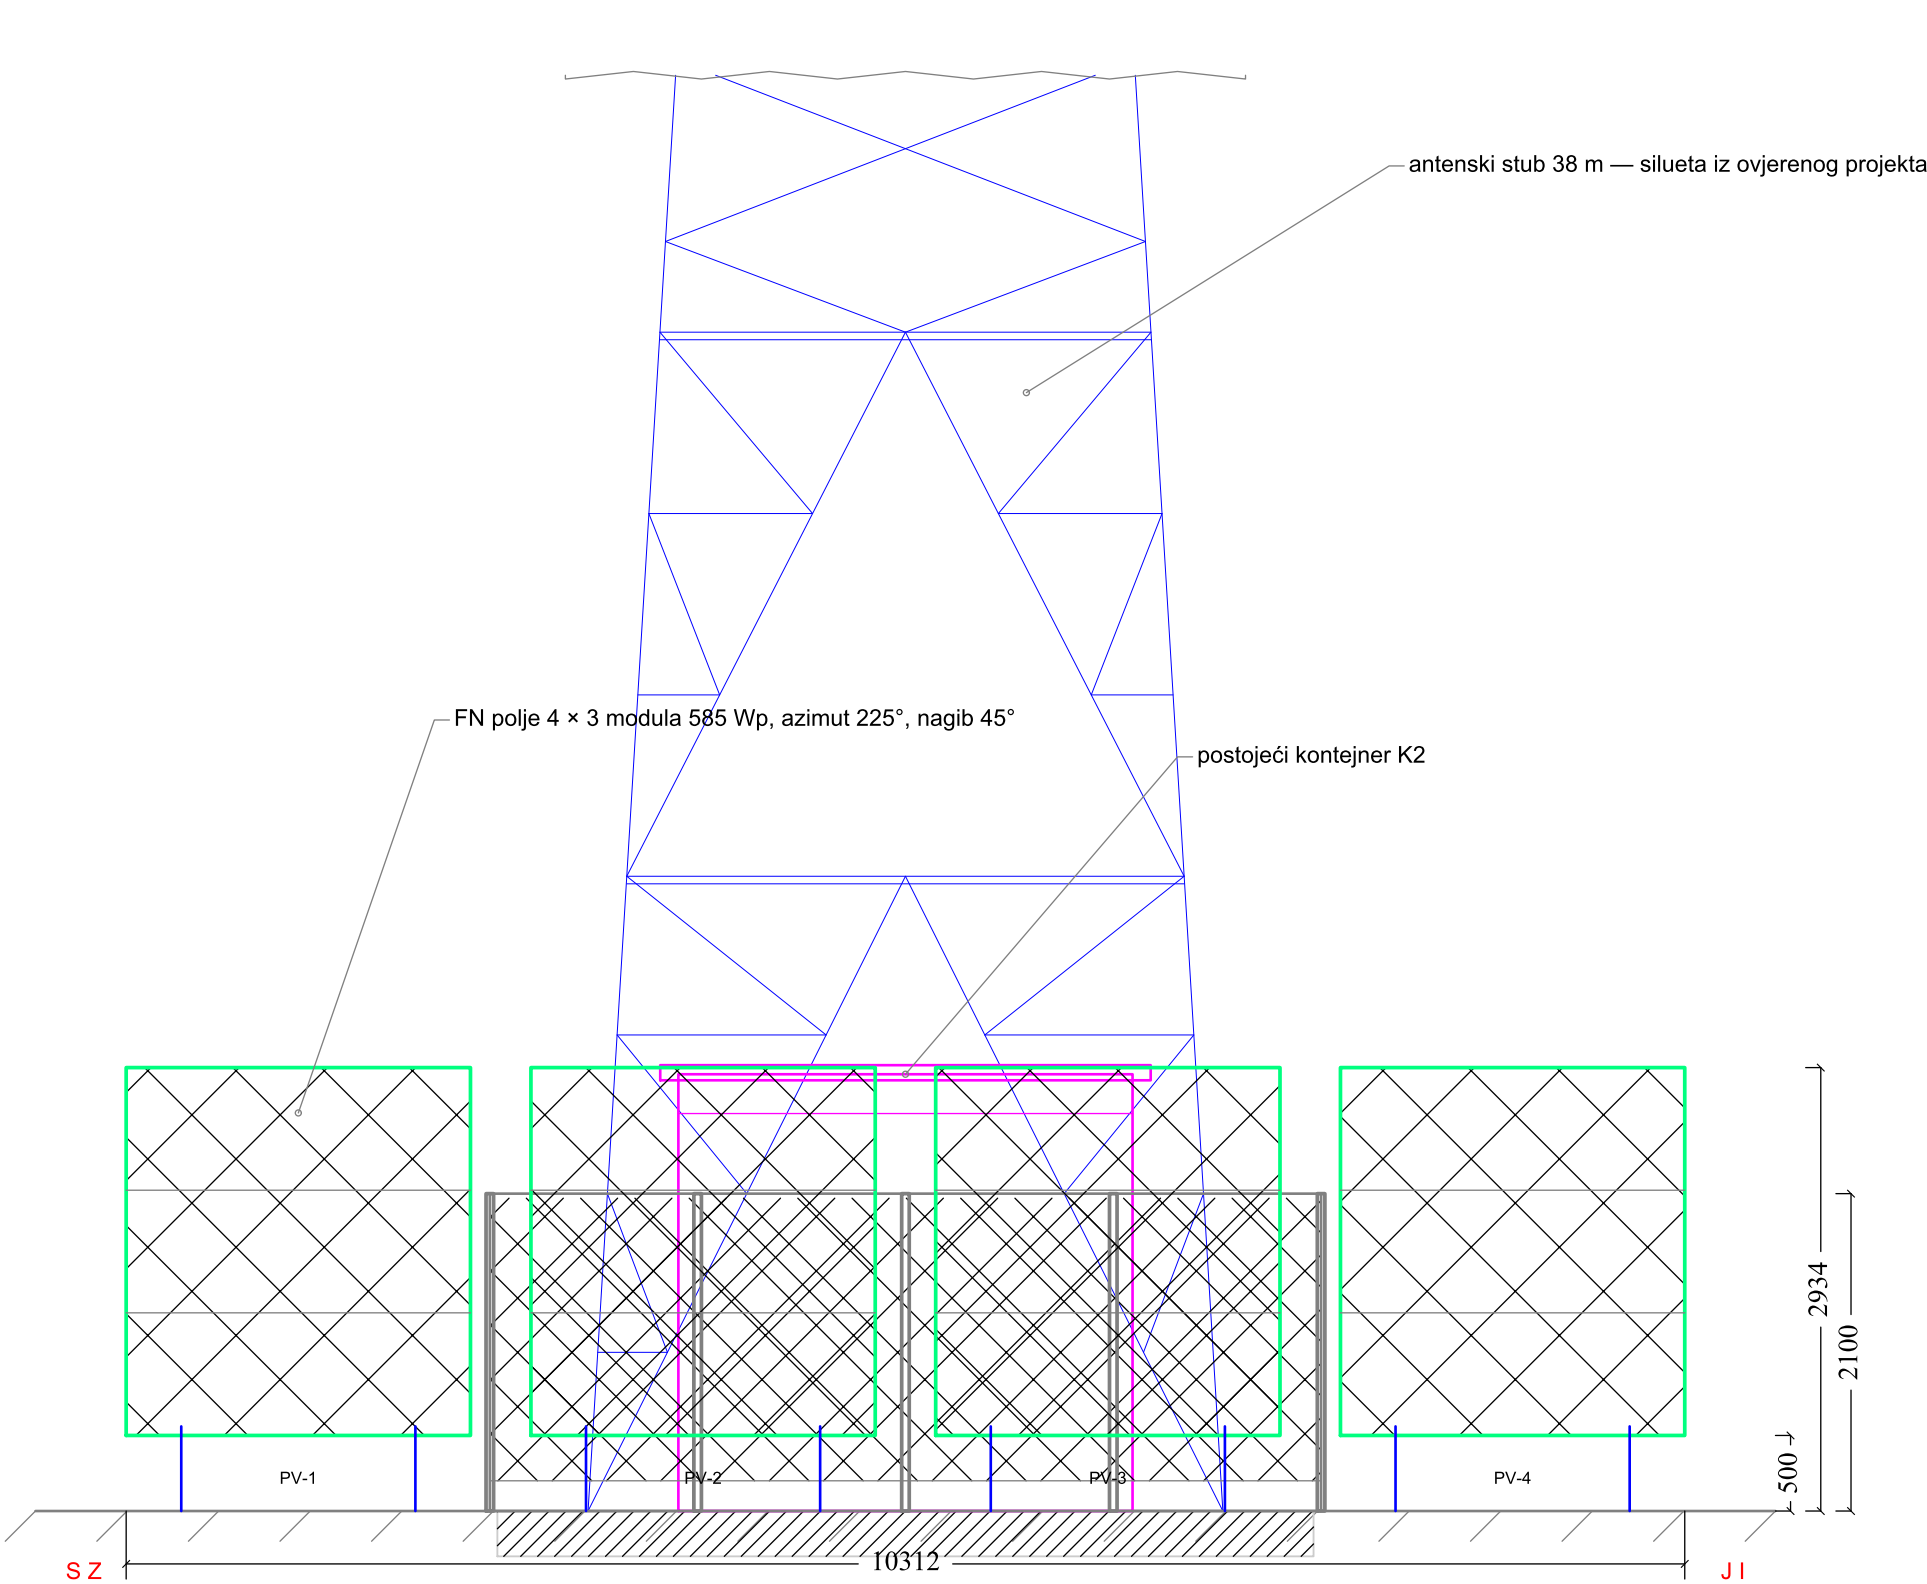

- LEGENDA
- LOT 1 — FN moduli i nosači (ispred ograde, JZ)
 - postojeci antenski stub — silueta iz ovjerenog projekta
 - postojeci kontejner K2 na postojećoj ploči
 - postojeca oграда h = 2,10 m

- NAPOMENE:
- Prava ortogonalna elevacija u pravcu azimuta 45°; visine i širine su mjerljive.
 - Paneli gledaju u posmatrača pod 45°, pa se po visini vide skraćeno: +0,50 do +2,93 m.
 - Stub je prikazan do +9,50 m i prekinut; h = 38 m prema ovjerenom projektu (list 462 — 01_ANTENSKI STUB 38 m).
 - Zahtjevi: Prilog I, Tačke 3 i 4.

bh BH TELECOM d.d. SARAJEVO Izvršna direkcija za tehnologiju i razvoj servisa		
Investitor: BH Telecom d.d. Sarajevo, Franca Lehara 7, Sarajevo		
Objekat: BS SJEDNICA (Bileća) — autonomni hibridni sistem napajanja		
Faza: Tenderska dokumentacija — Prilog III		šifra projekta: BHT-SJEDNICA-2026
Naziv crteža: Pogled sa JUGOZAPADA — kompleks sa FN poljem		razmjera: 1:50
Projektant: Rusmir Skopljak, dipl. ing. el.	ovjerio: Rusmir Skopljak, dipl. ing. el.	godina / broj crteža: 2026. S-04