


PRESJEK A–A (osa SZ trake nosača PV-2 — pogled prema SJEVEROZAPADU)

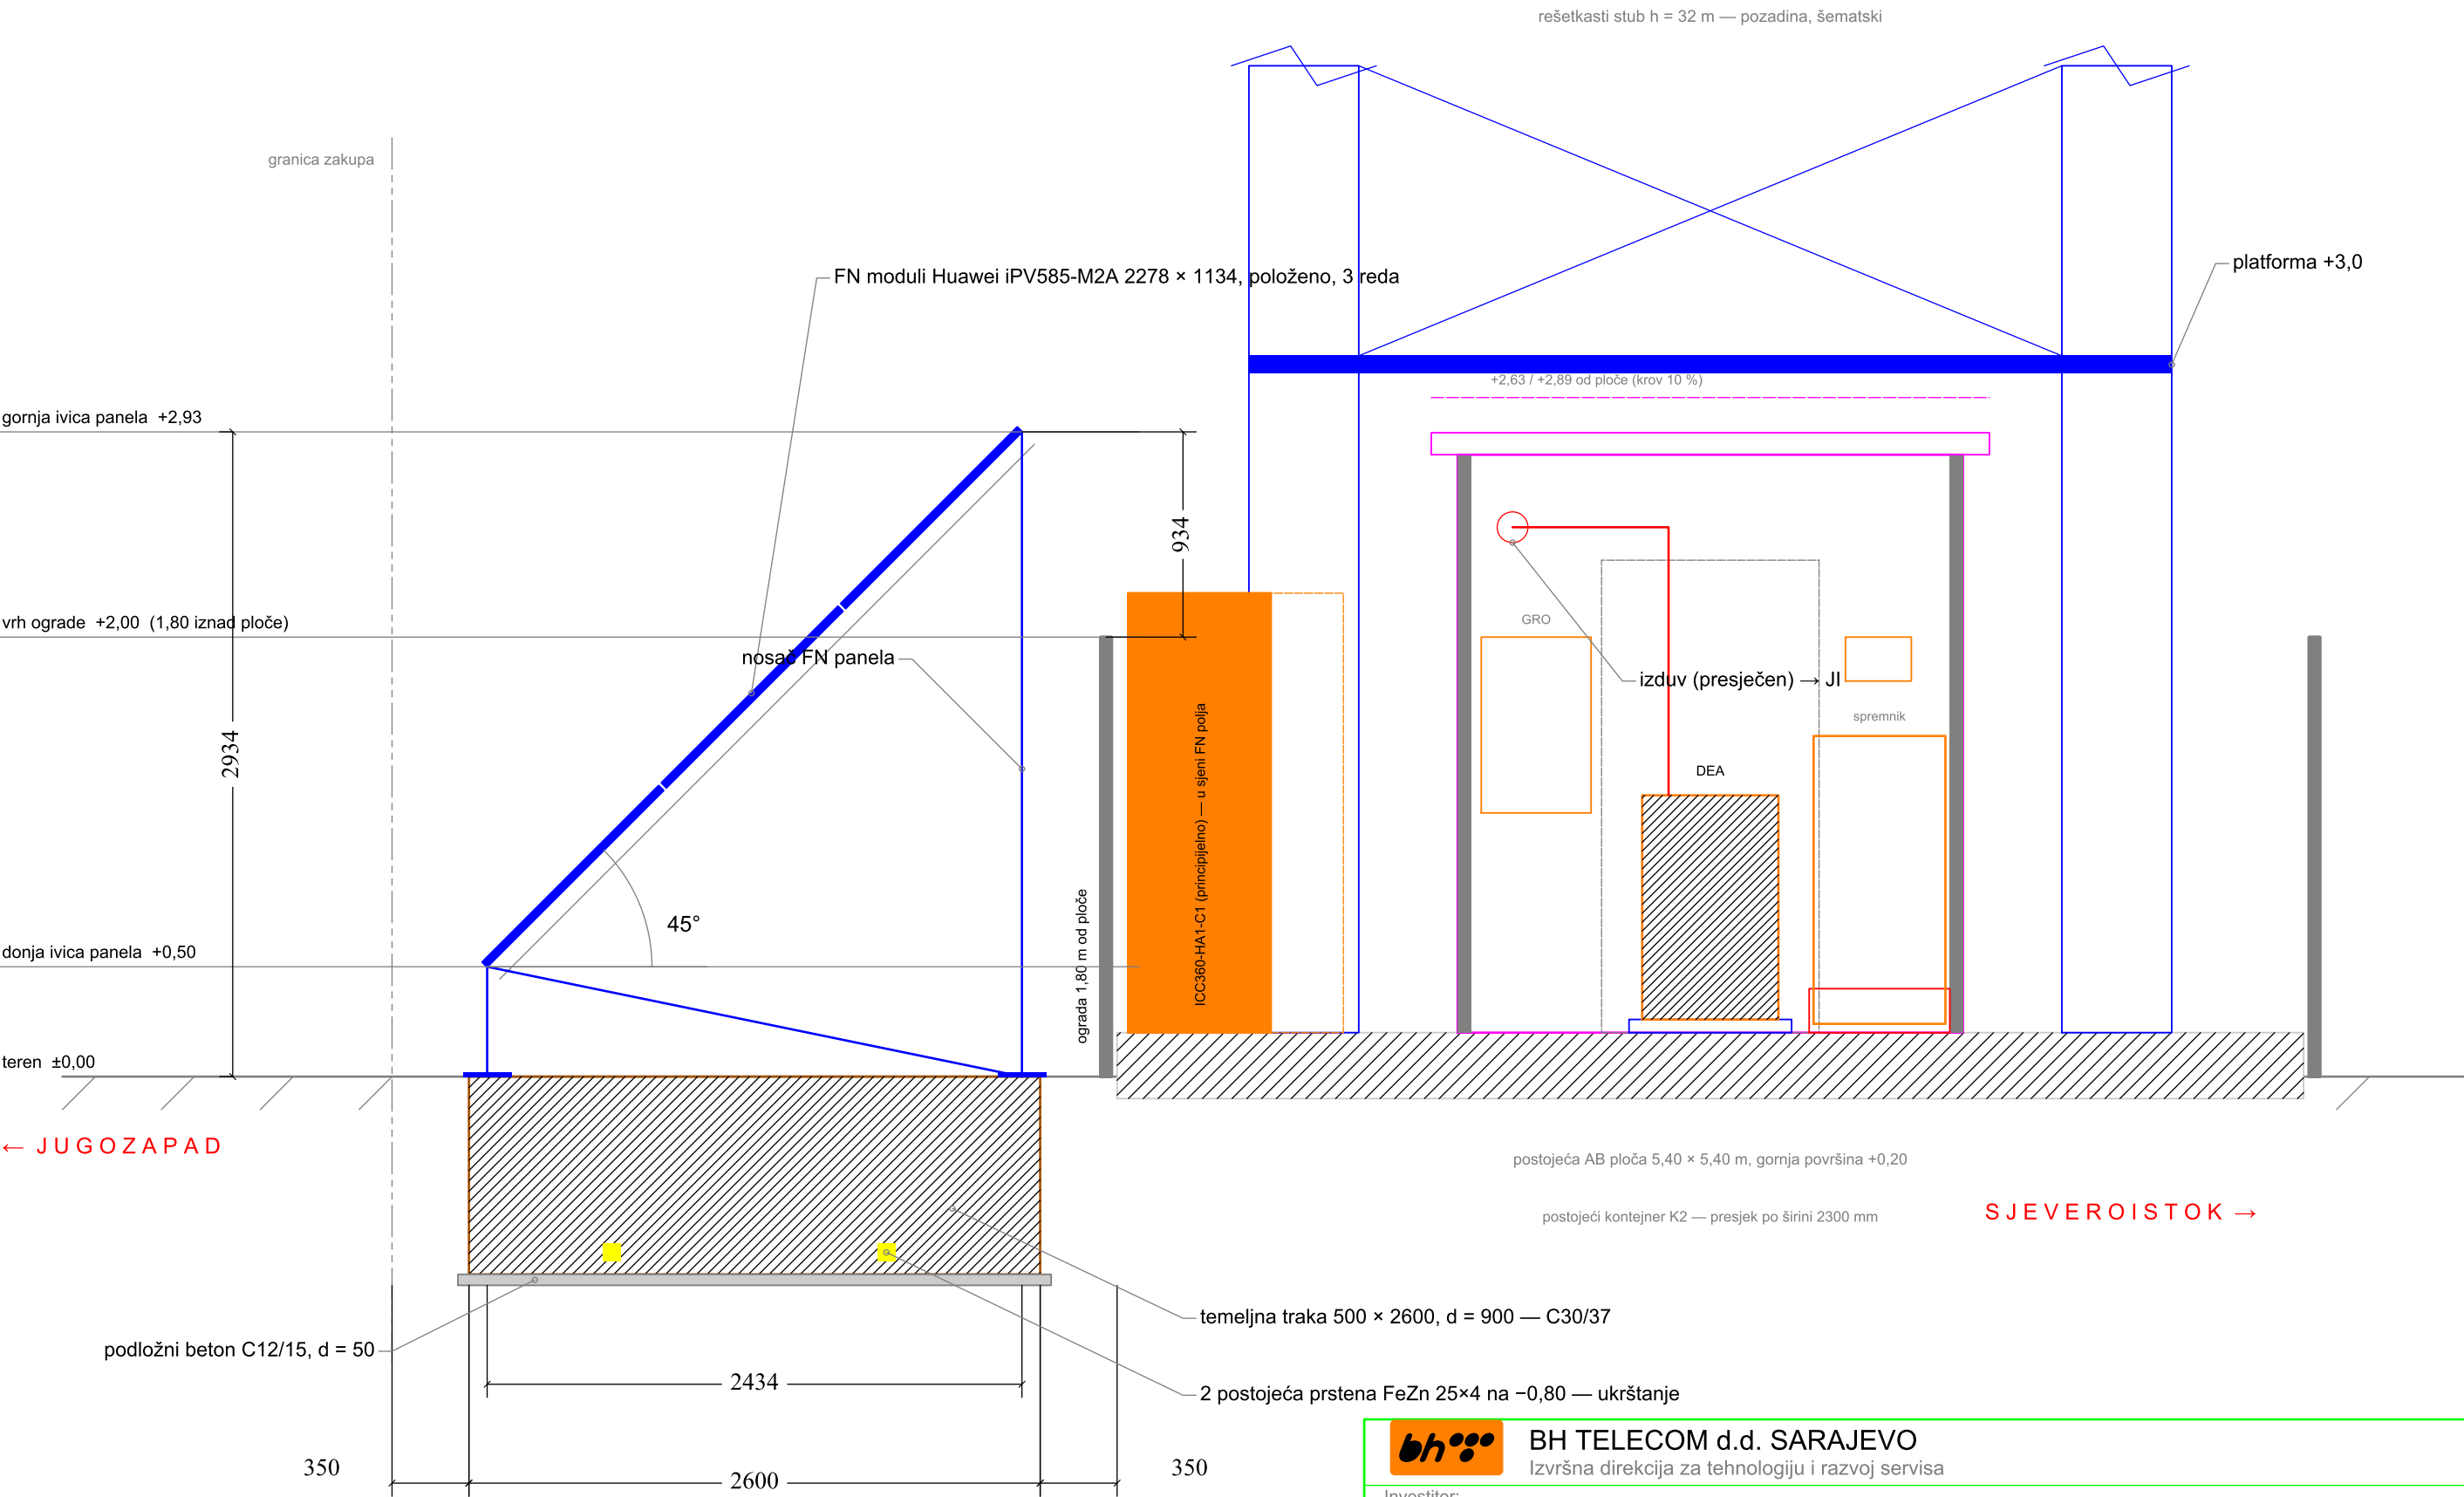

- NAPOMENE:**
- Polje: 3 reda x 1 modul 585 Wp, položeno; nagib 45°, projekcija 2434 mm; 4 odvojena nosača u nizu (H-02).
 - Dvije temeljne trake po nosaču 500 x 2600 mm, dubina 900 mm, razmak 1600 mm (druga iza ravni presjeka); beton C30/37 (XC4+XF3), armatura B500B, na podložnom betonu C12/15 d = 50 mm.
 - Kote od terena uz FN polje; teren je -0,20 m ispod ploče (04_Ograda). Donja ivica panela +0,50, gornja +2,93; vrh ograde +2,00 (1,80 m iznad ploče) — gornja ivica je 0,93 m iznad ograde.
 - Postojeći prsteni uzemljivača na 0,8 m presijecaju traku: lociranje, otkopavanje i premještanje ili premoštavanje prstena (LOT 1).
 - Trake su 350 mm od granice zakupa (JZ) i od ploče (SI); položaj presjeka na H-02.
 - Stub, platforma P I (+3,0 m), kontejner i ormari šematski; ICC360 i MTS su iza FN polja.

bh BH TELECOM d.d. SARAJEVO Izvršna direkcija za tehnologiju i razvoj servisa		
Investitor: BH Telecom d.d. Sarajevo, Franca Lehara 7, Sarajevo		
Objekat: BS HAMZIĆI (ČITLUK) — autonomni hibridni sistem napajanja		
Faza: Tenderska dokumentacija — Prilog III		šifra projekta: BHT-HAMZICI-2026
Naziv crteža: Presjek A–A kroz FN polje		razmjera: 1:30
Projektant: Rusmir Skopljak, dipl. ing. el.	ovjerio: Rusmir Skopljak, dipl. ing. el.	godina / broj crteža: 2026. H-03