
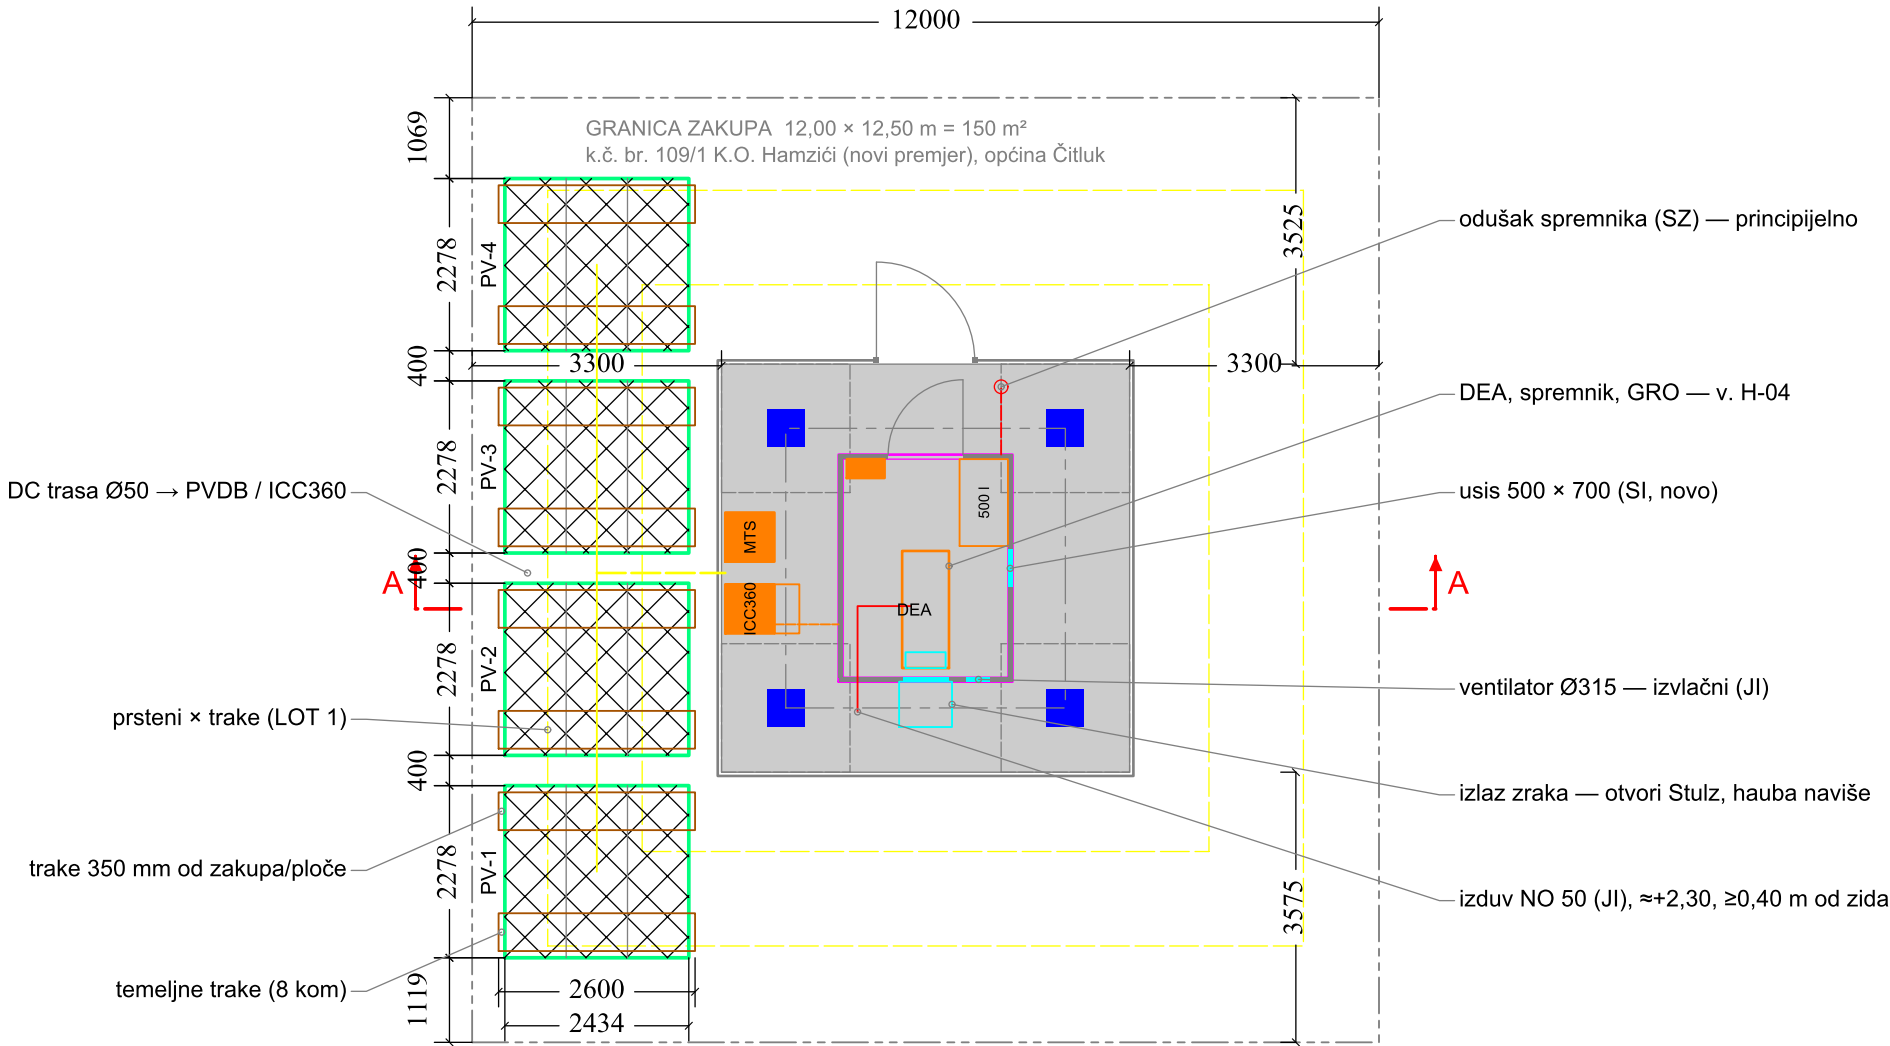


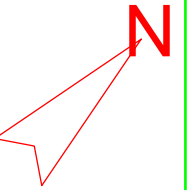

NAPOMENA — ORIJENTACIJA:
Prema Google Maps (Naručilac 11.09.2026) kompleks je zakrenut 45°: vrata kontejnera i kapija gledaju na SJEVEROZAPAD (SZ), klima-uređaj Stulz na JI. Crtež je pravougaon na kompleks (gore SZ, desno SI, dolje JI, lijevo JZ); strelica pokazuje pravi sjever. Ovjereni crtež lokacije iz 2017 (GP-BS-10472-291, 01_Situacija 1_200) zakrenut je ≈180° u odnosu na teren. Orijehtaciju potvrđuje Ponuđač obilaskom lokacije.

- NAPOMENE:**
- 1 Nosači na JUGOZAPAD (azimut 225°), nagib 45°; ivica panela +0,50 / +2,93 m.
 - 2 4 odvojena nosača u nizu: 4 × 2278 + 3 × 400 = 10312 mm, u pojasu JZ.
 - 3 Temeljne trake 500 × 2600 mm, d = 900 mm, na podložnom betonu 50 mm.
 - 4 Postojeći prsteni uzemljivača (0,8 m) ukrštaju temeljne trake — LOT 1.
 - 5 Vjetar qp ≥ 1,20 kN/m²; nosač CUSTOM izrade, proračun dostavlja Ponuđač.
 - 6 Raspored u kontejneru prema H-04.
 - 7 Ormari ICC360-HA1-C1 i MTS iza FN polja, u sjeni — principijelno.

LEGENDA

- FN nosači PV-1..PV-4 — po 3 × 585 Wp (1 × 3, položeno), 45°, azimut 225° (JZ) — 2 stringa × 6
- AB temeljne trake 500 × 2600 mm, d = 900 mm, razmak 1600 mm — 8 kom
- DC trasa u PEHD Ø50 (isprekidano) — od polja do PVDB uz ICC360
- DEA 18 kVA (skid), spremnik 500 l u koritu, novi GRO
- usis 500 × 700 (SI), izlaz zraka kroz otvore Stulz (JI) i haubu naviše, ventilator Ø315 (JI)
- izdub NO 50 (JI, ≈+2,30 m); odušak spremnika (SZ, isprekidano); presjek A–A
- Huawei ICC360-HA1-C1 i MTS vani na ploči (JZ), iza FN polja — principijelno



bh BH TELECOM d.d. SARAJEVO Izvršna direkcija za tehnologiju i razvoj servisa		
Investitor: BH Telecom d.d. Sarajevo, Franca Lehara 7, Sarajevo		
Objekat: BS HAMZIĆI (ČITLUK) — autonomni hibridni sistem napajanja		
Faza: Tenderska dokumentacija — Prilog III		šifra projekta: BHT-HAMZICI-2026
Naziv crteža: Situacija — BUDUĆE STANJE		razmjera: 1:100
Projektant: Rusmir Skopljak, dipl. ing. el.	ovjerio: Rusmir Skopljak, dipl. ing. el.	godina / broj crteža: 2026. H-02