
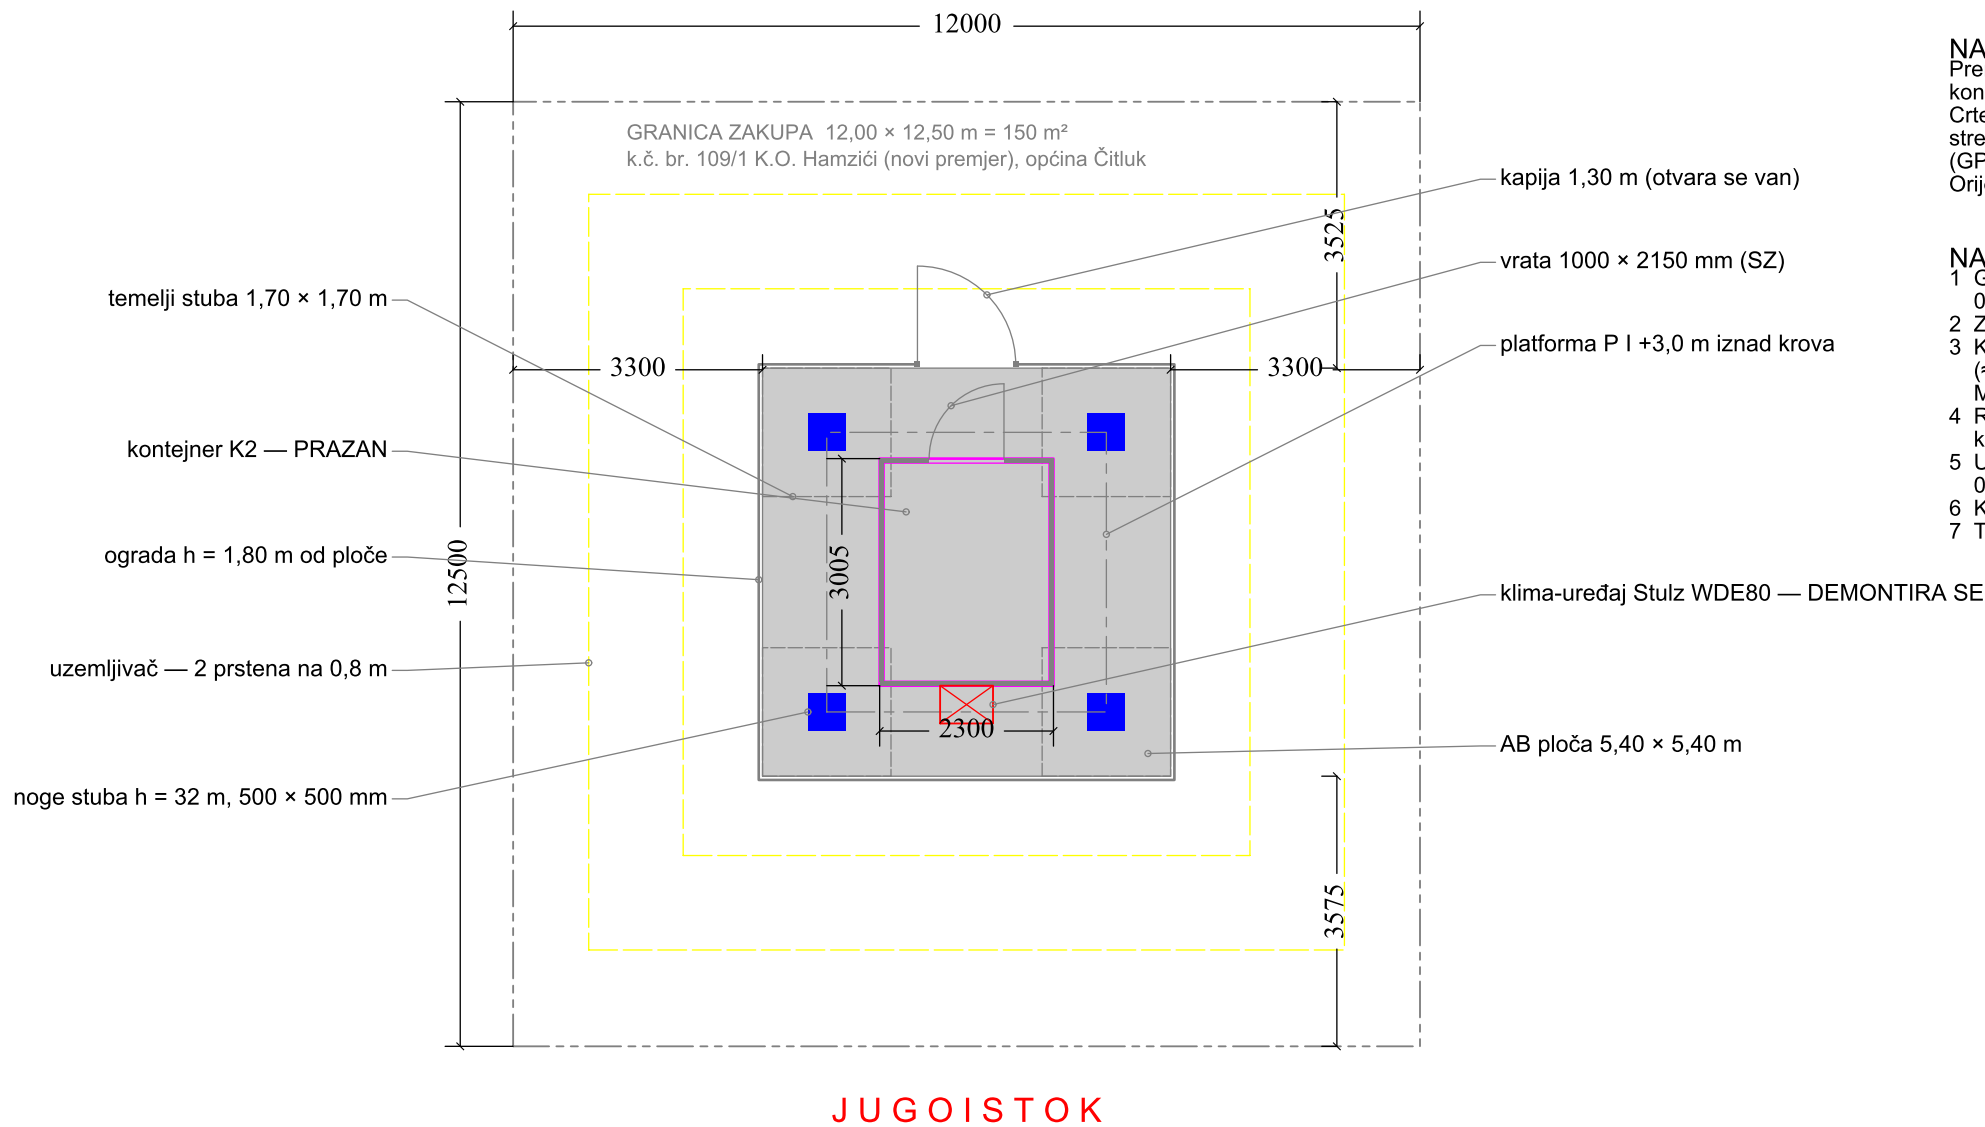


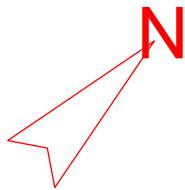

NAPOMENA — ORIJENTACIJA:
Prema Google Maps (Naručilac 11.09.2026) kompleks je zakrenut 45°: vrata kontejnera i kapija gledaju na SJEVEROZAPAD (SZ), klima-uređaj Stulz na JI. Crtež je pravougaon na kompleks (gore SZ, desno SI, dolje JI, lijevo JZ); strelica pokazuje pravi sjever. Ovjereni crtež lokacije iz 2017 (GP-BS-10472-291, 01_Situacija 1_200) zakrenut je ≈180° u odnosu na teren. Orijehtaciju potvrđuje Ponuđač obilaskom lokacije.

- NAPOMENE:**
- Geometrija iz ovjerenog projekta lokacije GP-BS-10472-291 (2017): 01_Situacija 1_200, 04_Ograda, 01_Osnova, 04_Fasade, 01_Dispozicija S32 m, 3.6.9 Plan uzemljivača objekta.
 - Zakup 12,00 × 12,50 m = 150 m²: k.č. br. 109/1 K.O. Hamzići (novi premjer), općina Čitluk.
 - Kontejner je PRAZAN; na jugoistočnom (JI) zidu, u sredini, je samo klima-uređaj Stulz WDE80 (≈700 × 500 × 2200 mm, procjena s fotografija; Naručilac 11.09.2026). Mjere uređaja i otvora u zidu uzimaju se na obilasku lokacije.
 - Rešetkasti stub h = 32 m; platforma P I na +3,0 m je iznad krova kontejnera (+2,63 / +2,89 m) — izduv agregata ne može završiti iznad krova.
 - Uzemljivač FeZn 25×4 mm: prsten u temeljima stopa stuba i dva prstena na dubini 0,8 m oko ploče (kvadrati 7,50 i 10,00 m prema 3.6.9).
 - Kapija se otvara prema van: krilo 1,30 m udarilo bi u kontejner (1,25 m od ograde).
 - Teren uz ploču je na -0,20 m (04_Ograda): ograda je 1,80 m iznad ploče, 2,00 m iznad terena.

LEGENDA

- postojeća ograda 5,50 × 5,50 m, h = 1,80 m od ploče (2,00 m od terena) — kapija 1,30 m na SZ strani
- postojeća AB ploča 5,40 × 5,40 m
- postojeći kontejner K2 2300 × 3005 mm — vrata na SZ strani
- noge rešetkastog stuba h = 32 m, baza 3,70 × 3,70 m
- klima-uređaj Stulz WDE80 (JI zid, u sredini) — demontira se
- postojeći uzemljivač FeZn 25×4 mm (isprekidano — u tlu)



BH TELECOM d.d. SARAJEVO Izvršna direkcija za tehnologiju i razvoj servisa		
Investitor: BH Telecom d.d. Sarajevo, Franca Lehara 7, Sarajevo		
Objekat: BS HAMZIĆI (ČITLUK) — autonomni hibridni sistem napajanja		
Faza: Tenderska dokumentacija — Prilog III		šifra projekta: BHT-HAMZICI-2026
Naziv crteža: Situacija — POSTOJEĆE STANJE		razmjera: 1:100
Projektant: Rusmir Skopljak, dipl. ing. el.	ovjerio: Rusmir Skopljak, dipl. ing. el.	godina / broj crteža: 2026. H-01