



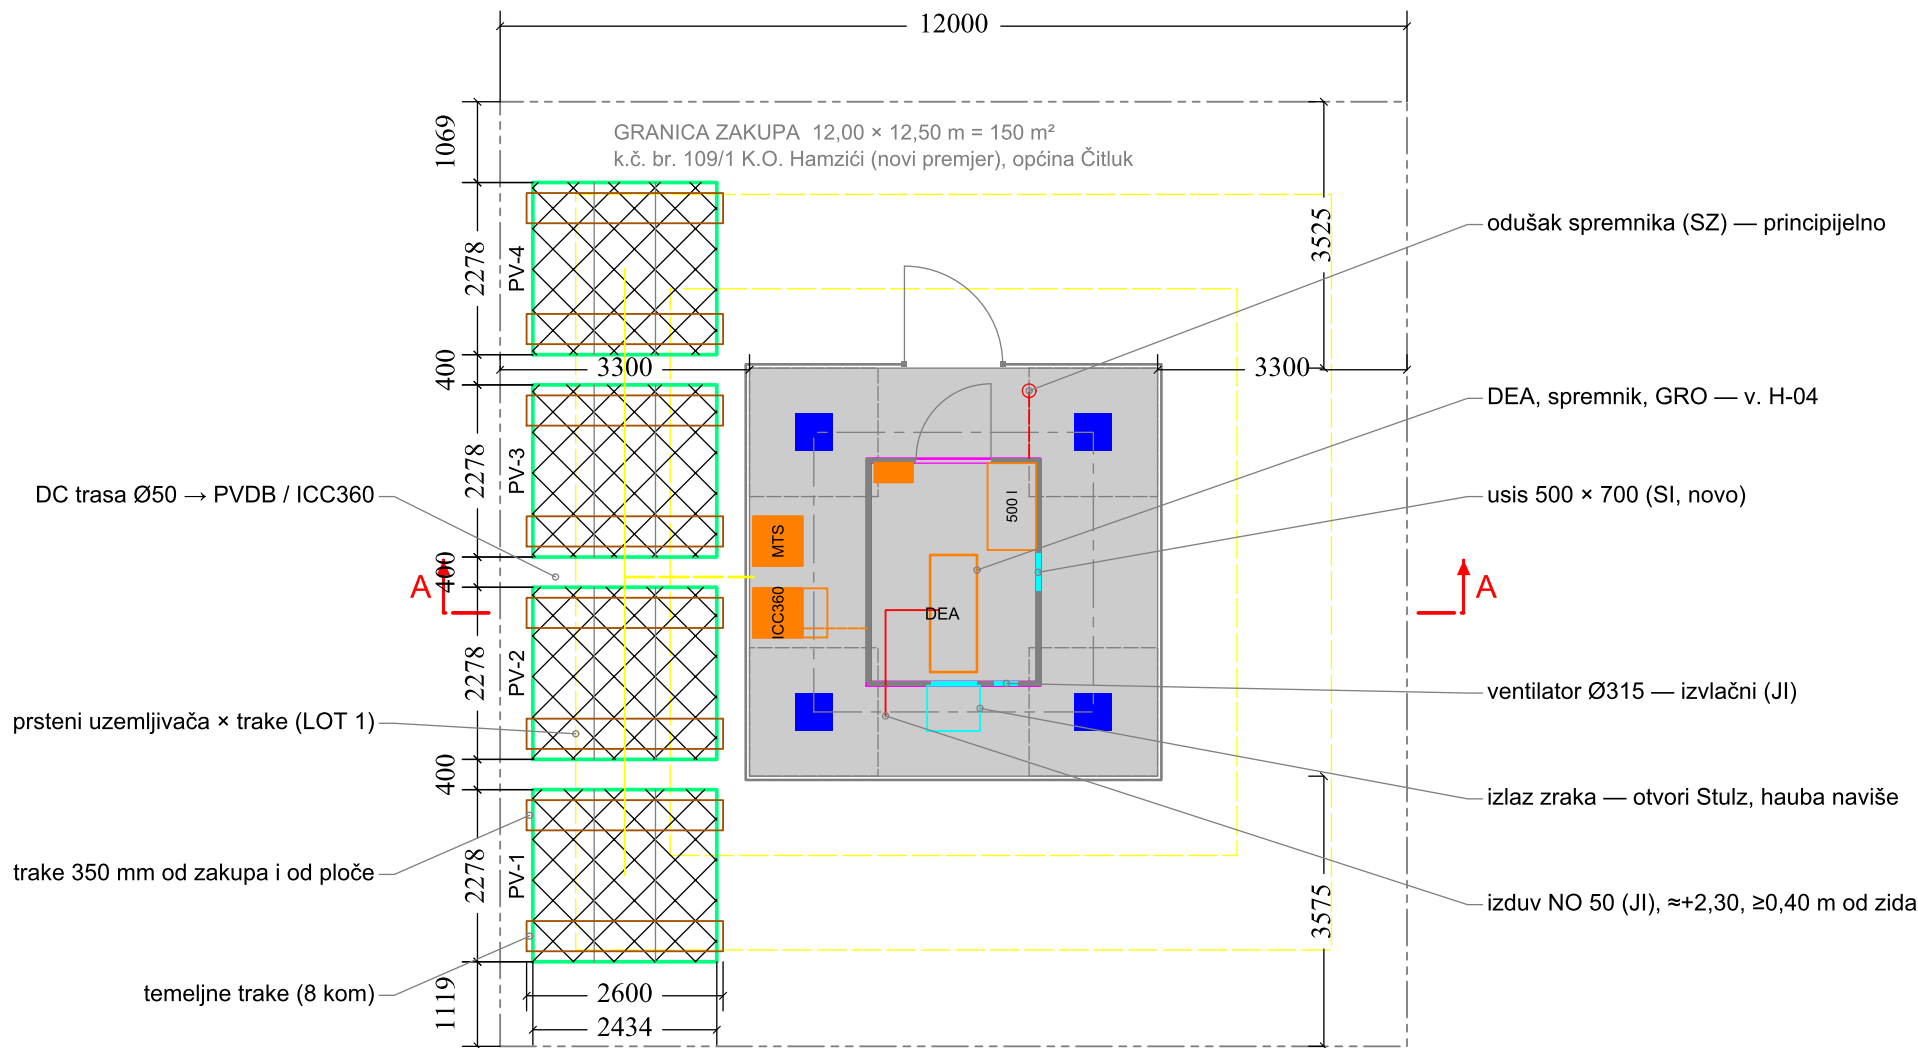

NAPOMENA — ORIJENTACIJA:
Prema Google Maps (Naručilac 11.09.2026) kompleks je zakrenut 45°: vrata kontejnera i kapija gledaju na SJEVEROZAPAD (SZ), klima-uređaj Stulz na JI. Crtež je pravougaon na kompleks (gore SZ, desno SI, dolje JI, lijevo JZ); strelica pokazuje pravi sjever. Ovjereni crtež lokacije iz 2017 (GP-BS-10472-291, 01_Situacija 1_200) zakrenut je ≈180° u odnosu na teren. Orijehtaciju potvrđuje Ponuđač obilaskom lokacije.

- NAPOMENE:**
- Nosači su okrenuti prema JUGOZAPADU (azimut 225°), nagib 45°; donja ivica panela +0,50 m, gornja +2,93 m — 0,93 m iznad vrha ograde (ograda 1,80 m iznad ploče = 2,00 m iznad terena).
 - 4 odvojena nosača u jednom nizu (Naručilac 11.09.2026): 4 × 2278 + 3 × 400 = 10312 mm, u pojasu JZ 3,30 × 12,50 m, centrirano na ploču; sve je unutar granice zakupa.
 - Temeljne trake 400/500 × 2600 mm, d = 900 mm, na podložnom betonu 50 mm, pravac JZ–SI; 350 mm od granice zakupa i od ploče.
 - Postojeći prsteni uzemljivača (0,8 m; 1,05 i 2,30 m od ploče): ukrštanja sa temeljnim trakama — lociranje, otkopavanje i premještanje ili premoštavanje prstena (LOT 1).
 - Vjetar qp ≥ 1,20 kN/m² — nosač CUSTOM izrade; ovjereni statički proračun dostavlja Ponuđač.
 - Raspored u kontejneru prema H-04; izlaz zraka kroz otvore Stulz (JI) i haubu naviše.
 - Ormari ICC360-HA1-C1 i MTS — principijelno, potvrđuju se na licu mjesta; iza FN polja, u njegovoj sjeni; napajanje iz GRO (izvod F1) kroz JZ zid. Odušak spremnika kroz SZ zid — principijelno, konačno prema elaboratu zaštite od požara (≥3 m od izduva i usisa, ≥1 m od ormara).

- LEGENDA**
- FN nosači PV-1..PV-4 — po 3 × 585 Wp (1 × 3, položeno), 45°, azimut 225° (JZ) — 2 stringa × 6
 - AB temeljne trake 400/500 × 2600 mm, d = 900 mm, razmak 1600 mm — 8 kom
 - DC trasa u PEHD Ø50 (isprekidano) — od polja do PVDB uz ICC360
 - DEA 18 kVA (skid), spremnik 500 l u koritu, novi GRO
 - usis 500 × 700 (SI), izlaz zraka kroz otvore Stulz (JI) i haubu naviše, ventilator Ø315 (JI)
 - izduv NO 50 (JI, ≈+2,30 m); odušak spremnika (SZ, isprekidano); presjek A–A
 - Huawei ICC360-HA1-C1 i MTS vani na ploči (JZ), iza FN polja — principijelno

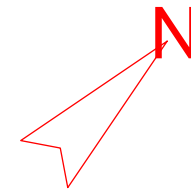

BH TELECOM d.d. SARAJEVO

Izvršna direkcija za tehnologiju i razvoj servisa

Investitor:
BH Telecom d.d. Sarajevo, Franca Lehara 7, Sarajevo

Objekat:
BS HAMZIĆI (ČITLUK) — autonomni hibridni sistem napajanja

Faza:
Tenderska dokumentacija — Prilog III

šifra projekta:
BHT-HAMZICI-2026

Naziv crteža:
Situacija — BUDUĆE STANJE

razmjera:
1:100

Projektant:
Rusmir Skopljak, dipl. ing. el.

ovjerio:
Rusmir Skopljak, dipl. ing. el.

godina / broj crteža:
2026. H-02