


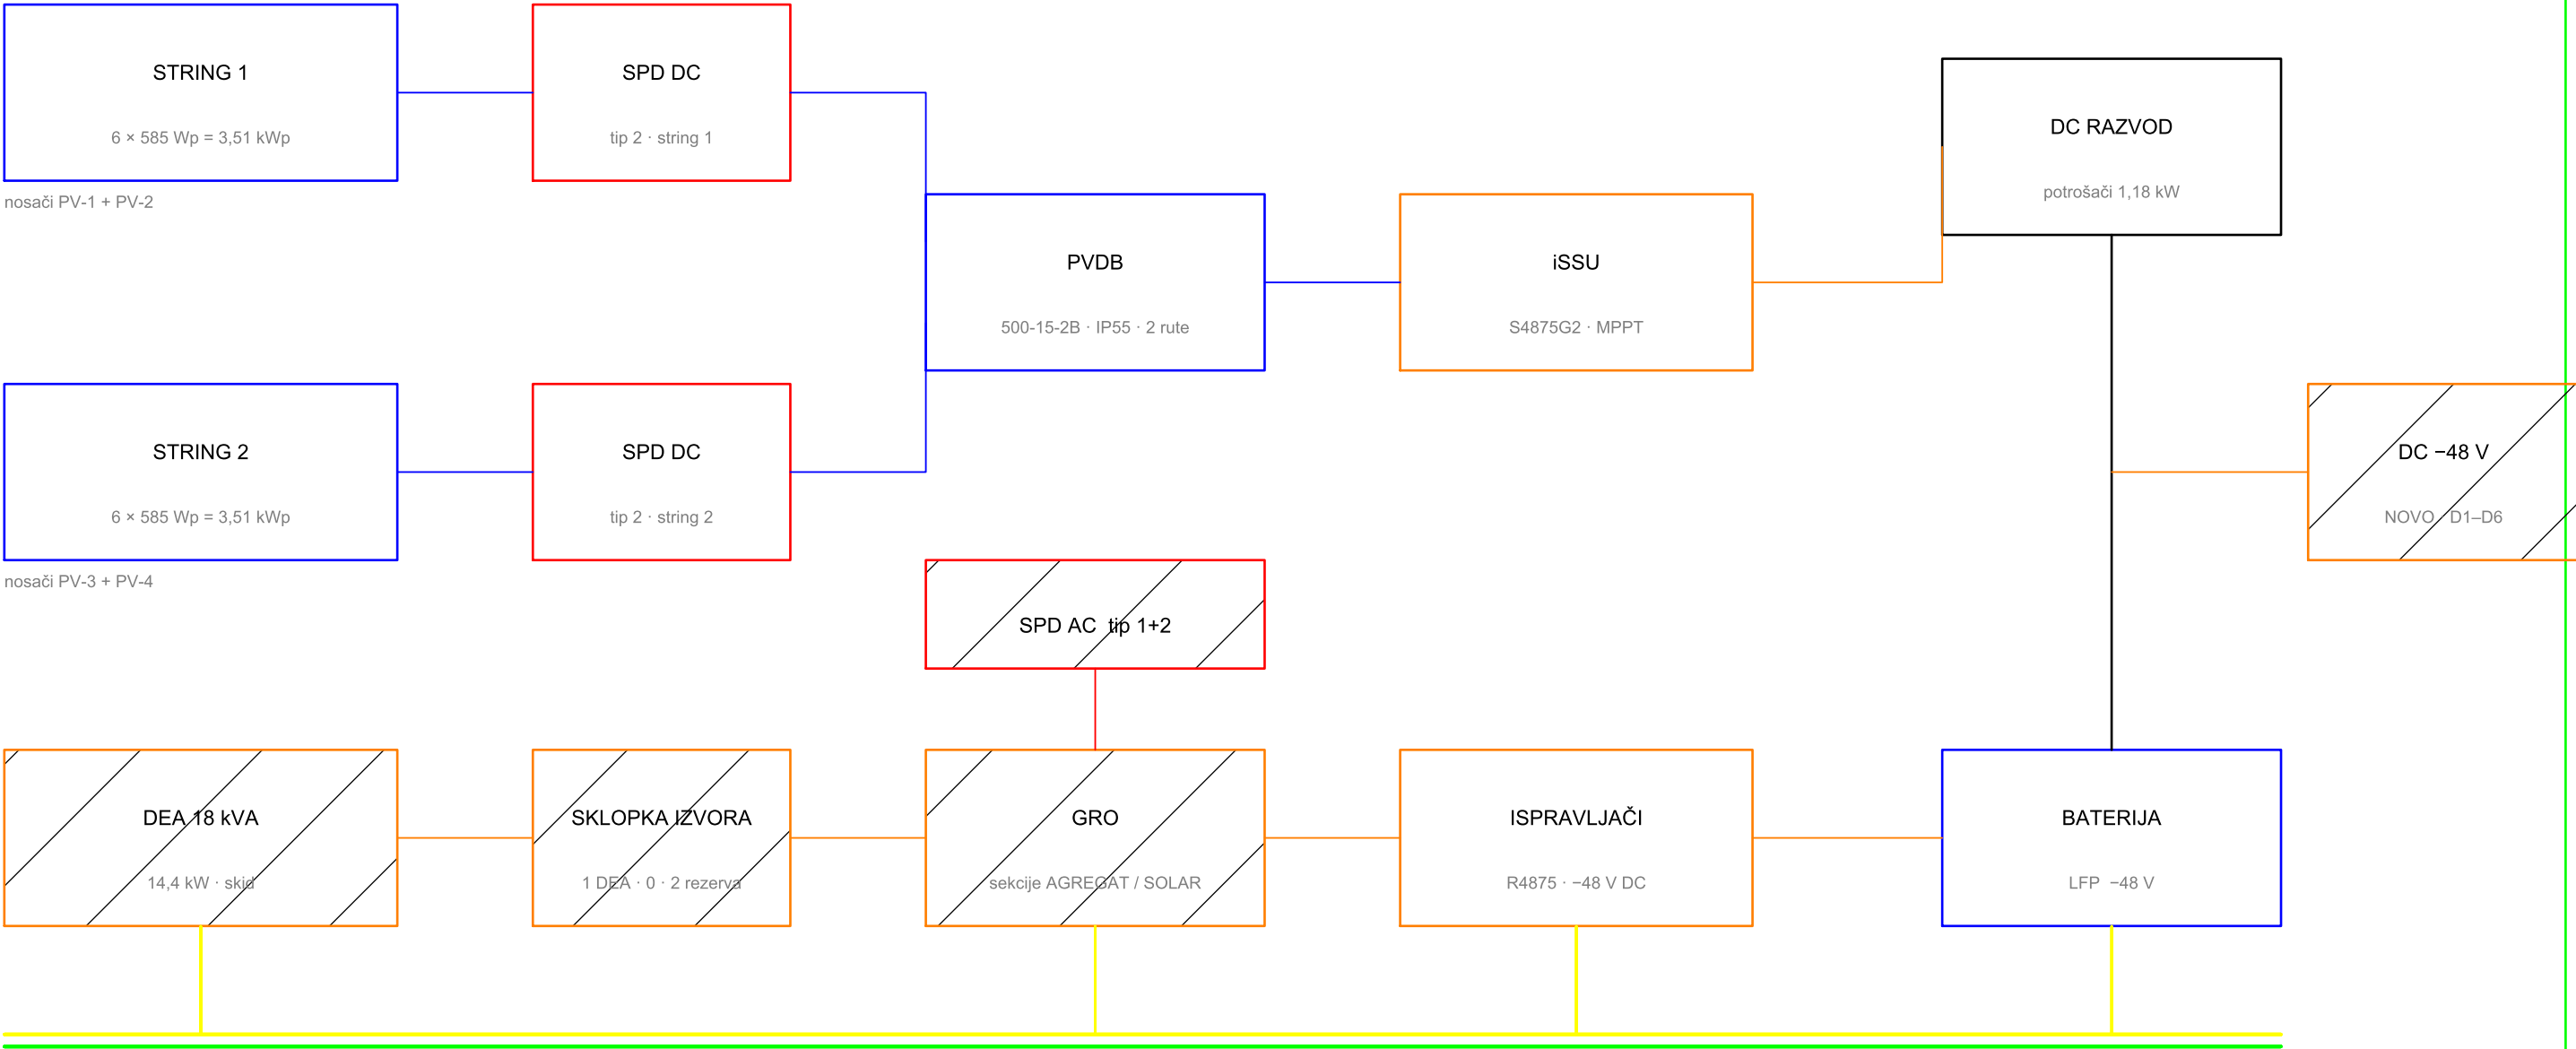

postojeći prstenasti uzemljivač Fe/Zn 25×4 · R ≤ 10 Ω · nosači FN vezani bakrenim užetom 50 mm² preko bimetalnih spojeva

- NAPOMENE:**
- Lokacija NIJE na mreži — DEA je jedini AC izvor; sklopka izvora 1 DEA · 0 · 2 rezerva.
 - Uzemljenje TN-S: spoj N-PE samo u novom GRO.
 - Odvodnici: AC tip 1+2, DC tip 2 po stringu, signalni vodovi EN 61643-21.
 - 12 modula = 2 stringa × 6 (nosači PV-1 + PV-2, PV-3 + PV-4); PVDB ima 2 rute.
 - DC razvod -48 V (NOVO): D1 rasvjeta prepreke, D2 vatrodojava, D3 punjač aku. DEA, D4 ventilator 48 V, D5 rasvjeta DC, D6 predgrijač DEA; bez grijača prostora.



BH TELECOM d.d. SARAJEVO
Izvršna direkcija za tehnologiju i razvoj servisa

Investitor:
BH Telecom d.d. Sarajevo, Franca Lehara 7, Sarajevo

Objekat:
BS SJEDNICA (Bileća) — autonomni hibridni sistem napajanja

Faza:
Tenderska dokumentacija — Prilog III

Naziv crteža:
Jednopolna shema — hibridni sistem napajanja

Projektant:
Rusmir Skopljak, dipl. ing. el.

ovjerio:
Rusmir Skopljak, dipl. ing. el.

šifra projekta:
BHT-SJEDNICA-2026

razmjera:
—

godina / broj crteža:
2026. E-01