


PRESJEK A-A (osa SZ trake nosača PV-2 — pogled prema SJEVEROZAPADU)

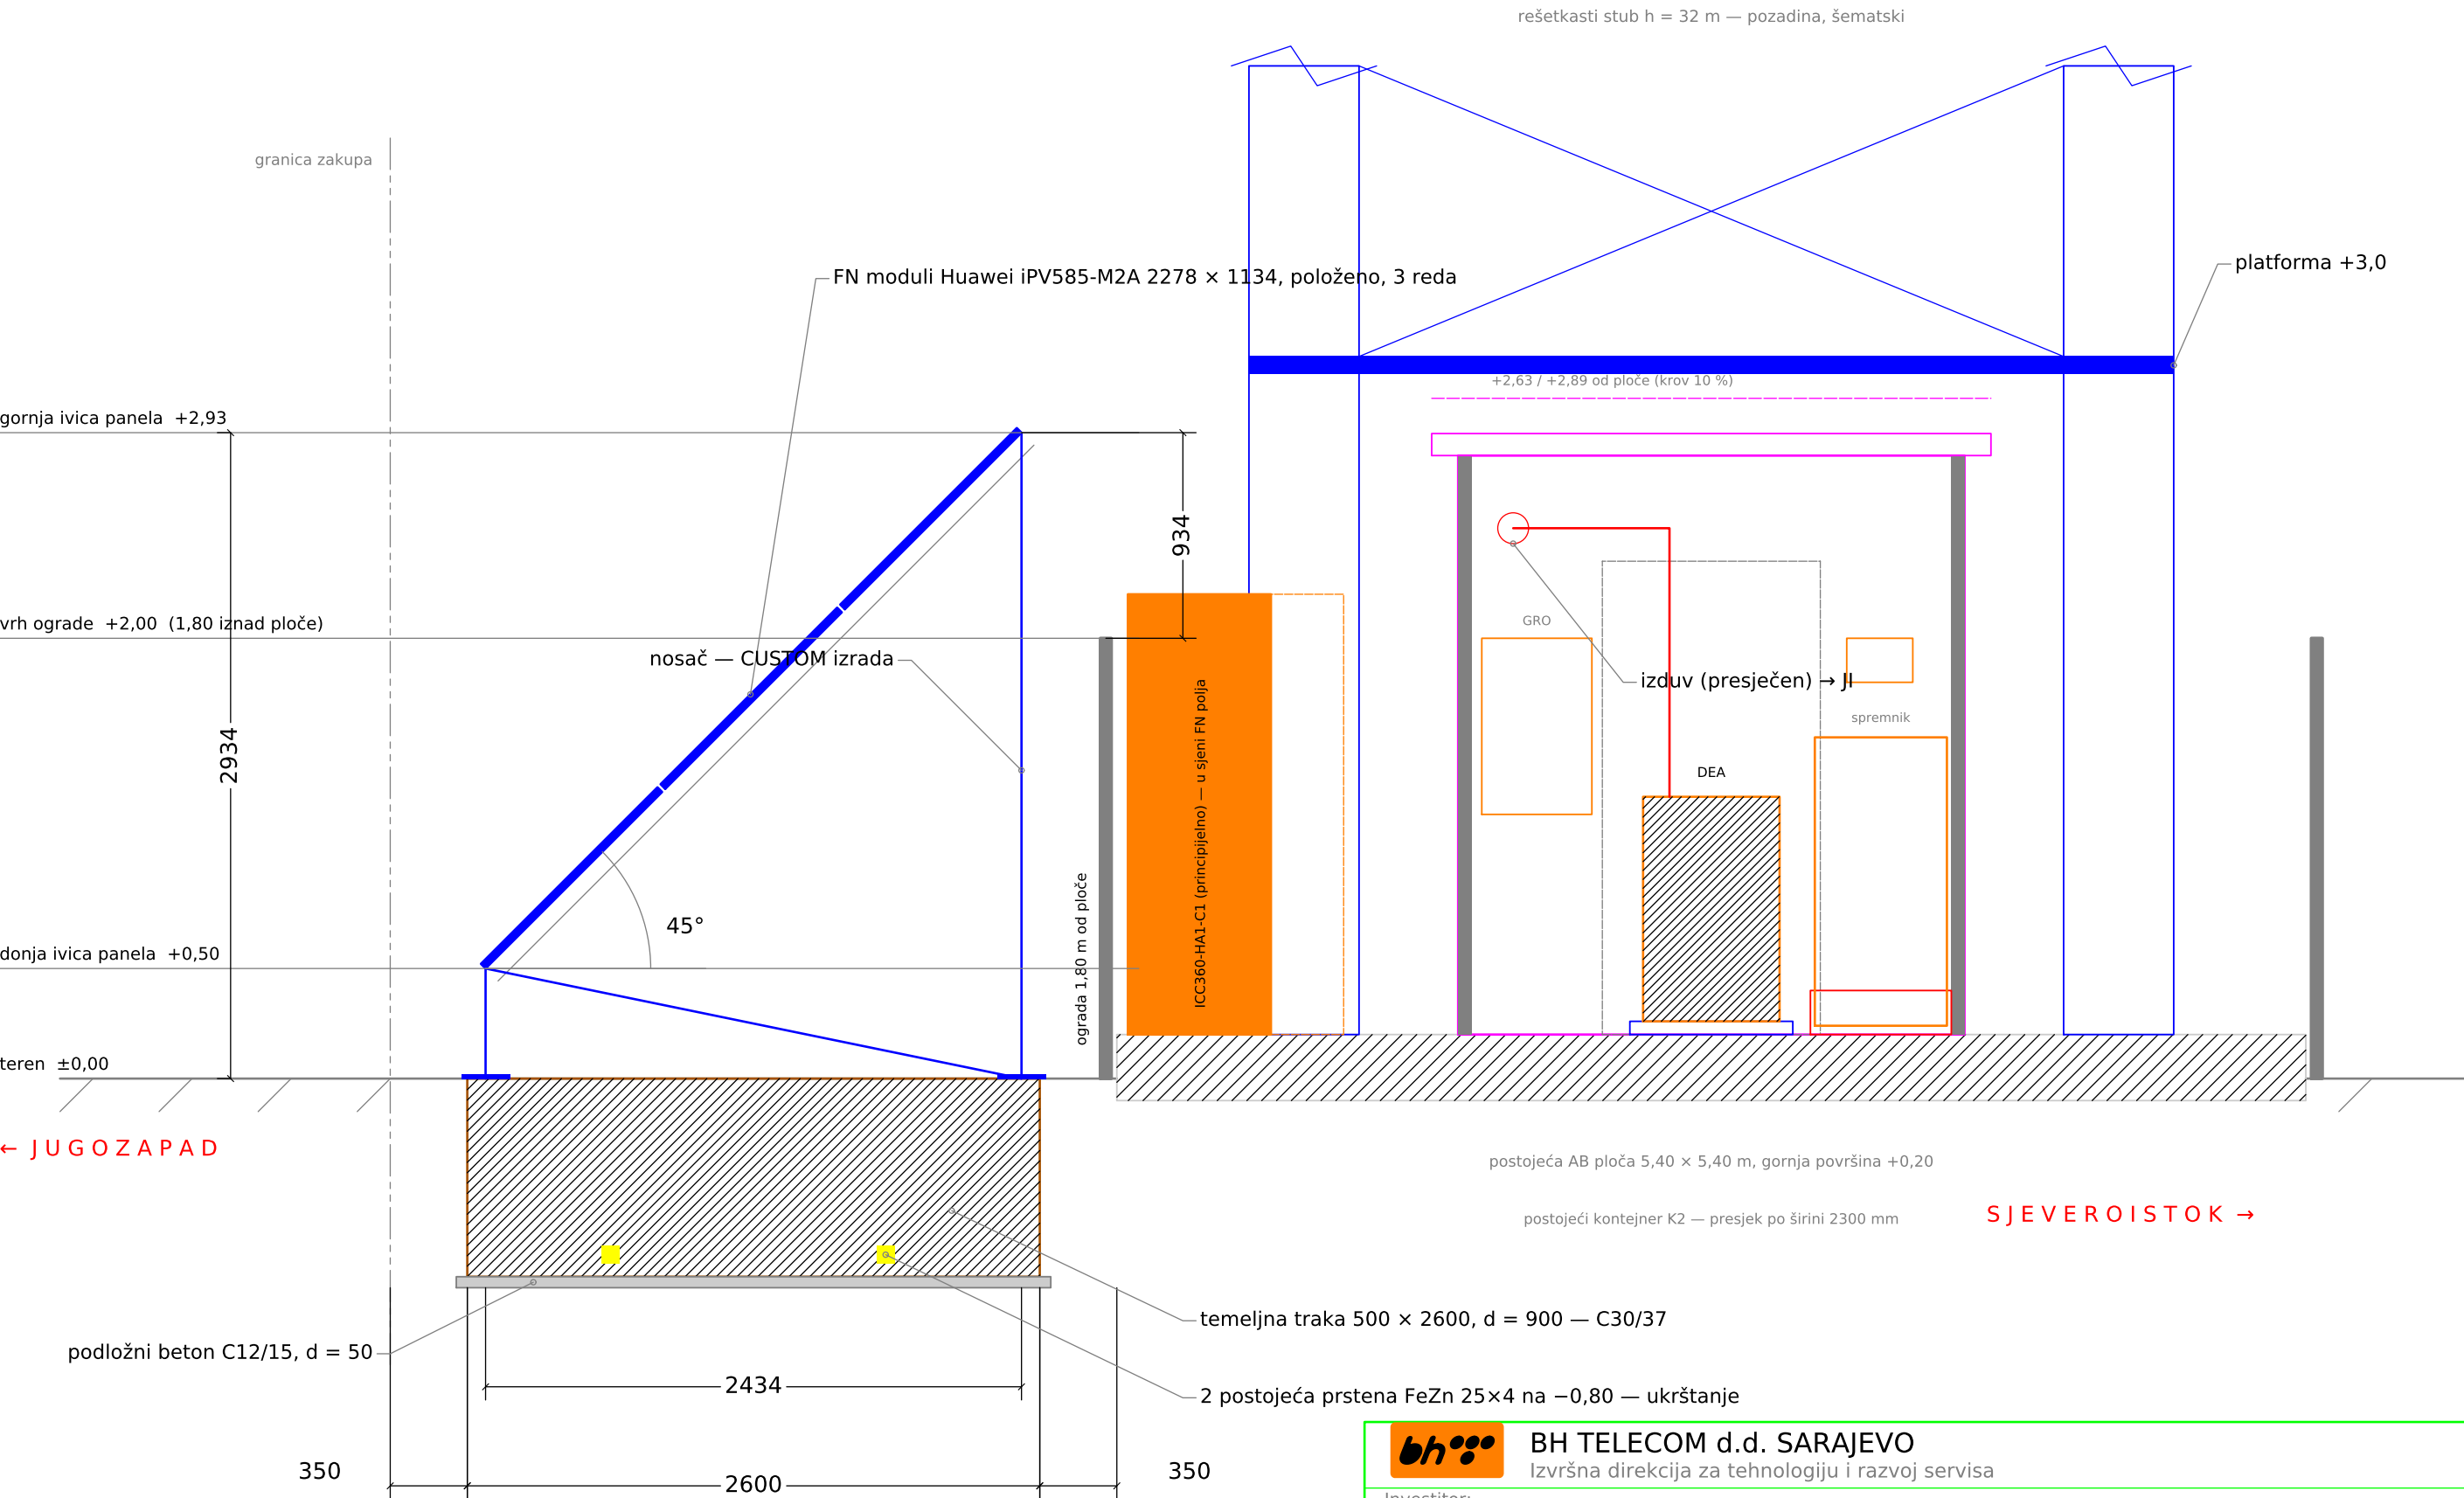

OBJAŠNENJA:

- Polje: 3 reda x 1 modul 585 Wp, položeno; nagib 45°, projekcija 2434 mm; 4 odvojena nosača u nizu (H-02).
- Dvije temeljne trake po nosaču 500 x 2600 mm, dubina 900 mm, razmak 1600 mm (druga iza ravni presjeka); beton C30/37 (XC4+XF3), armatura B500B, na podložnom betonu C12/15 d = 50 mm.
- Kote od terena uz FN polje; teren je -0,20 m ispod ploče (04\_Ograda). Donja ivica panela +0,50, gornja +2,93; vrh ograde +2,00 (1,80 m iznad ploče) — gornja ivica je 0,93 m iznad ograde.
- Postojeći prsteni uzemljivača na 0,8 m presijecaju traku: lociranje, otkopavanje i premještanje ili premoštavanje prstena (LOT 1).
- Trake su 350 mm od granice zakupa (JZ) i od ploče (SI); položaj presjeka na H-02.
- Stub, platforma P I (+3,0 m), kontejner i ormari šematski; ICC360 i MTS stoje iza FN polja, u njegovoj sjeni.

|                                                                                         |                                             |                                     |
|-----------------------------------------------------------------------------------------|---------------------------------------------|-------------------------------------|
| <b>bh</b> BH TELECOM d.d. SARAJEVO<br>Izvršna direkcija za tehnologiju i razvoj servisa |                                             |                                     |
| Investitor:<br>BH Telecom d.d. Sarajevo, Franca Lehara 7, Sarajevo                      |                                             |                                     |
| Objekat:<br>BS HAMZIĆI (ČITLUK) — autonomni hibridni sistem napajanja                   |                                             |                                     |
| Faza:<br>Tenderska dokumentacija — Prilog III                                           |                                             | šifra projekta:<br>BHT-HAMZICI-2026 |
| Naziv crteža:<br>Presjek A-A kroz FN polje                                              |                                             | razmjera:<br>1:30                   |
| Projektant:<br>Rusmir Skopljak, dipl. ing. el.                                          | ovjerio:<br>Rusmir Skopljak, dipl. ing. el. | godina / broj crteža:<br>2026. H-03 |