



OSNOVA — kontejner je PRAZAN; klima-uređaj Stulz se demontira

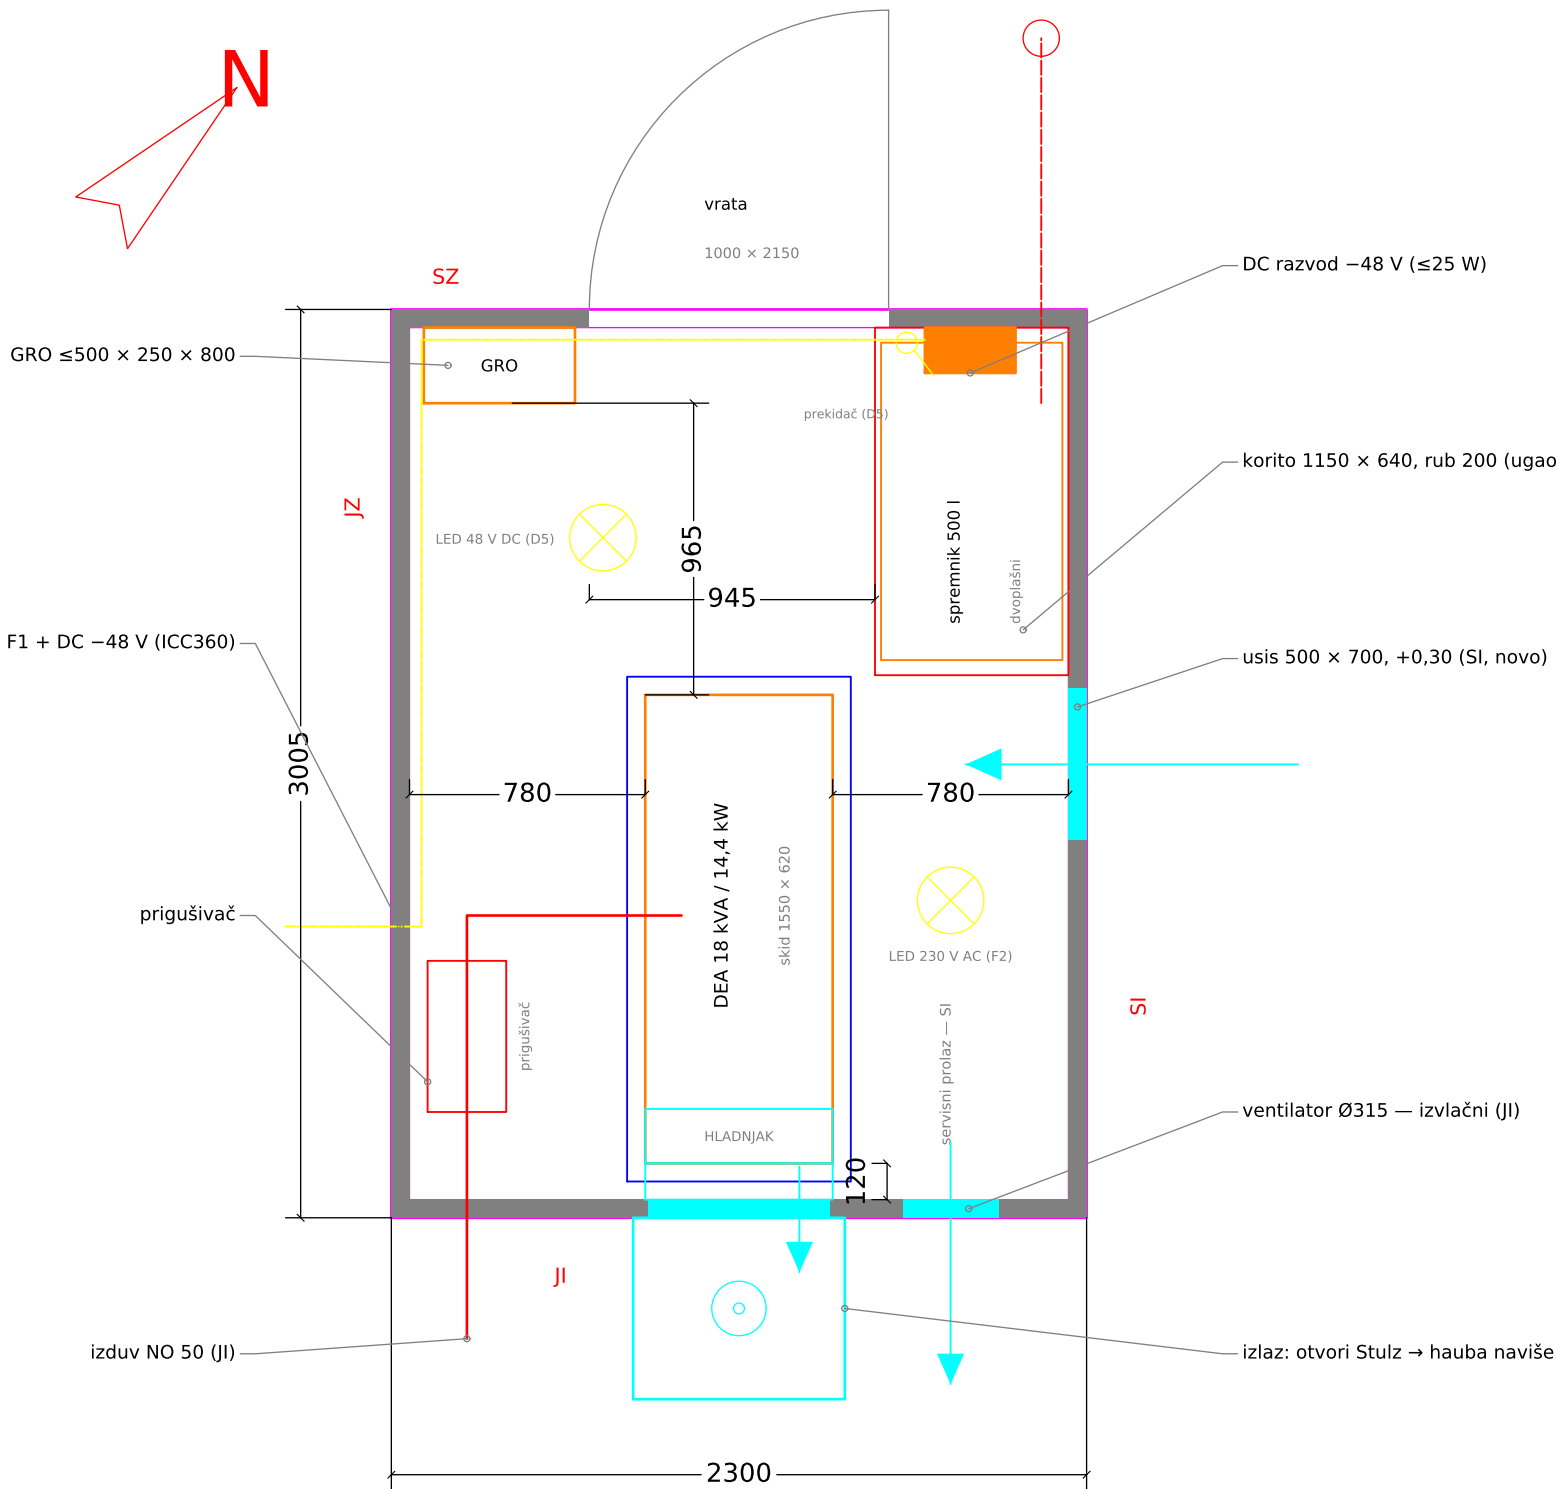

- NAPOMENE:**
- DEA FG Wilson P18-6 (skid) ili ekv., 18 kVA / 14,4 kW; os SZ-Jl, hladnjak Jl.
 - Izlaz zraka kroz postojeće otvore Stulz (sredina Jl zida), ≥0,36 m² bruto, limeni plenum i hauba 700 x 600 — topli zrak NAVIŠE.
 - Usis 500 x 700 na SI zidu (+0,30). Izduv NO 50 kroz Jl zid na ≈+2,30 m, ispod platforme stuba.
 - GRO ≤500 x 250 x 800 na SZ zidu; spremnik 500 l dvoplašni u koritu 1150 x 640; roštilj OBAVEZAN pod skidom i koritom.
 - Servisni prolazi 780 / 780 mm i 965 mm do GRO; unos skida 620 mm kroz vrata 990 mm.
 - Ventilator Ø315 (Jl, izvlačni, D4) i DC razvod -48 V istočno od vrata — H-05.
 - Raspored je principijelan; mjere otvora i servisne tačke potvrđuje Ponuđač na licu mjesta. Zahtjevi: Prilog I, Tačka 4.

PRESJEK 1-1 (os agregata — pogled prema SI, SZ lijevo)

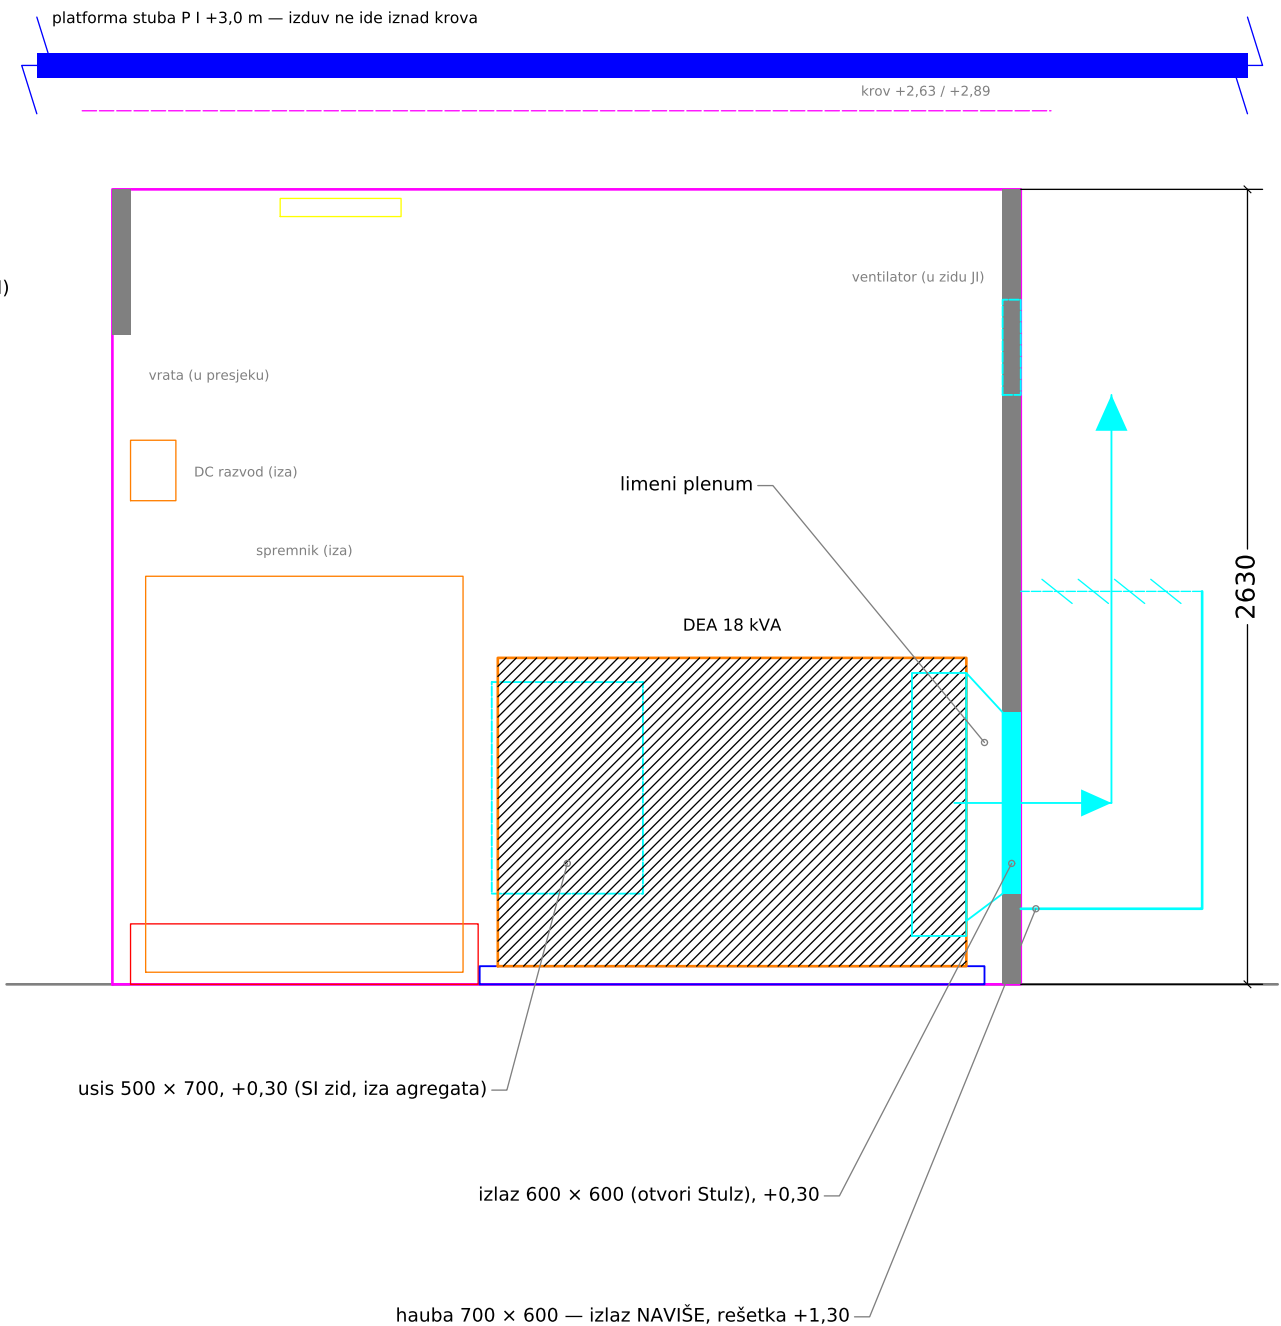

BH TELECOM d.d. SARAJEVO

Izvršna direkcija za tehnologiju i razvoj servisa

Investitor:

BH Telecom d.d. Sarajevo, Franca Lehara 7, Sarajevo

Objekat:

BS HAMZIĆI (ČITLUK) — autonomni hibridni sistem napajanja

Faza:

Tenderska dokumentacija — Prilog III

Naziv crteža:

Agregat u kontejneru — osnova i presjek 1-1

Projektant:

Rusmir Skopljak, dipl. ing. el.

ovjerio:

Rusmir Skopljak, dipl. ing. el.

šifra projekta:

BHT-HAMZICI-2026

razmjera:

1:25

godina / broj crteža:

2026. H-04