
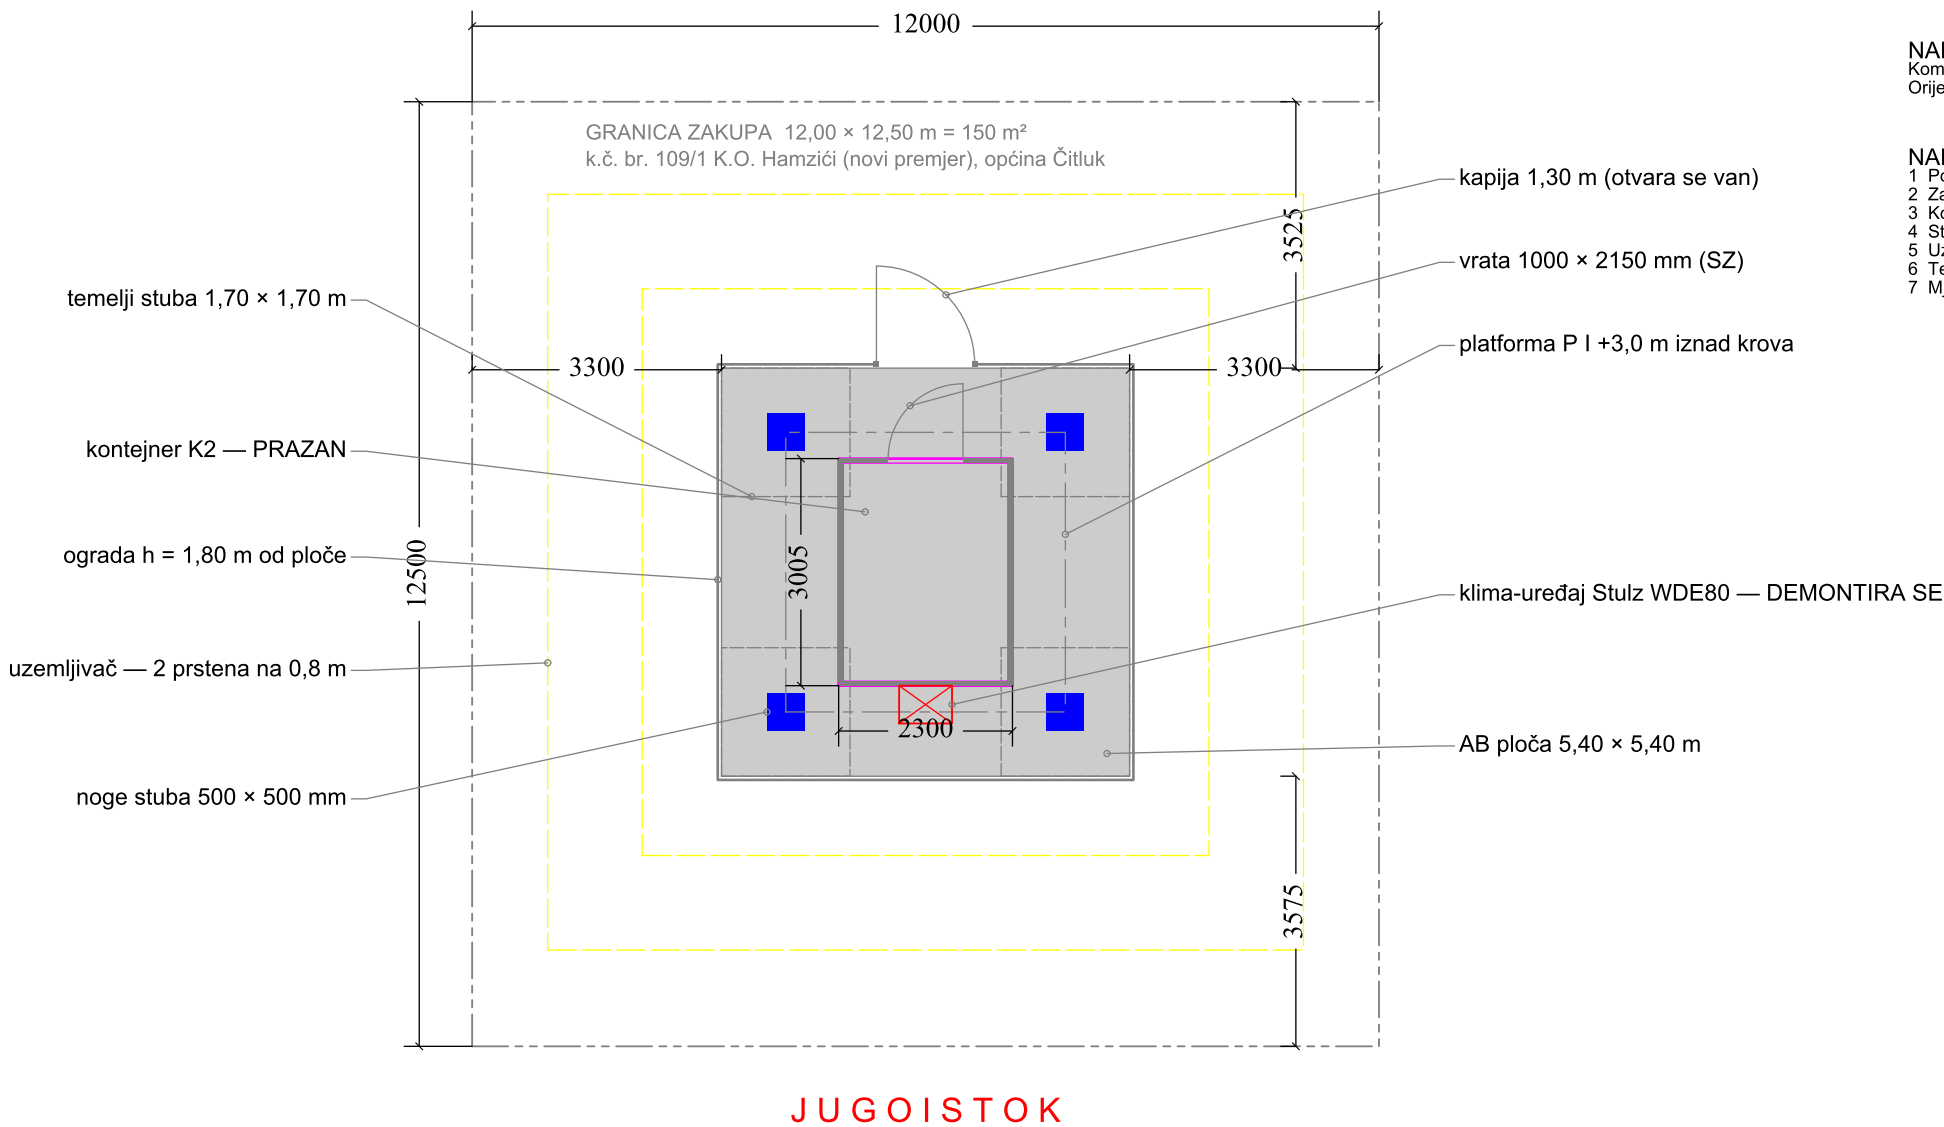


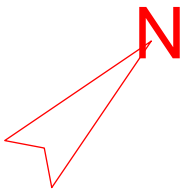

NAPOMENA — ORIJENTACIJA:
Kompleks je zakrenut za 45°; strelica označava pravi sjever.
Orijentaciju potvrđuje Ponuđač na lokaciji.

NAPOMENE:
1 Podloga: ovjereni projekat lokacije GP-BS-10472-291 (2017).
2 Zakup 12,00 x 12,50 m (150 m²), k.č. 109/1, općina Čitluk.
3 Kontejner je prazan; klima-uređaj Stulz WDE80 je na JI zidu.
4 Stub h = 32 m; platforma P I je na +3,0 m.
5 Uzemljivač FeZn 25x4 mm: prsten u temeljima stuba i dva prstena na 0,8 m.
6 Teren uz ploču je na -0,20 m; ograda je 1,80 m iznad ploče.
7 Mjere se potvrđuju obilaskom lokacije.

LEGENDA

- postojeća ograda 5,50 x 5,50 m, h = 1,80 m od ploče (2,00 m od terena) — kapija 1,30 m na SZ strani
- postojeća AB ploča 5,40 x 5,40 m
- postojeći kontejner K2 2300 x 3005 mm — vrata na SZ strani
- noge rešetkastog stuba h = 32 m, baza 3,70 x 3,70 m
- klima-uređaj Stulz WDE80 (JI zid, u sredini) — demontira se
- postojeći uzemljivač FeZn 25x4 mm (isprekidano — u tlu)



bh BH TELECOM d.d. SARAJEVO Izvršna direkcija za tehnologiju i razvoj servisa		
Investitor: BH Telecom d.d. Sarajevo, Franca Lehara 7, Sarajevo		
Objekat: BS HAMZIĆI (ČITLUK) — autonomni hibridni sistem napajanja		
Faza: Tenderska dokumentacija — Prilog III		šifra projekta: BHT-HAMZICI-2026
Naziv crteža: Situacija — POSTOJEĆE STANJE		razmjera: 1:100
Projektant: Rusmir Skopljak, dipl. ing. el.	ovjerio: Rusmir Skopljak, dipl. ing. el.	godina / broj crteža: 2026. H-01