


POGLED SA JUGOZAPADA (pravac gledanja azimut 45°)

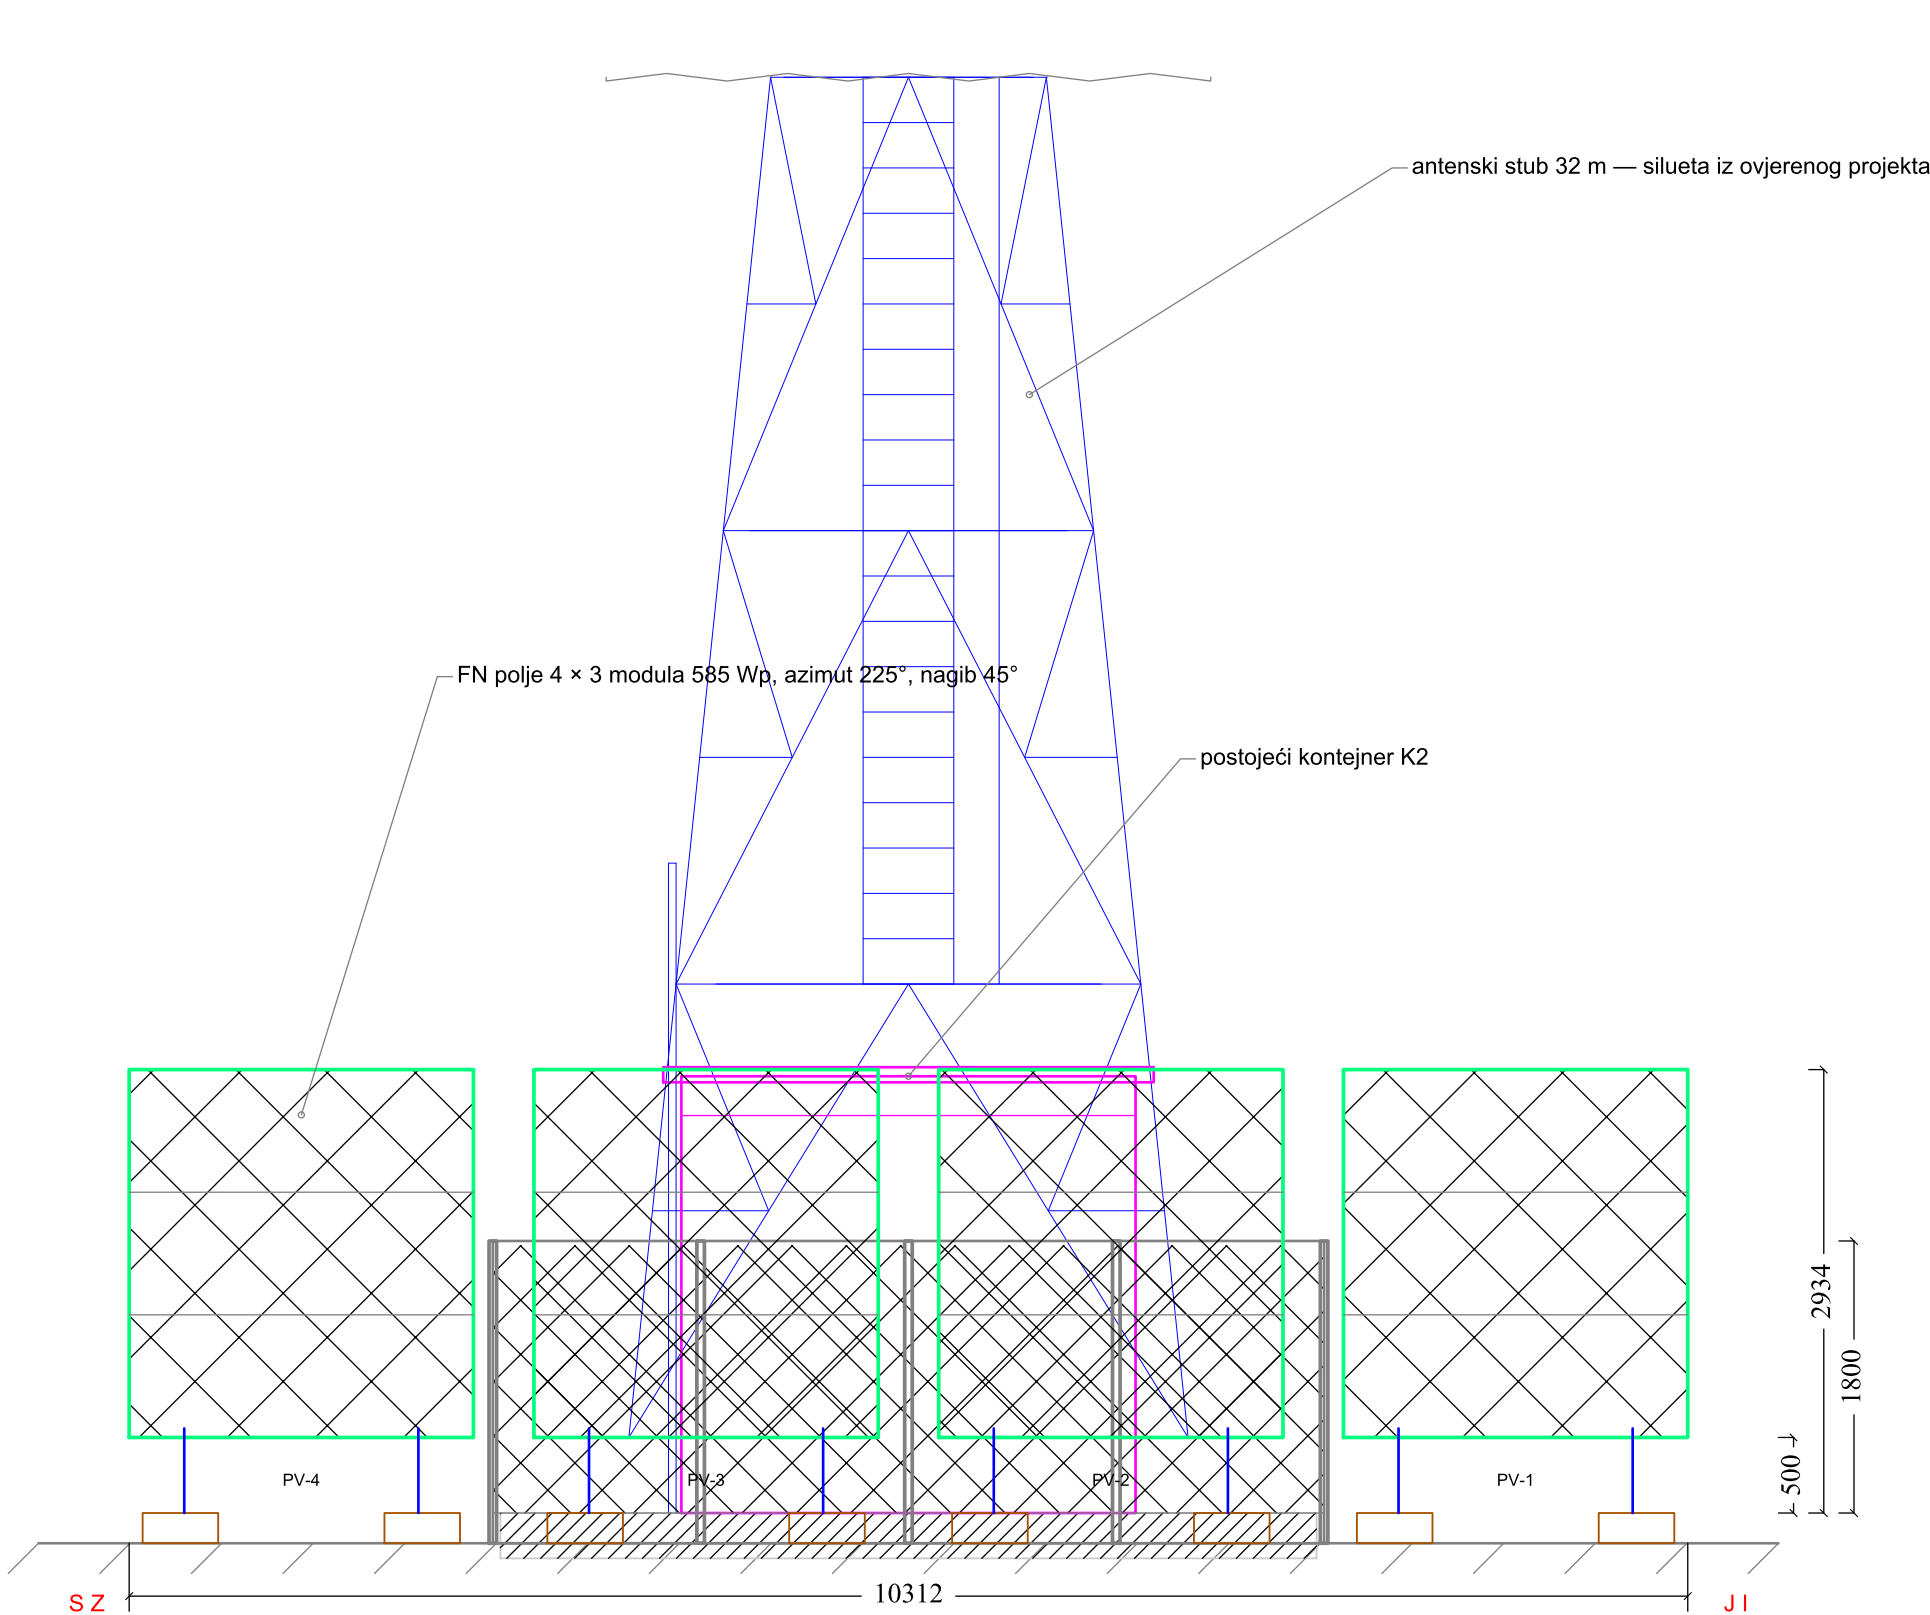

- LEGENDA
- LOT 1 — FN moduli i nosači (ispred ograde, JZ)
 - postojeći antenski stub — silueta iz ovjerenog projekta
 - postojeći kontejner K2 na postojećoj ploči
 - postojeća oграда 1,80 m iznad ploče

- NAPOMENE:
- Ortogonalni pogled u pravcu azimuta 45°.
 - Paneli su prikazani skraćeno: +0,50 do +2,93 m od ploče.
 - Teren uz FN polje je na -0,20 m.
 - Stub je prekinut na +9,50 m; h = 32 m.
 - Zahtjevi: Prilog I, Tačke 3 i 4.

BH TELECOM d.d. SARAJEVO Izvršna direkcija za tehnologiju i razvoj servisa		
Investitor: BH Telecom d.d. Sarajevo, Franca Lehara 7, Sarajevo		
Objekat: BS HAMZIĆI (ČITLUK) — autonomni hibridni sistem napajanja		
Faza: Tenderska dokumentacija — Prilog III		šifra projekta: BHT-HAMZICI-2026
Naziv crteža: Pogled sa JUGOZAPADA — kompleks sa FN poljem		razmjera: 1:50
Projektant: Rusmir Skopljak, dipl. ing. el.	ovjerio: Rusmir Skopljak, dipl. ing. el.	godina / broj crteža: 2026. H-06