
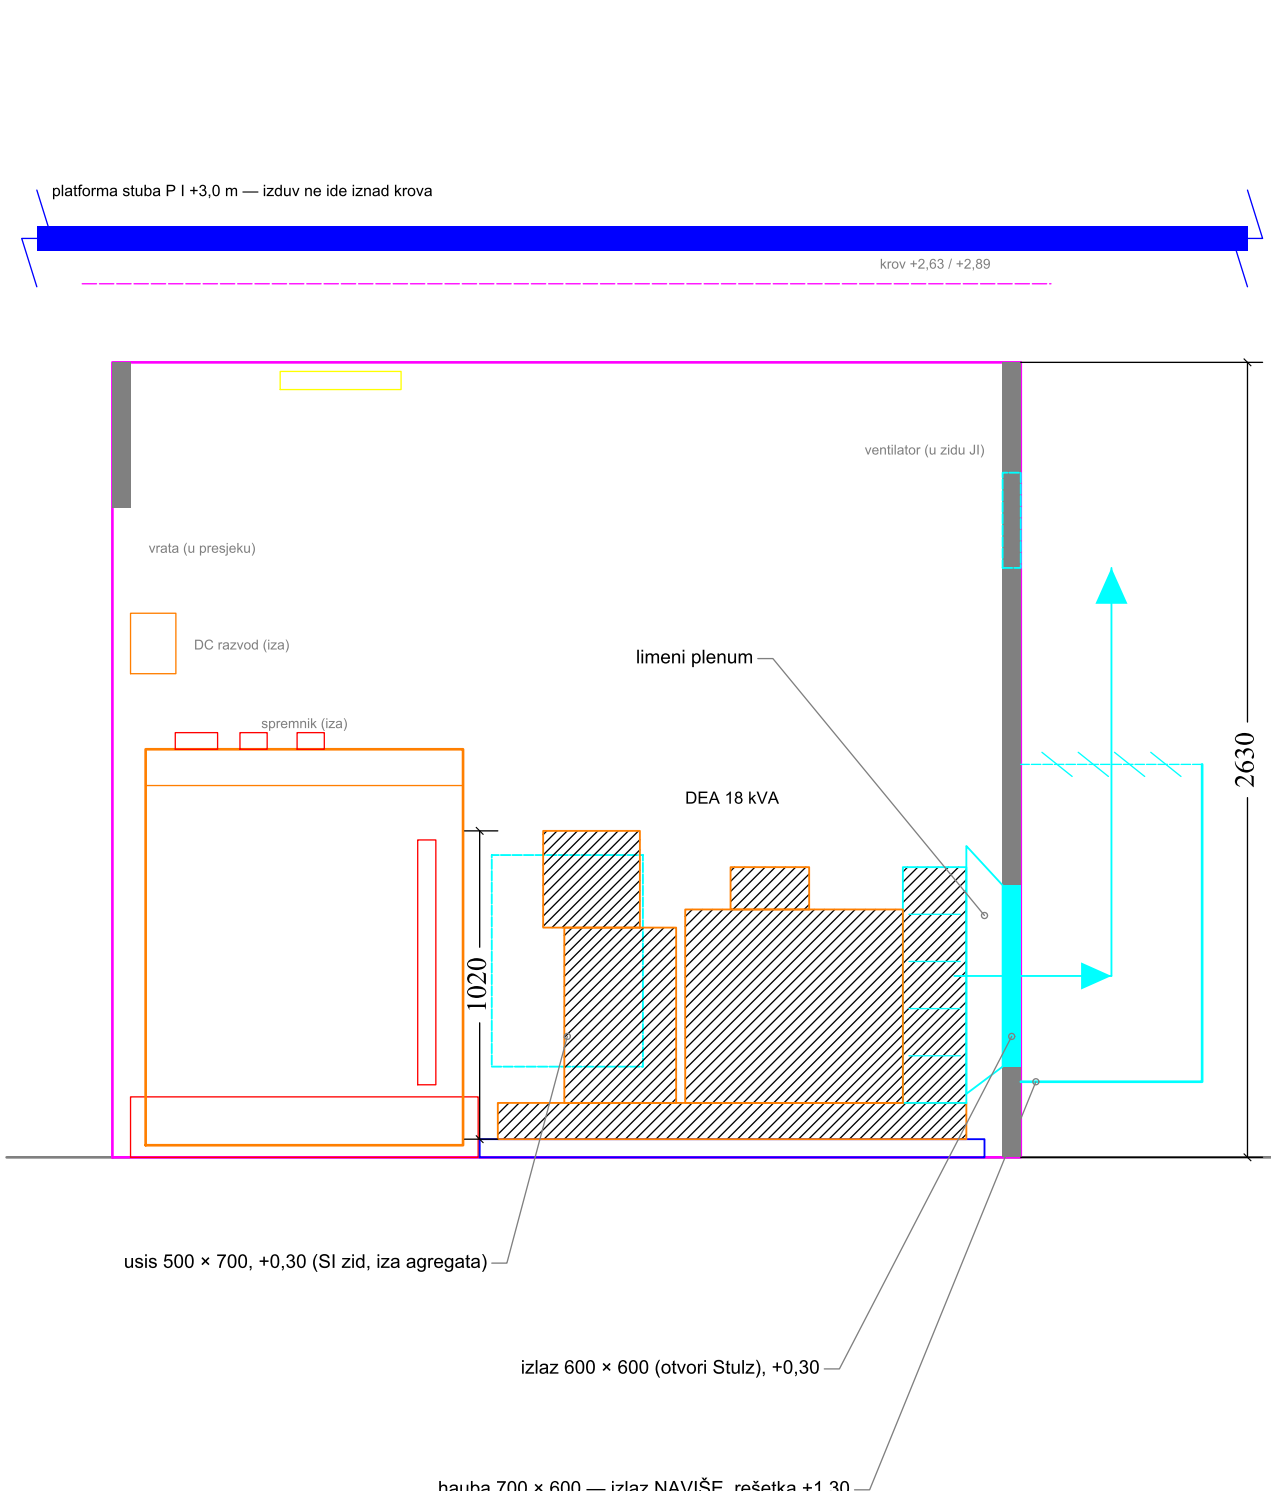


OSNOVA — kontejner je PRAZAN; klima-uređaj Stulz se demontira

PRESJEK 1–1 (os agregata — pogled prema SI, SZ lijevo)

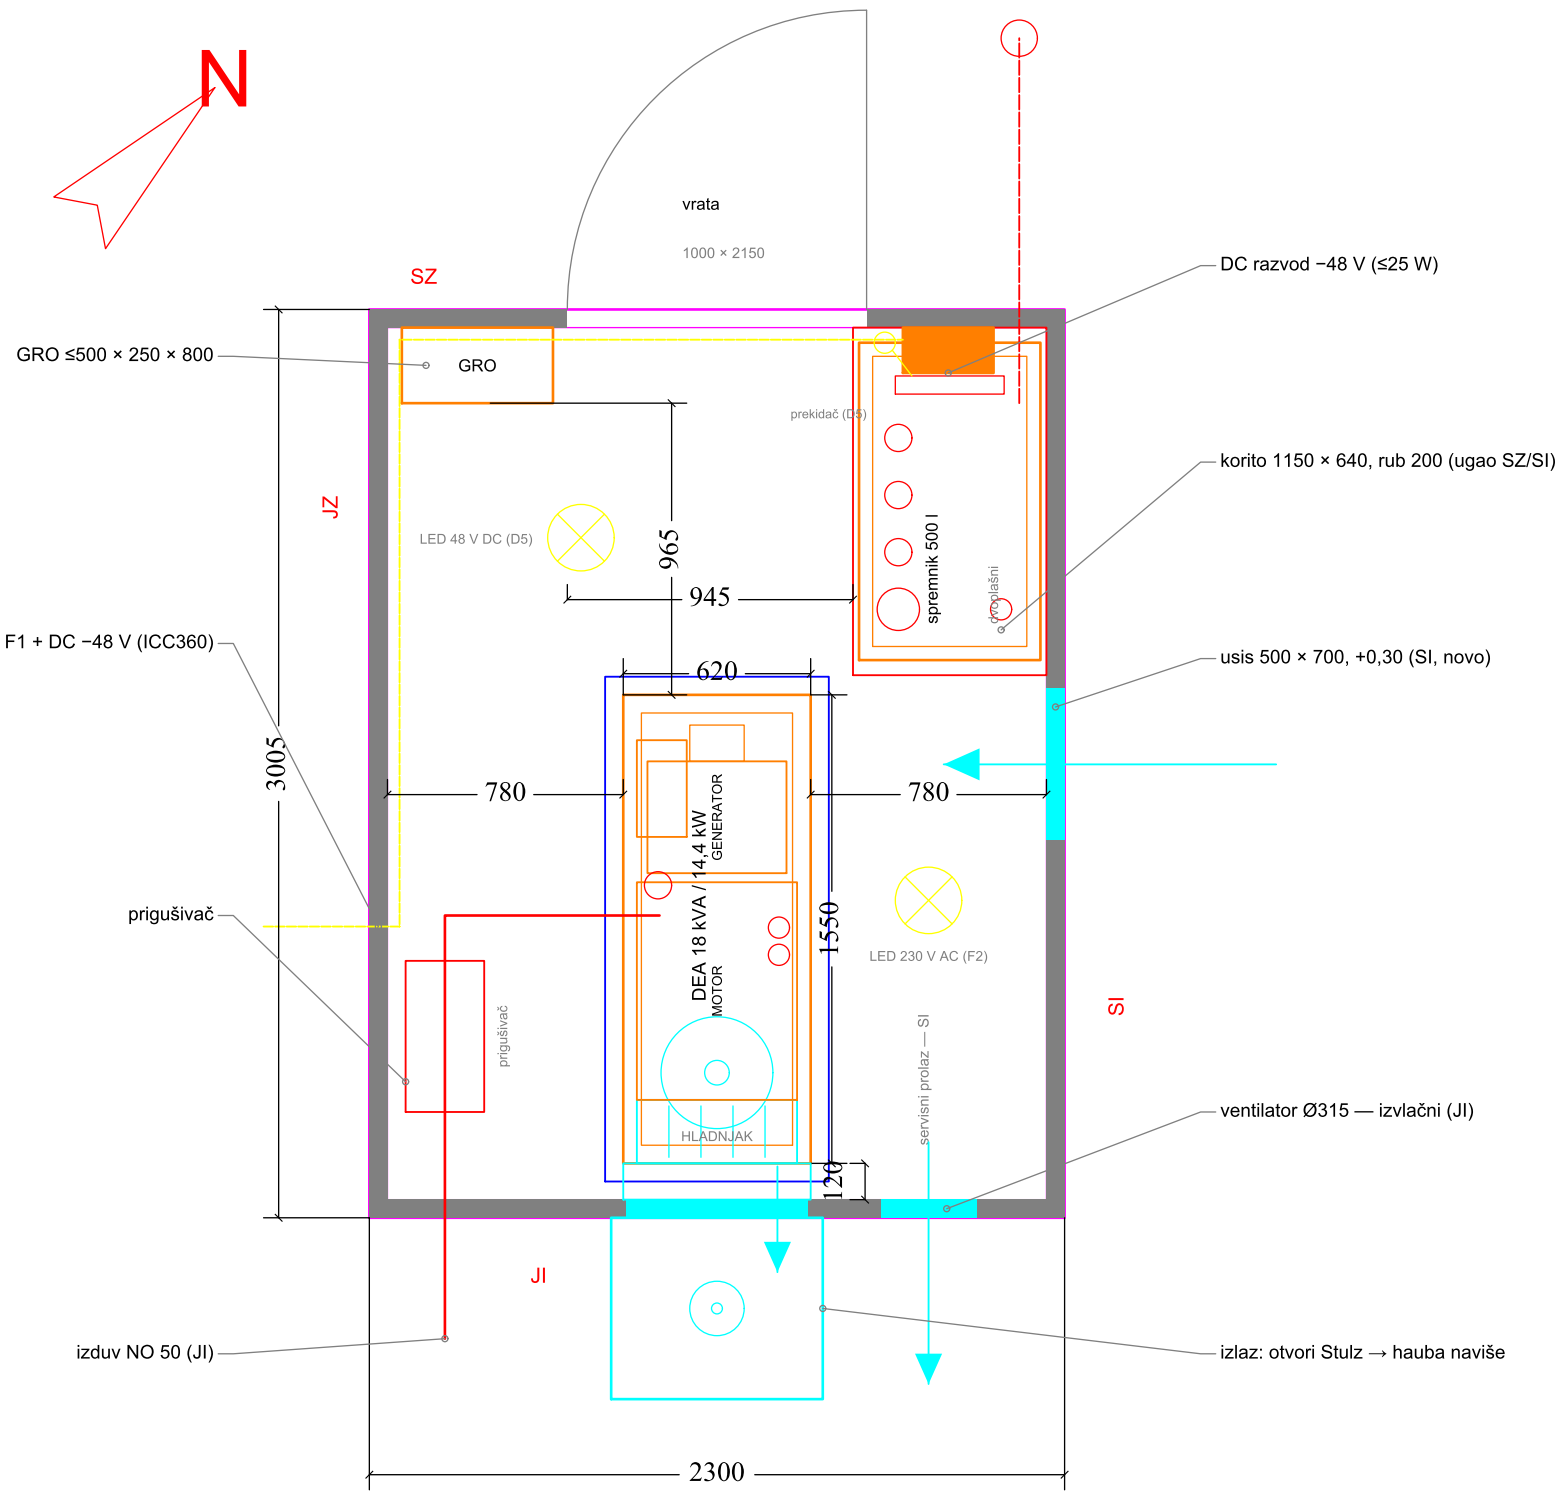

- NAPOMENE:
- 1 DEJA FG Wilson P18-6 ili ekvivalent, 18 kVA / 14.4 kW.
 - 2 Izlaz zraka kroz otvore Stulz (JI), najmanje 0,36 m²; hauba usmjerava zrak naviše.
 - 3 Usis 500 x 700 mm (SI, +0,30 m); izduv NO 50 kroz JI zid na ≈+2,30 m.
 - 4 Spreminik 500 I je dvoplašni, u koritu; roštilj ispod skida i korita je obavezan.
 - 5 Servisni prolazi se ne zauzimaju.
 - 6 Raspored je principijelan. Zahtjevi: Prilog I, Tačka 4.

bh BH TELECOM d.d. SARAJEVO Izvršna direkcija za tehnologiju i razvoj servisa		
Investitor: BH Telecom d.d. Sarajevo, Franca Lehara 7, Sarajevo		
Objekat: BS HAMZIĆI (ČITLUK) — autonomni hibridni sistem napajanja		
Faza: Tenderska dokumentacija — Prilog III		šifra projekta: BHT-HAMZICI-2026
Naziv crteža: Agregat u kontejneru — osnova i presjek 1–1		razmjera: 1:25
Projektant: Rusmir Skopljak, dipl. ing. el.	ovjerio: Rusmir Skopljak, dipl. ing. el.	godina / broj crteža: 2026. H-04