


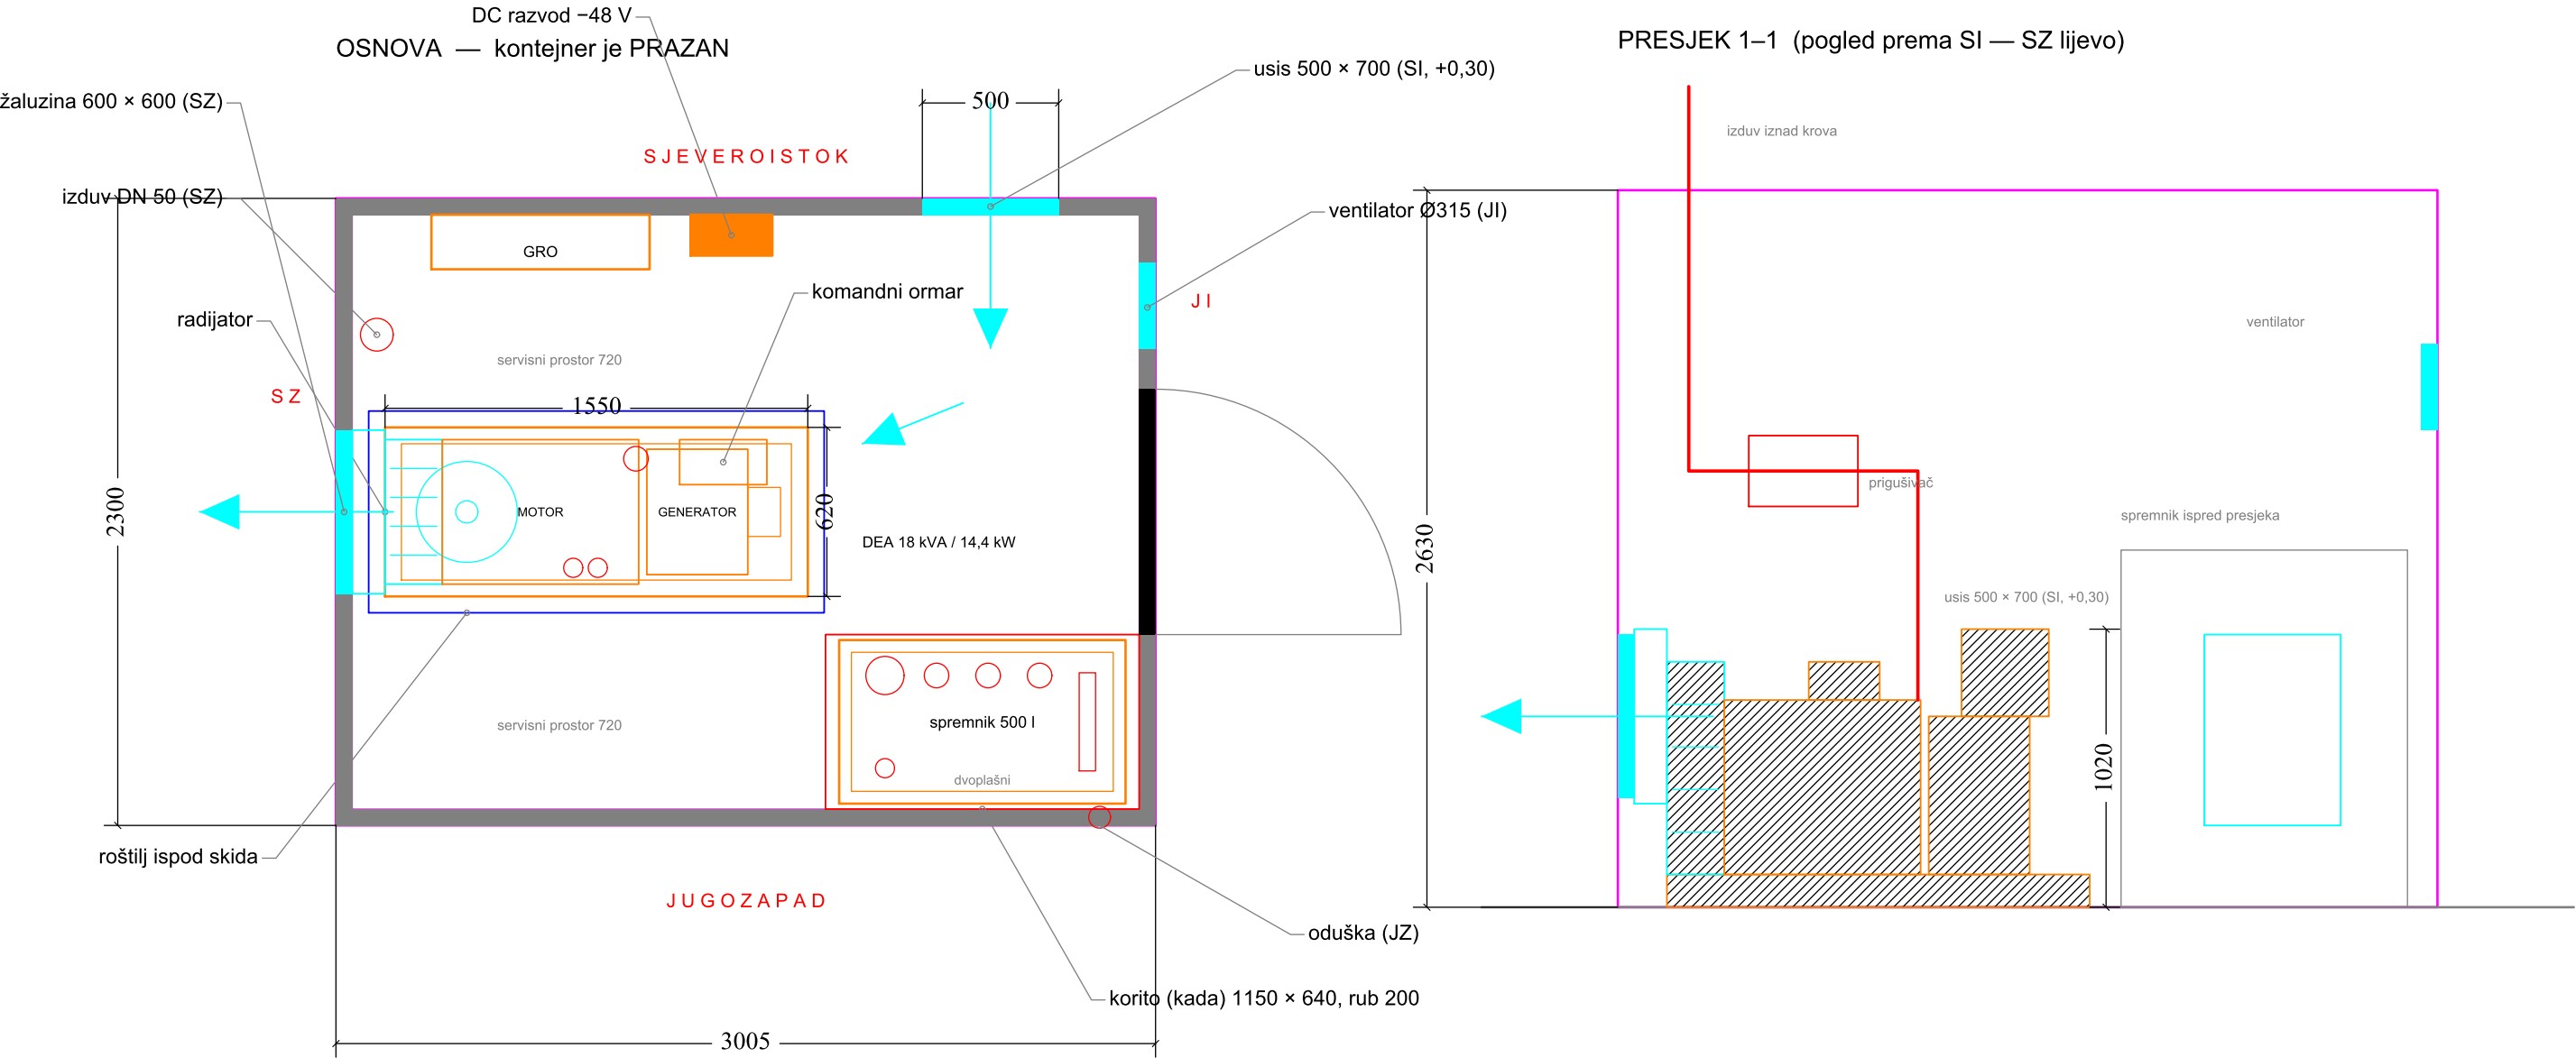

NAPOMENE:
1 DEA FG Wilson P18-6 ili ekvivalent, 18 kVA / 14,4 kW.
2 Usis 500 × 700 mm (SI); izlaz 600 × 600 mm i izduv DN 50 (SZ); ventilator Ø315 (JI).
3 Spremnik 500 l je dvoplašni, u koritu; roštilj ispod skida i korita je obavezan.
4 Servisni prolazi 720 / 720 / 1155 mm se ne zauzimaju.
5 DC razvod -48 V je na SI zidu; potrošači D1-D6 prikazani su na E-01.
6 Raspored je principijelan. Zahtjevi: Prilog I, Tačka 4.

bh BH TELECOM d.d. SARAJEVO Izvršna direkcija za tehnologiju i razvoj servisa		
Investitor: BH Telecom d.d. Sarajevo, Franca Lehara 7, Sarajevo		
Objekat: BS SJEDNICA (Bileća) — autonomni hibridni sistem napajanja		
Faza: Tenderska dokumentacija — Prilog III		šifra projekta: BHT-SJEDNICA-2026
Naziv crteža: DEA u postojećem kontejneru — osnova i presjek		razmjera: 1:25
Projektant: Rusmir Skopljak, dipl. ing. el.	ovjerio: Rusmir Skopljak, dipl. ing. el.	godina / broj crteža: 2026. M-01